



TIM(SHANG HAI) SIRSPACE DESIGN CO.,LTD
福州安润福设计工程有限公司
TEL:+86-591-88067888
FAX:+86-591-83329099
E-M:TIMSPACE@163.COM
F-T:800-820-2780

CLIENT (项目名称):

平潭富春城幼儿园二次装修

JOB LOCATION (项目位置):

平潭

JOB NO. (项目编号):

T/D20211012

DESIGN APPROVAL (出图盖章处):

Remarks (说明):

- 本设计为案所有权属本公司, 未经公司盖章不得擅自使用。
- 施工图纸上的图形、文字、说明等, 的著作权属本公司, 施工结束后收回其使用权。
- 施工图符合《建筑内部装修设计防火规范》GB50222-95规定。
- 现场尺寸由施工单位负责核实。施工单位必须具备图样翻样能力, 在施工中因保证外形尺寸不变的情况下内部构造允许进行调整; 若发现其与施工图标注有出入等, 施工单位有责任立即通知本公司; 否则, 施工单位须承担所有责任。

DESCRIPTION (内容):

一层平面布置图


项目负责人 APPROVED DIRECTOR BY	彭晓	
设计负责人 PROJECT DIRECTOR BY	彭晓	
审核 CHECK	陈锋	
设计人 DESIGNED BY	黄章翔	
制图 DRAWING	黄章翔	
图别 STATUS	A1	
比例 SCALE	1:100	
制图日期 DNG. DATE	2021/11/27	
修改日期 MODIFY DATE		

图号
DRAWING No.
FF-1.0

序号
No.
3

CLIENT'S APPROVAL (客户确认):

DATE (日期):

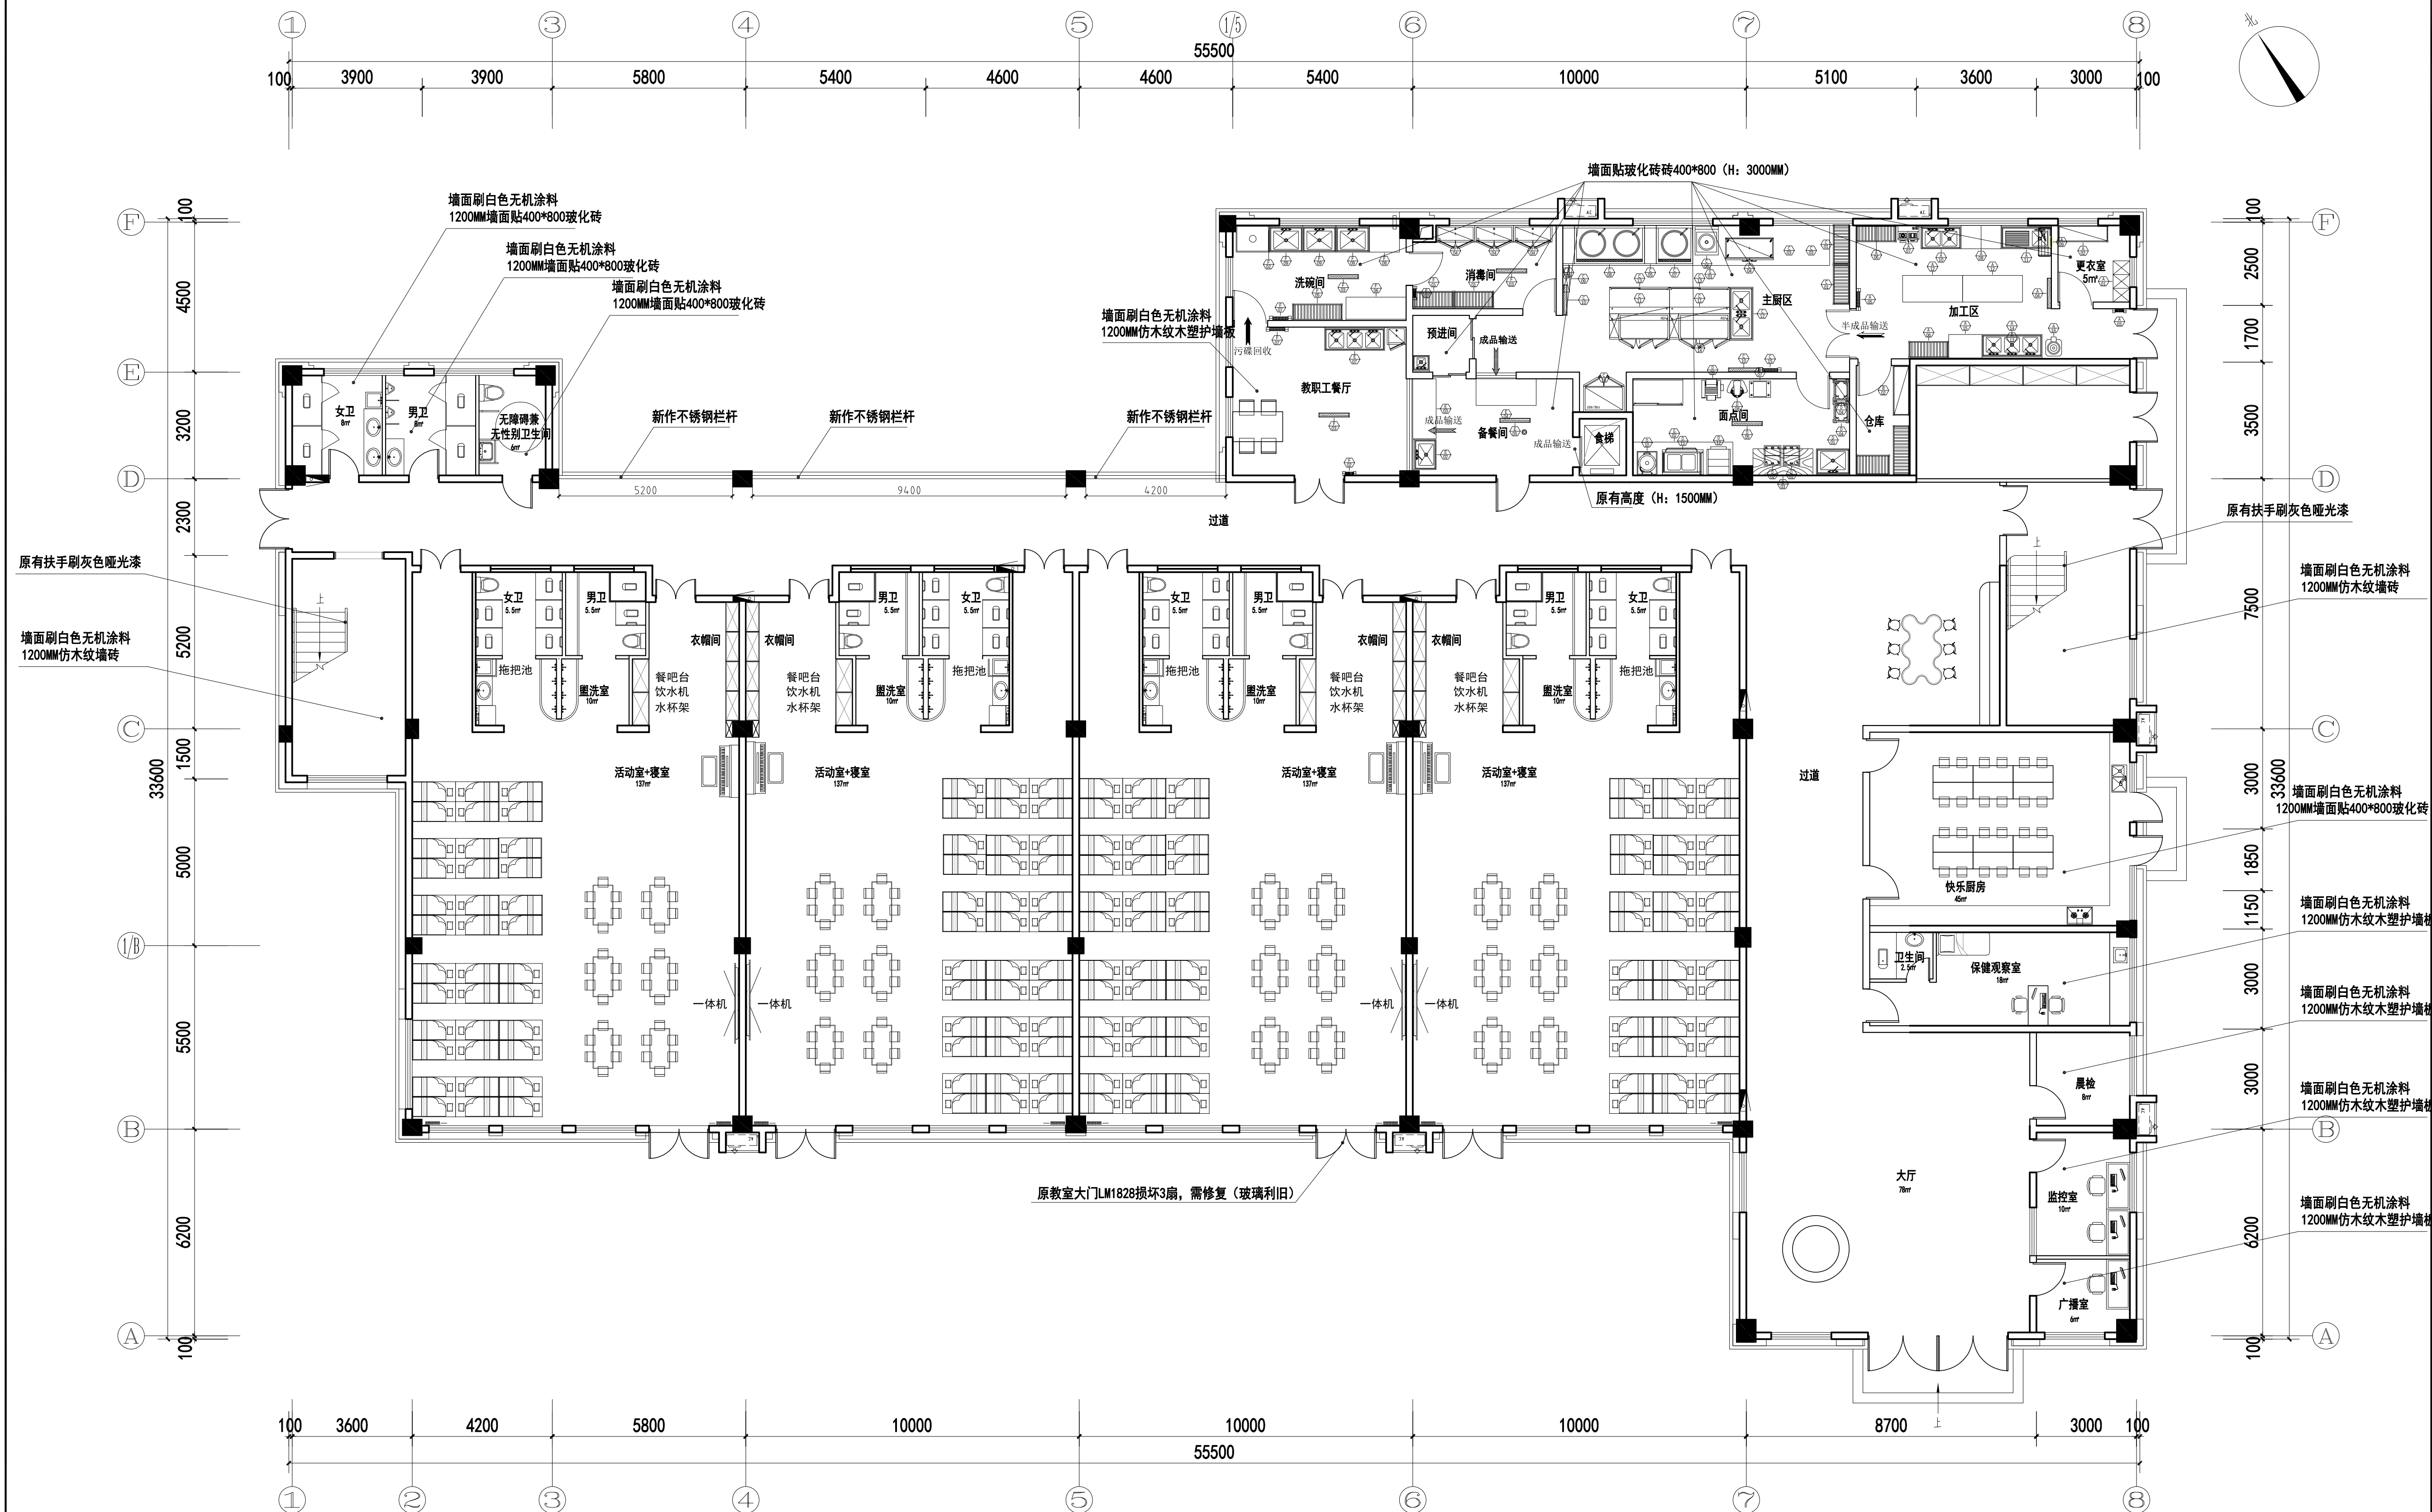

FF PLAN 平潭富春城幼儿园
Scale: 1:100 一层平面布置图



TIM(SHANG HAI) SIRSPACE DESIGN CO.,LTD
福州安润福设计工程有限公司
TEL:+86-591-88067888
FAX:+86-591-83329099
E-M:TIMSPACE@163.COM
T:1800-820-2780

CLIENT (项目名称):

平潭富春城幼儿园二次装修

JOB LOCATION (项目位置):

平潭

JOB NO. (项目编号):

T/D20211012

DESIGN APPROVAL (出图盖章处):

Remarks (说明):

- 本设计为方案所有权属本公司，未经公司盖章不得擅自使用。
- 施工图纸上的图形、文字、说明等，的著作权属本公司，施工结束后收回其使用权。
- 施工应符合《建筑内部装修设计防火规范》GB50222-95规定。
- 现场尺寸由施工单位负责核实，施工单位必须具备图纸翻样能力，在施工中如发现尺寸不符的情况，应立即通知设计单位进行变更，与施工图纸的标注有出入等，施工单位有责任立即通知本公司，否则，施工单位须承担所有责任。

DESCRIPTION (内容):

二层平面布置图


项目负责人 APPROVED DIRECTOR BY	彭晓	
设计负责人 PROJECT DIRECTOR BY	彭晓	
审核 CHECK	陈锋	
设计人 DESIGNED BY	黄章翔	
制图 DRAWING	黄章翔	
图别 STATUS	A1	
比例 SCALE	1:100	
制图日期 DNG. DATE	2021/11/27	
修改日期 MODIFY DATE		

图号
DRAWING No.
FF-2.0

序号
No.
10

CLIENT'S APPROVAL (客户确认):

DATE (日期):

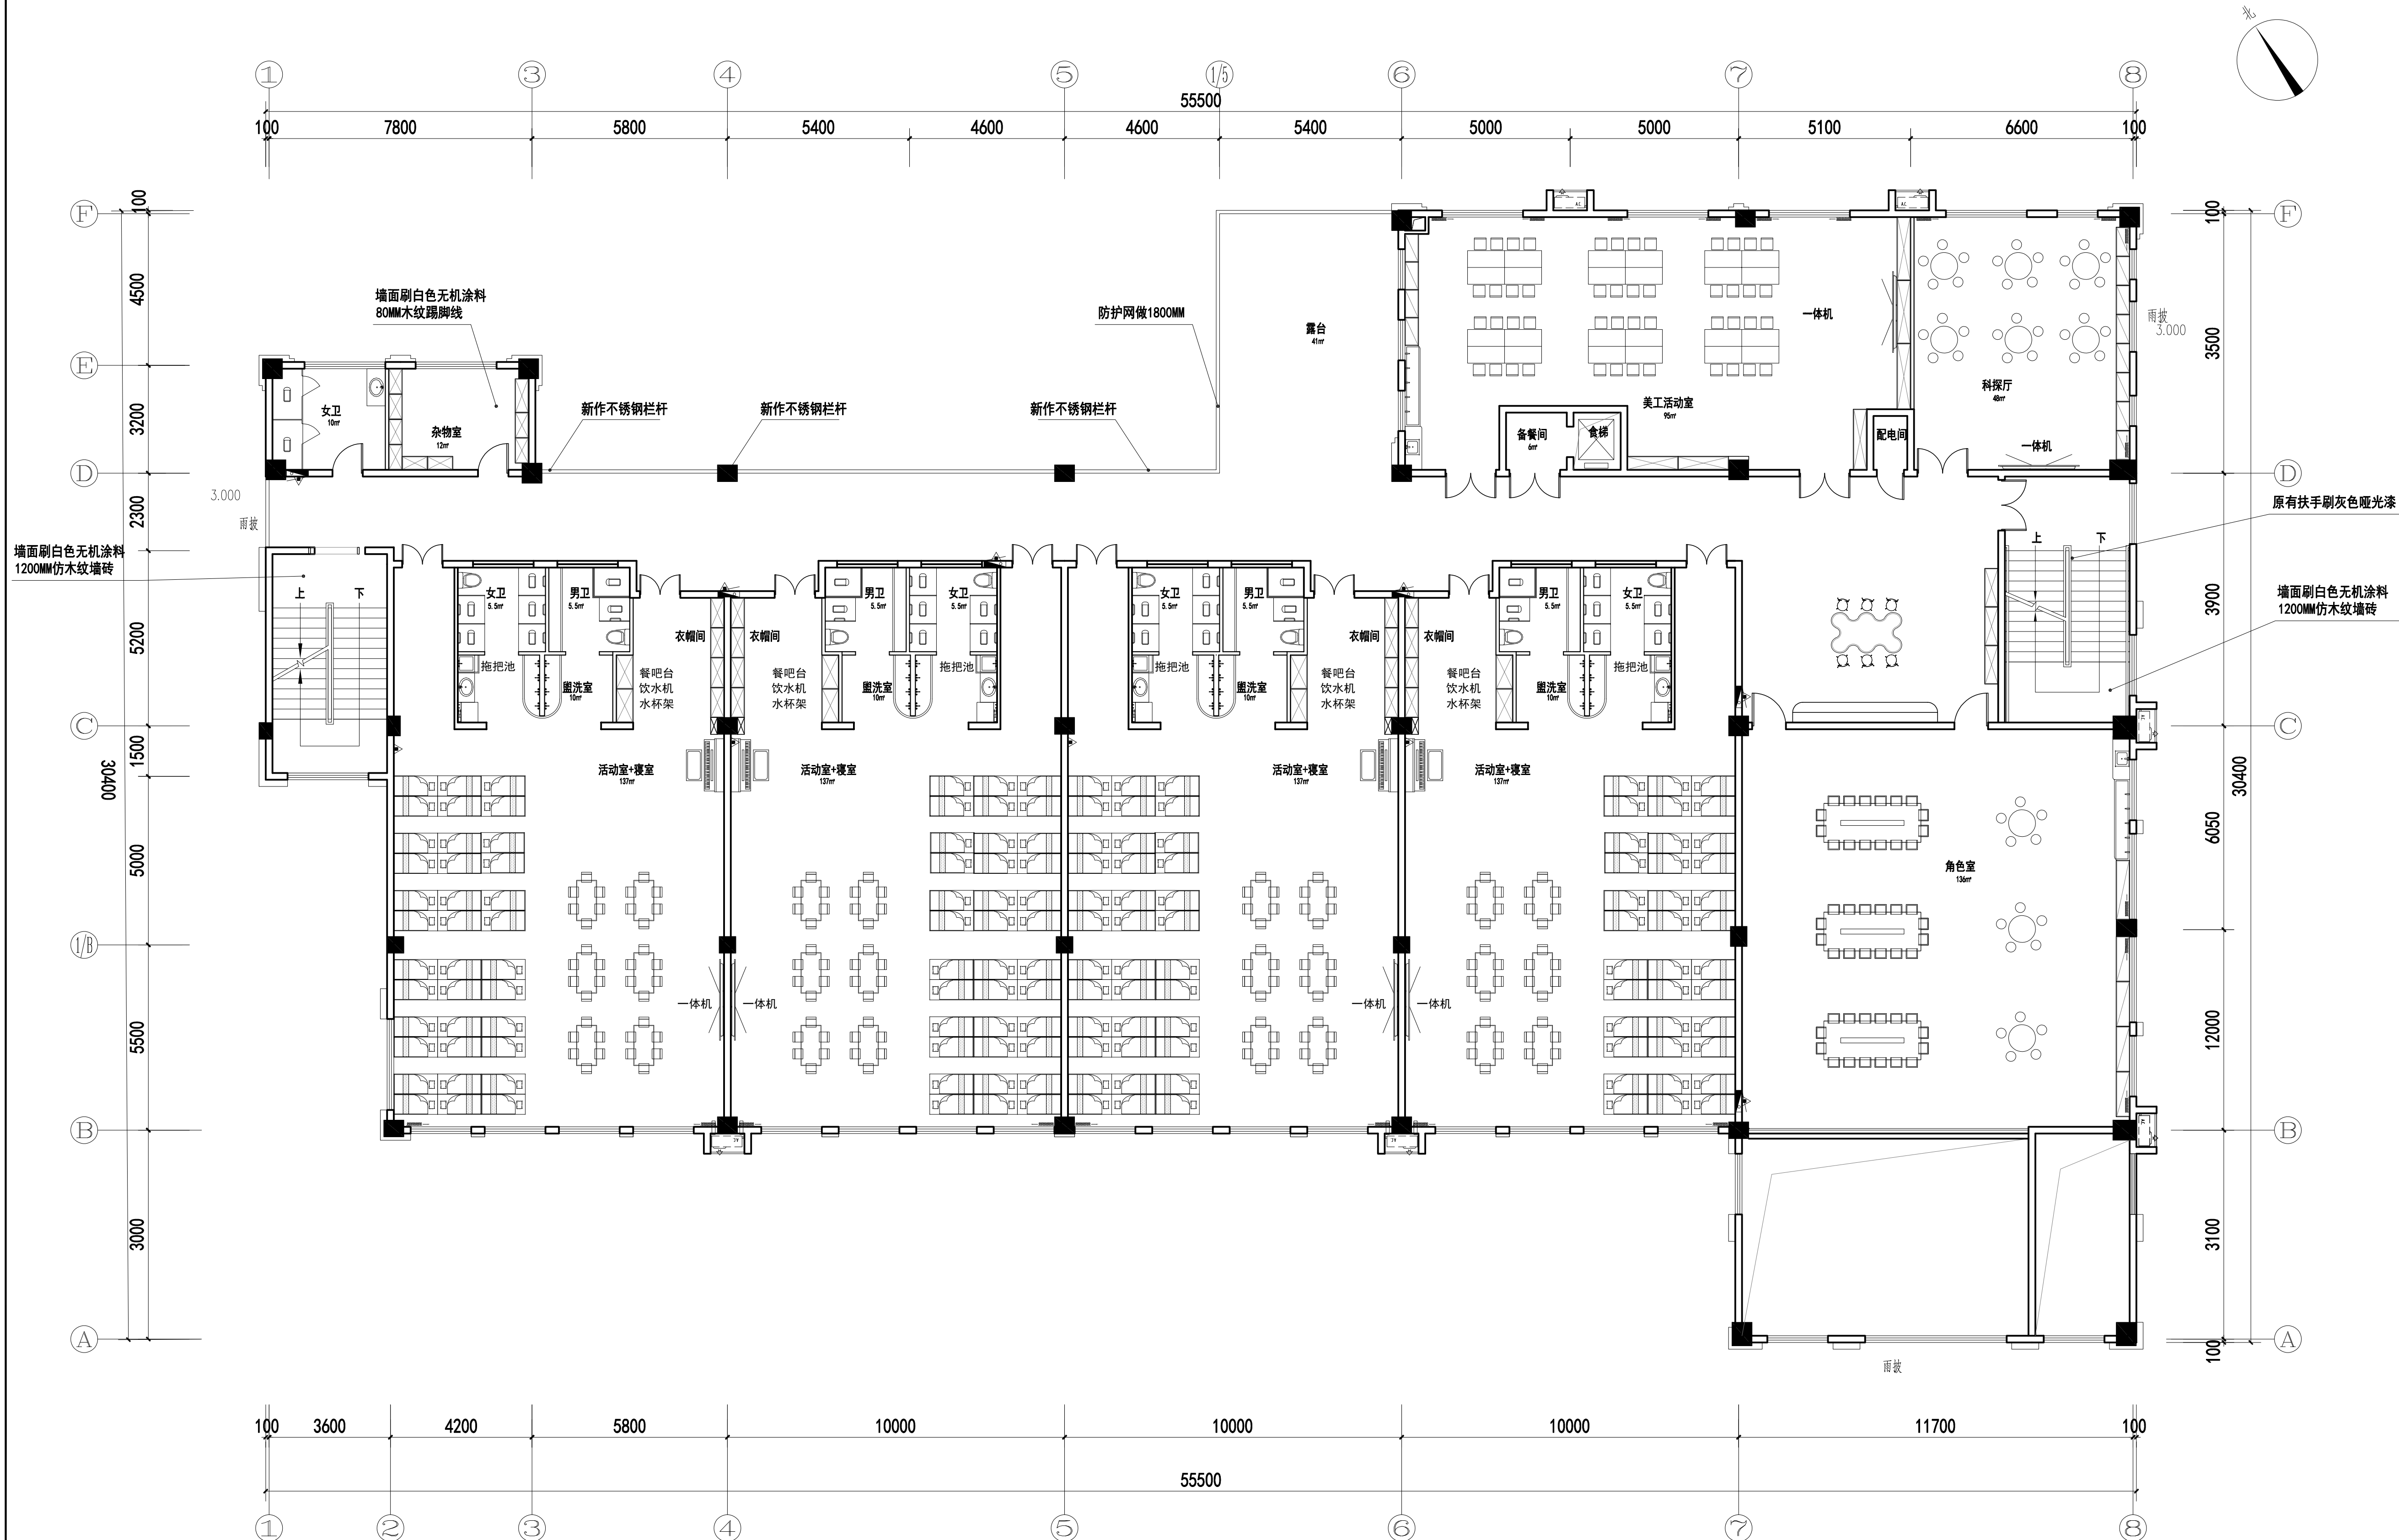

FF PLAN 平潭富春城幼儿园
Scale: 1:100 二层平面布置图



TIM(SHANG HAI) SIRSPACE DESIGN CO.,LTD
福州安润福设计工程有限公司
TEL:+86-591-88067888
FAX:+86-591-83329099
E-M:TIMSPACE@163.COM
F-T:800-820-2780

CLIENT (项目名称):

平潭富春城幼儿园二次装修

JOB LOCATION (项目位置):

平潭

JOB NO. (项目编号):

T/D20211012

DESIGN APPROVAL (出图盖章处):

Remarks (说明):

1. 本设计为方案所有权属本公司, 未经公司盖章不得擅自使用。
2. 施工图纸上的图形、文字、说明等, 的著作权属本公司, 施工结束后收回其使用权。
3. 施工应符合《建筑内部装修设计防火规范》GB50222-95规定。
4. 现场尺寸由施工单位负责核实, 施工单位必须具备图纸翻样能力, 在施工中应保证外形尺寸不变的情况下内部构造允许进行调整; 若发现其与施工图纸的标注有出入等, 施工单位有责任立即通知本公司; 否则, 施工单位须承担所有责任。

DESCRIPTION (内容):

三层平面布置图


项目负责人 APPROVED DIRECTOR BY	彭晓	
设计负责人 PROJECT DIRECTOR BY	彭晓	
审核 CHECK	陈锋	
设计人 DESIGNED BY	黄章翔	
制图 DRAWING	黄章翔	
图别 STATUS	A1	
比例 SCALE	1:100	
制图日期 DNG. DATE	2021/11/27	
修改日期 MODIFY DATE		

图号
DRAWING No.
FF-3.0

序号
No.
17

CLIENT'S APPROVAL (客户确认):

DATE (日期):

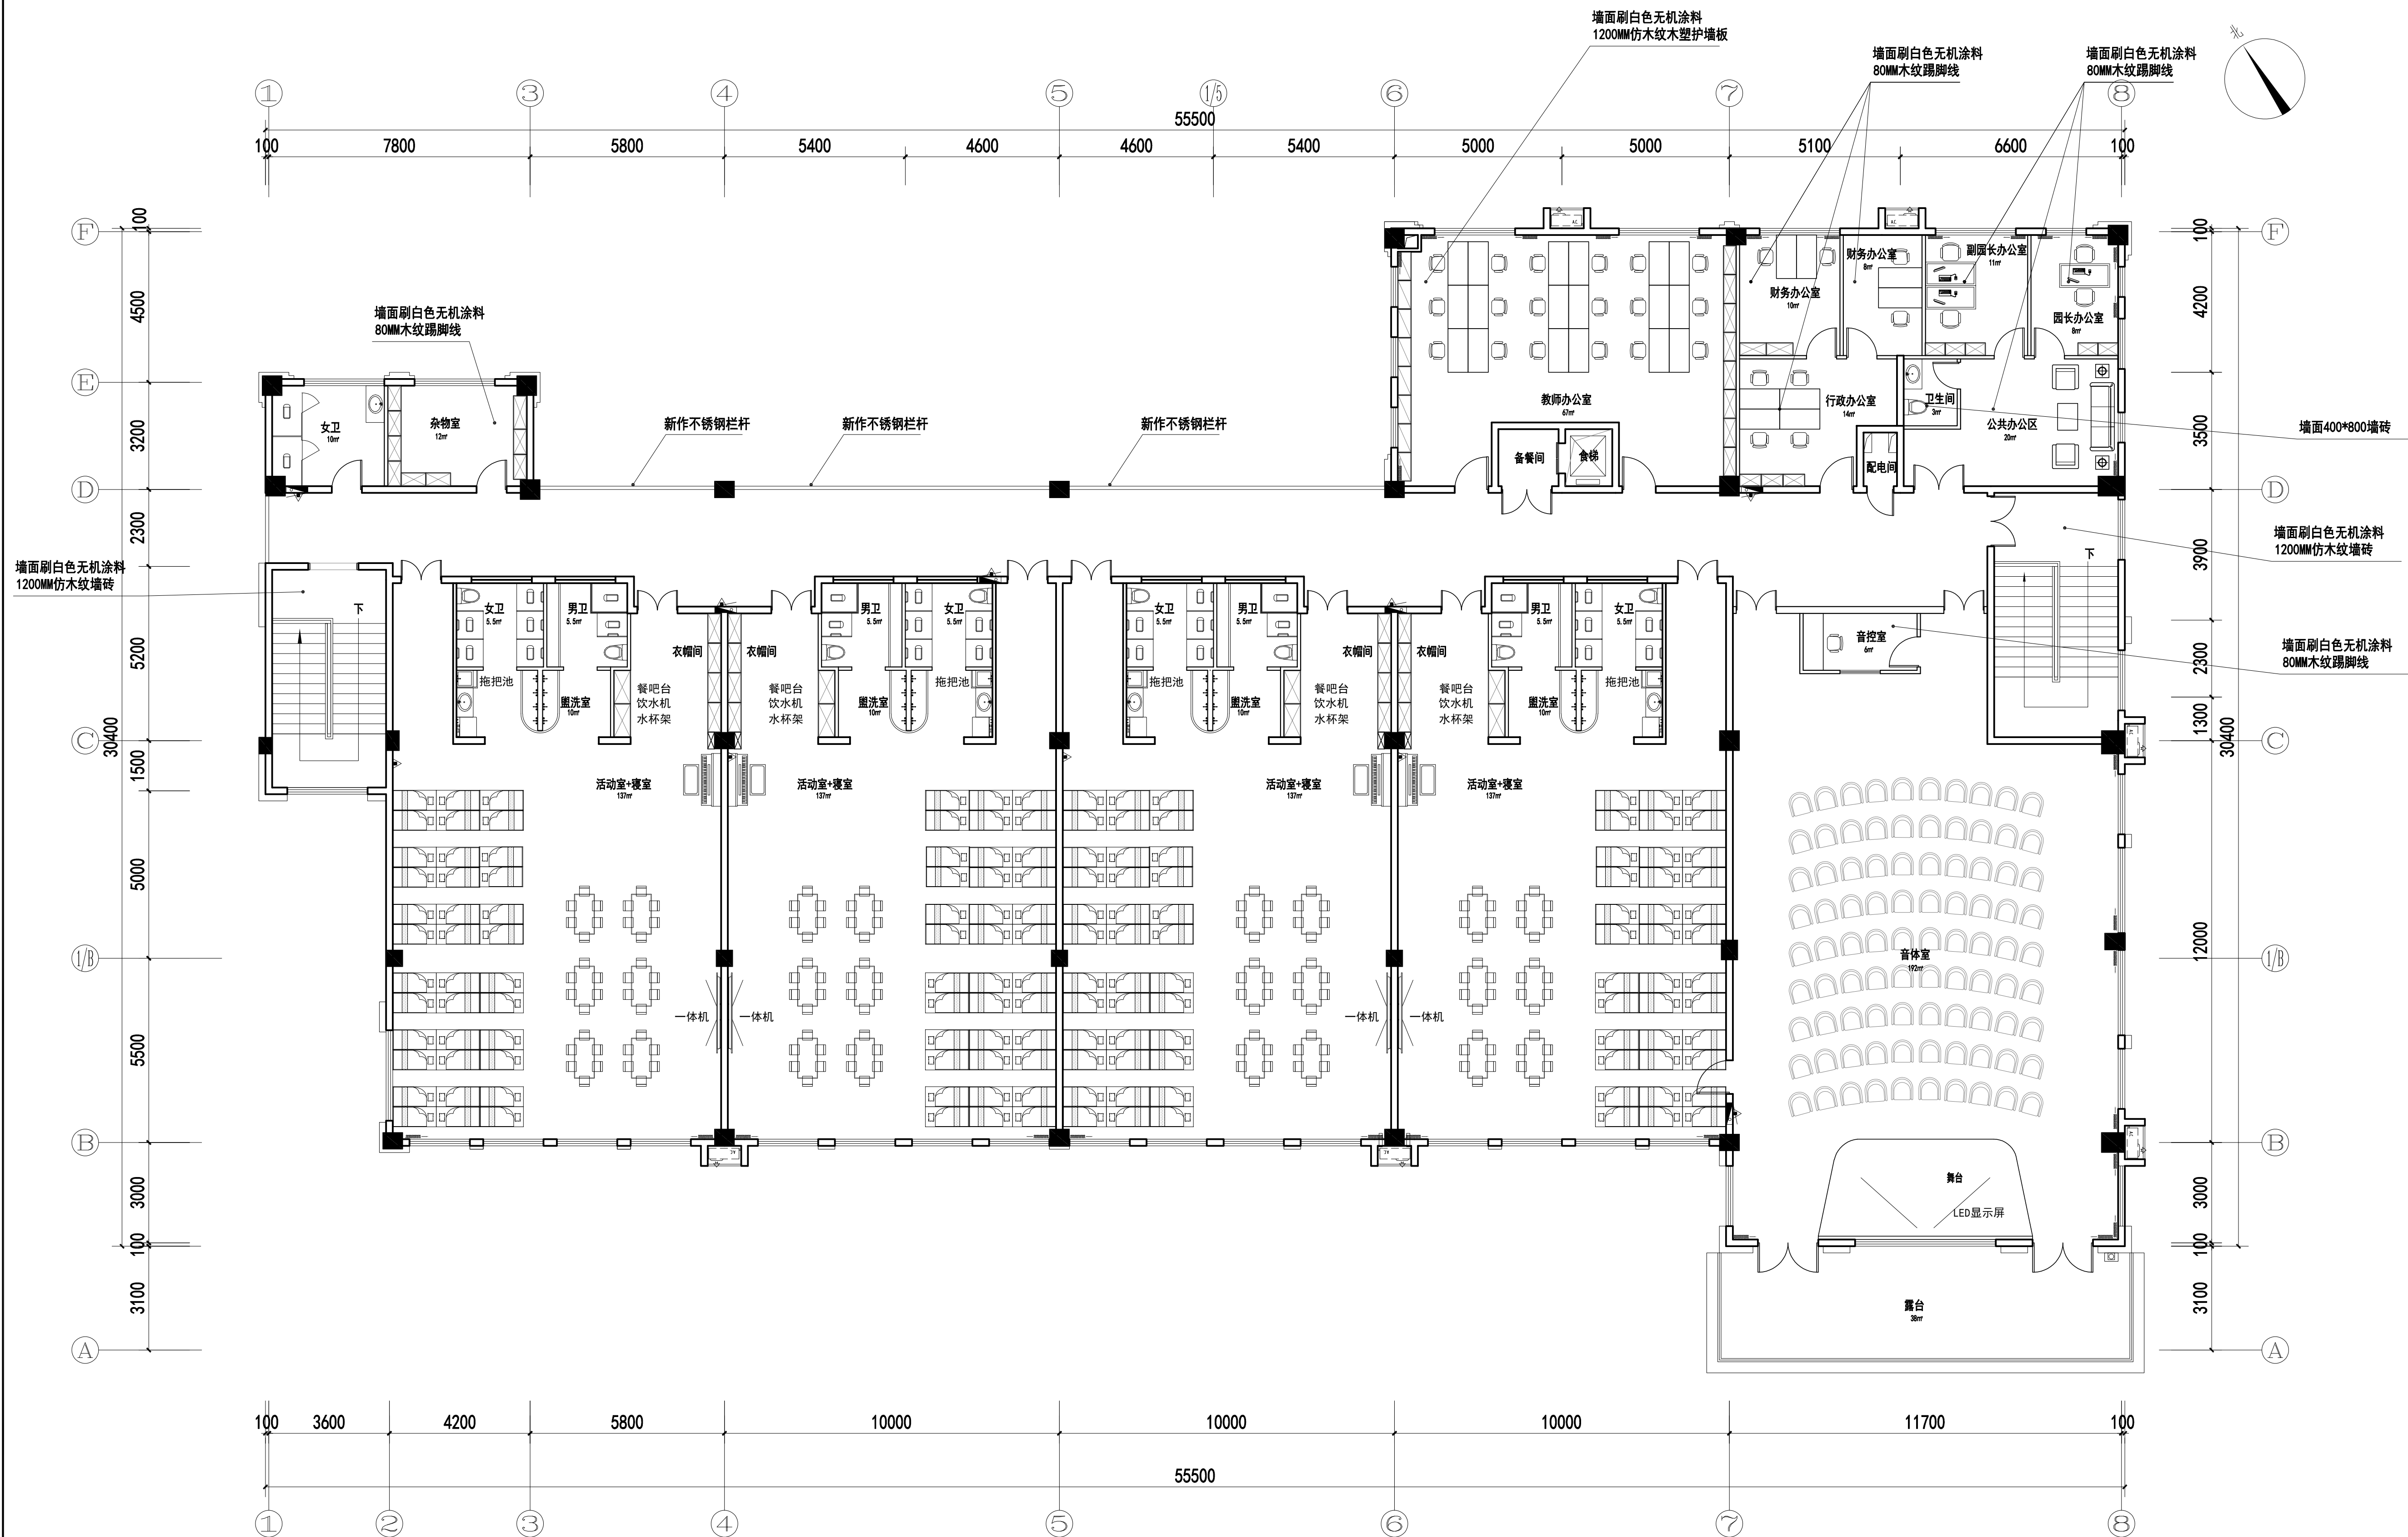

FF PLAN 平潭富春城幼儿园
Scale: 1:100 三层平面布置图



TIM(SHANG HAI) SIRSPACE DESIGN CO.,LTD
福州安润福设计工程有限公司
TEL:+86-591-88067888
FAX:+86-591-83329099
E-M:TIMSPACE@163.COM
F-T:800-820-2780

CLIENT (项目名称):

平潭富春城幼儿园二次装修

JOB LOCATION (项目位置):

平潭

JOB NO. (项目编号):

T/D20211012

DESIGN APPROVAL (出图盖章处):

Remarks(说明):

- 1.本设计为案所有权属本公司,未经公司盖章不得擅自挪用。
- 2.施工图纸上的图形、文字、说明等,的著作权属本公司,施工结束后收回其使用权。
- 3.施工应符合<建筑内部装修设计防火规范> GB50222-95规定。
- 4.现场尺寸由施工单位负责核实,施工单位必须具备图纸翻样能力,在施工中应保证外形尺寸不变的情况下内部构造允许进行调整;若发现其与施工图纸的标注有出入等,施工单位有责任立即通知本公司;否则,施工单位须承担所有责任。

DESCRIPTION (内容):


操场索引总平面图

项目负责人 APPROVED DIRECTOR BY	彭晓	
设计负责人 PROJECT DIRECTOR BY	彭晓	
审核 CHECK	陈锋	
设计人 DESIGNED BY	黄章翔	
制图 DRAWING	黄章翔	
图别 STATUS	A1	
比例 SCALE	1:100	
制图日期 DNG. DATE	2021/11/27	
修改日期 MODIFY DATE		
图号 DRAWING No.	JS-04	

序号
No. 67

CLIENT'S APPROVAL (客户确认):

DATE (日期):

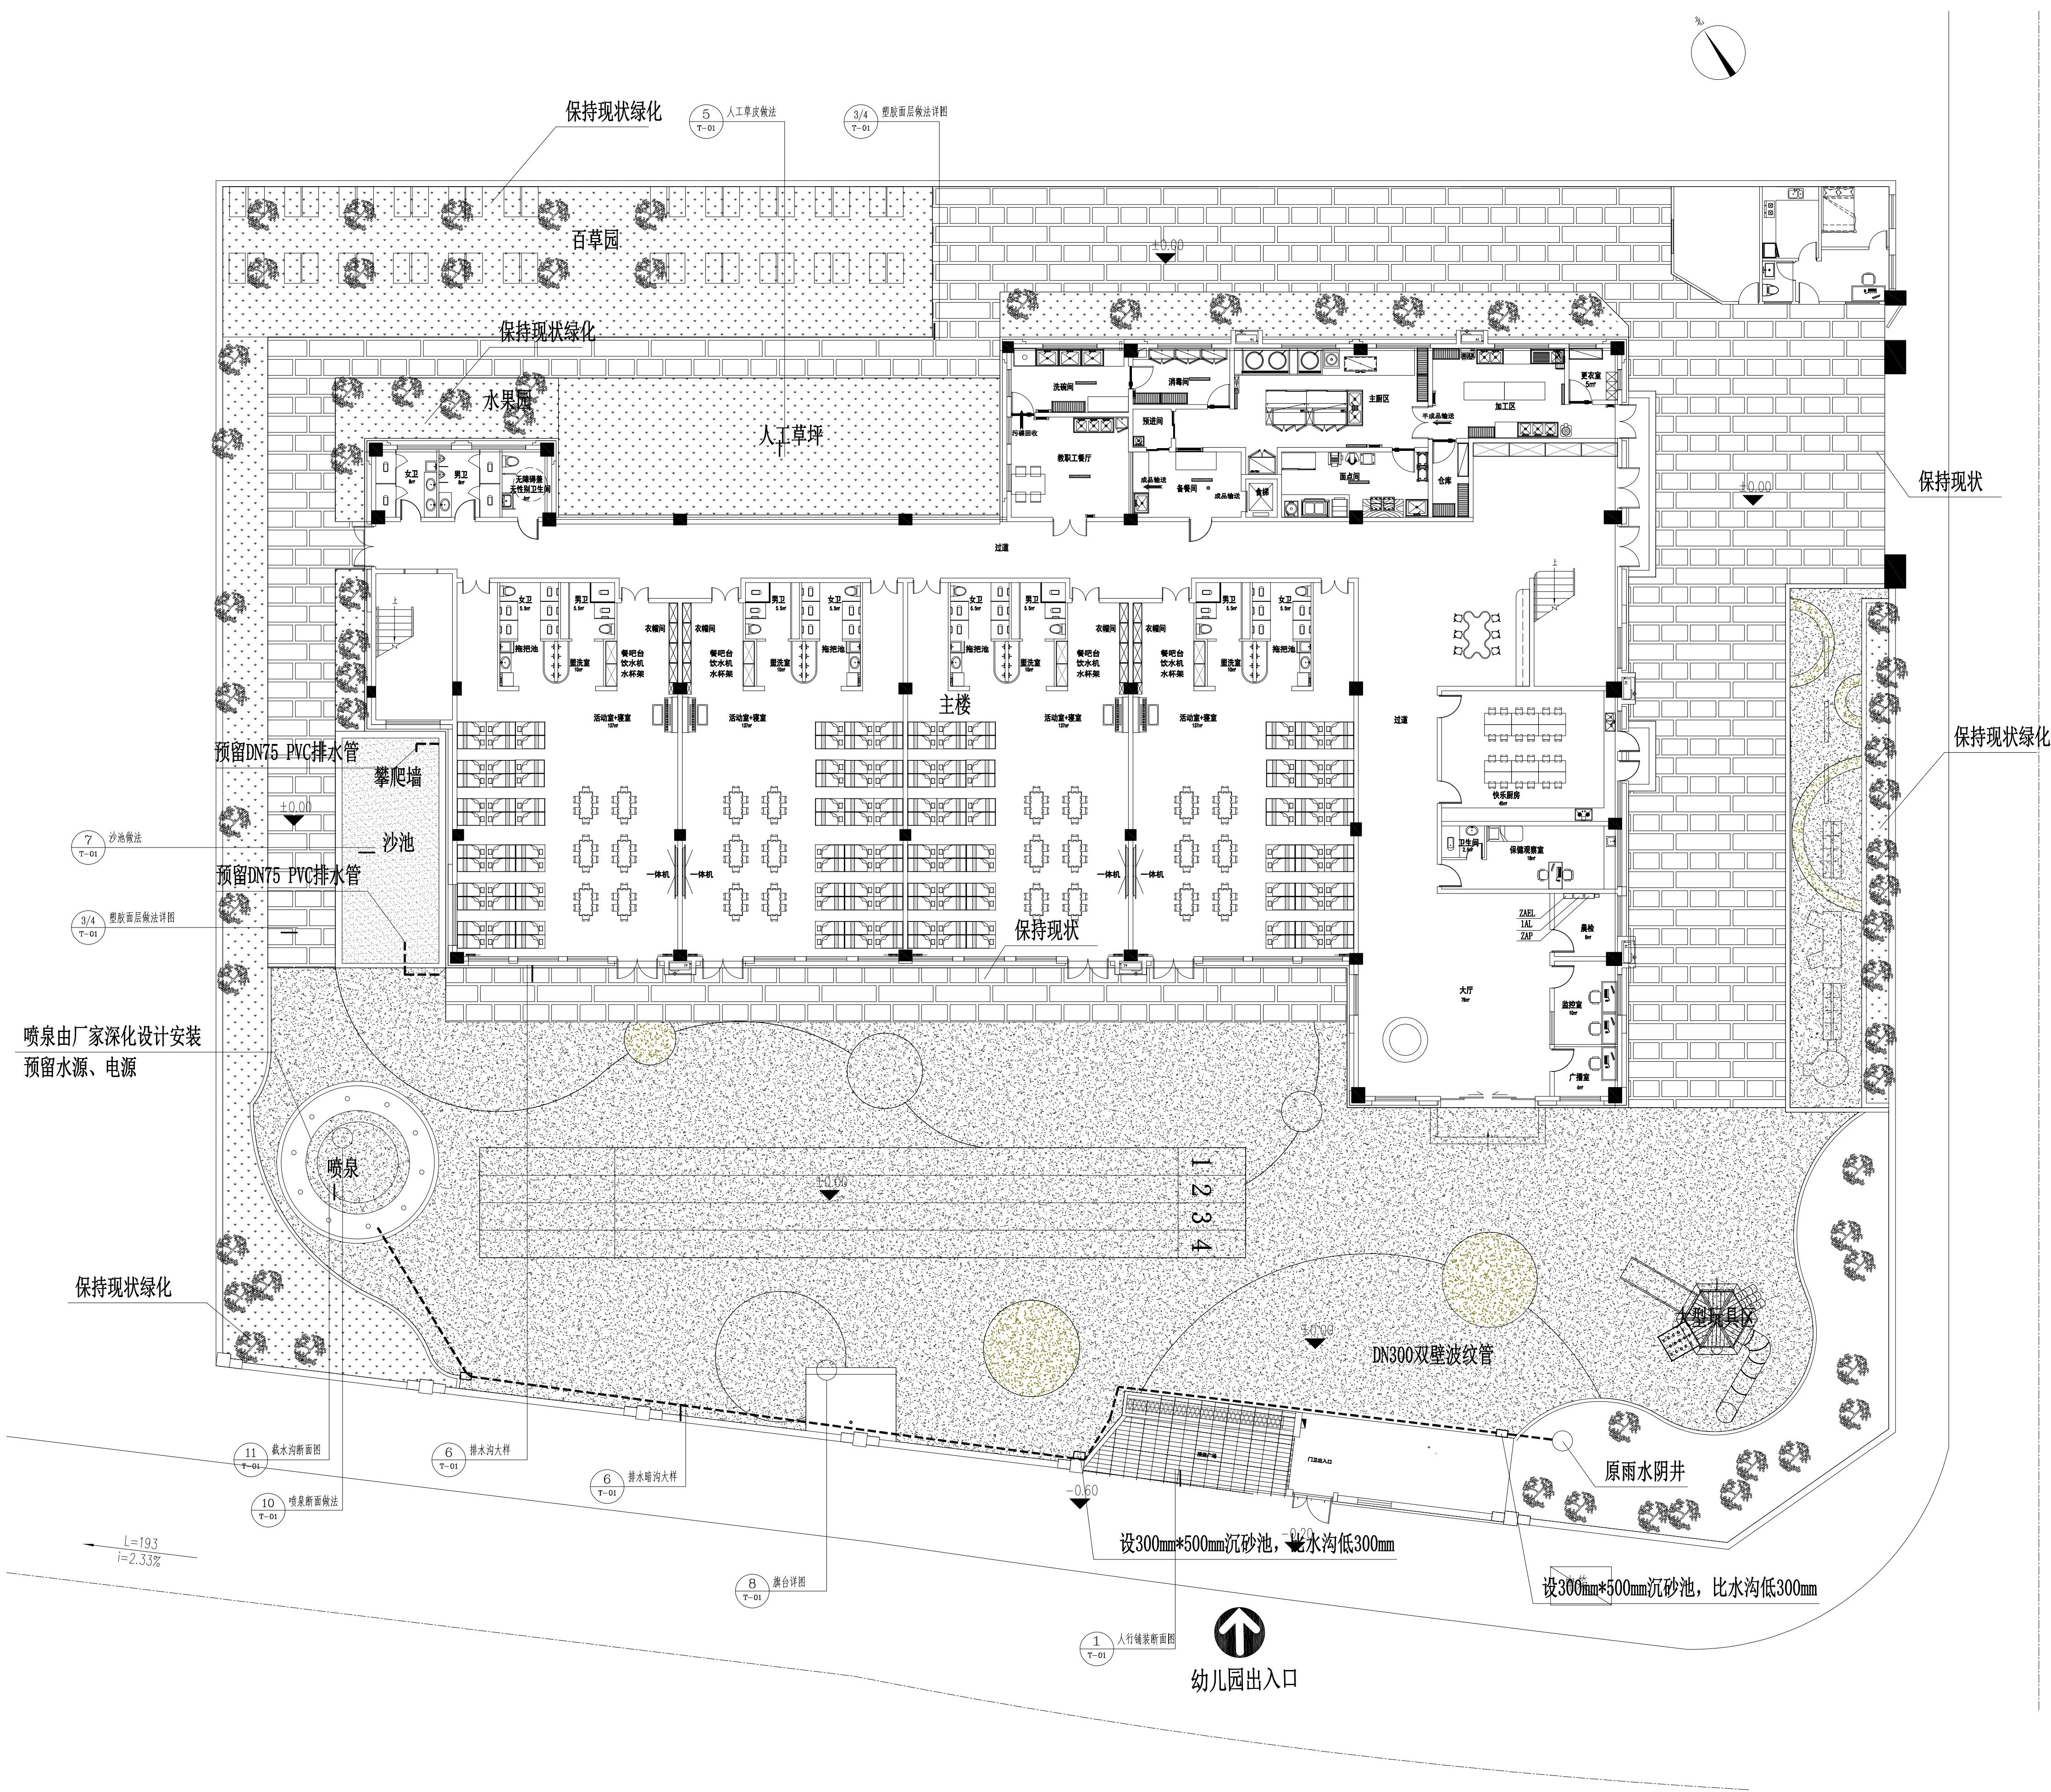

① 操场索引总平面图 1:150