


青峰二期风电场升压站检修楼选址红线图

测绘单位：福州市勘测院平潭分院

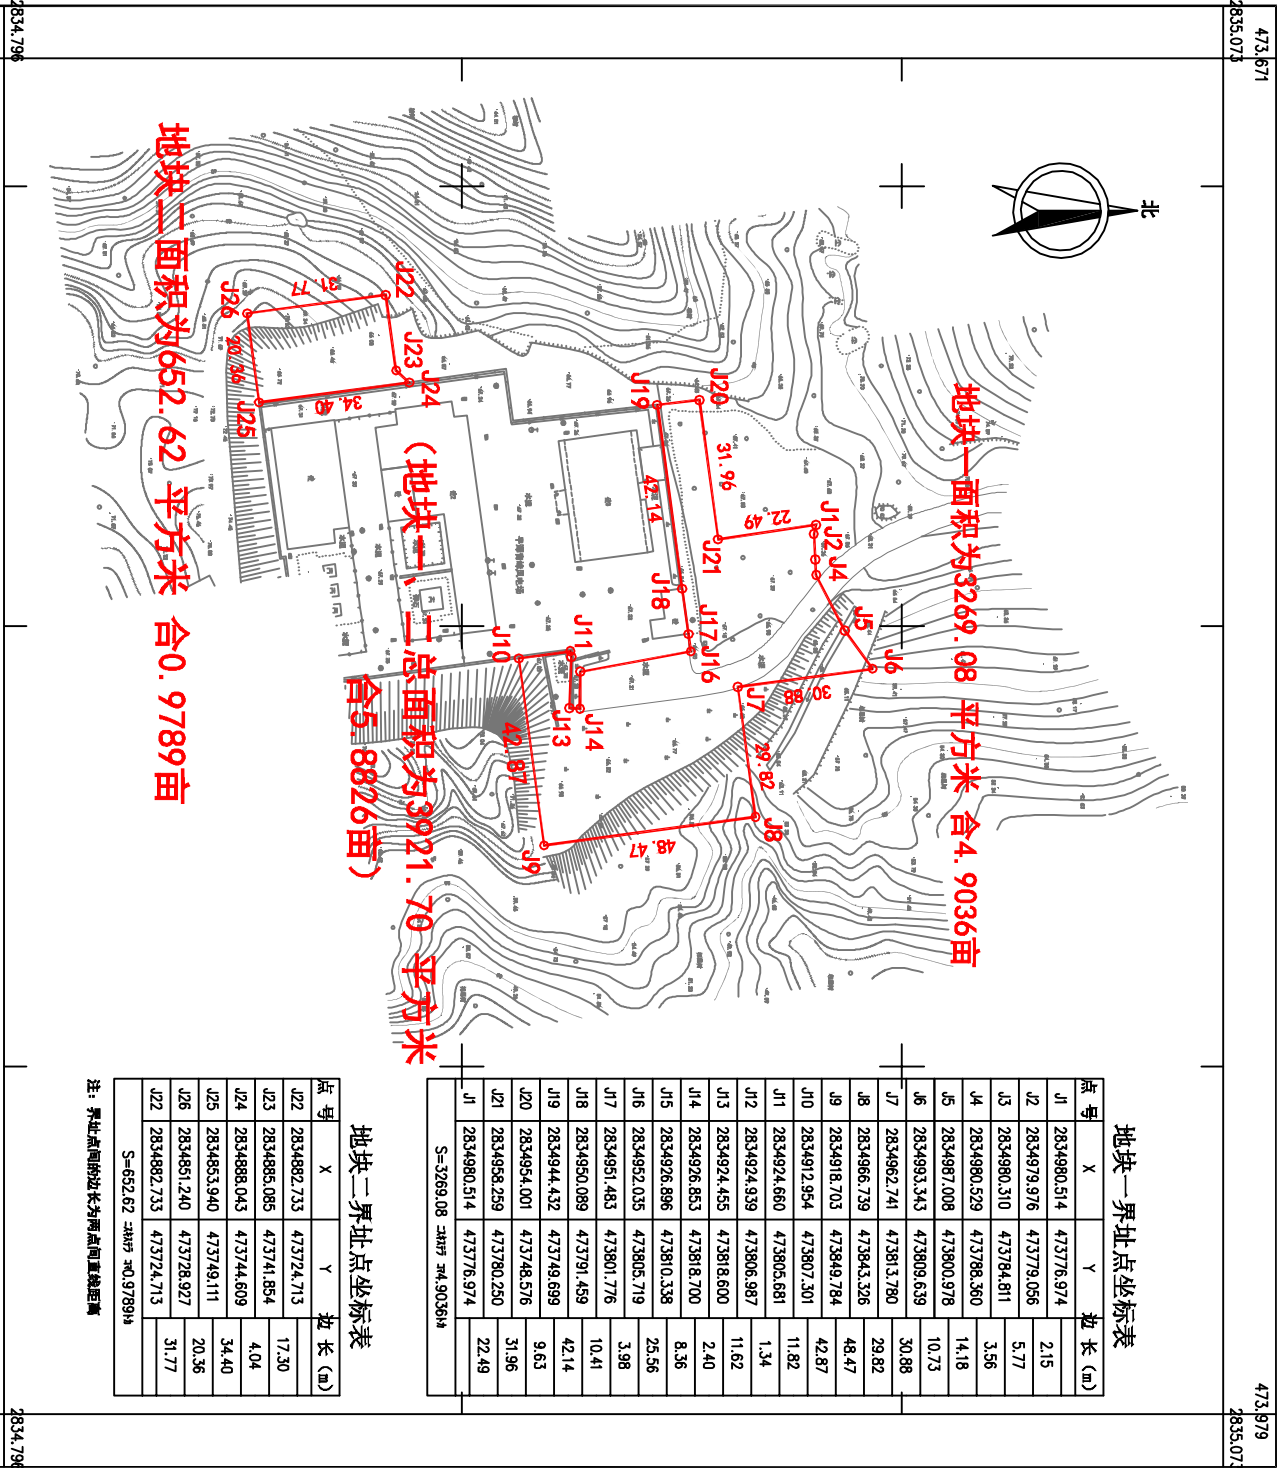

地块一界址点坐标表

点号	X	Y	边长 (m)
J1	2834980.514	473776.974	2.15
J2	2834979.976	473779.056	5.77
J3	2834980.310	473784.811	3.56
J4	2834980.529	473786.360	14.18
J5	2834987.008	473800.978	10.73
J6	2834993.343	473809.639	30.88
J7	2834962.741	473813.780	29.82
J8	2834966.739	473843.326	48.47
J9	2834918.703	473849.784	42.87
J10	2834912.954	473807.301	11.82
J11	2834924.660	473805.681	1.34
J12	2834924.939	473806.987	11.62
J13	2834924.455	473818.600	2.40
J14	2834926.853	473818.700	8.36
J15	2834926.896	473810.338	25.56
J16	2834952.035	473805.719	3.98
J17	2834951.483	473801.776	10.41
J18	2834950.089	473791.459	42.14
J19	2834944.432	473749.699	9.63
J20	2834954.001	473748.576	31.96
J21	2834958.259	473780.250	22.49
J1	2834980.514	473776.974	

S=3269.08 2km² 74.9036h

地块二界址点坐标表

点号	X	Y	边长 (m)
J22	2834882.733	473724.713	17.30
J23	2834885.085	473741.854	4.04
J24	2834888.043	473744.609	34.40
J25	2834853.940	473749.111	20.36
J26	2834851.240	473728.927	31.77
J22	2834882.733	473724.713	

S=652.62 2km² 74.9036h

注：界址点间的边长为两点间直线距离

2010年7月数字化成图
2000国家大地坐标系
1985国家高程基准
2002年福州市勘测院地形图量算，方为正式材料

1:1000

Autodesk 教育版产品制作