


龙南初中（改扩建）工程选址红线图

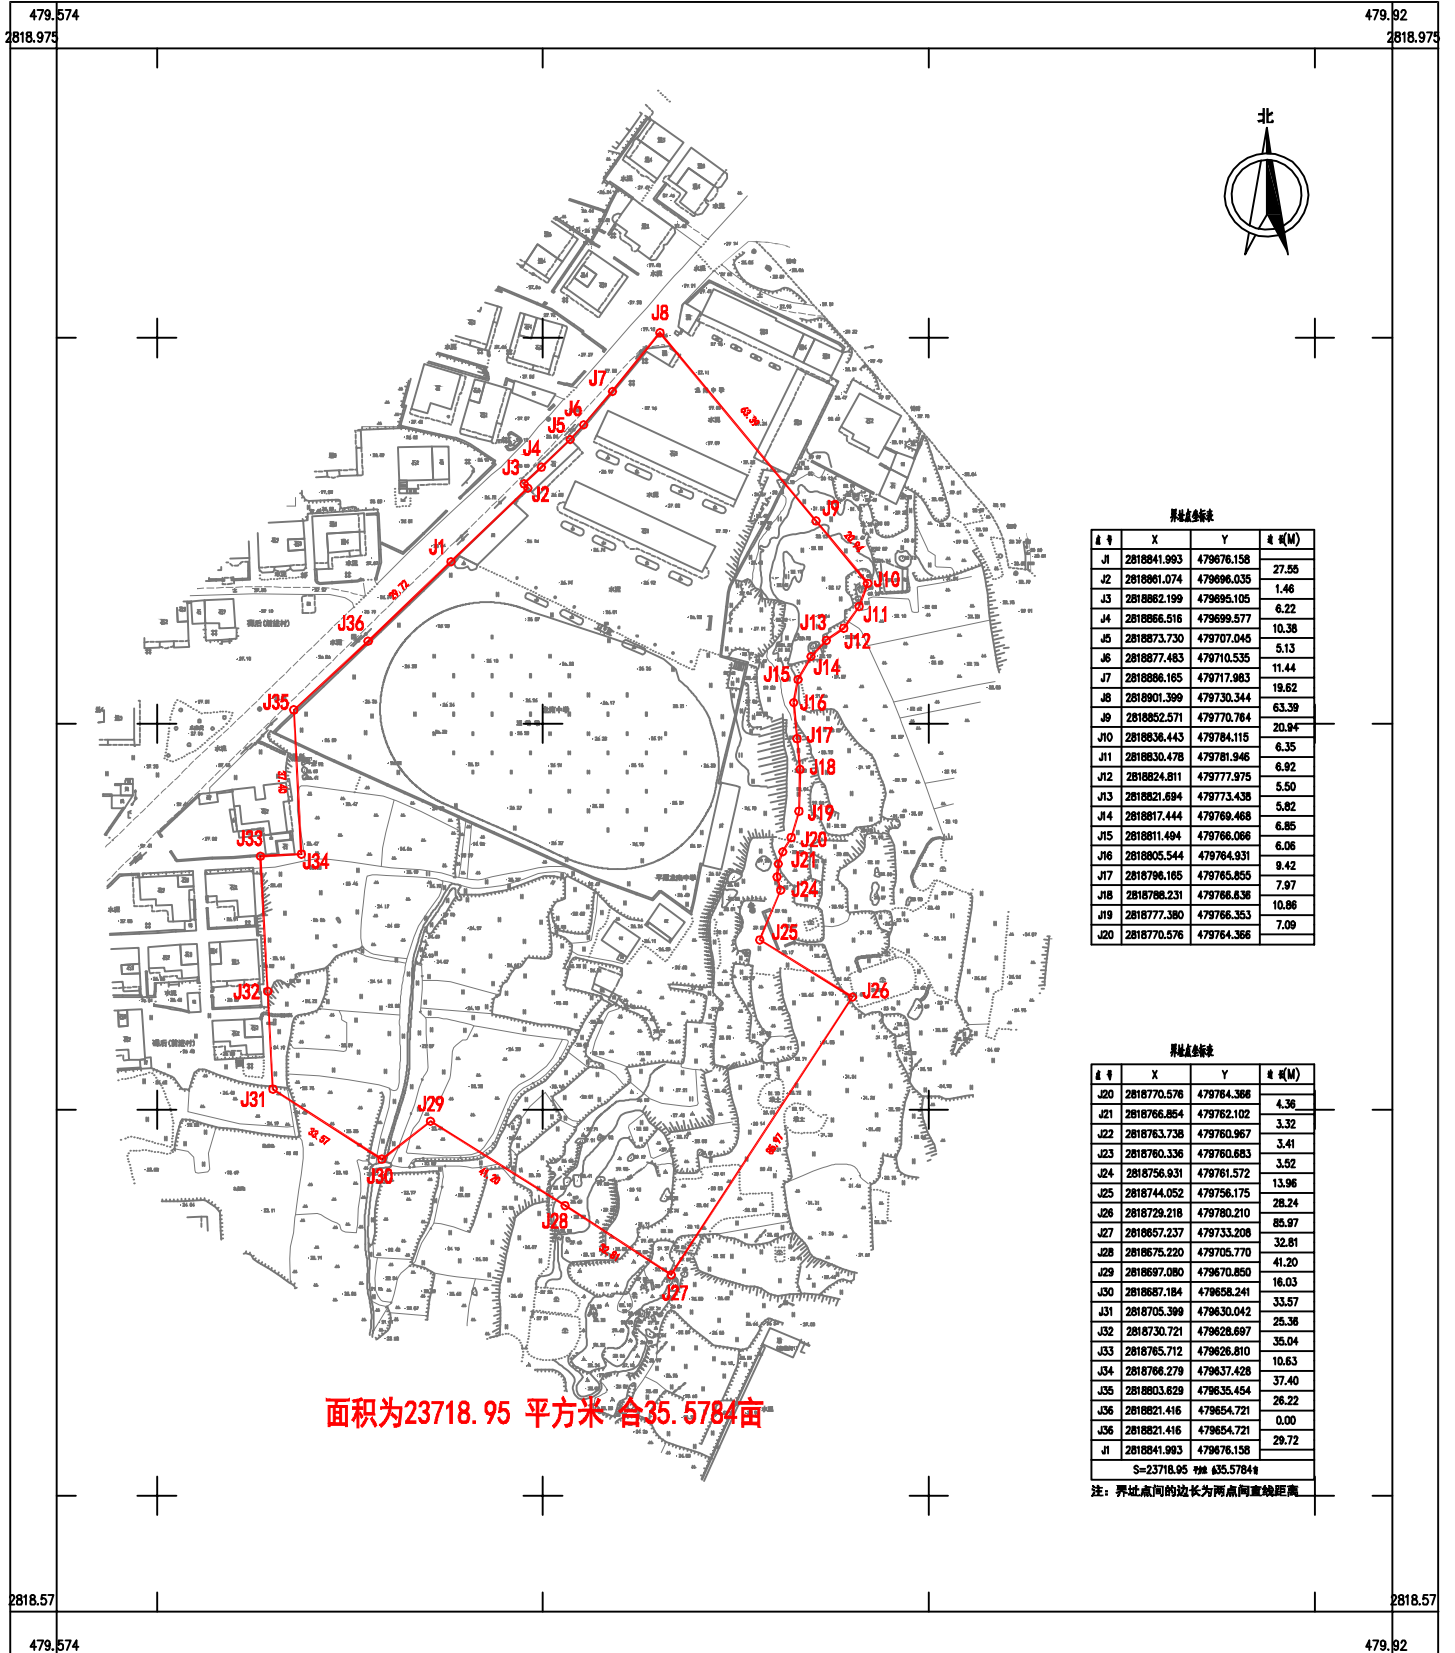

界址点坐标			
点号	X	Y	长度(M)
J1	2818841.993	479676.156	27.55
J2	2818861.074	479686.035	1.46
J3	2818862.199	479685.105	6.22
J4	2818866.516	479699.577	10.36
J5	2818873.730	479707.045	5.13
J6	2818877.483	479710.535	11.44
J7	2818886.165	479717.983	19.62
J8	2818901.399	479730.344	63.39
J9	2818952.571	479770.764	20.94
J10	2818936.443	479784.115	6.35
J11	2818930.478	479781.946	6.92
J12	2818924.811	479777.975	5.50
J13	2818921.694	479773.438	5.82
J14	2818917.444	479769.468	6.85
J15	2818911.494	479766.066	6.06
J16	2818905.544	479764.931	9.42
J17	2818796.165	479765.855	7.97
J18	2818788.231	479766.836	10.86
J19	2818777.380	479766.353	7.09
J20	2818770.576	479764.366	

界址点坐标			
点号	X	Y	长度(M)
J20	2818770.576	479764.366	4.36
J21	2818766.854	479762.102	3.32
J22	2818763.736	479760.967	3.41
J23	2818760.336	479760.683	3.52
J24	2818756.931	479761.572	13.96
J25	2818744.052	479756.175	28.24
J26	2818729.216	479780.210	85.97
J27	2818657.237	479733.208	32.81
J28	2818675.220	479705.770	41.20
J29	2818697.080	479670.850	16.03
J30	2818687.184	479658.241	33.57
J31	2818705.399	479630.042	25.36
J32	2818730.721	479628.697	35.04
J33	2818765.712	479626.810	10.63
J34	2818766.279	479637.428	37.40
J35	2818803.629	479635.454	26.22
J36	2818821.416	479654.721	0.00
J1	2818841.993	479676.156	29.72
S=23718.95 ㎡ 合35.5784亩			

注：界址点间的边长为两点间直线距离

测绘单位：福州市勘测院平潭分院

2010年7月数字化制图
2000国家大地坐标系
1985国家高程基准
2009年福州市地形图影像数据
龙南初中改扩建工程选址红线图，为正式图件

1:1000