


平原镇综合运输服务站用地红线图

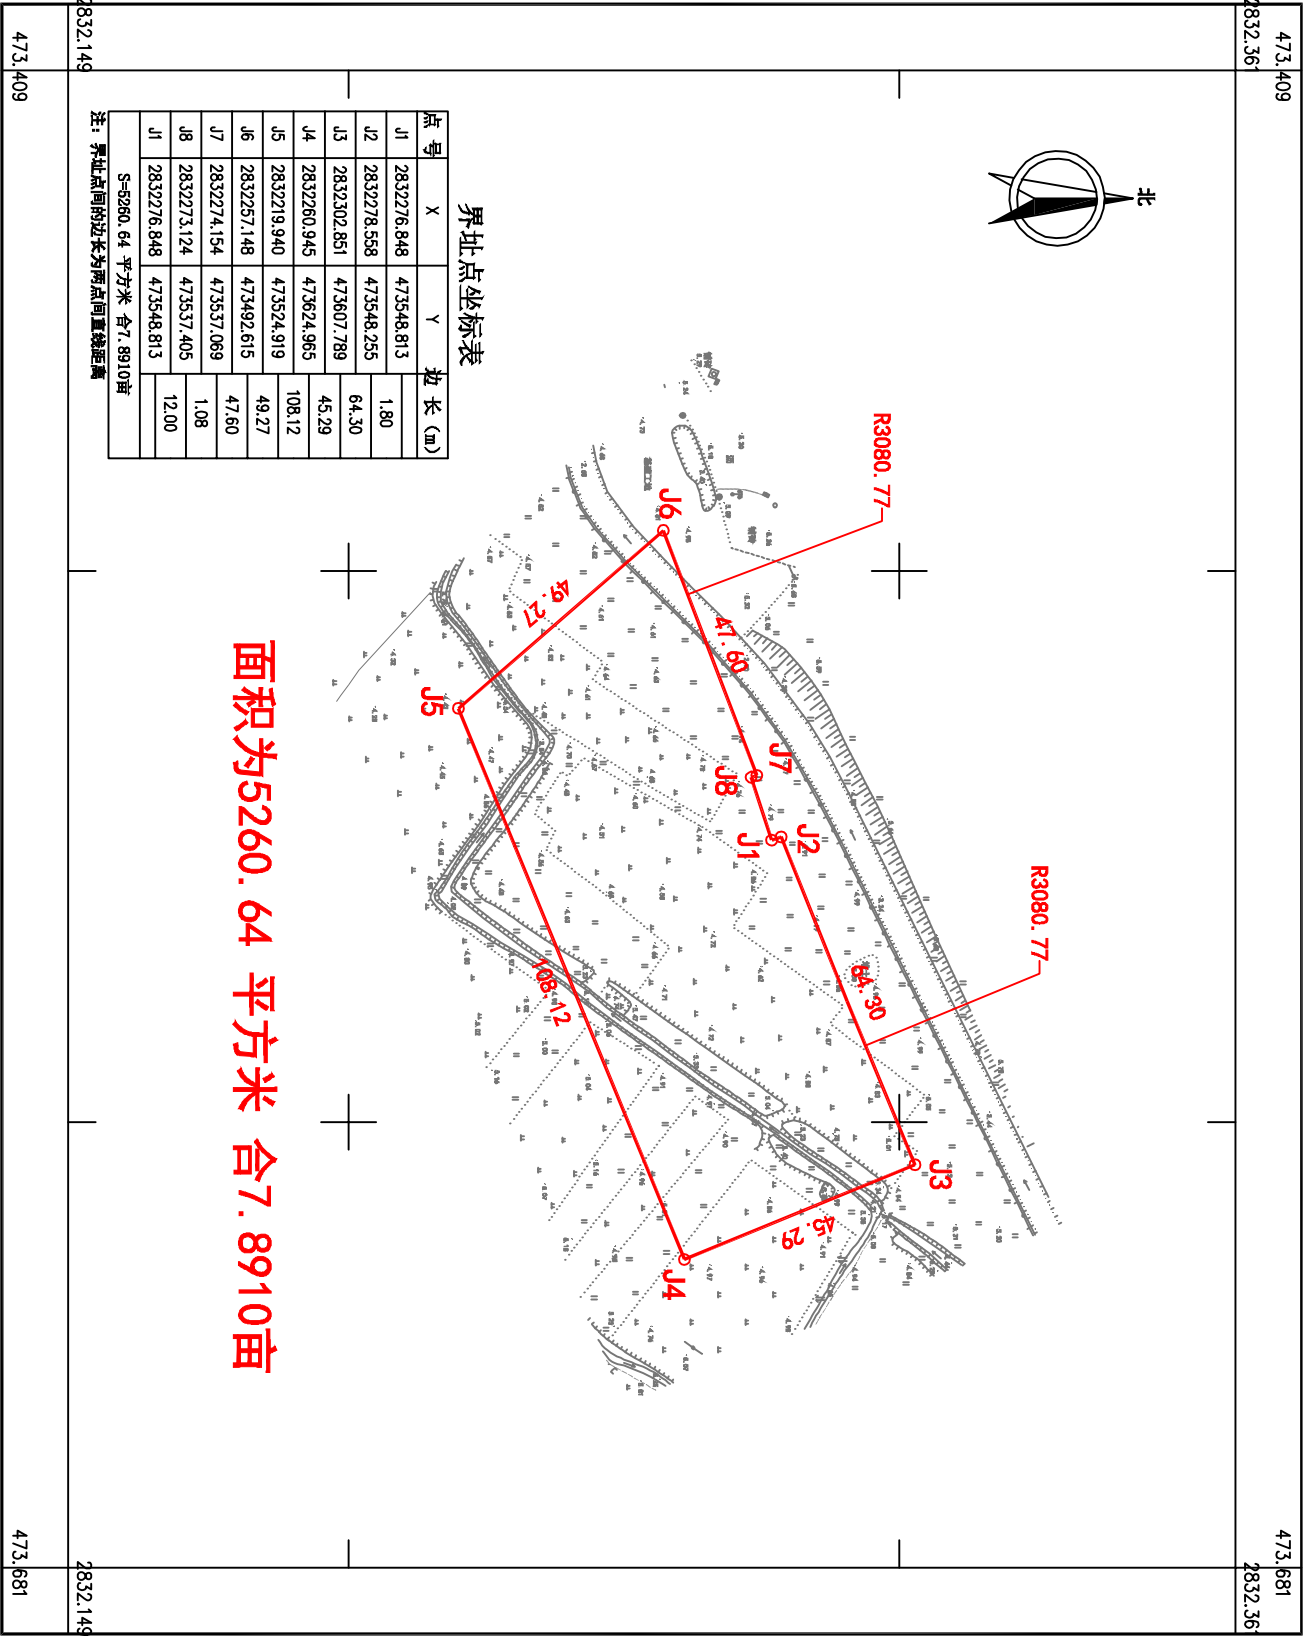

测绘单位：福州市勘测院平潭分院

2019年6月全野外数字测量
2000国家大地坐标系
1985国家高程基准
2009年福州基础地理信息数据图式
加盖福州市勘测院地形图盖章, 方为正式材料

1:1000