


敖东镇钱便澳码头停车场改造选址红线图

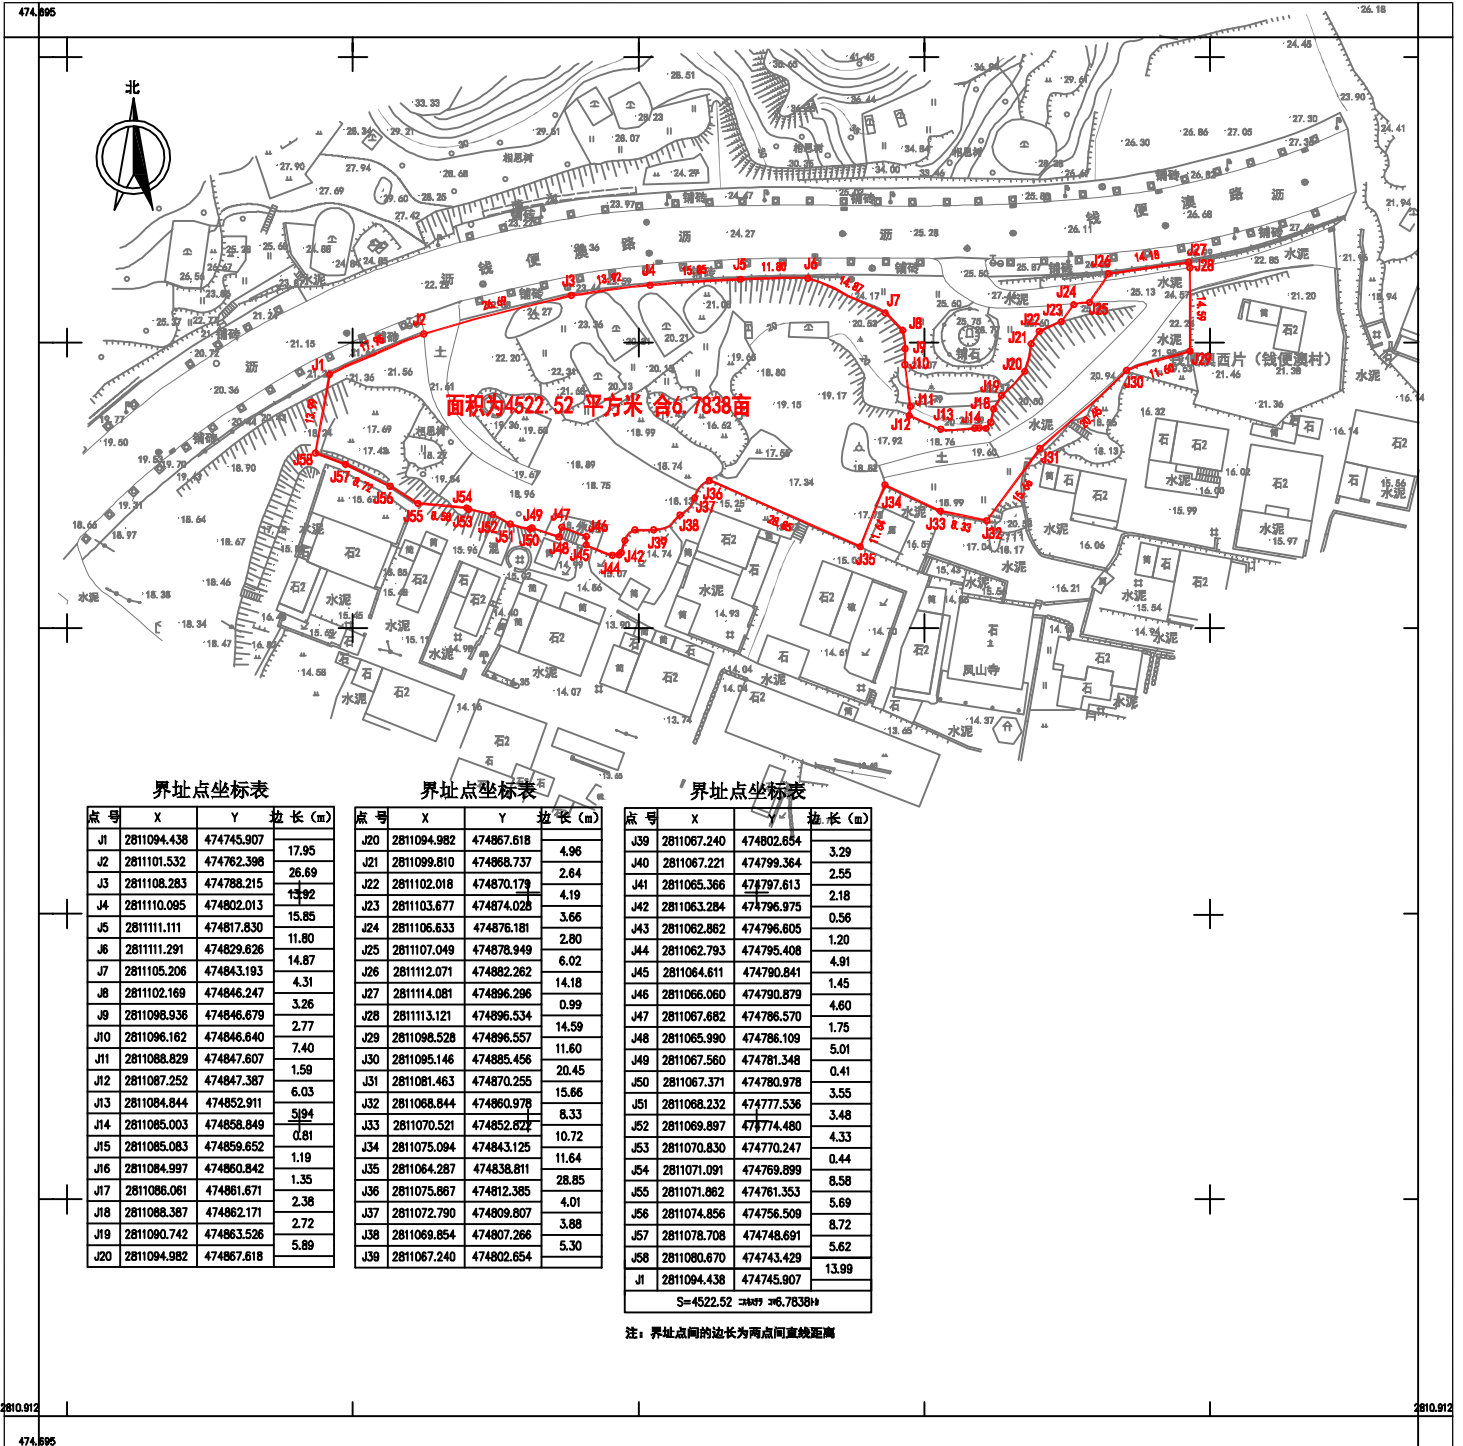

面积为4522.52平方米 合6.7838亩

界址点坐标表

点号	X	Y	边长 (m)
J1	2811094.438	474745.907	17.95
J2	2811101.532	474762.398	26.69
J3	2811108.283	474788.215	13.92
J4	2811110.095	474802.013	15.85
J5	2811111.111	474817.830	11.80
J6	2811111.291	474829.626	14.87
J7	2811105.206	474843.193	4.31
J8	2811102.169	474846.247	3.26
J9	2811098.936	474846.679	2.77
J10	2811096.162	474846.640	7.40
J11	2811088.829	474847.607	1.59
J12	2811087.252	474847.387	6.03
J13	2811084.844	474852.911	5.94
J14	2811085.003	474858.849	0.81
J15	2811085.083	474859.652	1.19
J16	2811084.997	474860.842	1.35
J17	2811086.061	474861.671	2.38
J18	2811088.387	474862.171	2.72
J19	2811090.742	474863.526	5.89
J20	2811094.982	474867.618	

界址点坐标表

点号	X	Y	边长 (m)
J20	2811094.982	474867.618	4.96
J21	2811099.810	474868.737	2.64
J22	2811102.018	474870.179	4.19
J23	2811103.677	474874.028	3.66
J24	2811106.633	474876.181	2.80
J25	2811107.049	474878.949	6.02
J26	2811112.071	474882.262	14.18
J27	2811114.081	474886.296	0.99
J28	2811113.121	474896.534	14.59
J29	2811098.528	474896.557	11.60
J30	2811095.146	474885.456	20.45
J31	2811081.463	474870.255	15.66
J32	2811068.844	474860.978	8.33
J33	2811070.521	474852.822	10.72
J34	2811075.094	474843.125	11.64
J35	2811064.287	474838.811	28.85
J36	2811075.887	474812.385	4.01
J37	2811072.790	474809.807	3.88
J38	2811069.854	474807.266	5.30
J39	2811067.240	474802.654	

界址点坐标表

点号	X	Y	边长 (m)
J39	2811067.240	474802.654	3.29
J40	2811067.221	474799.384	2.55
J41	2811065.366	474797.613	2.18
J42	2811063.284	474796.975	0.56
J43	2811062.862	474796.605	1.20
J44	2811062.793	474795.408	4.91
J45	2811064.611	474790.841	1.45
J46	2811066.060	474790.879	4.60
J47	2811067.682	474786.570	1.75
J48	2811065.990	474786.109	5.01
J49	2811067.560	474781.348	0.41
J50	2811067.371	474780.978	3.55
J51	2811068.232	474777.536	3.48
J52	2811069.897	474774.480	4.33
J53	2811070.830	474770.247	0.44
J54	2811071.091	474769.899	8.58
J55	2811071.882	474761.353	5.69
J56	2811074.856	474756.509	8.72
J57	2811078.708	474748.691	5.62
J58	2811080.670	474743.429	13.99
J1	2811094.438	474745.907	
S=4522.52 合6.7838亩			

注：界址点间的边长为两点间直线距离

测绘单位：福州市勘测院平潭分院

474.695

2000国家大地坐标系
2009年福州市勘测院信息数据格式
加盖福州市勘测院地形图章，方为正式材料

1:500

2810.912