

地震台周边路网工程选址红线图


476.279

2822.007

477.129

2822.007

面积为21745.13 平方米 合32.6177亩

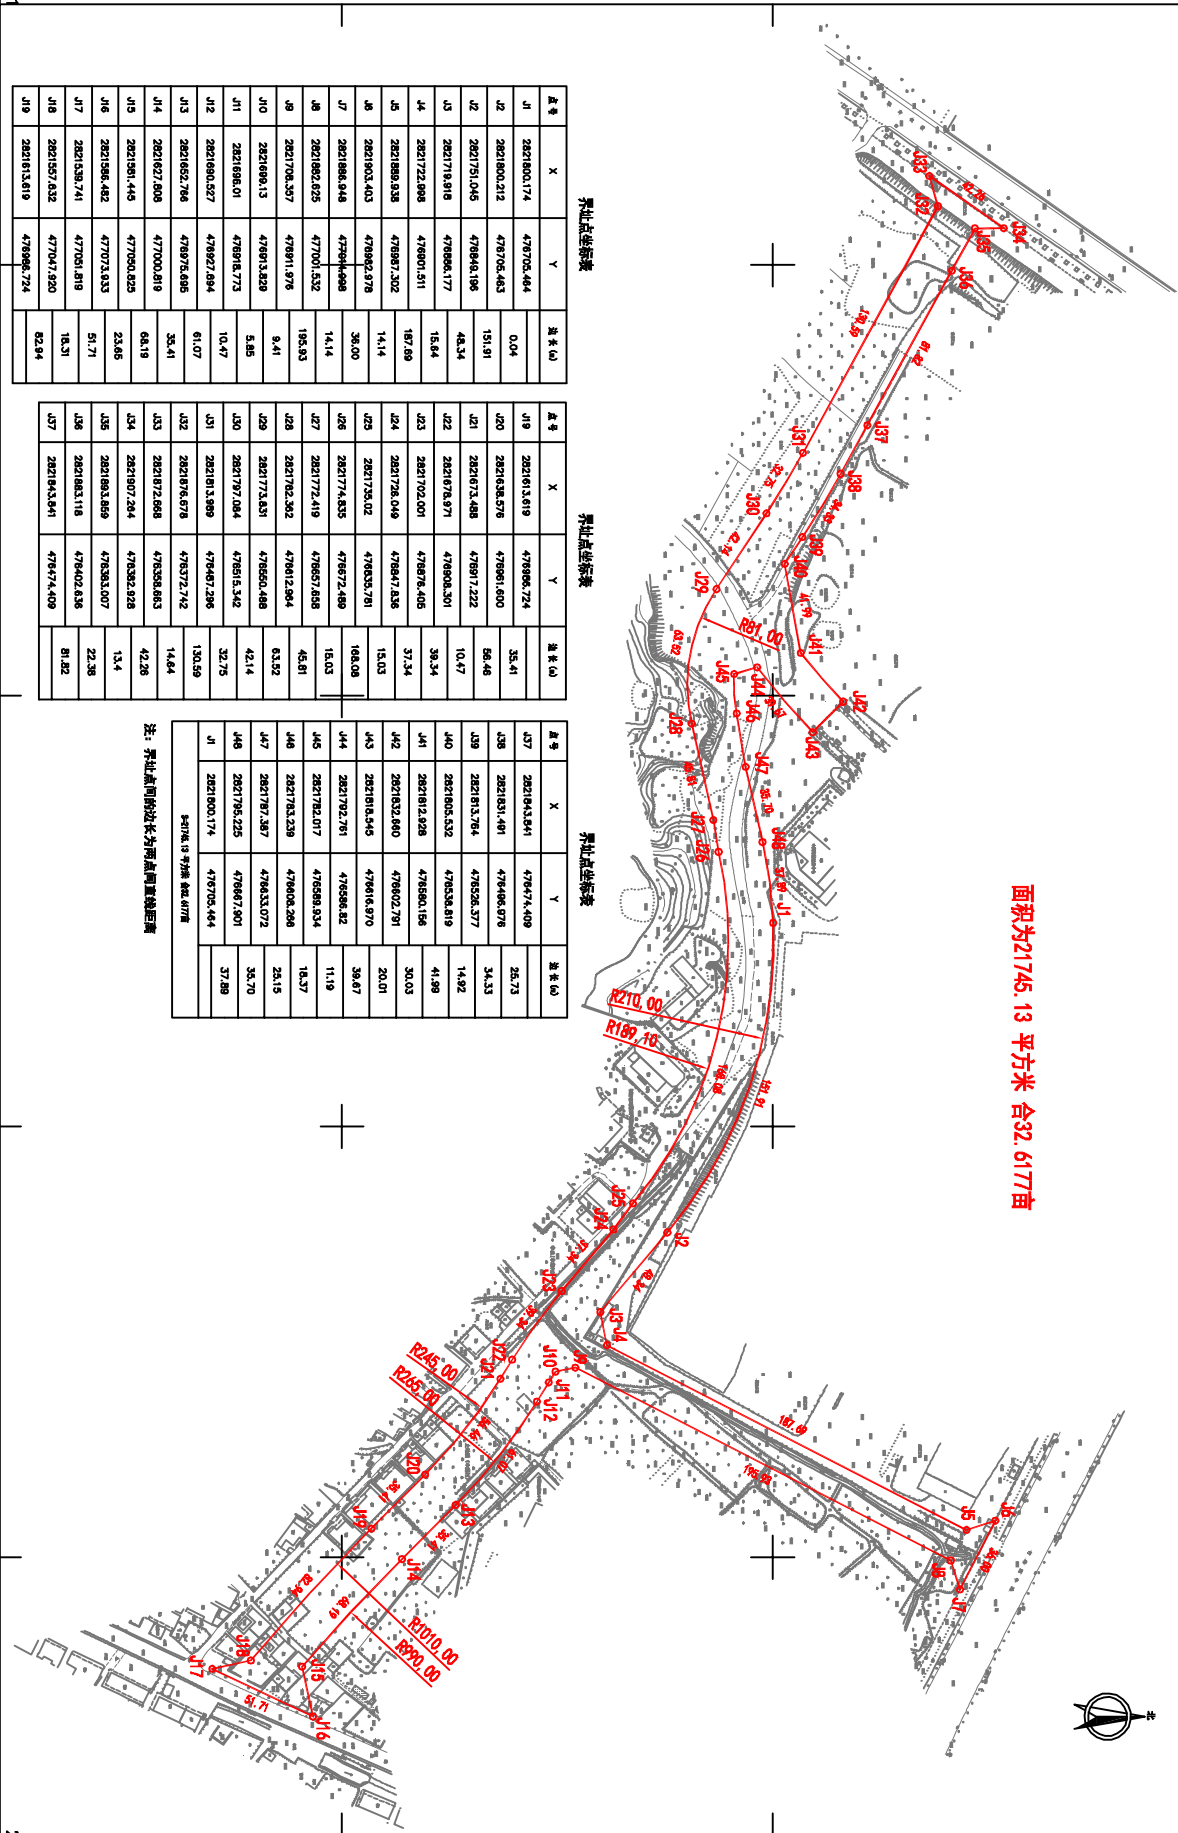

界址点坐标表

点号	X	Y	距离(m)
J1	2821800.174	476705.464	0.04
J2	2821800.212	476705.463	151.91
J2	2821751.046	476646.196	48.34
J3	2821719.818	476664.177	15.64
J4	2821722.988	476601.511	187.89
J5	2821889.838	476667.302	14.14
J6	2821803.403	476662.978	38.00
J7	2821888.848	476644.888	14.14
J8	2821882.825	477001.532	195.83
J8	2821708.357	476911.976	9.41
J10	2821698.13	476913.839	5.85
J11	2821698.01	476918.773	10.47
J12	2821690.527	476927.894	61.07
J13	2821652.766	476975.685	35.41
J14	2821627.808	477000.619	68.19
J15	2821581.448	477004.825	23.86
J16	2821586.482	477073.833	51.71
J17	2821535.741	477001.819	18.31
J18	2821557.832	477047.920	82.84
J19	2821813.619	476986.724	

界址点坐标表

点号	X	Y	距离(m)
J19	2821813.619	476986.724	35.41
J20	2821636.578	476961.600	86.46
J21	2821673.488	476917.222	10.47
J22	2821678.971	476908.301	38.34
J23	2821702.001	476878.405	37.34
J24	2821726.049	476847.836	15.03
J25	2821735.02	476835.791	168.08
J26	2821774.835	476872.489	16.03
J27	2821778.419	476857.658	45.81
J28	2821782.262	476812.864	63.52
J29	2821773.831	476850.488	42.14
J30	2821797.064	476815.342	32.75
J31	2821815.989	476847.286	130.59
J32	2821876.678	476872.742	14.64
J33	2821872.688	476538.863	42.28
J34	2821907.264	476582.928	13.4
J35	2821883.869	476583.007	22.38
J36	2821883.118	476402.836	81.82
J37	2821843.641	476474.409	

界址点坐标表

点号	X	Y	距离(m)
J37	2821843.641	476474.409	25.73
J38	2821831.481	476468.978	34.33
J39	2821813.764	476526.377	14.92
J40	2821603.532	476538.819	41.88
J41	2821812.828	476804.166	30.03
J42	2821832.860	476802.791	20.01
J43	2821816.545	476816.970	38.67
J44	2821792.791	476868.82	11.19
J45	2821782.077	476888.934	18.37
J46	2821783.239	476808.286	25.15
J47	2821787.387	476833.072	35.70
J48	2821785.225	476867.901	37.89
J1	2821800.174	476705.464	

注：界址点间的边长为两点间直线距离

测绘单位：福州市勘测院平潭分院

476.279

477.129

2821.441

2010年7月数字化成果
2000国家大地坐标系
1985国家高程基准
2009年福州市基础地理信息数据图式
加盖福州市勘测院地形图底章，方为正式材料

1:2000