
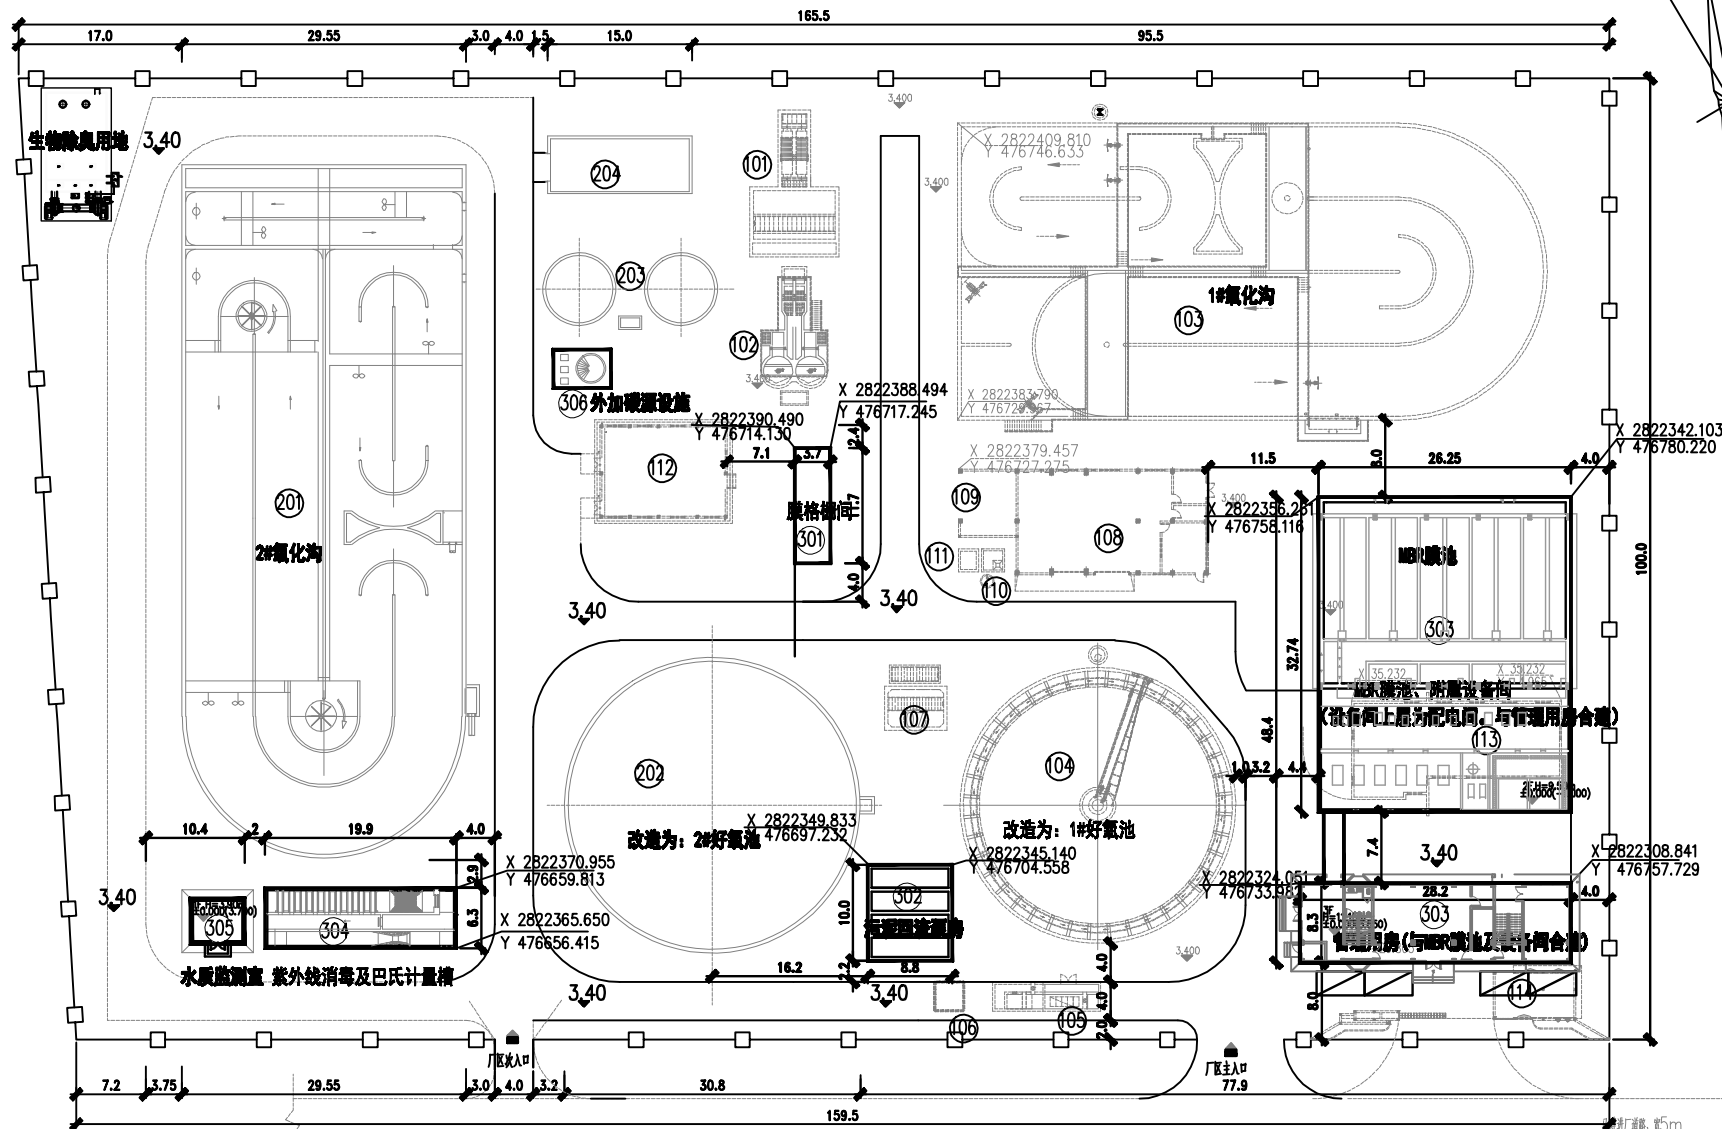


工	士	电	机
艺	建	气	城

项 目	指 标
总征占地面积	16700m ²
围墙内用地面积	16249m ²
总建筑面积	1998.82m ²
地上建筑面积	1820.98m ²
地下建筑面积	177.84m ²
建筑占地面积	1107.8m ²
构筑物占地面积	5933.6m ²
绿地总面积	4849m ²
道路用地面积	4358.6m ²
容积率	0.109
建筑密度	6.82%
建筑系数	43.3%
绿地率	29.85%

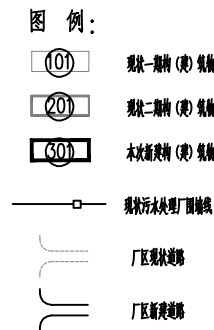

厂区平面布置图 1:500

本工程主要新增建(构)筑物及工程量一览表

编号	名 称	规 格 (mm)	单位	数量	本工程改造及利用情况
①01	细格栅及旋流沉砂器	LxB=15.3x9.3	座	1	设备完好继续使用, 改造后截留4.0mm/d ³
①02	细格栅及旋流沉砂池	LxB=12.7x7.0	座	1	设备完好继续使用, 改造后截留4.0mm/d ³
①03	1#集水池	LxB=61.35x30.9	座	1	新建MBR前池 #集水池, 改造后截留2.0mm/d ³
①04	二沉池	D=28..8	座	1	新建MBR前池 #二沉池, 改造后截留2.0mm/d ³
①05	紫外消毒池	LxB=11.25x3.05	座	1	新建大流量紫外、紫外消毒设备并设计量控制柜后
①06	尾水提升井	LxB=3.00x3.00	座	1	拆除, 池内污泥清理
①07	污泥泵井	LxB=4.65x6.55	座	1	拆除
①08	污泥浓缩、脱水车间	LxB=20.0x11.0	座	1	设备完好继续使用, 改造后截留4.0mm/d ³
①09	污泥堆棚	LxB=7.1x6.2	座	1	本工程继续使用
①10	储泥池	LxB=2.4x2.4	座	1	本工程继续使用
①11	反冲洗水池	LxB=2.1x2.4	座	1	本工程继续使用
①12	变 配 电 间	LxB=13.2x9.7	座	1	本工程继续使用
①13	泵 公 楼	F=666.7m ²	座	1	本工程新建, 池体结构采用MBR膜池及提升机房
①14	传 送 室	F=33m ²	座	1	本工程新建

现状二期建(构)筑物改造及利用情况一览表

编号	名 称	规 格	单位	数量	本工程改造及利用情况
201	2#集水池	Lx _B =72.125m×9.55m	座	1	改造池MBR 池#2 2#集水池改造, 改造后面积2.0万 m ² /d ³
202	二沉池	D ₀ =30m	座	1	改造池MBR 池#2 2#集水池, 改造后面积2.0万 m ² /d ³
203	浓液池	D ₀ =7.0m	座	2	本工程新建池
204	加药间	Lx _B =15.0m×6.0m	座	1	新建池, 改造后面积4.0万 m ² /d ³

说明：1. 本标段建设方提供1:500污水厂厂区总图。

2. 图中尺寸、标高单位为米，1980年坐标系，平面地形高程系。厂区设计地面高程与现状厂区地坪统一，为3.40m。

3. 平流污水厂现状（一期）覆土 $1.0\text{m}/\text{d}^3$ 现状（二期）覆土 $1.0\text{m}/\text{d}^3$ 现状污水厂出水水质执行《城镇污水厂污水处理排放标准》（GB18918—2002）一级B标准。根据当前环保相关要求，本污水厂出水水质标准应执行一级A排放标准。需进行技术改造。同时，根据实际情况，为满足日益增长的进水污水量需求，需要进行扩容，扩容量按 $2.0\text{m}^3/\text{d}$ 。现状、扩容工程完成后，本污水厂日覆土 $4.0\text{m}^3/\text{d}$ 。

4. 污水厂现状扩容技术改造工程在现有厂区范围内进行，不另征用新地。污水厂一期征地16700m²，围填内占地面积16249m²。

5. 本污水厂污水处理采用A/O₂（氧化沟）+MBR膜处理工艺；污泥处理采用带式浓缩脱水一体机工艺。

6. 工程实施前，应严格按照设计提供的流程，确定与工艺流程相匹配后，方可施工。

7. 本图中（黄）线物标的标注尺寸均为黄（物）线物标外尺寸。

8. 厂区内主要车道宽度4m，转弯半径为9.0m。

9. 其他未尽事宜按市政工程施工设计说明。

编号	名 称	规 格	结构形式	单位	数量	备注
⑤01	膜曝气间	LxB=11.7mx3.7m	钢架砼	座	1	膜池4.0 m^3/d ,
⑤02	污泥泥脱水房	LxB=10.0mx8.8m	钢架砼	座	1	膜池4.0 m^3/d
⑤03	MBR膜池、膜池污泥处理池	LxB=48.4mx29.7m,其中 膜池S=530.12 m^2 (2F, S池=352.28 m^2 , S池=177.84 m^2); 污泥池S=702 m^2 (3F)	组合	座	1	膜池4.0 m^3/d 、污泥池停产检修池、膜风房、 污泥池、大文池污泥脱水池。
⑤04	废水收集池及巴氏计量槽	LxB=19.90mx6.30m	钢架砼	座	1	膜池4.0 m^3/d
⑤05	水质监测室	S=26.73 m^2 (1F)	框架	座	1	大文池污泥脱水池
⑤06	外加碳源投加池	LxB=4.0mx6.0m	复合	座	1	膜池4.0 m^3/d 、一份池系多、该份池在池 内加乙酸钠溶液池 (V=20 m^3)1只、膜池大文 池池 Q=1000L/h)3台等池系设备
	厂区土方开挖			万 m^3	0.7	
	厂区新建道路	B=4.0~2.0m	混凝土	m^2	2300	含路面硬化及雨水管网
	厂区修线			项	1	含线路敷设及原有线路拆除
	既有构筑物改造			项	1	
	厂区绿化			项	1	
	厂区现场工程防护			项	1	
	地基处理			项	1	
	生物除臭			项	1	含除臭工程及设计费

● 中国市政工程中南设计研究总院有限公司
CENTRAL AND SOUTHERN CHINA MUNICIPAL
ENGINEERING DESIGN & RESEARCH INSTITUTE

工程设计综合资质甲级A142001257
工程咨询甲级12120070023

图纸专用章:

注册执业章:

施工图审查单位:

施工图审查合格书编号:

工程名称：
平遥县污水处理厂提标扩容技术改造工程

子 项: 污水、污泥处理工程

建设单位: 福建大成环保有限公司

审 定	张卫东	张卫东
设计负责人	周林凡 林文辉	周林凡
专业负责人	李 涛	
审 核	赵红兵	赵红兵
校 对	周林凡	周林凡
设 计	林文辉	
制 图	林文辉	林文辉

图名:

修改后厂区规划建筑总平面布置图

工程编号	排11-201709
------	------------

图 别	方案设计
-----	------

图 号	方-建20
-----	-------

日期 | 2018.06