


工程名称	平潭县污水处理厂提标扩容技术改造工程
建设单位	福建大成环保有限公司
设计单位	中国市政工程中南设计研究总院有限公司
设计阶段	初步设计
设计日期	2017.10

主要技术经济指标

项 目	指 标
总征地面积	16700m ²
围墙内用地面积	16249m ²
总建筑面积	2008.1m ²
建筑物占地面积	1107.8m ²
构筑物占地面积	5933.6m ²
绿地总面积	4849m ²
道路用地面积	4358.6m ²
容积率	0.12
建筑密度	6.82%
建筑系数	43.3%
绿地率	29.85%

图 例：

- (101) 现状一期建(构)筑物
(201) 现状二期建(构)筑物
(301) 本次新建建(构)筑物
— 现状污水处理厂围墙线
— 厂区现状道路
— 厂区新建道路

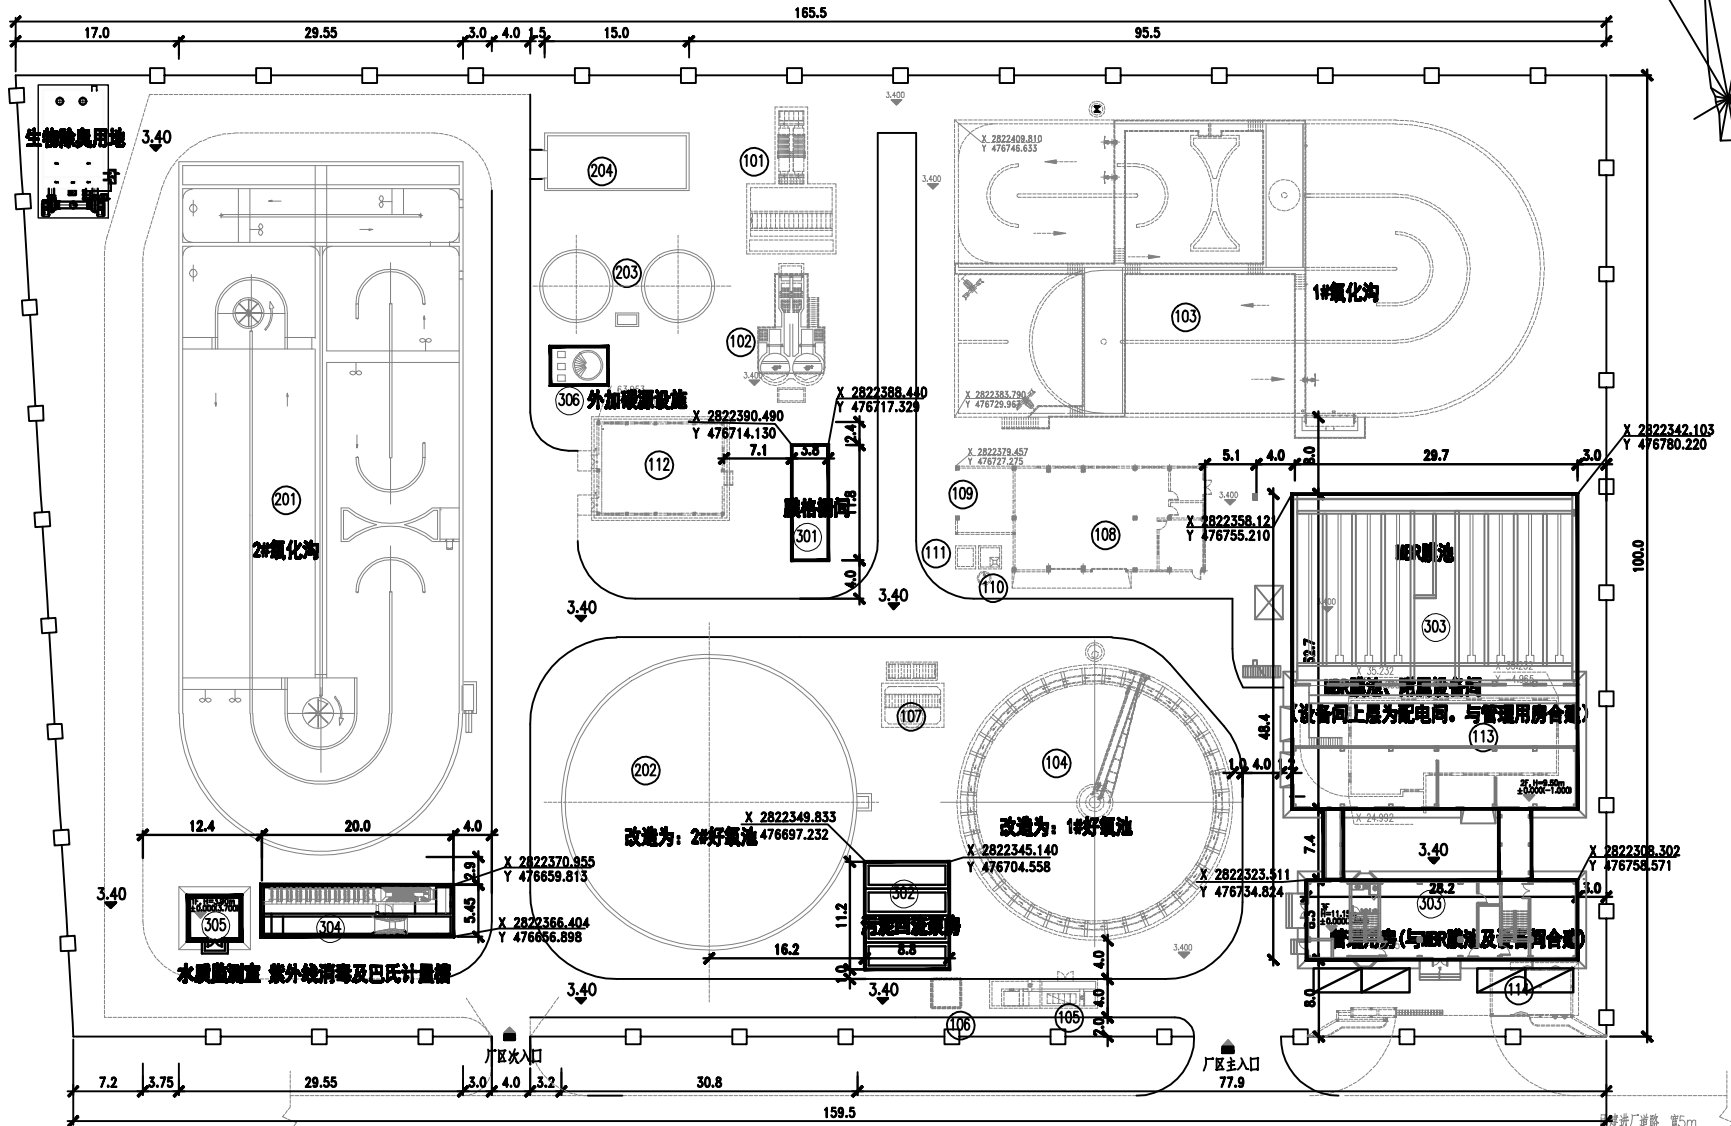

厂区平面布置图 1:500

现状一期建(构)筑物改造及利用情况一览表

编号	名 称	规 格 (m)	单 位	数 量	本工程改造及利用情况
(101)	粗格栅及进水泵房	LxB=15.3x9.3	座	1	设备及管道改造, 改造后规模4.0万m ³ /d
(102)	细格栅及旋流沉砂池	LxB=12.7x7.0	座	1	设备及管道改造, 改造后规模4.0万m ³ /d
(103)	1#氧化沟	LxB=61.35x30.9	座	1	改造后MBR首端氧化沟系统, 改造后规模2.0万m ³ /d
(104)	二沉池	D=28.8	座	1	改造后MBR首端1#好氧池, 改造后规模2.0万m ³ /d
(105)	紫外消毒池	LxB=11.25x3.05	座	1	新建水质监测室、紫外消毒及巴氏计量槽改造后
(106)	尾水检测井	LxB=3.00x3.00	座	1	拆除, 地块用新建道路
(107)	污泥泵井	LxB=4.65x6.55	座	1	拆除
(108)	污泥浓缩、脱水车间	LxB=20.0x11.0	座	1	设备及管道改造, 改造后规模4.0万m ³ /d
(109)	污泥堆棚	LxB=7.1x6.2	座	1	本工程继续使用
(110)	储泥池	LxB=2.4x2.4	座	1	本工程停用
(111)	反冲洗水池	LxB=2.1x2.4	座	1	本工程继续使用
(112)	变 配 电 间	LxB=13.2x9.7	座	1	本工程继续使用
(113)	办 公 楼	F=666.7m ²	座	1	本工程拆除, 地块用新建MBR膜池及管理用房
(114)	传 达 室	F=33m ²	座	1	本工程拆除

现状二期建(构)筑物改造及利用情况一览表

编号	名 称	规 格	单 位	数 量	本工程改造及利用情况
(201)	2#氧化沟	LxB=72.125m29.55m	座	1	改造后MBR首端氧化沟系统, 改造后规模2.0万m ³ /d
(202)	二沉池	D _中 =30m	座	1	改造后MBR首端2#好氧池, 改造后规模2.0万m ³ /d
(203)	液氧池	D _中 =7.0m	座	2	本工程继续使用
(204)	加药间	LxB=15.0m6.0m	座	1	设备改造, 改造后规模4.0万m ³ /d

说 明：

本图根据建设方提供的污水处理厂红线图。

图中尺寸、标高单位为米, 西安坐标系, 平潭地方高程系。厂区设计地面高程。

平潭污水处理厂现状(一期)规模为万, 现状(二期)规模为万。原设计污水处理厂出水

水质执行《城镇污水处理厂污染物排放标准》()一级标准。根据国家环保相关要求,

本污水处理厂出水水质标准应执行一级排放标准, 需进行提标改造。同时, 根据实际情况, 为满足日益增长的

进厂污水量需求, 需要进行扩容, 扩容规模为万。提标、扩容工程完成后, 本污水处理厂总规模万。

污水厂提标及扩容技术改造工程在现有厂区围墙内建设, 不须另行征地。污水厂一期征地围墙内占地面积。

本工程污水处理拟采用(氧化沟)膜处理工艺, 污泥处理拟采用带式浓缩脱水一体机工艺。

本图中建(构)筑物的标注尺寸均为建(构)筑物外包尺寸。

厂区内主要车行道宽度转弯半径为。

其他未尽事宜详初步设计说明书。

本工程主要新增建(构)筑物及工程量一览表

编号	名 称	规 格	结构形式	单 位	数 量	备注
(301)	膜格栅间	LxB=11.8mx3.8m	钢筋砼	座	1	规模4.0万m ³ /d
(302)	污泥回流泵房	LxB=11.2mx8.8m	钢筋砼	座	1	规模4.0万m ³ /d
(303)	MBR膜池、设备间及管理用房	LxB=48.4mx29.7m, 其中 膜池设备间S=539.4m ² (2F); 管理用房S=702m ² (3F)	组合	座	1	规模4.0万m ³ /d。设备间含产水设备间、鼓风机房、 配电间。火灾危险性属丙类。
(304)	紫外线消毒及巴氏计量槽	LxB=20.0mx5.45m	钢筋砼	座	1	规模4.0万m ³ /d
(305)	水质监测室	S=26.7m ² 1F	框架	座	1	火灾危险性属戊类
(306)	外加碳源设施	LxB=4.0mx6.0m	钢结构	座	1	规模4.0万m ³ /d
	厂区土方开挖			万m ³	0.7	
	厂区新建道路	B=4.0~2.0m	混凝土	m ²	2300	含道路硬化后修复面积
	厂区管线			项	1	
	厂区现状管线拆除			项	1	
	厂区绿化			项	1	
	厂区现状工程防护			项	1	
	地基处理			项	1	
	生物除臭			项	1	

中国市政工程中南设计研究总院有限公司
CENTRAL AND SOUTHERN CHINA MUNICIPAL
ENGINEERING DESIGN & RESEARCH INSTITUTE

工程设计综合资质甲级A142001257
工程咨询甲级12120070023

图纸专用章：

注册执业章：

施工图审查单位：

施工图审查合格书编号：

工程名称：

平潭县污水处理厂提标扩容技术改造工程

子 项：

建设单位：

福建大成环保有限公司

审 定

张卫东

张卫东

设计负责人

周林凡 林文辉

周林凡

专业负责人

李 涛

李涛

审 核

赵红兵

赵红兵

校 对

周林凡

周林凡

设 计

林文辉

林文辉

制 图

林文辉

林文辉

图名：

原厂区规划建设总平面布置图

工程编号

排11-201709

图 别

建筑方案

图 号

方-建201

日 期

2017. 10