

备注:
本图版权属本公司所有。若需复制或用于
本工程以外的其他用途,须获得本公司书面许
可,若发生侵权行为,将追究法律责任。
本设计图纸未经规划部门同意和审图机构认可
不得用于现场施工,仅供业主建设投资前估算建
设造价之参考图。

施工图审查批准单位:

施工图审查批准书证号:

图纸专用章:
本图加盖原始图纸专用章方有效。
图纸专用章晒制或复印无效。

注册建筑师执业章:

注册结构师执业章:

工程名称:
康德世家三期29号楼1梯电梯加装

建设单位: 康德世家三期29号楼1梯


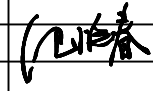
审 定		
工程负责人	纪晓春	
专业负责人	纪晓春	
审 核	纪晓春	
校 对	黄红萍	
设 计	连全超	
制 图	连全超	

图 名:
加装电梯总平面图


工程编号	18176	
图 别	方案	
图 号	01	
日 期	2018.11	

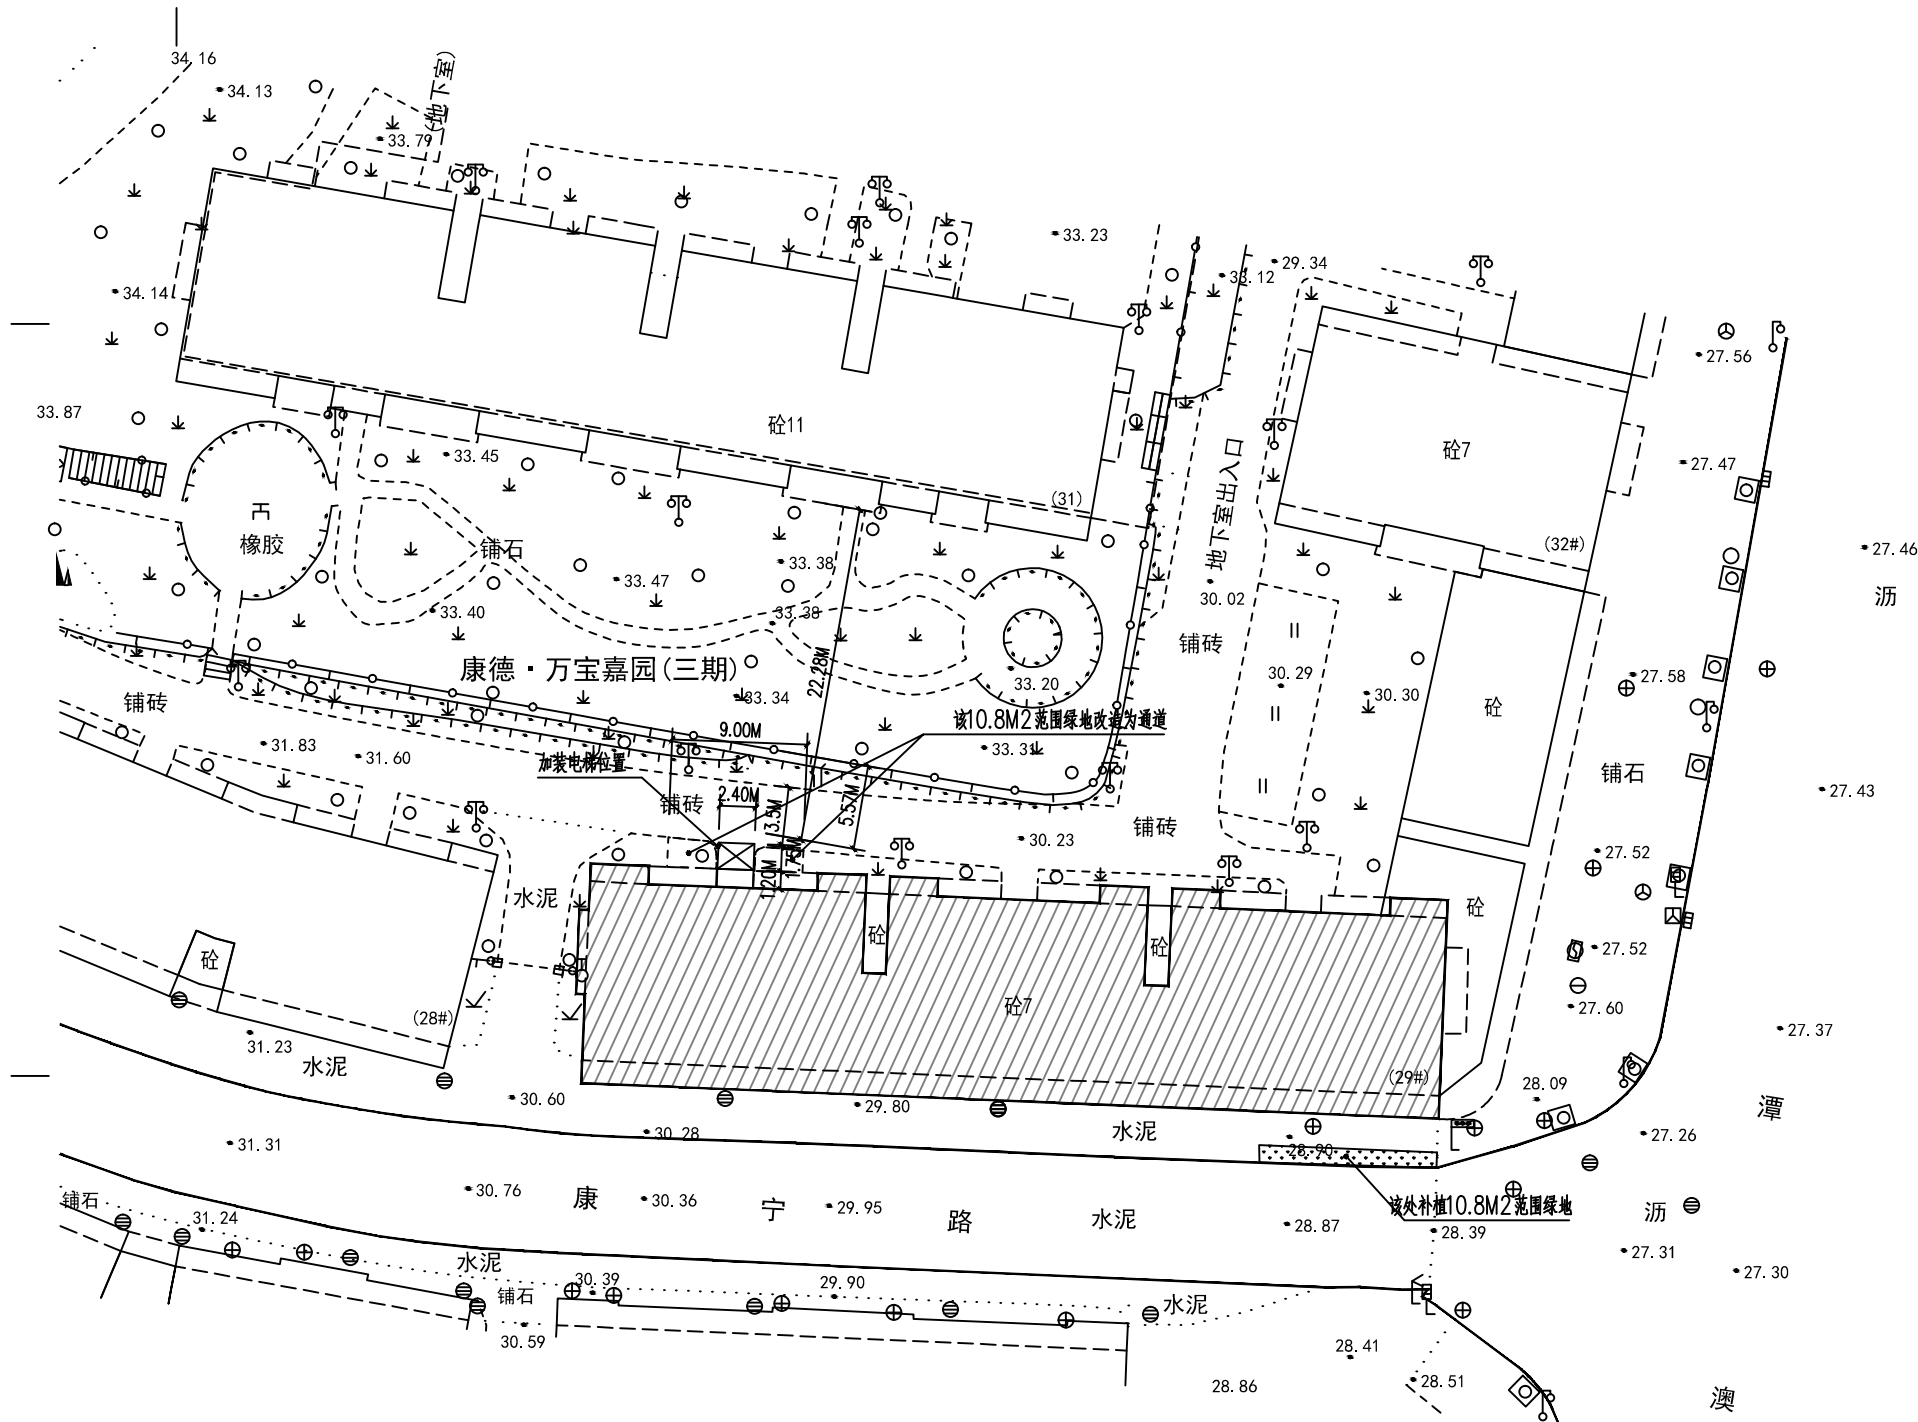

加装电梯部分技术经济指标

序号	项目	合计
1	加装电梯占地面积 (m²)	7.08
2	加装电梯增加面积 (m²)	49.56

总平面图 1:500

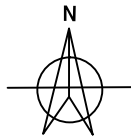

退距计算方法: 本栋建筑高度19.40m。本栋楼一层及北侧建筑一层均为杂物间。
计算退距有效建筑高度为: 16.80m
加装电梯建筑最小退距: 16.80×0.6=10.08m
本方案建筑最小建筑退距为22.28m, 满足建筑退距要求。