


总平面图

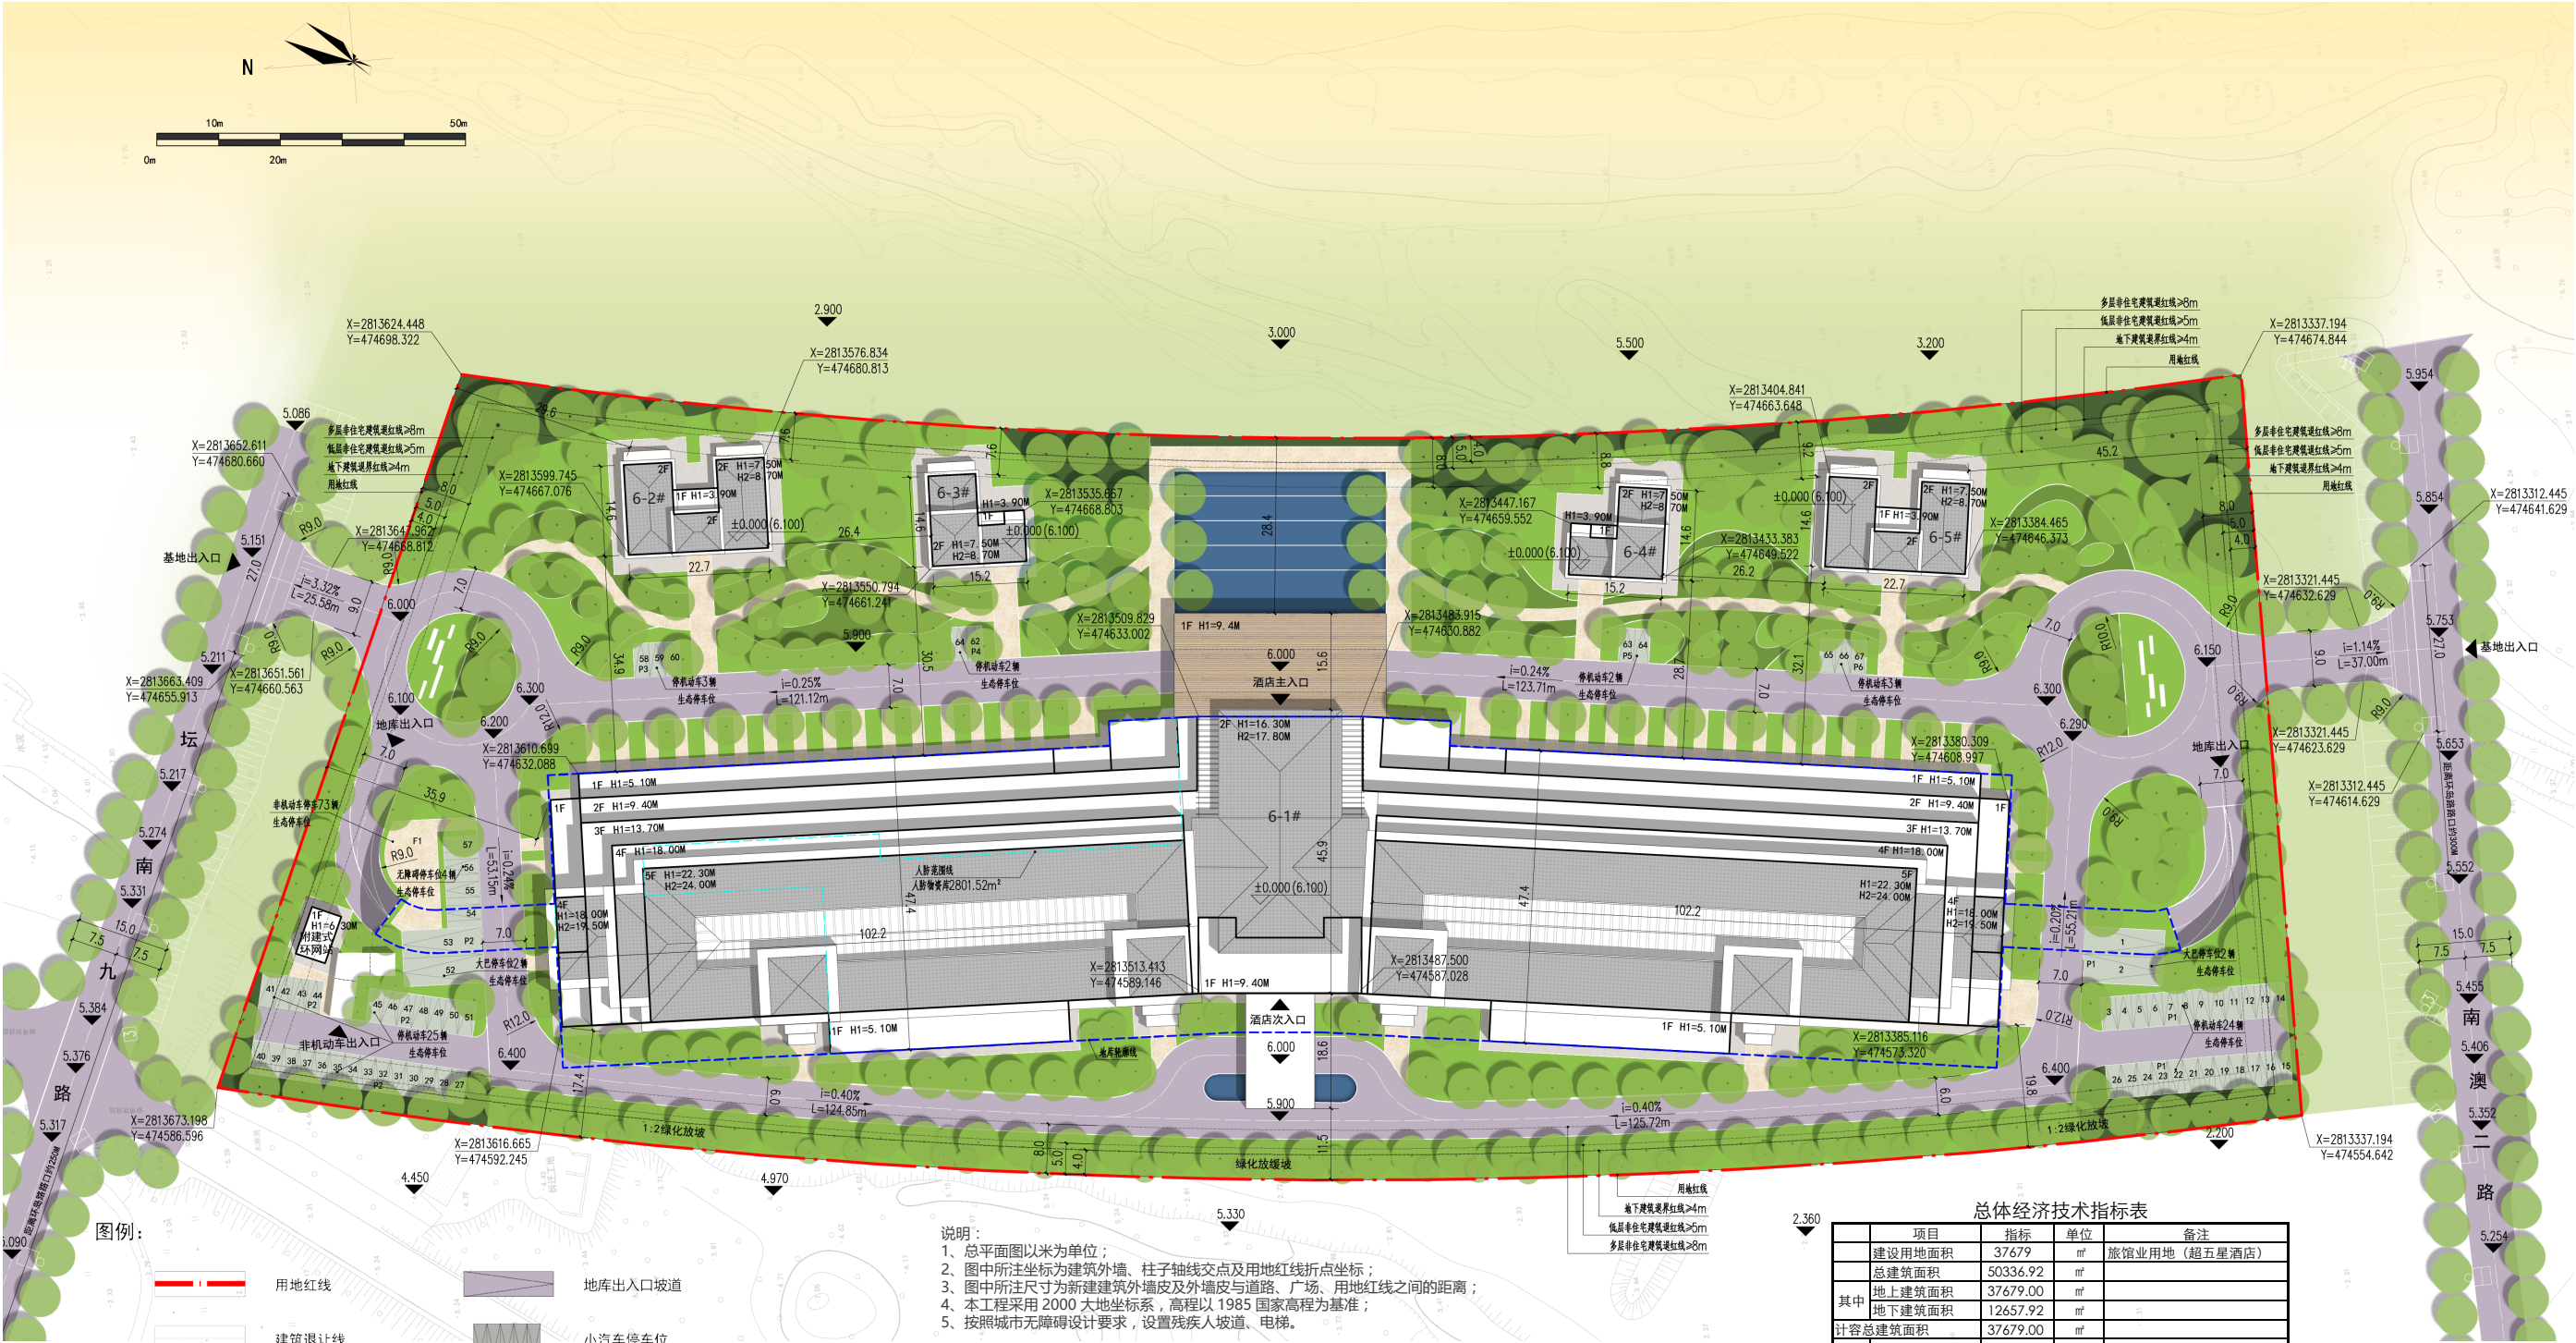

图例：

- 用地红线
- 建筑退让线
- 车行道路线
- 人防范围线
- 地下室范围线
- 车行道中心线
- 地库出入口坡道
- 小汽车停车位
- 大巴停车位
- 场地绝对标高
- 室内地坪相对标高（绝对标高）
- H1 建筑室外设计地面至其屋面结构板高度
- H2 建筑室外设计地面至其檐口顶+檐口挑出宽度

环网站说明：
2路独立10KV排管埋地从室外进入西北侧环网站的高压进线柜，环网站内设2组高压柜（2组分别包括高压进线柜、计量柜、PT保护柜，高压出线柜），2组高压柜分别对应2段10KV高压母线段，2段母线段中间设高压联络开关，高压出线柜出线后给本工程一层变配电房变压器供电。

- 说明：
- 1、总平面图以米为单位；
 - 2、图中所注坐标为建筑外墙、柱子轴线交点及用地红线折点坐标；
 - 3、图中所注尺寸为新建筑外墙皮及外墙皮与道路、广场、用地红线之间的距离；
 - 4、本工程采用2000大地坐标系，高程以1985国家高程为基准；
 - 5、按照城市无障碍设计要求，设置残疾人坡道、电梯。

人防面积计算：
依据《美丽之冠一期人防分布图》2015G009-3地块人防总建筑面积要求为2637.53㎡；
本案设计人防面积：2801.52㎡，满足相关要求（具体以人防部门批示为准）。

车位计算公式：
机动车停车位=251(五星级酒店客房数)*0.7+9874.29(酒店配套餐饮、娱乐等功能)*1.2/100+639.36(办公)*0.8/100+645.35(商业)*0.6/100=303辆；
地面停车位P1:26辆；P2:31辆（其中无障碍车位4辆）；P3:3辆；P4:2辆；P5:2辆；P6:3辆；地下停车位：253辆；
设计车位=P1+P2+P3+P4+P5+P6+地下停车位=320辆，满足规范要求；

备注：该项目初期需要配置的充电桩：320辆X20%=64辆（地下车库配置）
充电桩（快充）：64X10%=7辆；
充电桩（慢充）：64-7=57辆
依据：福建省电动汽车充电基础设施建设技术规程
无障碍机动车停车位配置：320X1%=4个
依据：GB50763-2012无障碍设计规范

非机动车停车位=251(五星级酒店客房数)*0.4+9874.29(酒店配套餐饮、娱乐等功能)*4/100+639.36(办公)*4/100+645.35(商业)*8/100=573辆；
设计车位数573辆，地面F1:73辆，地下500辆，满足规范要求。

- 注：
- 1、机动车停车位按照五星级酒店每个客房0.7个，餐饮、娱乐、酒店大堂每100平方米1.2个；办公每100平方米0.8个；商业每100平方米0.6个；
 - 2、非机动车停车位按照五星级酒店每个客房0.4个，餐饮、娱乐、酒店大堂每100平方米4个；办公每100平方米4个；商业每100平方米8个；

总体经济技术指标表

	项目	指标	单位	备注
	建设用地面积	37679	㎡	旅馆业用地（超五星酒店）
	总建筑面积	50336.92	㎡	
其中	地上建筑面积	37679.00	㎡	
	地下建筑面积	12657.92	㎡	
计容总建筑面积	总建筑面积	37679.00	㎡	
其中	旅馆建筑面积	26480.00	㎡	≥25590㎡
	酒店配套	11159.00	㎡	≤12045㎡
其中	酒店大堂	2960.03	㎡	
	餐饮	6914.26	㎡	
	配套办公	639.36	㎡	
	配套精品店	645.35	㎡	
	附建式环网站	40.00	㎡	
地下不计容面积	设备用房	1997.20	㎡	
其中	机动车库	9744.72	㎡	
	非机动车库	916.00	㎡	
机动车位		320	个	
其中	地上停车位	67	个	
	地下停车位	253	个	
非机动车位		573	个	
其中	地上停车位	73	个	
	地下停车位	500	个	
绿地面积		11341.38	㎡	
绿地率		30.10	%	≥30%
建筑占地面积		14996.24	㎡	
建筑密度		39.80%	%	≤40%
容积率		1.00		FAR≤1.0
客房数		251	间	地上总建面平均150㎡/间

注：地下室人防建筑面积2801.52㎡