



平潭县建筑勘察设计院
PINGTIAN ARCHITECTURAL DESIGN INSTITUTE

设计证书编号: 135034-sb
ARCHITECTURAL DESIGN LICENSE No. 135034-sb

备注

图章专用章



注册建筑师执业章

中华人民共和国二级注册建筑师
姓名: 陈明建
注册号: 3500561-0001
有效期至: 2018年6月

施工图审查批准单位

施工图审查批准书证号

工程名称

陈平个人住宅


建设单位	
审定	
工程负责人	
专业负责人	
审核	
校对	
设计	
制图	

图名

一层平面图
二层平面图

工程编号 MF170302

图别 建筑

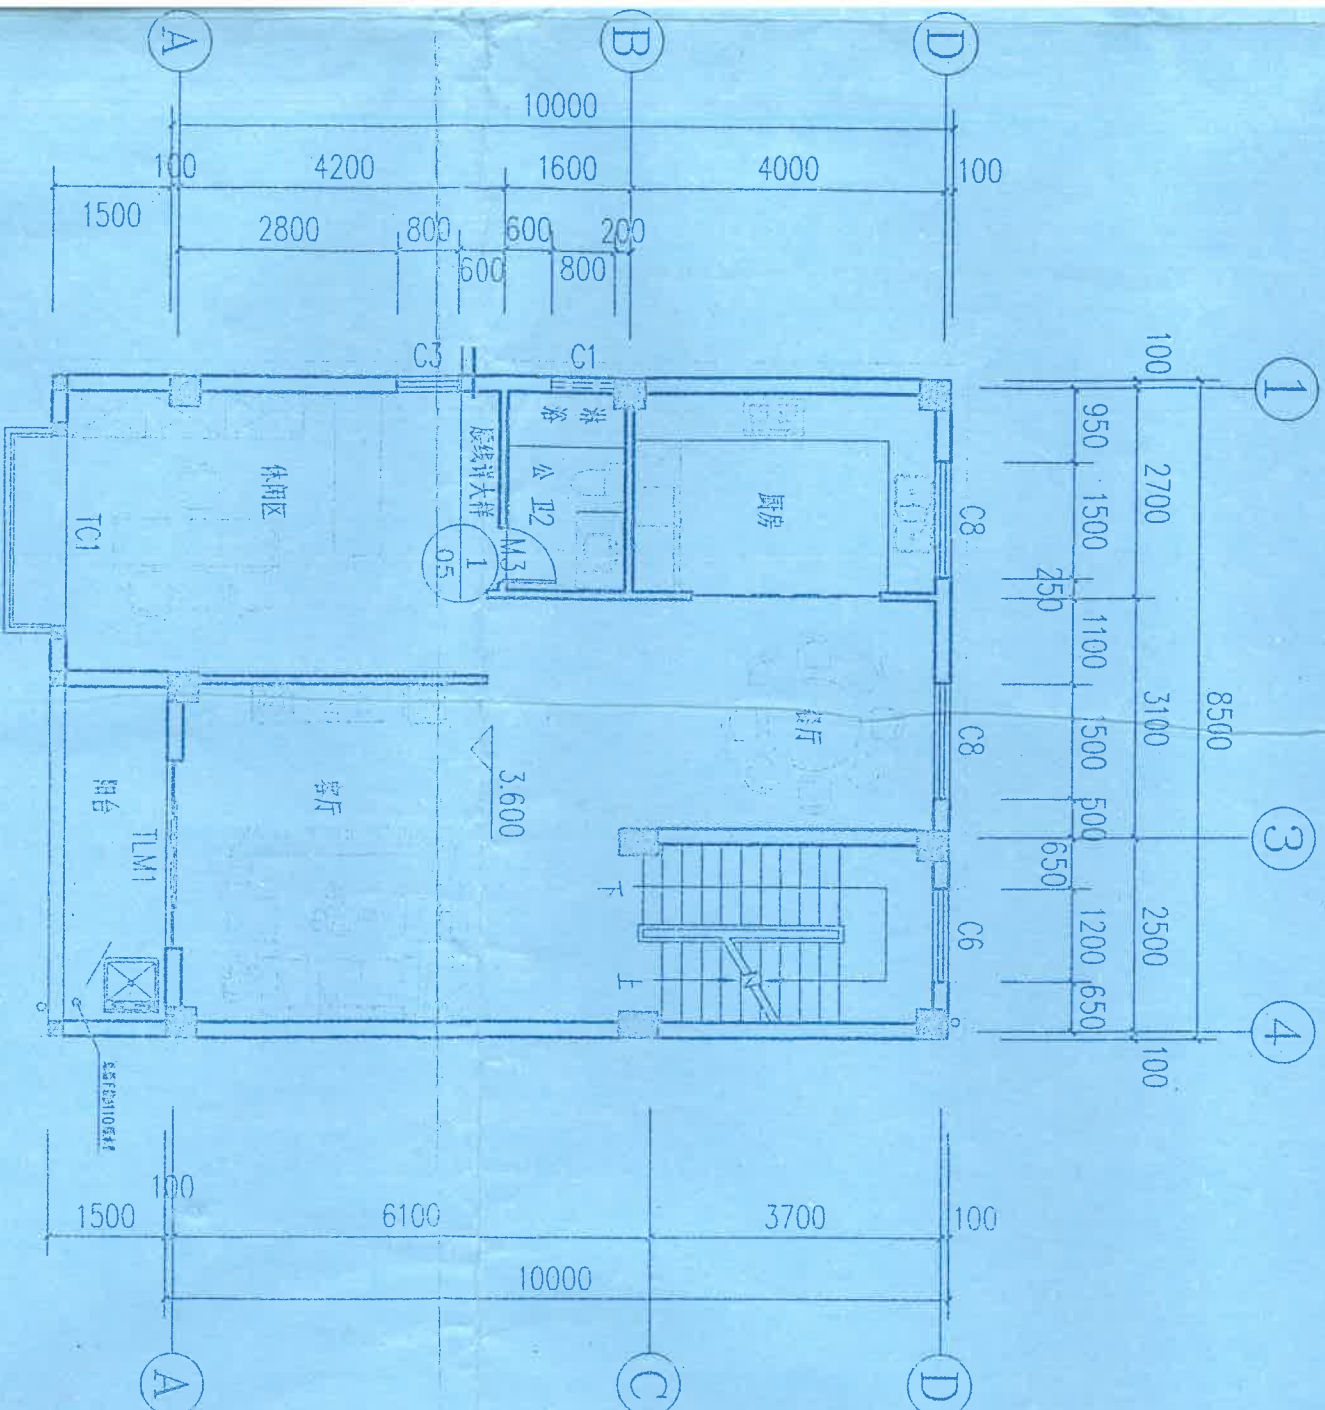

二层平面图 1:100

- 注: 1. 本层建筑面积: 94.38m², 计容面积为85m².
2. 未注明墙厚均为100, 靠柱开门时靠柱边.
3. 本图局部留洞均不含砖模数处请用C15素混凝土.
4. 厨房门由业主自理.
5. 地面高差15mm均做斜面过渡.
6. 图中卫生间与厨房地面标高同比楼面标高降低50mm, 且均做1.0%坡度找向地漏或出水口.
7. ○表示φ110雨水管, ⊙表示φ90地漏, 本层共2根雨水管.

