


主要经济技术指标				
序号	项目	数量	单位	备注
1	建筑用地面积	26667	m²	
2	建筑占地面积	14123.74	m²	
3	总建筑面积	53322.14	m²	
	地上建筑面积	46248.33	m²	
	其中 生产用房地上建筑面积	35588.06	m²	
	行政办公及生活服务设施用地地上建筑面积	10660.27	m²	
	地下建筑面积	7073.81	m²	
其中	地下基坑建筑面积	5338.36	m²	
	地下停车位、人防、设备用房建筑面积	1735.45	m²	其中人防面积820m²、泵房80m²
4	计容建筑面积	53331.52	m²	
6	生产用房计容面积	42671.25	m²	环网站，套内面积55m²
	其中 1#厂房计容面积	42659.25	m²	
	门卫计容面积	12.00	m²	
	2#楼行政办公及生活服务设施用房计容面积	10660.27	m²	
7	不计容建筑面积	7073.81	m²	
	其中 地下基坑建筑面积	5338.36	m²	
其中	地下停车位、人防、设备用房建筑面积	1735.45	m²	
	容积率	1.9999		不小于0.9，且不大于2.0
9	建筑密度	52.96%		
10	建筑系数	53.02%		不小于40%
11	构筑物占地面积	16.00	m²	
	其中 成品质地式一体化生化处理池	6.00	m²	
	成品质地式化粪池	10.00	m²	
12	绿地面积	2669.37	m²	
13	绿地率	10.01%		不小于10%，且不大于20%
14	机动车停车位	88	辆	地上88辆，地下0辆，共88辆
15	其中 地面机动车停车位	64	辆	
	地下机动车停车位	24	辆	
16	地面非机动车停车位	445	辆	
17	行政办公及生活服务设施用地面积	1735.45	m²	
18	行政办公及生活服务设施用地面积与总用地面积比例	6.5%		不超过7%
19	行政办公及生活服务设施用房建筑面积与总建筑面积比例	19.99%		小于20%

车位配套表				
项目	数值	单位	机动车配建标准	非机动车配建标准
行政办公及生活服务设施用房	10660.27	m²	0.8车位/100m²	4车位/100m²
			85.28	426.41

- 备注：1. H1表示室外地面至屋面楼板。
2. H2表示室外地面至屋面女儿墙高度。
3. 女儿墙上人按照1.5m计算，不上人按0.5m计算。
4. 图中尺寸单位皆为米。与建筑有关尺寸均标注至建筑外墙。
5. 1#楼建筑室内内外高差均为0.30m；2#楼建筑室内内外高差均为0.60m。
6. 本项目按照《福建省城市规划管理技术规定》（2017年）等规定执行。
7. 本图标高采用2000国家大地坐标系，1985国家高程基准。
8. 生产车间为单层建筑，建筑高度超过8m，按规定不加计算容积率该层建筑面积加倍计算，计算建筑面积不加倍计算。
9. 厂区道路的转弯半径除标注为12米其余均为9米。
10. (行政办公及生活服务设施用地面积)/(总用地面积)=1735.45/26667=6.5%
11. 建筑系数=(建筑占地面积+构筑物占地面积-堆场用地面积)/总用地面积=(14123.74+16+0)/26667=53.02%
12. 需建人防面积：行政办公及生活服务设施用房计容建筑面积 10660.27*7%=746.22。满足要求。最终需建人防面积以人防部门批复为准。
13. 地面小型汽车车位2辆，折算系数1.0，折算为标准车位2*1=2辆。
地面大型汽车车位25辆，折算系数2.5，折算为标准车位25*2.5=62辆。
14. 根据《福建省电动汽车充电基础设施建设技术规程》DBJ 13-278-2017要求，充电桩按机动车数量的20%考虑。
标准车位88辆，充电车位88*20%=18辆，其中快充2辆，慢充16辆。
15. 行政办公及生活服务设施用房建筑面积与总建筑面积比例=10660.27/53331.52=19.99%
16. 根据《福建省电动汽车充电基础设施建设技术规程》DBJ 13-278-2017要求，充电桩按机动车数量的20%考虑。
标准车位88辆，充电车位88*20%=18辆，其中快充2辆，慢充16辆。

分栋面积表				
项目	占地 (m²)	层数	计容总面积 (m²)	地上总建筑面积 (m²)
生产用房面积	12498.18	4F	42671.25	35588.06
1#厂房	12498.18	4F	42659.25	35576.06
门卫值班室	12	1F	12	12
2#办公	1635.56	9F	10660.27	10660.27
总计	14123.74		53331.52	46248.33

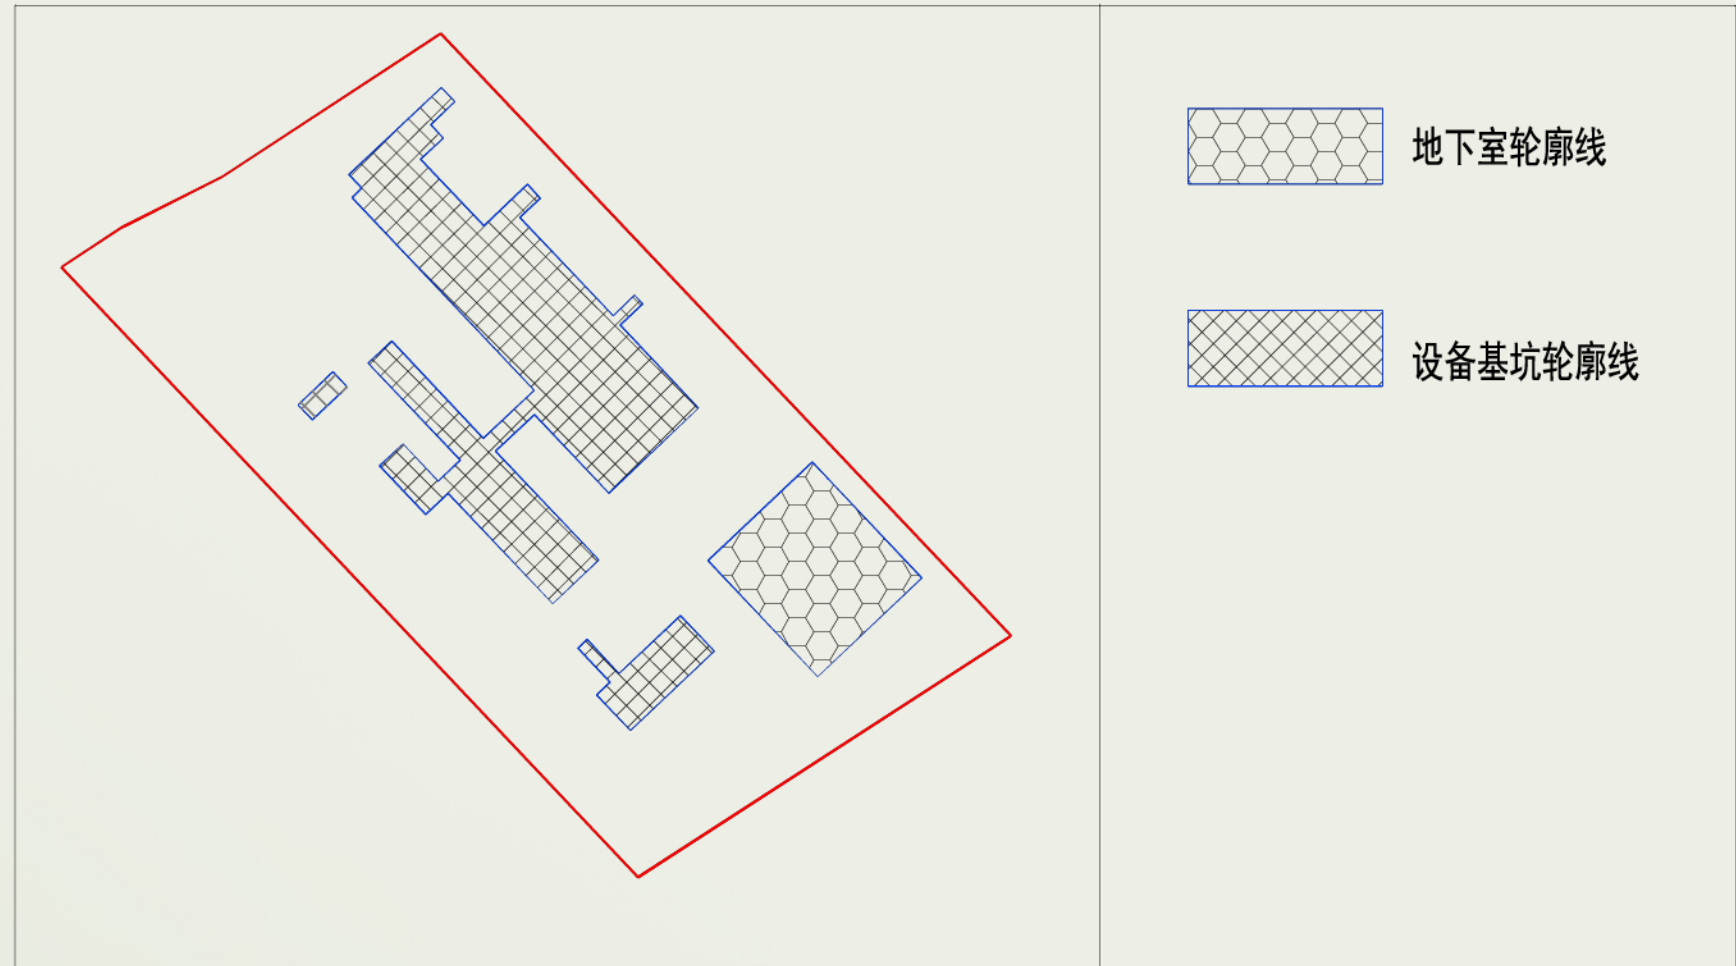

- 图例
- 规划建筑
 - 用地界线
 - 道路
 - 道路转弯半径
 - 18
 - 地面机动车停车
 - 地下室轮廓线
 - 规划出入口
 - 地下室轮廓线
 - 室内地坪标高
 - 室外地坪标高
 - 民用垃圾收集点
 - 工业垃圾收集点
 - 设备基坑轮廓线
 - 围墙
 - 坐标定位点

总平面图 1:500