


综合技术经济指标一览表				
序号	项目	单位	数值	备注
01	规划用地面积	m²	9145	按土地出让合同
02	总建筑面积	m²	20985.41	
	其中 地上建筑面积	m²	15255.72	
其中	地下建筑面积	m²	5729.69	
	计容建筑面积	m²	15247.58	9145m²≤S≤15250m²
03	01、住宅建筑面积	m²	3749.13	住宅面积不大于3750m²
	02、零售商业面积	m²	11034.84	S≤11455m²
其中	普通商业	m²	6985	
	农贸市场	m²	4049.82	S≥4045且设置一层，含一层配套中的报警阀间、雨淋阀间、发电机房、商业配电房、消防室
03	03、其他配套设施面积	m²	463.61	
	物业管理用房	m²	88.78	总建筑面积的千分之四
其中	电子商务代收服务网点	m²	81.96	S≥80m²且设置一层
	环境站	m²	82.43	“原环网箱80m²含附建式环网箱45m²”
其中	变电用房	m²	127.74	住宅变配电120m²、
	公共配电房	m²	58.52	
04	电视机房	m²	24.18	
	非计容建筑面积	m²	5737.83	
其中	地下室建筑面积	m²	5729.69	
	其中 人防地下室面积	m²	1070.00	计容面积的7%设计即15250*7%=1068m²
其中	非人防地下室面积	m²	4659.69	
	通往地下室的楼梯、竖井建筑面积	m²	8.14	
05	住宅户数	户	39	
06	总人数	个	137	按每户3.5人统计
07	容积率		1.607	1<FAR≤1.67
08	建筑占地面积	m²	4536.70	
09	建筑密度	%	49.609%	≤50%
10	绿地面积	m²	1380	
11	绿地率	%	15.09%	≥15%
12	建筑高度	m	24.5	H≤30米
13	机动车停车位	辆	137	
	其中 地面停车位	辆	9	按商业车位的10%停
其中	地下室停车位	辆	128	含住宅公共停车位10%即42*10%=5辆，配置6辆，且无产权
	非机动车停车位	辆	716	
14	其中 地面停车位	辆	228	
	地下室停车位	辆	488	
地块停车设施配置指标表				
建筑类型		套数	面积/人数	计算单位
				指标
				应配建车位数(辆)
				实际配建车位数(辆)
				指标
				应配建车位数(辆)
				实际配建车位数(辆)
住宅	每户建筑面积40~90m²	16		个/户
			0.8	12.80
住宅	每户建筑面积90~150m²	23		个/户
			1.2	27.60
商业	商业	6985.02	个/100m²建筑面积	0.6
				41.91
商业	农贸市场	4049.82	个/100m²建筑面积	1.2
				48.60
配套设施	配套设施	464	个/100m²建筑面积	0.8
				3.71
合计				134.02
				137.00
				713.34
				716.00
地块停车设施充电桩指标表				
建筑类型		配建车位数	配建要求	配建充电桩数量
				快充要求
				配建快充充电桩数量
住宅		42		9
配套		4	20%	1
商业		91		19
合计		137		29

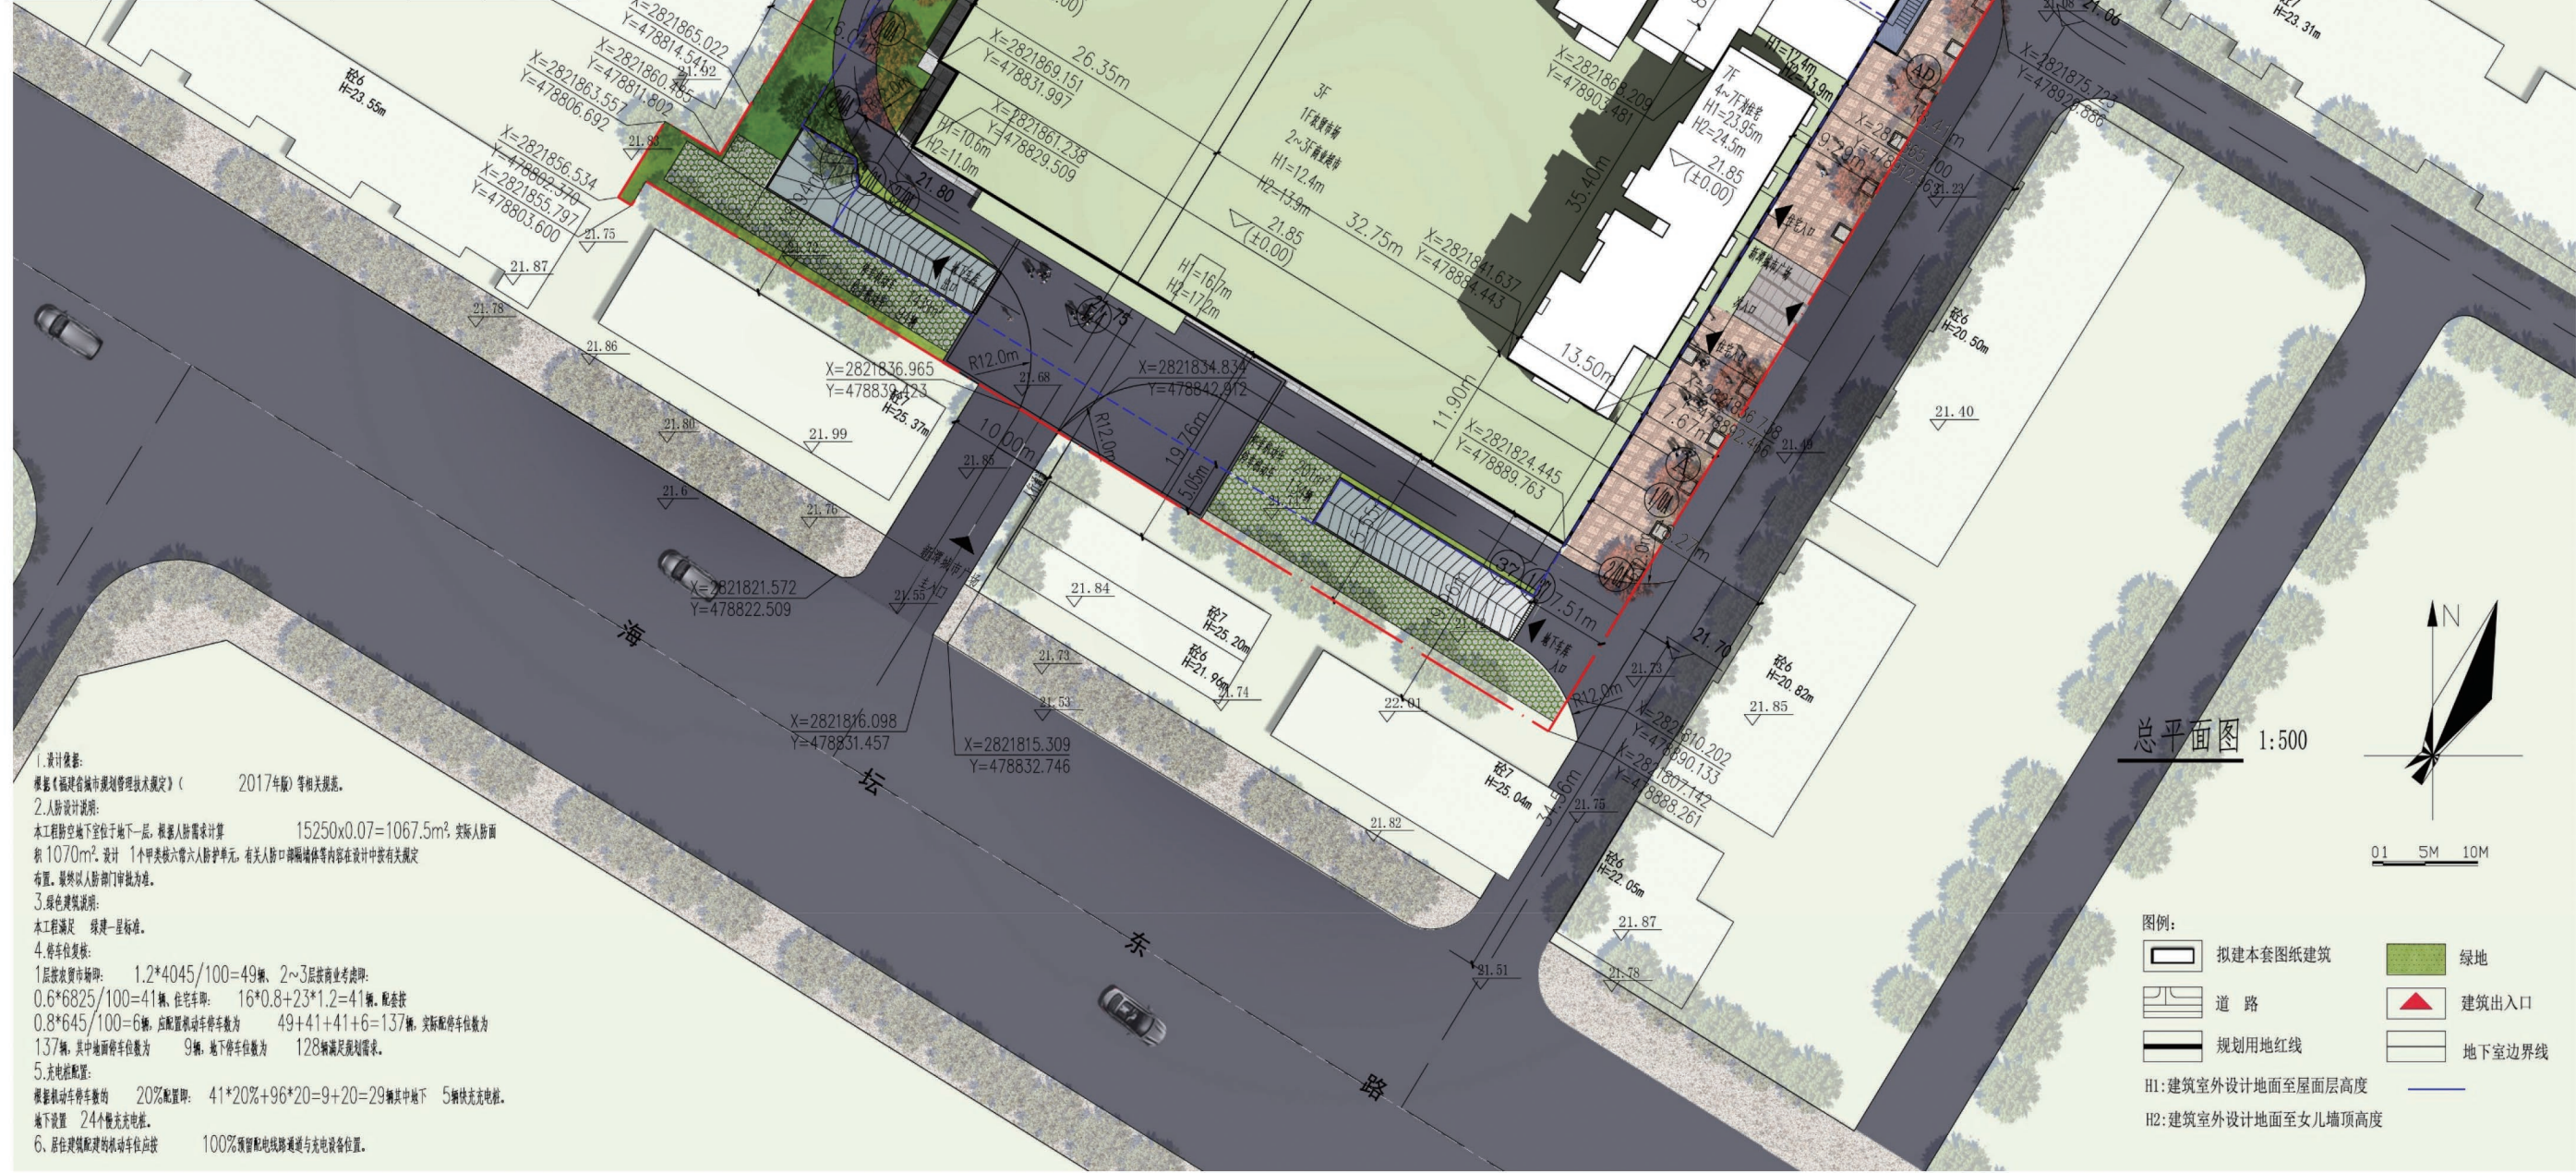

	地块方向	商业多层退红线最小距离(m)	商业实际退距距离(m)	商业退距是否满足要求	多层住宅退红线最小距离(m)	多层住宅退红线实际距离(m)	住宅退距是否满足要求	与周边现有建筑最小间距要求(m)	与周边现有建筑实际距离(m)	拟建建筑与周边建筑退距要求
主要朝向	南	9	15.55		10	27.28		12	18.93	
	北	9	15.50		10	27.46		12	19.71	
次要朝向	东	7	12.85	满足要求	8	26.23	满足要求	12	18.28	满足要求
	西	7	7.67		8	9.30		12	14.29	