


主要技术经济指标		
项 目	指	标
总征地面积	16700m ²	
围墙内用地面积	16249m ²	
总建筑面积	2188.1m ²	
建筑物占地面积	1163.4m ²	
构筑物占地面积	6412.2m ²	
绿地总面积	4793.4m ²	
道路用地面积	3880m ²	
容积率	0.13	
建筑密度	7.2%	
建筑系数	46.6%	
绿地率	29.50%	

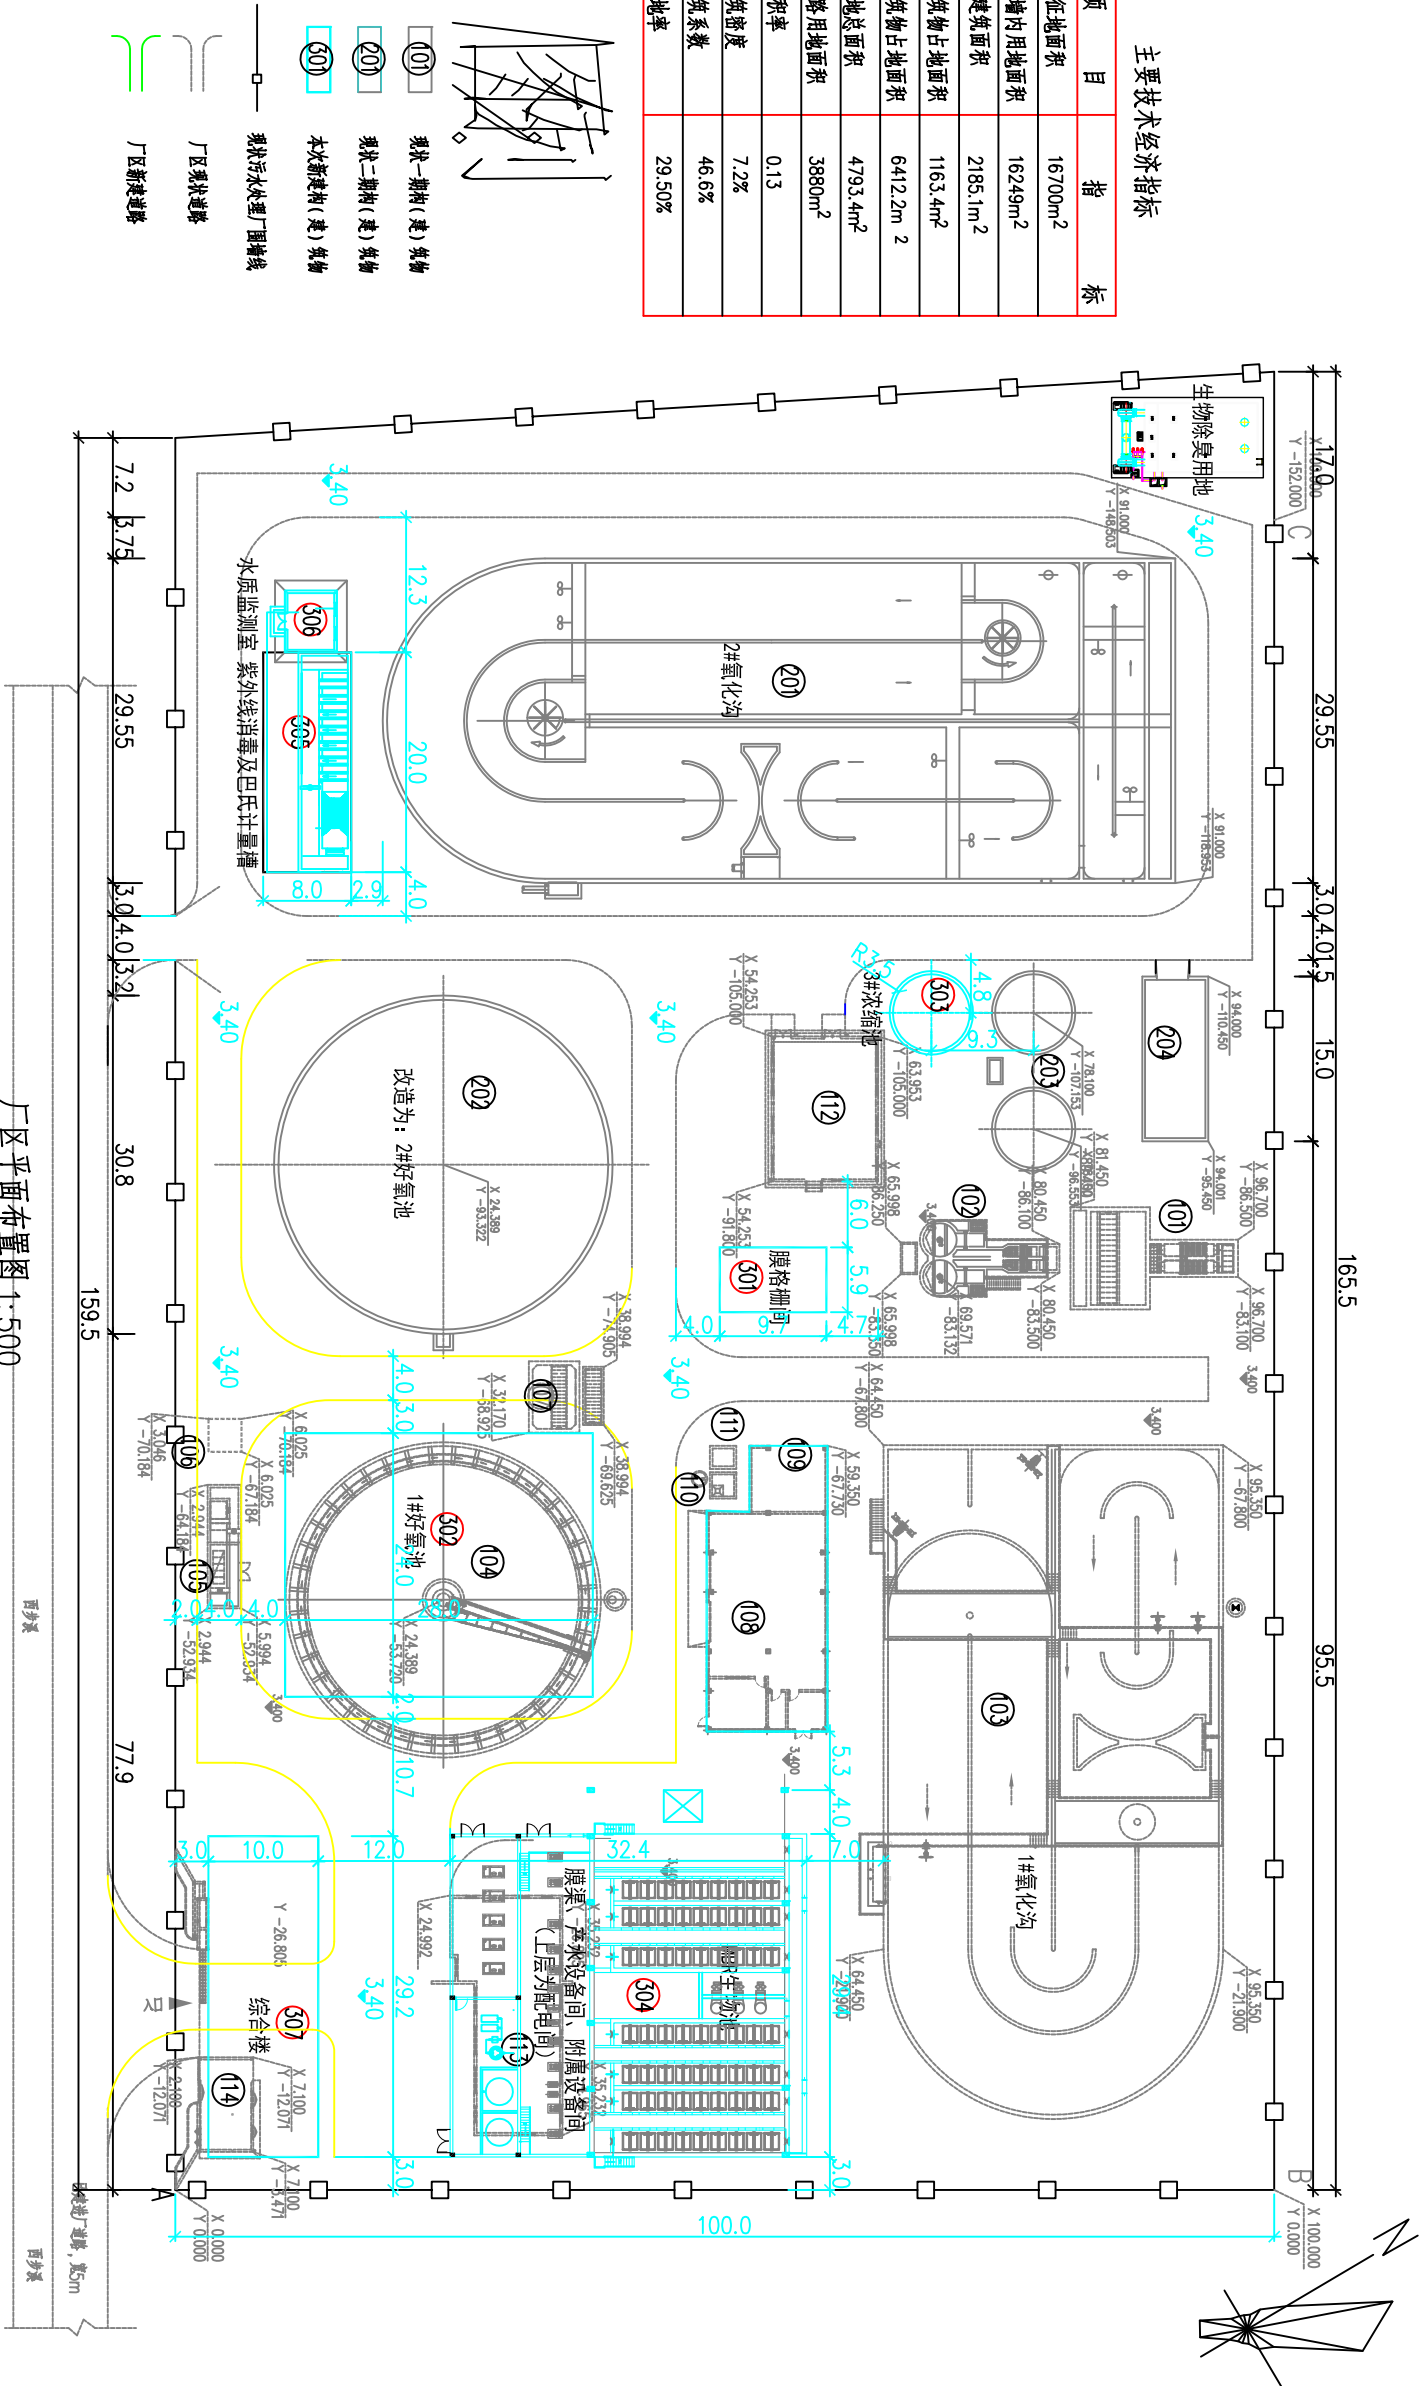

现状一期建(构)筑物改造及利用情况一览表

编号	名称	规格 (m)	单位	数量	本工程改造及利用情况
(001)	规格槽及进大泵房	LxB=15.3x9.3	座	1	设备及管道改造，改造后规格4.0m ³ /d
(002)	细格栅及旋流沉砂池	LxB=12.7x7.0	座	1	设备及管道改造，改造后规格4.0m ³ /d
(003)	1#气浮池	LxB=61.35x30.9	座	1	改造由BRP替代生化系统，改造后规格2.0m ³ /d
(004)	二流池	D=28.8	座	1	本工程拆除，地块用于新建BRP生物池及设备间
(005)	紫外消毒池	LxB=11.25x3.05	座	1	新建水泵监测室，紫外消毒及反冲洗量测池改造后
(006)	尾水检测井	LxB=3.00x3.00	座	1	拆除，地块用于新建1#排油池
(007)	污泥泵井	LxB=4.65x6.55	座	1	拆除，地块用于新建2#排油池
(008)	污泥浓缩、脱水车间	LxB=20.0x11.0	座	1	设备及管道改造，改造后规格4.0m ³ /d
(009)	污泥堆棚	LxB=7.1x6.2	座	1	本工程继续使用
(010)	储泥池	LxB=2.4x2.4	座	1	本工程使用
(011)	反冲洗水池	LxB=2.1x2.4	座	1	本工程继续使用
(012)	变配电间	LxB=13.2x9.7	座	1	本工程继续使用
(013)	办公楼	F=666.7m	座	1	本工程拆除，地块用于新建BRP生物池及设备间
(014)	传达室	F=33m	座	1	本工程拆除，地块用于新建设备间

现状二期建(构)筑物改造及利用情况一览表

编号	名称	规格	单位	数量	本工程改造及利用情况
(20)	2#生化池	L×B=72.125m×29.55m	座	1	改造为MBR膜生化处理系统,改造后曝气 $0.0\pi\text{m}^3/\text{d}$
(20)	二沉池	D=30m	座	1	改造为MBR膜池,改造后曝气 $0.0\pi\text{m}^3/\text{d}$
(20)	浓缩池	D=7.0m	座	2	本工程继续使用
(20)	加药间	L×B=15.0m×6.0m	座	1	设备改造,改造后曝气 $0.0\pi\text{m}^3/\text{d}$

说明:

1. 本图根据建设方提供的:500污水处理、红线图,采用假定坐标线绘制而成。
2. 图中尺寸、标高、坐标单位为米,高程系统采用黄海高程,厂区设计地面高程3.40m。
3. 平零污水收集管(一期)管径为 $0.75m^3/d$,管径(二期)管径为 $0.75m^3/d$,原设计污水处理厂出水水质执行《城镇污水处理厂污染物排放标准》(GB18918-2002)一级B标准,根据国家环保相关要求,本污水处理厂出水水质标准执行一级A排放标准,需进行提标改造。同时,根据实际情况,为满足日益增长的生活污水量需求,需要进行扩建,扩建规模按 $2.07m^3/d$ 、提标、扩建工程完成后,本污水处理厂总规模 $4.07m^3/d$ 。
4. 污水厂扩建及提标改造工程在现有厂区内围墙内建设,不须另行征地,污水厂一期征用 $67700m^2$ 围墙内占地面积 $6249m^2$ 。
5. 本工程污水处理采用 O_3/O_3 氧化沟+MBR膜处理工艺,污泥处理采用重力浓缩+机械脱水工艺。
6. 本图中建(构)筑物的标注尺寸均为建筑(物)基础外包尺寸。
7. 厂区内主要行车道宽度 $4m$,转弯半径为 $30m$ 。
8. 其他未尽事宜详行性研究报告说明书。

本工程主要新增建(构)筑物及工程量一览表

编号	名称	规格	结构形式	单位	数量	备注
501	渠格槽同	LxB=9.7m×5.9m	钢筋砼	座	1	灌溉4.0πm ³ /d
502	1号好氧池	LxB=28.0m×24.0m	钢筋砼	座	1	灌溉4.0πm ³ /d
503	3号厌氧池	D _内 =7.0m	钢筋砼	座	1	
504	MBR生物池、设备间及配间	LxB=32.5m×29.4m	组合	座	1	灌溉4.0πm ³ /d,设备间用于存放各种、灌溉设备,最大堆放量,上层为配电柜385m ²
505	紫外线消毒及巴氏计量槽	LxB=20.0m×8.0m	钢筋砼	座	1	灌溉4.0πm ³ /d
506	水质监测室	S=26.7m ²	框架	座	1	
507	综合楼	S=880m ²	框架	座	1	
	厂区土方开挖			万m ³	0.7	
	厂区新建道路	B=4.0~2.0m	混凝土	m ²	900	
	厂区管线			项	1	
	厂区硬化			项	1	
	厂区渠坎工程防护			项	1	
	地基处理			项	1	
	生物除臭			项	1	