


兴业路（中山大道-瑶竹北路）红线图

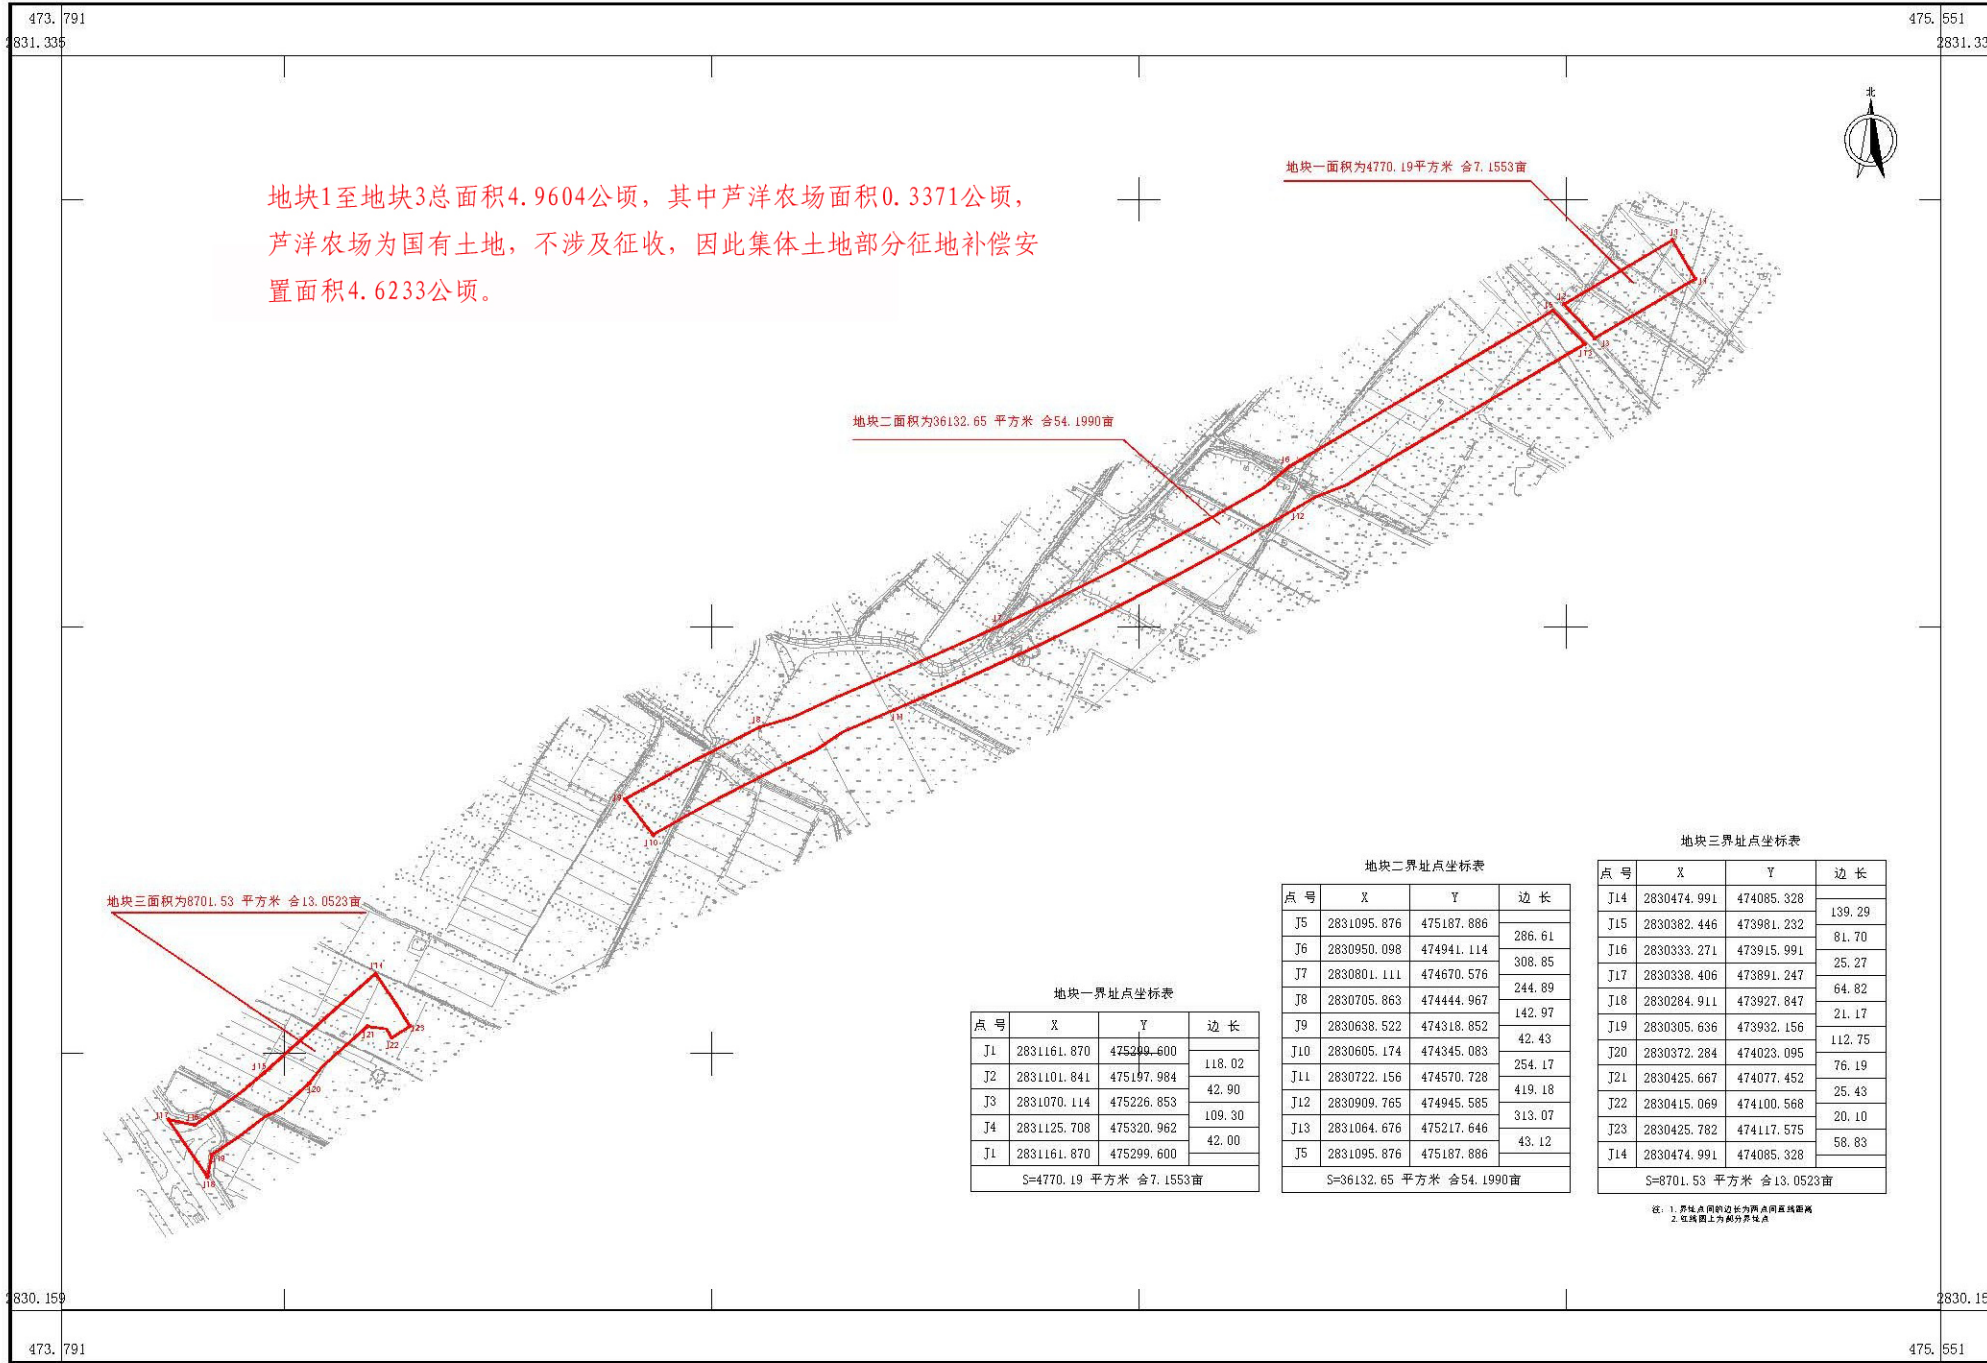

地块1至地块3总面积4.9604公顷，其中芦洋农场面积0.3371公顷，  
芦洋农场为国有土地，不涉及征收，因此集体土地部分征地补偿安  
置面积4.6233公顷。

地块一面积为4770.19平方米 合7.1553亩

地块二面积为36132.65 平方米 合54.1990亩

地块三面积为8701.53 平方米 合13.0523亩

地块一界址点坐标表

| 点号                     | X           | Y          | 边长     |
|------------------------|-------------|------------|--------|
| J1                     | 2831161.870 | 475299.600 | 118.02 |
| J2                     | 2831101.841 | 475197.984 | 42.90  |
| J3                     | 2831070.114 | 475226.853 | 109.30 |
| J4                     | 2831125.708 | 475320.962 | 42.00  |
| J1                     | 2831161.870 | 475299.600 |        |
| S=4770.19 平方米 合7.1553亩 |             |            |        |

地块二界址点坐标表

| 点号                       | X           | Y          | 边长     |
|--------------------------|-------------|------------|--------|
| J5                       | 2831095.876 | 475187.886 | 286.61 |
| J6                       | 2830950.098 | 474941.114 | 308.85 |
| J7                       | 2830801.111 | 474670.576 | 244.89 |
| J8                       | 2830705.863 | 474444.967 | 142.97 |
| J9                       | 2830638.522 | 474318.852 | 42.43  |
| J10                      | 2830605.174 | 474345.083 | 254.17 |
| J11                      | 2830722.156 | 474570.728 | 419.18 |
| J12                      | 2830909.765 | 474945.585 | 313.07 |
| J13                      | 2831064.676 | 475217.646 | 43.12  |
| J5                       | 2831095.876 | 475187.886 |        |
| S=36132.65 平方米 合54.1990亩 |             |            |        |

地块三界址点坐标表

| 点号                      | X           | Y          | 边长     |
|-------------------------|-------------|------------|--------|
| J14                     | 2830474.991 | 474085.328 | 139.29 |
| J15                     | 2830382.446 | 473981.232 | 81.70  |
| J16                     | 2830333.271 | 473915.991 | 25.27  |
| J17                     | 2830338.406 | 473891.247 | 64.82  |
| J18                     | 2830284.911 | 473927.847 | 21.17  |
| J19                     | 2830305.636 | 473932.156 | 112.75 |
| J20                     | 2830372.284 | 474023.095 | 76.19  |
| J21                     | 2830425.667 | 474077.452 | 25.43  |
| J22                     | 2830415.069 | 474100.568 | 20.10  |
| J23                     | 2830425.782 | 474117.575 | 58.83  |
| J14                     | 2830474.991 | 474085.328 |        |
| S=8701.53 平方米 合13.0523亩 |             |            |        |

注：1.界址点间距边长为两点间直线距离  
2.红线图上为斜分界址点