


中山大道与平岗二路交叉口东南侧SC202100017地块红线图

市勘测院
地形图专用章(3)
资料严禁外借

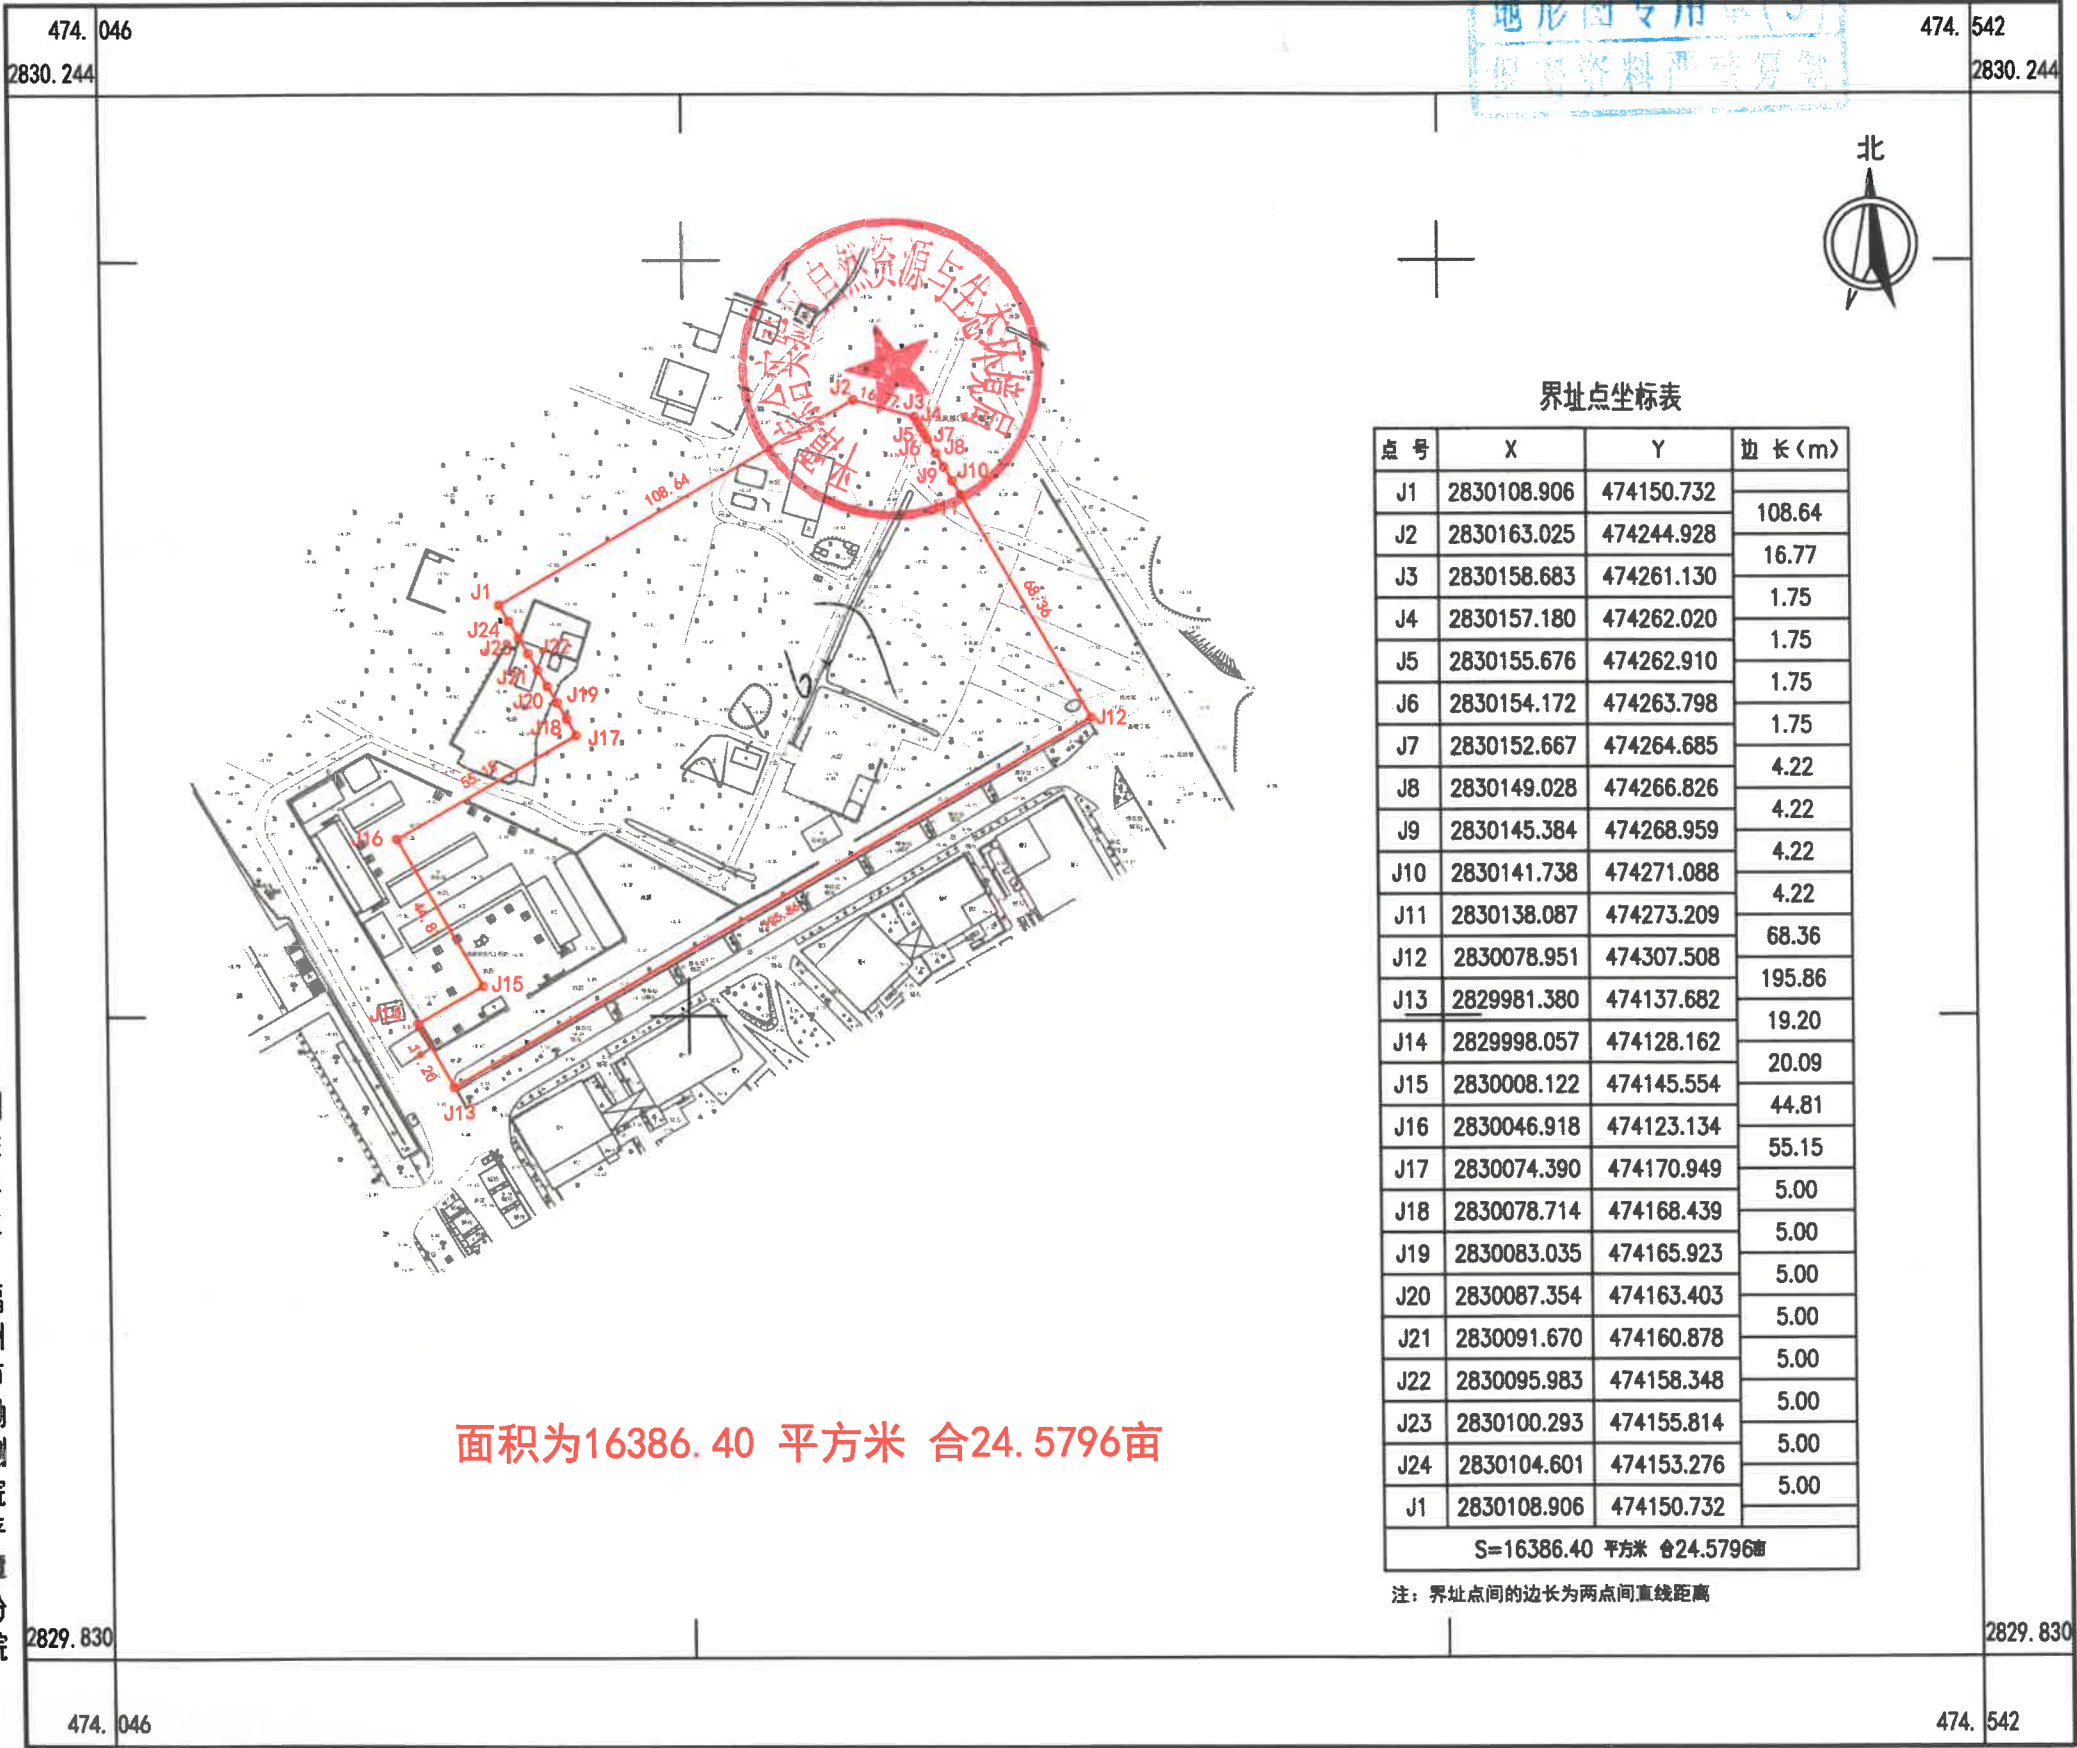

2010年7月数字化成图
2000国家大地坐标系
1985国家高程基准
2009年福州基础地理信息数据图式
加盖福州市勘测院地形图蓝章，方位正式材料

1:2000