


旺业路（鹿原北路-嘉兴路）选址红线图

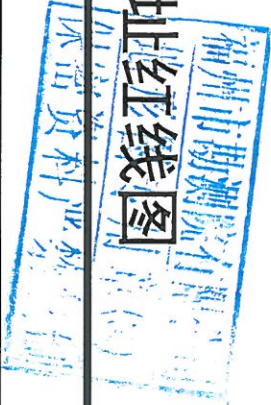


474. 678
2830. 424

475. 098
2830. 424



面积为14564. 66 平方米
合21. 8470亩

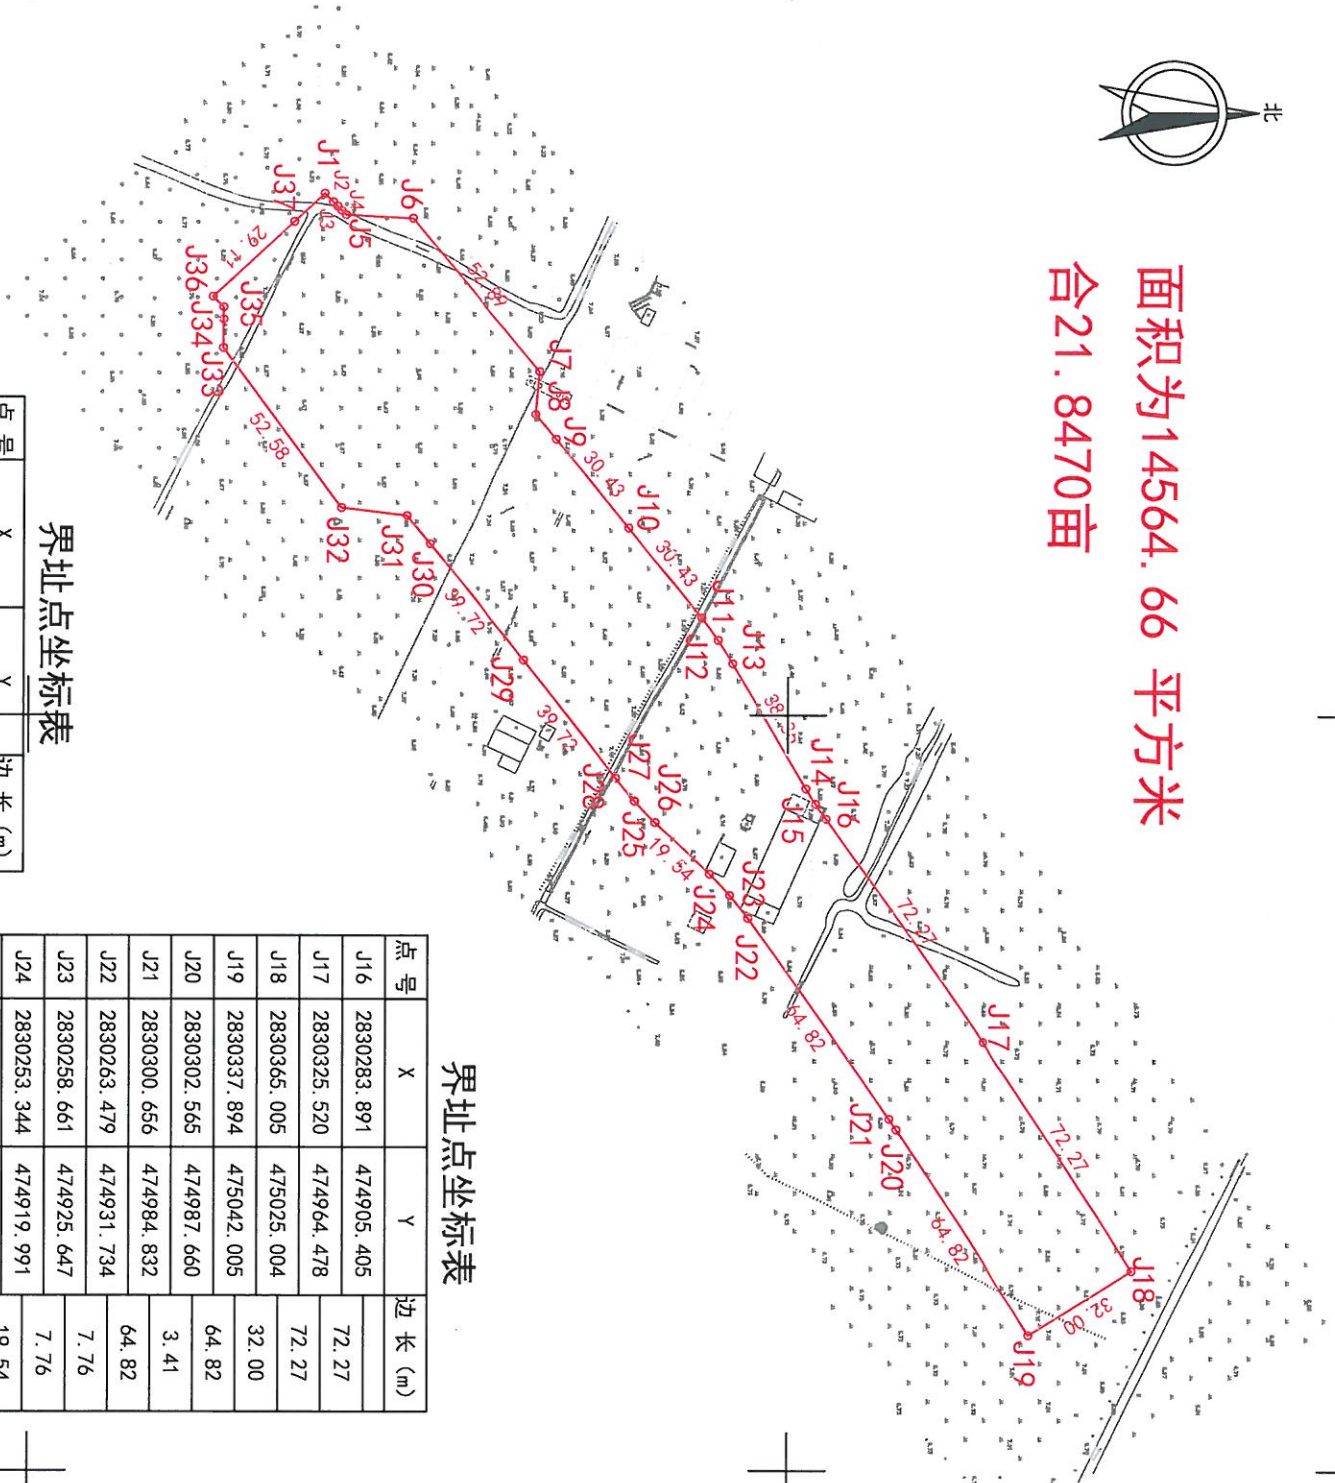

界址点坐标表

点号	X	Y	边长 (m)
J1	2830151. 378	474739. 581	
J2	2830153. 577	474741. 830	3. 15
J3	2830154. 696	474742. 976	1. 60
J4	2830155. 813	474744. 123	1. 60
J5	2830156. 929	474745. 273	1. 60
J6	2830174. 621	474746. 196	17. 72
J7	2830208. 517	474786. 791	52. 89
J8	2830207. 527	474798. 141	11. 39
J9	2830212. 977	474804. 709	8. 53
J10	2830232. 234	474828. 269	30. 43
J11	2830251. 134	474852. 117	30. 43
J12	2830255. 451	474858. 052	7. 34
J13	2830259. 356	474864. 266	7. 34
J14	2830278. 658	474897. 411	38. 36
J15	2830281. 170	474901. 477	4. 78
J16	2830283. 891	474905. 405	4. 78

界址点坐标表

点号	X	Y	边长 (m)
J16	2830283. 891	474905. 405	
J17	2830325. 520	474964. 478	72. 27
J18	2830365. 005	475025. 004	72. 27
J19	2830337. 894	475042. 005	32. 00
J20	2830302. 565	474987. 660	64. 82
J21	2830300. 656	474984. 832	3. 41
J22	2830263. 479	474931. 734	64. 82
J23	2830258. 661	474925. 647	7. 76
J24	2830253. 344	474919. 991	7. 76
J25	2830239. 370	474906. 335	19. 54
J26	2830234. 036	474900. 737	7. 73
J27	2830233. 911	474900. 596	0. 19
J28	2830228. 999	474894. 623	7. 73
J29	2830204. 564	474863. 308	39. 72
J30	2830179. 504	474832. 490	39. 72
J31	2830173. 331	474825. 052	9. 67
J32	2830156. 088	474822. 947	17. 37
J33	2830124. 951	474780. 578	52. 58
J34	2830124. 970	474772. 995	7. 58
J35	2830124. 979	474769. 796	3. 20
J36	2830122. 218	474766. 973	3. 95
J37	2830143. 437	474747. 041	29. 11
J1	2830151. 378	474739. 581	10. 90

注：界址点间的边长为两点间直线距离
红线图上为部分界址点

2829. 874

2829. 874

474. 678

475. 098

2010年7月数字化成图
CGCS2000坐标系，3度分带高斯投影，中央经线120度 1:2000
1985国家高程基准
2009年福州基础地理信息数据图
加盖福州市勘测院地形图蓝章，方为正式报告

测绘单位：福州市勘测院平潭分院