

莲花中路（和平大道-翠园中路）选址红线图



A、B段总面积为38391.47 平方米 合57.5872亩

A段面积为30332.91 平方米 合45.4994亩

桩号	X	Y	桩长 (m)
J02	282516.824	478492.656	10.25
J03	282520.713	478501.537	55.67
J04	282540.941	478549.709	30.20
J05	282546.943	478574.445	157.25
J06	2825387.452	478710.421	32.00
J07	282539.717	478694.659	110.49
J08	282540.345	478606.494	141.81
J09	282540.084	478463.587	32.00
J60	2825306.693	478499.767	6.58
J61	2825211.976	478494.833	3.05
J02	282516.824	478492.656	

5-8088.56 平方米 合12.0278亩

注：界址点前附桩号为相邻点间直线距离

A 段界址点坐标表

桩号	X	Y	桩长 (m)
J1	2825896.656	47779.833	107.99
J2	2825819.070	477855.284	267.89
J3	2825732.469	477896.249	0.97
J4	2825731.983	477897.126	1.99
J5	2825728.111	477806.333	18.39
J6	2825722.852	477823.849	13.35
J7	2825716.594	477834.120	52.50
J8	2825658.582	477882.882	19.61
J9	2825697.248	477882.893	1.32
J10	2825696.328	477882.887	18.06
J11	2825713.13	477823.187	37.00
J12	2825691.067	477823.473	11.52
J13	2825688.432	477826.861	22.22
J14	2825666.686	477841.983	49.00
J15	2825636.587	477844.571	1.89
J16	2825635.647	477886.265	12.59
J17	2825628.742	477896.727	18.58
J18	2825617.672	477811.655	10.62
J19	2825614.849	477832.537	190.20
J20	2825536.524	477850.716	

A 段界址点坐标表


桩号	X	Y	桩长 (m)
J20	2825536.524	477850.716	20.79
J21	2825542.747	477947.671	62.00
J22	2825469.399	478439.869	15.75
J23	2825394.731	478453.485	59.07
J24	2825354.198	478384.286	12.59
J25	2825541.03	478271.754	18.58
J26	2825521.173	478308.636	11.62
J27	2825507.996	478349.594	57.63
J28	2825586.743	478388.006	11.62
J29	2825591.498	478294.509	18.59
J30	2825598.843	478273.429	12.48
J31	2825604.422	478262.271	52.47
J32	2825630.146	478264.534	20.04
J33	2825656.620	478297.116	19.88
J34	2825640.996	478184.058	37.00
J35	2825632.842	478155.765	5.33
J36	2825638.880	478164.122	1.71
J37	2825640.277	478162.112	22.54
J38	2825662.178	478156.791	30.73
J39	2825665.238	478111.612	

A 段界址点坐标表

桩号	X	Y	桩长 (m)
J39	2825665.238	478111.612	11.86
J40	2825639.126	478101.388	18.61
J41	2825710.229	478085.671	11.06
J42	2825706.654	478073.834	20.90
J43	2825715.788	478057.230	9.49
J44	2825718.932	478046.274	3.89
J45	2825717.793	478044.479	13.28
J46	2825724.253	478038.854	23.49
J47	2825734.688	478010.727	13.38
J48	2825741.673	477993.439	3.89
J49	2825744.624	477993.417	9.49
J50	2825749.221	477988.409	27.96
J51	2825808.495	477742.890	32.83
J1	2825836.656	477753.513	

5-90332.91 平方米 合45.4994亩

B段面积为8058.56 平方米 合12.0878亩

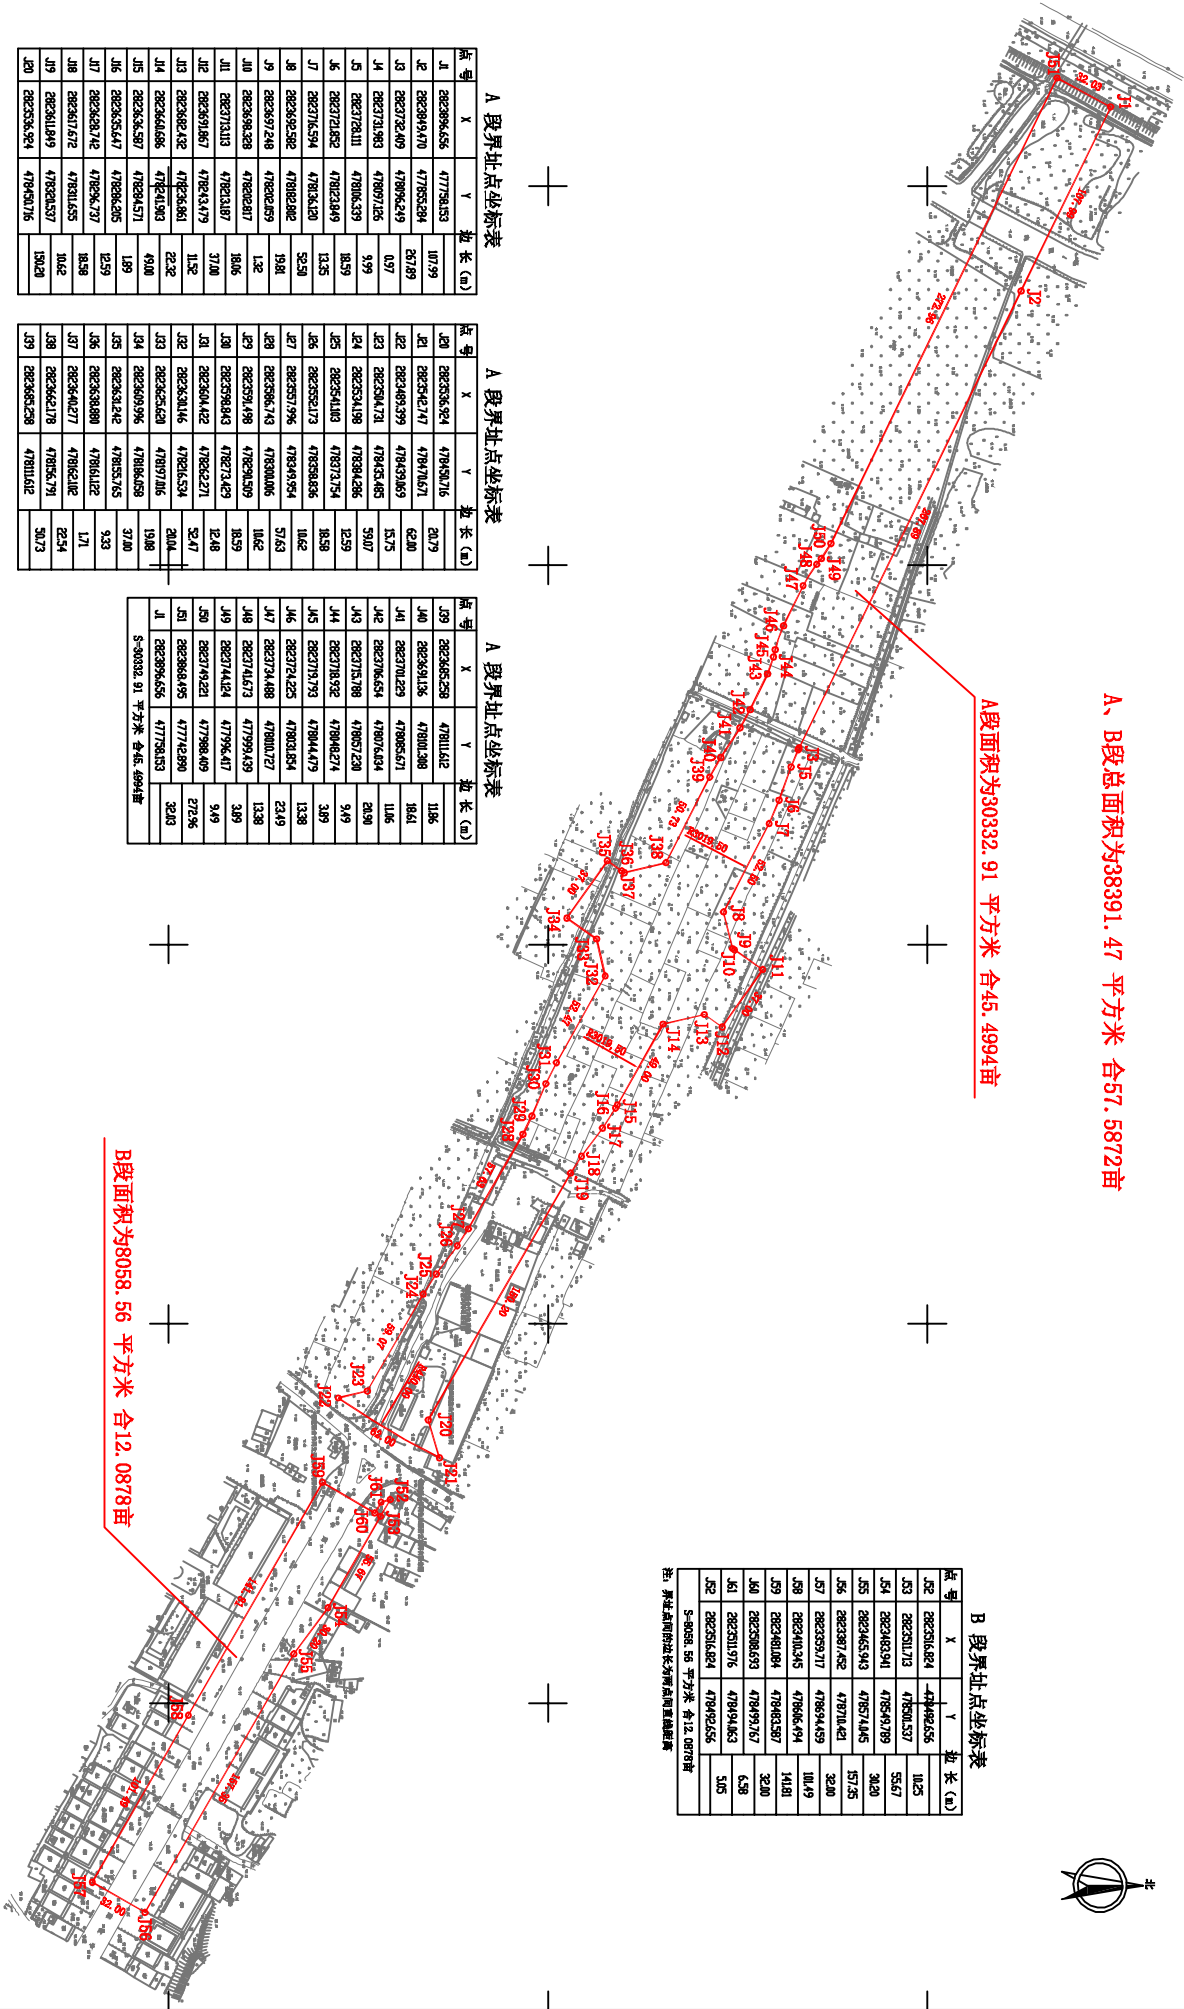

测绘单位：福州市勘测院平潭分院

2020年11月全野外数字测量
2000国家大地坐标系
1985国家高程基准
2009年福州市地形图数据
加盖福州市勘测院地形图盖章，方为正式材料