


嘉兴路与芦洋北路交叉口SC202200002地块村界图

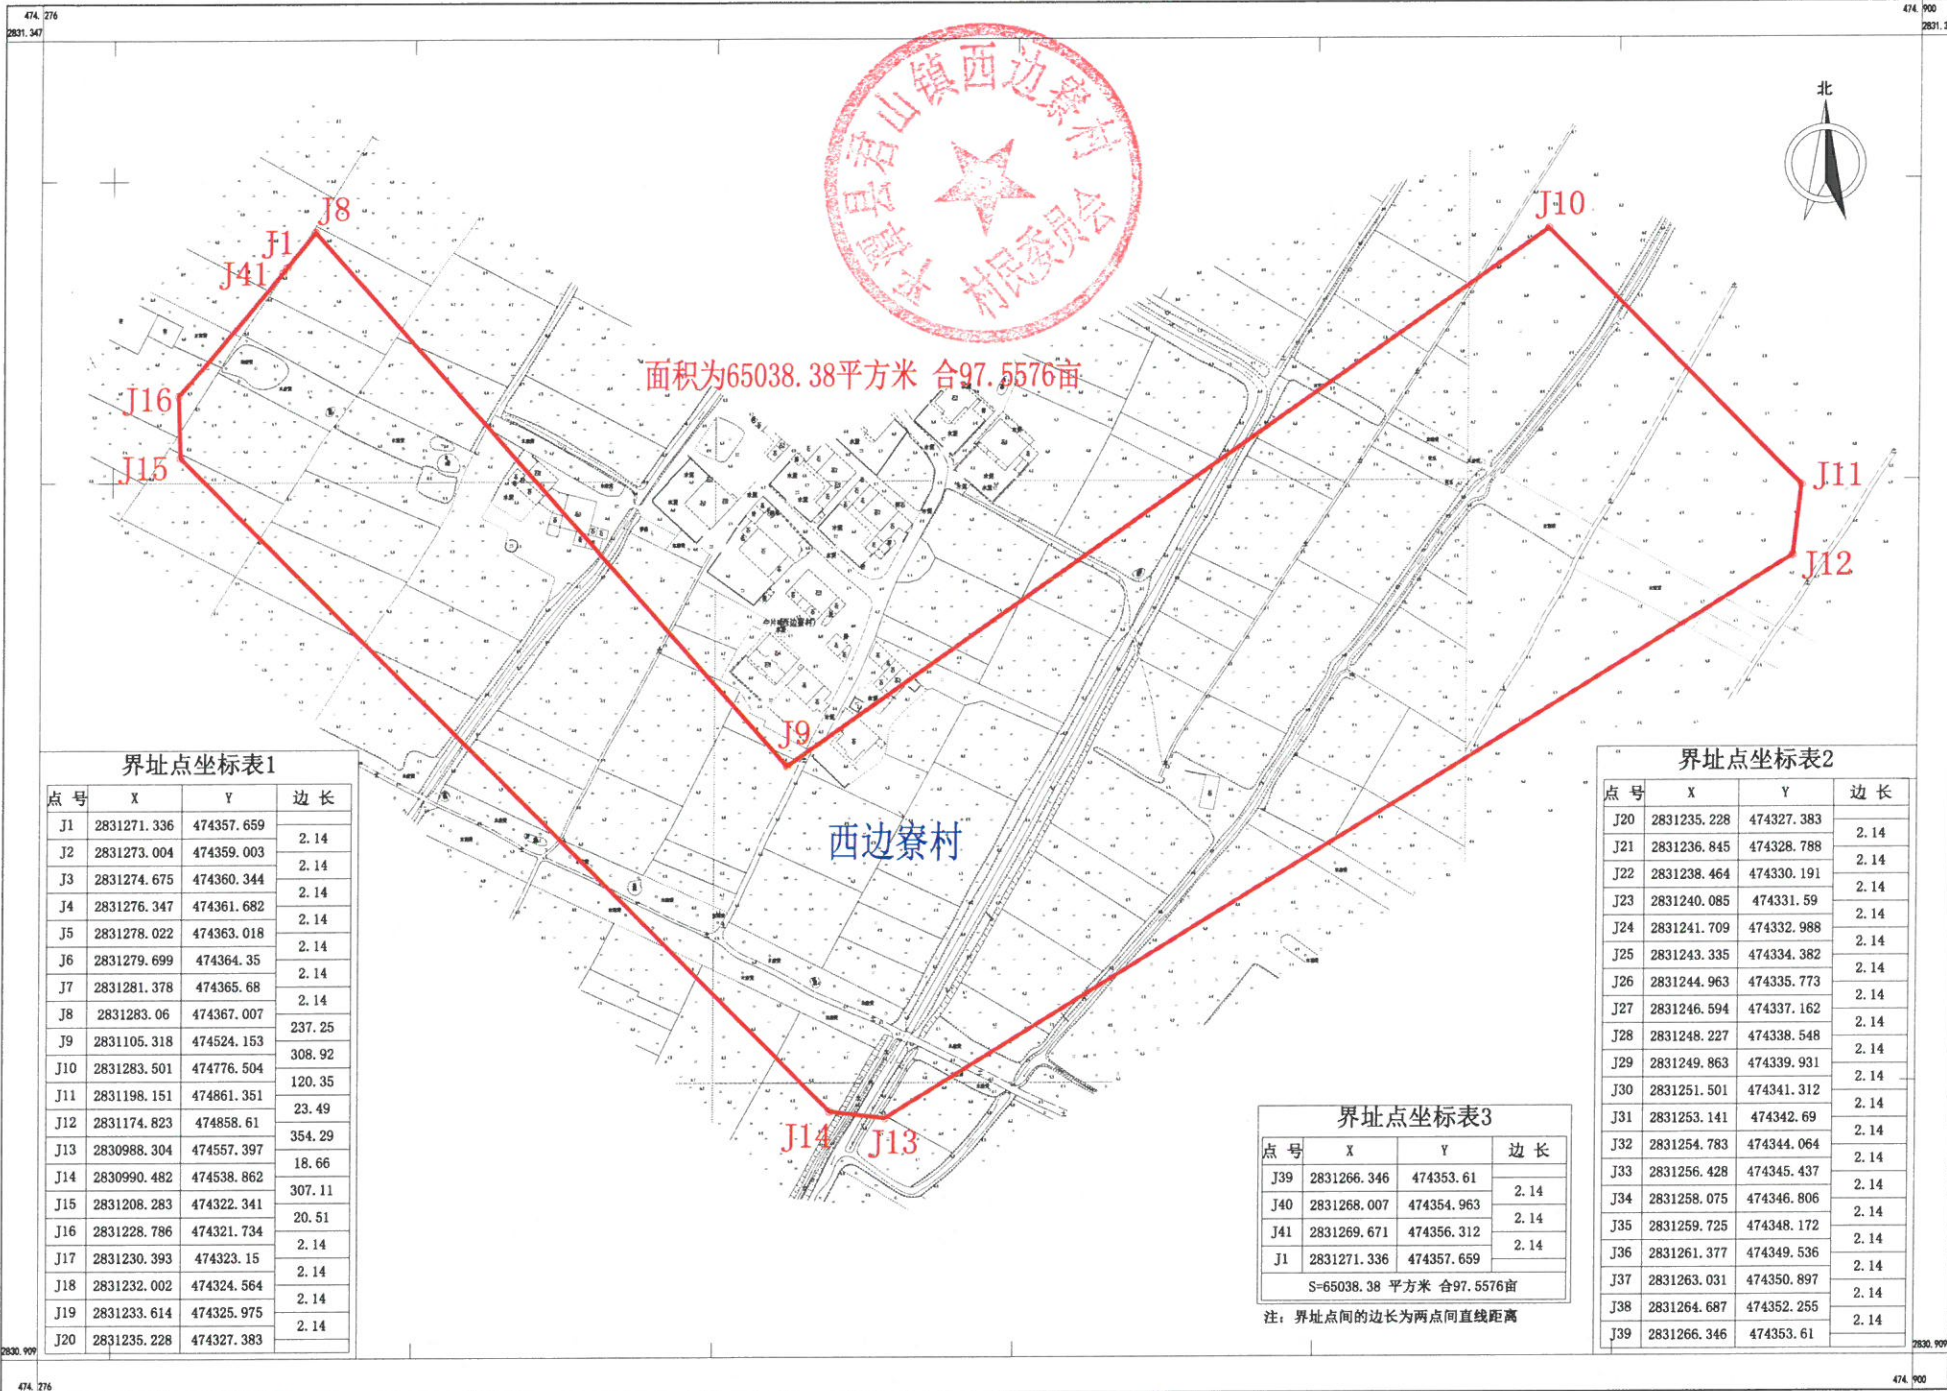

界址点坐标表1

点号	X	Y	边长
J1	2831271.336	474357.659	2.14
J2	2831273.004	474359.003	2.14
J3	2831274.675	474360.344	2.14
J4	2831276.347	474361.682	2.14
J5	2831278.022	474363.018	2.14
J6	2831279.699	474364.35	2.14
J7	2831281.378	474365.68	2.14
J8	2831283.06	474367.007	237.25
J9	2831105.318	474524.153	308.92
J10	2831283.501	474776.504	120.35
J11	2831198.151	474861.351	23.49
J12	2831174.823	474858.61	354.29
J13	2830988.304	474557.397	18.66
J14	2830990.482	474538.862	307.11
J15	2831208.283	474322.341	20.51
J16	2831228.786	474321.734	2.14
J17	2831230.393	474323.15	2.14
J18	2831232.002	474324.564	2.14
J19	2831233.614	474325.975	2.14
J20	2831235.228	474327.383	2.14

界址点坐标表2

点号	X	Y	边长
J20	2831235.228	474327.383	2.14
J21	2831236.845	474328.788	2.14
J22	2831238.464	474330.191	2.14
J23	2831240.085	474331.59	2.14
J24	2831241.709	474332.988	2.14
J25	2831243.335	474334.382	2.14
J26	2831244.963	474335.773	2.14
J27	2831246.594	474337.162	2.14
J28	2831248.227	474338.548	2.14
J29	2831249.863	474339.931	2.14
J30	2831251.501	474341.312	2.14
J31	2831253.141	474342.69	2.14
J32	2831254.783	474344.064	2.14
J33	2831256.428	474345.437	2.14
J34	2831258.075	474346.806	2.14
J35	2831259.725	474348.172	2.14
J36	2831261.377	474349.536	2.14
J37	2831263.031	474350.897	2.14
J38	2831264.687	474352.255	2.14
J39	2831266.346	474353.61	2.14

界址点坐标表3

点号	X	Y	边长
J39	2831266.346	474353.61	2.14
J40	2831268.007	474354.963	2.14
J41	2831269.671	474356.312	2.14
J1	2831271.336	474357.659	2.14

S=65038.38 平方米 合97.5576亩

注：界址点间的边长为两点间直线距离