


中山大道与旺业路交叉口东南侧SC202100029地块红线图


474. 200 2830. 112 474. 700 2830. 112

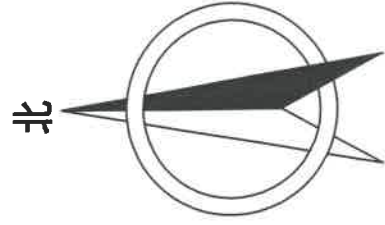

界址点坐标表

点号	X	Y	边长(m)
J1	2829785.828	474267.016	31.48
J2	2829801.633	474294.242	35.17
J3	2829822.227	474322.757	105.61
J4	2829875.235	474414.097	1.94
J5	2829876.210	474415.778	13.61
J6	2829873.233	474429.058	378.57
J7	2829561.650	474644.065	44.98
J8	2829583.028	474604.486	23.54
J9	2829596.326	474585.066	32.60
J10	2829612.190	474556.588	8.24
J11	2829615.530	474549.050	16.73
J12	2829625.549	474535.649	29.97
J13	2829636.476	474507.743	18.54
J14	2829646.424	474492.094	26.16
J15	2829656.505	474467.960	20.06
J16	2829667.298	474451.053	13.00
J17	2829670.637	474438.489	14.38
J18	2829676.077	474425.177	7.45
J19	2829681.492	474420.062	9.25
J20	2829680.331	474410.887	40.12
J21	2829669.586	474372.227	29.84
J22	2829658.113	474344.680	7.50
J23	2829655.615	474337.603	148.12
J1	2829785.828	474267.016	
S=43822.05 平方米 合65.7331亩			

注：界址点间的边长为两点间直线距离

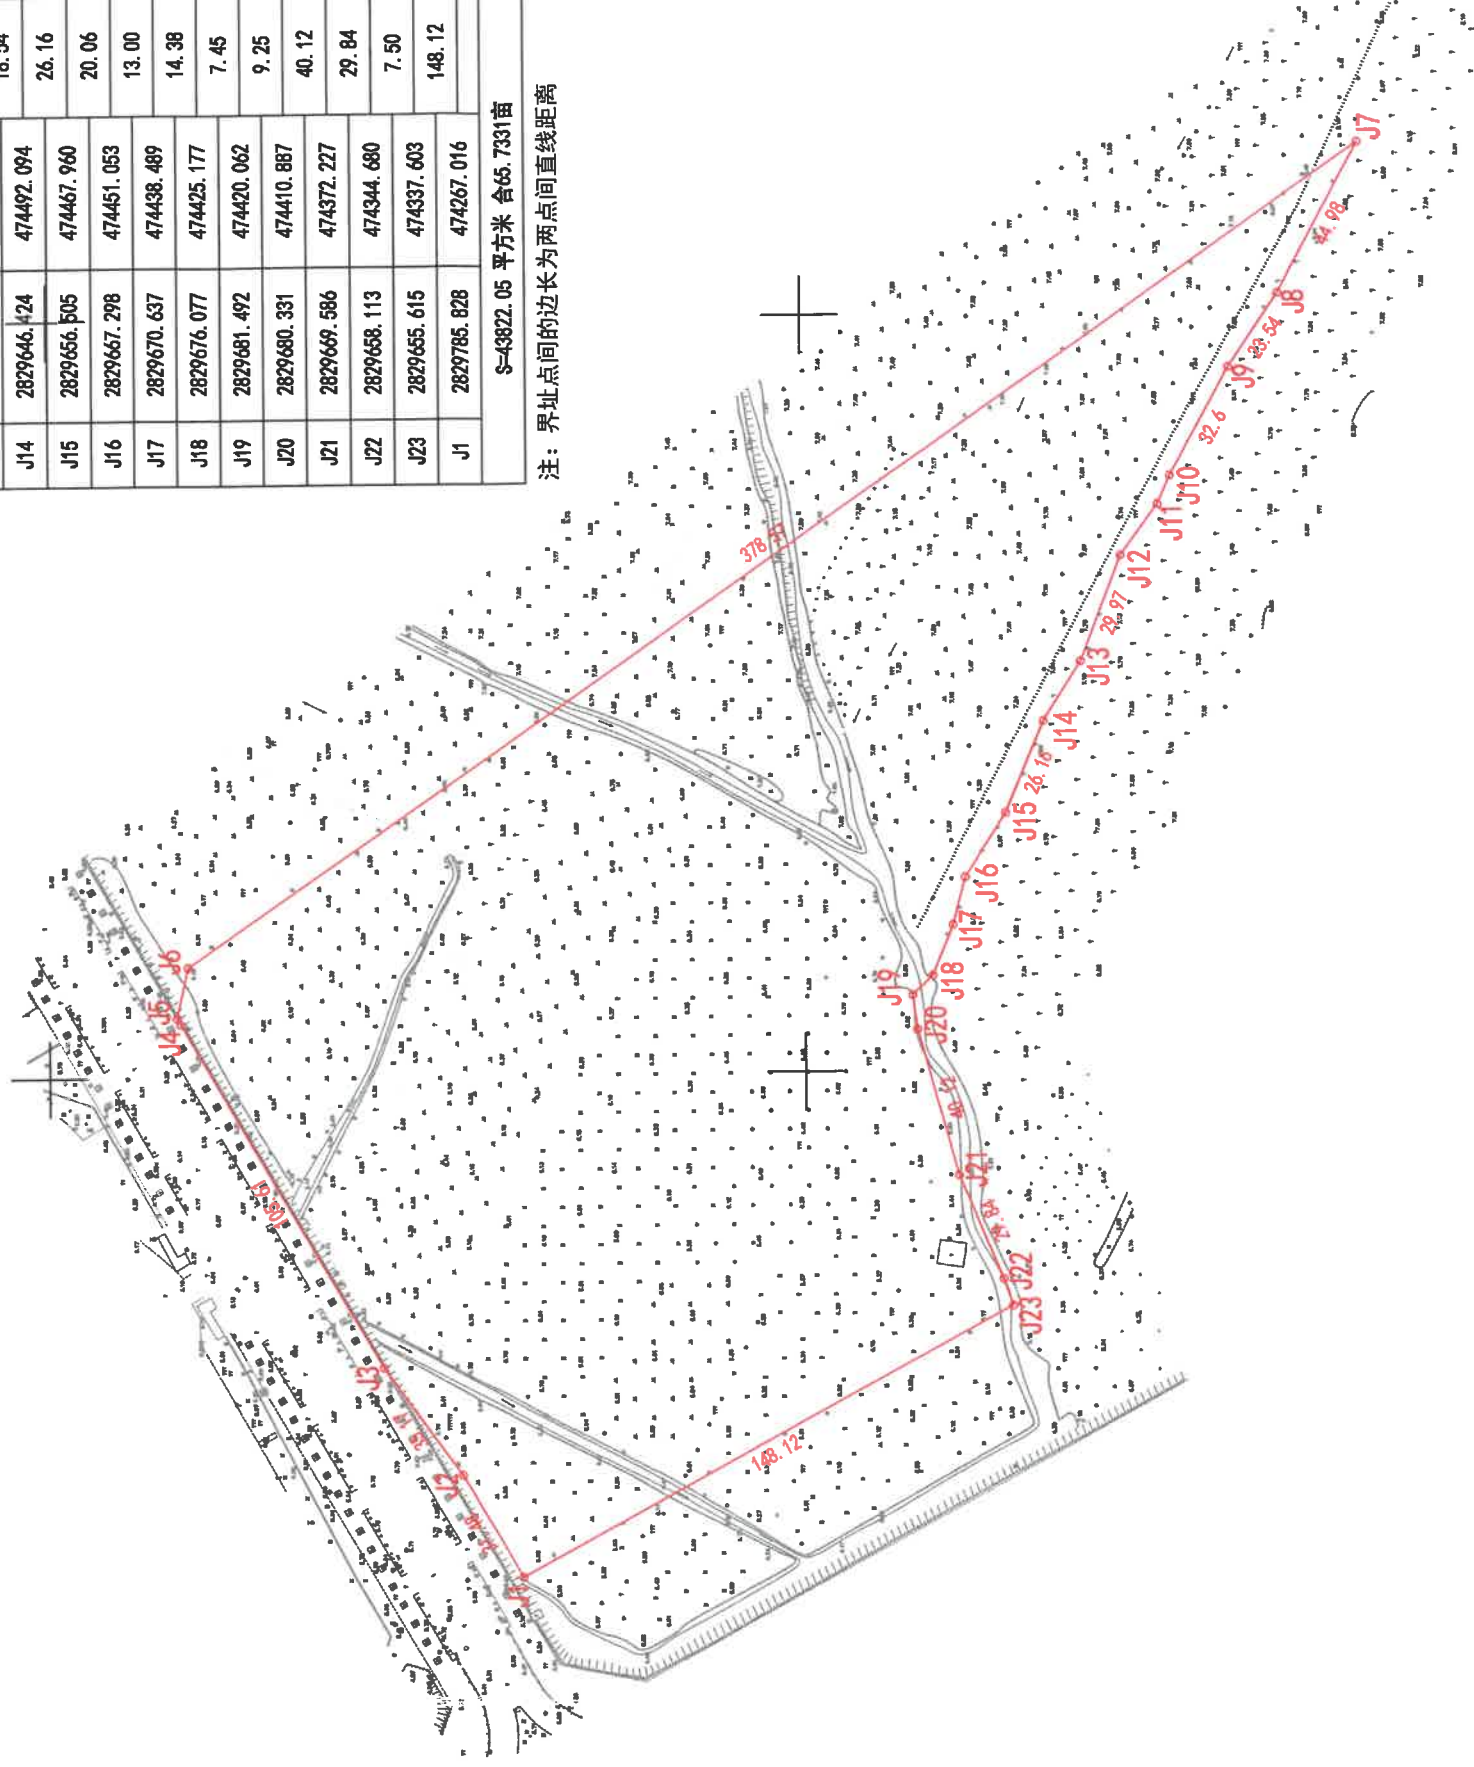

2829. 510 474. 200 2829. 510 474. 700

测绘单位：福州市勘测院平潭分院

2010年7月数字化成图
CGCS2000坐标系, 3度分带高斯投影, 中央经线120度
1985国家高程基准
2009年福州基础地理信息数据图式
加盖福州市勘测院地形图蓝章, 方为正式材料

1:2000