


供水管网完善工程III标段选址红线图(一)

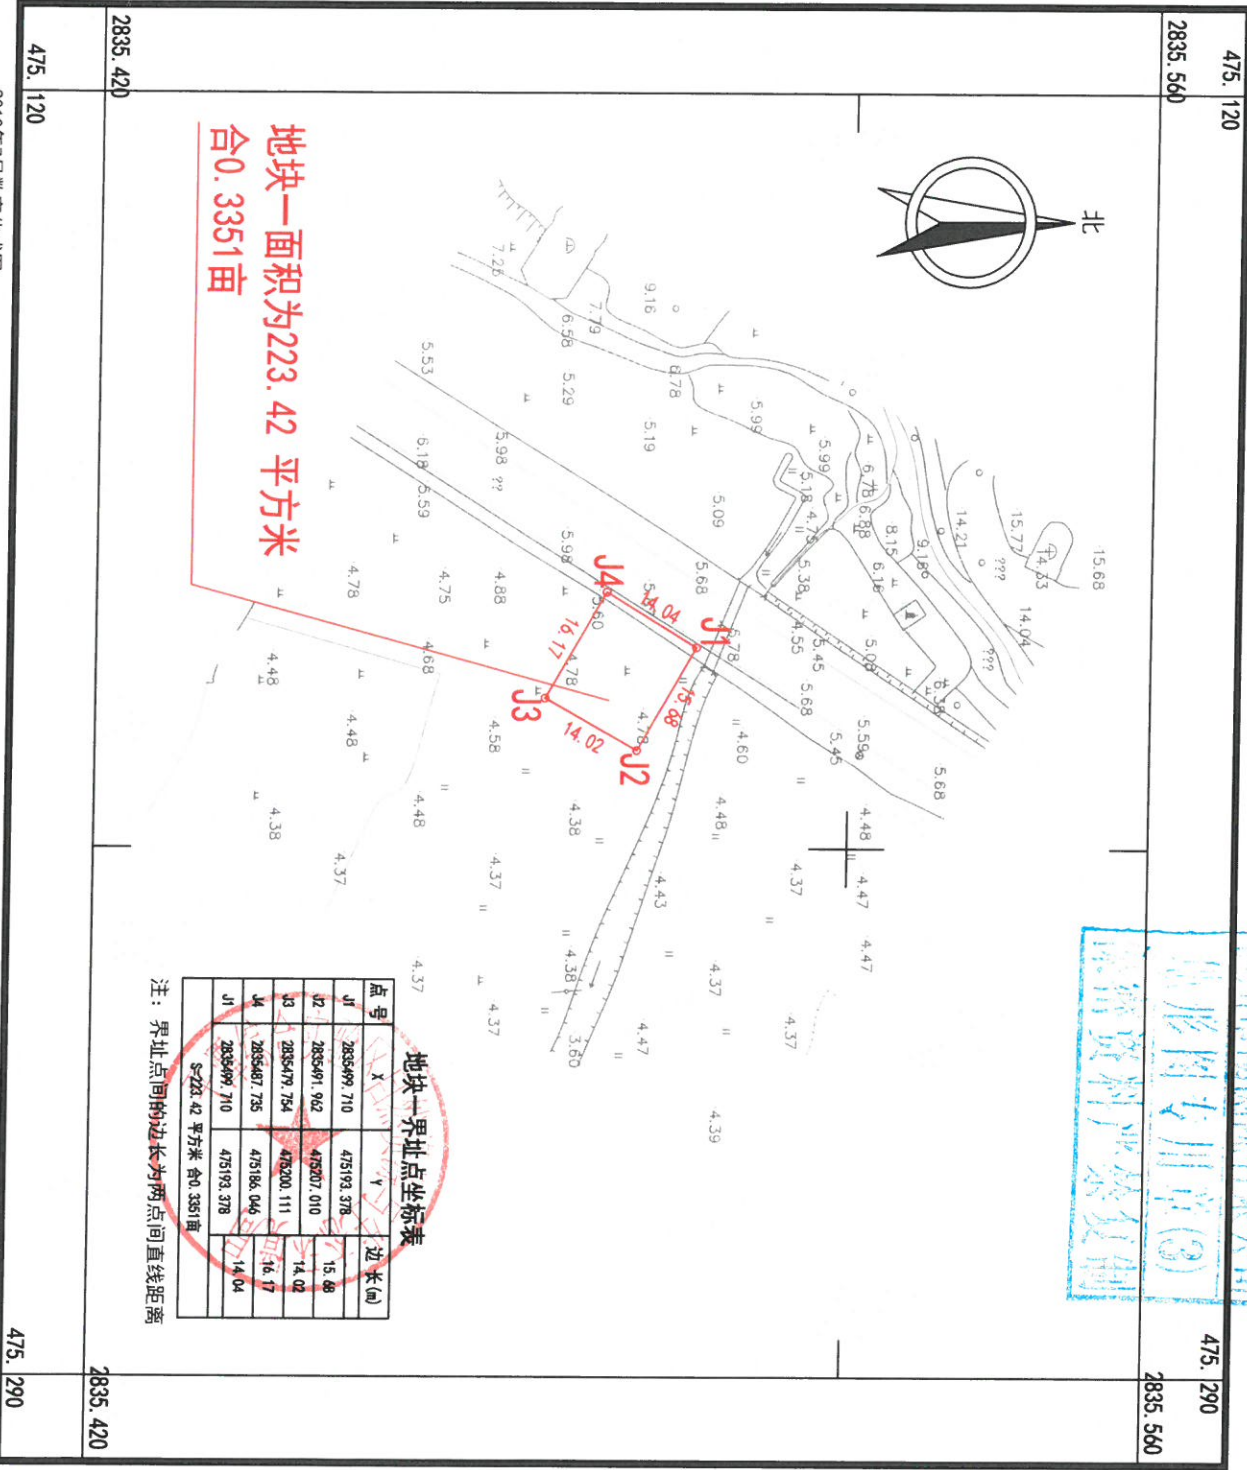

测绘单位：福州市勘测院平潭分院

2010年7月数字化成图
CGCS2000坐标系, 3度分带高斯投影, 中央经线120度
1985国家高程基准
2009年福州基础地理信息数据图式
加盖福州市勘测院地形图蓝章, 方为正式材料

1:1000