


麒麟大道（福平互通-瑶竹路）完善工程选址红线图

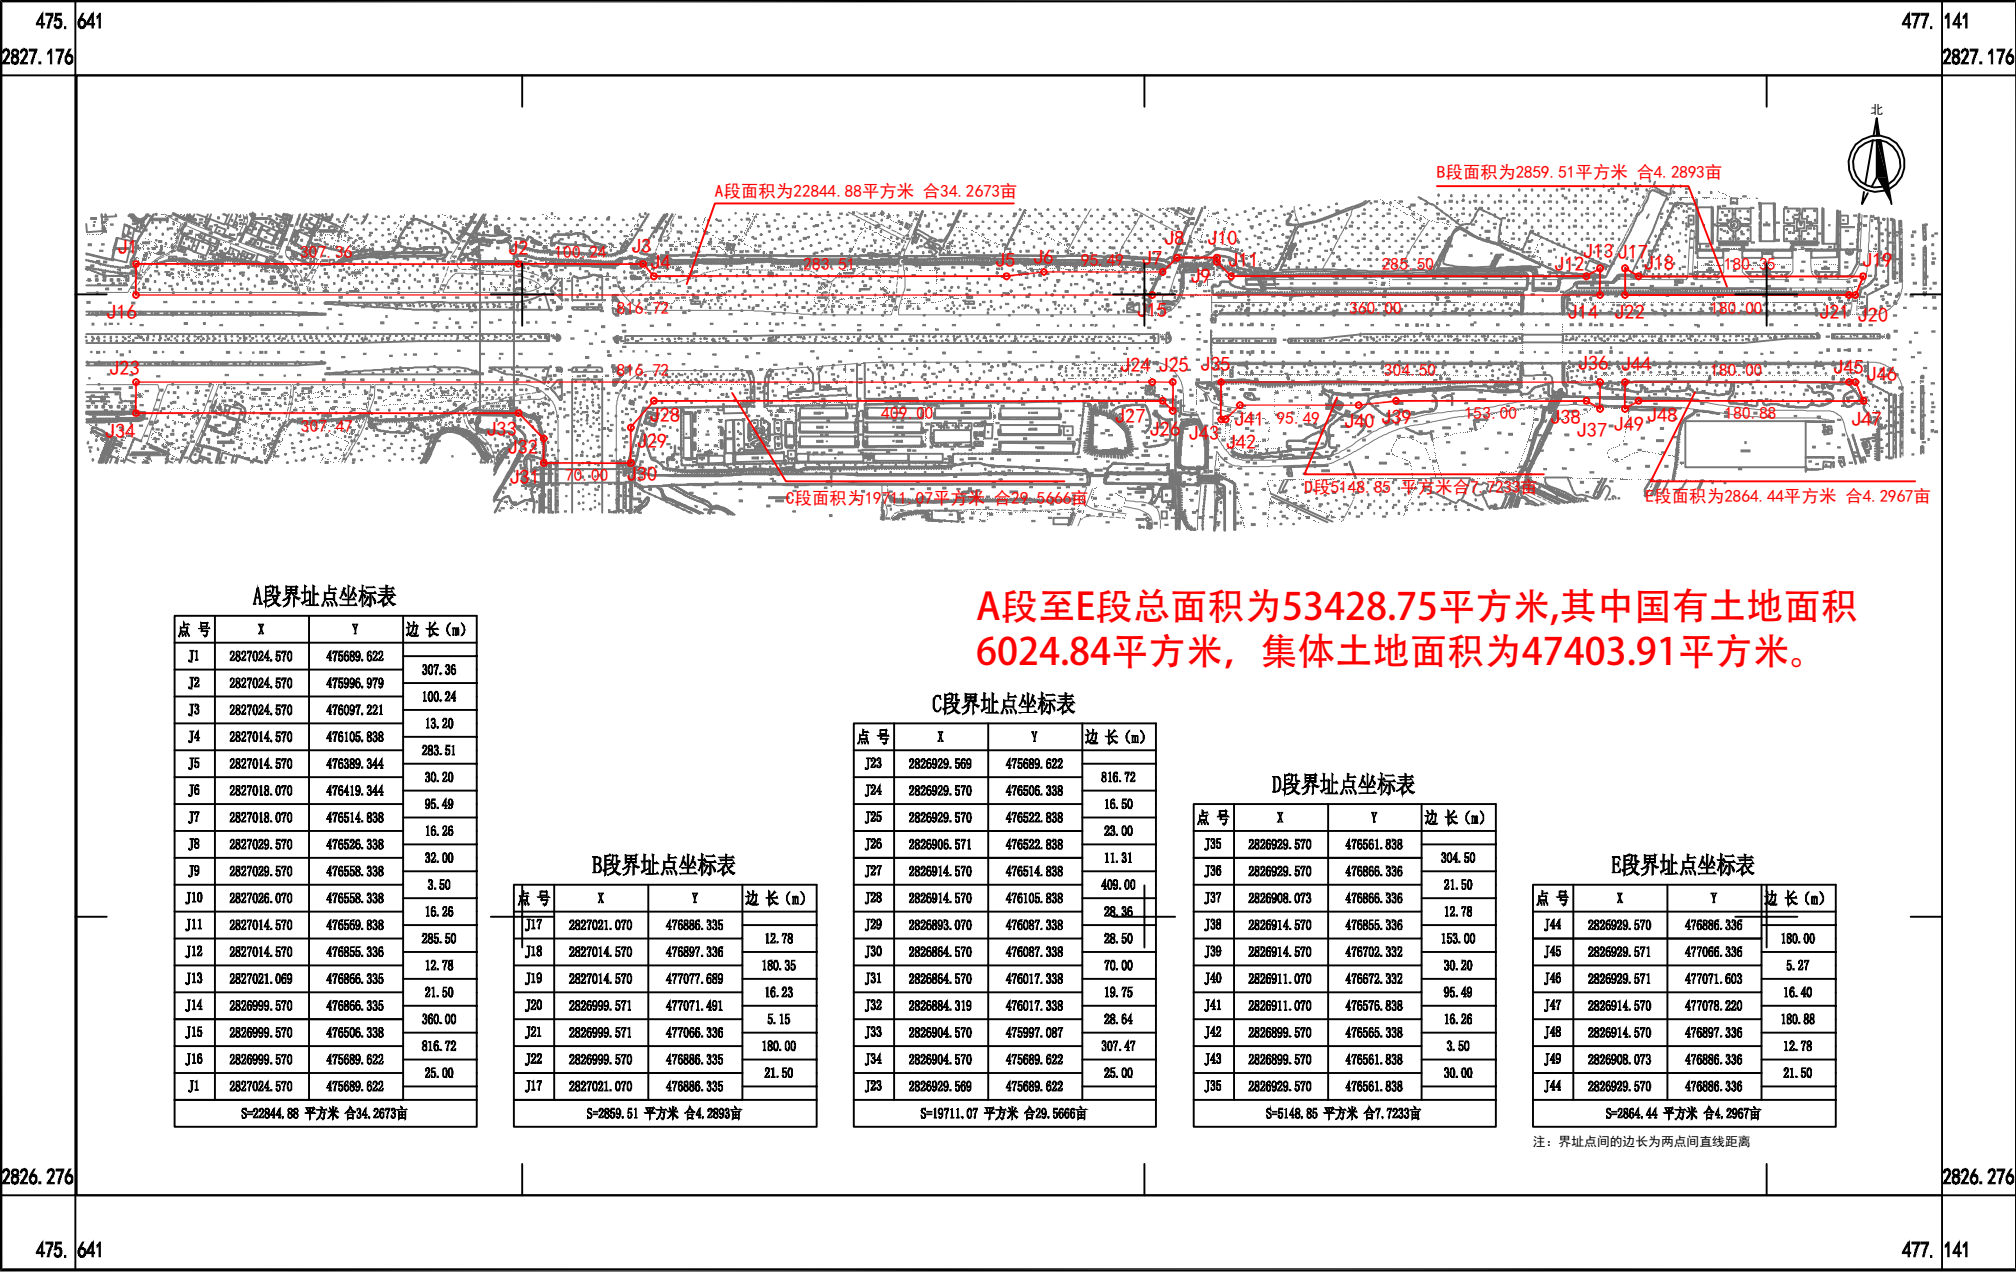

由 Autodesk 教育版产品制作

测绘单位：福州市勘测院平潭分院

2010年7月数字化成图
2000国家大地坐标系
1985国家高程基准
2009年福州基础地理信息数据图式
加盖福州市勘测院地形图蓝章，方为正式材料

1:5000

由 Autodesk 教育版产品制作