

A段面积为12782.27 平方米
合19.1734亩

A段+B段总面积为28832.85平方米
合43.2493亩

A段界址点坐标表

点号	X	Y	边长(m)
J1	2826829.570	476522.838	39.00
J2	2826829.570	476561.838	70.42
J3	2826859.146	476561.838	35.17
J4	2826824.146	476558.338	121.45
J5	2826702.699	476558.338	34.97
J6	2826667.902	476561.777	107.56
J7	2826590.358	476559.668	35.50
J8	2826562.030	476524.207	90.43
J9	2826652.436	476526.338	57.13
J10	2826709.571	476526.338	135.41
J11	2826844.978	476526.338	25.24
J12	2826889.978	476522.838	59.59
J1	2826829.570	476522.838	


S=12782.27 ㎡ 合 19.1734 亩

B段界址点坐标表

点号	X	Y	边长(m)
J13	2826482.473	476515.283	35.50
J14	2826479.323	476550.643	64.91
J15	2826414.774	476543.809	35.21
J16	2826379.584	476542.699	63.11
J17	2826317.246	476532.882	70.22
J18	2826248.296	476519.600	189.58
J19	2826064.933	476471.450	39.00
J20	2826076.656	476434.254	162.70
J21	2826253.331	476480.800	77.66
J22	2826329.599	476495.436	154.16
J13	2826482.473	476515.283	

S=16050.58 ㎡ 合 24.0759 亩

注：界址点间的边长为两点间直线距离

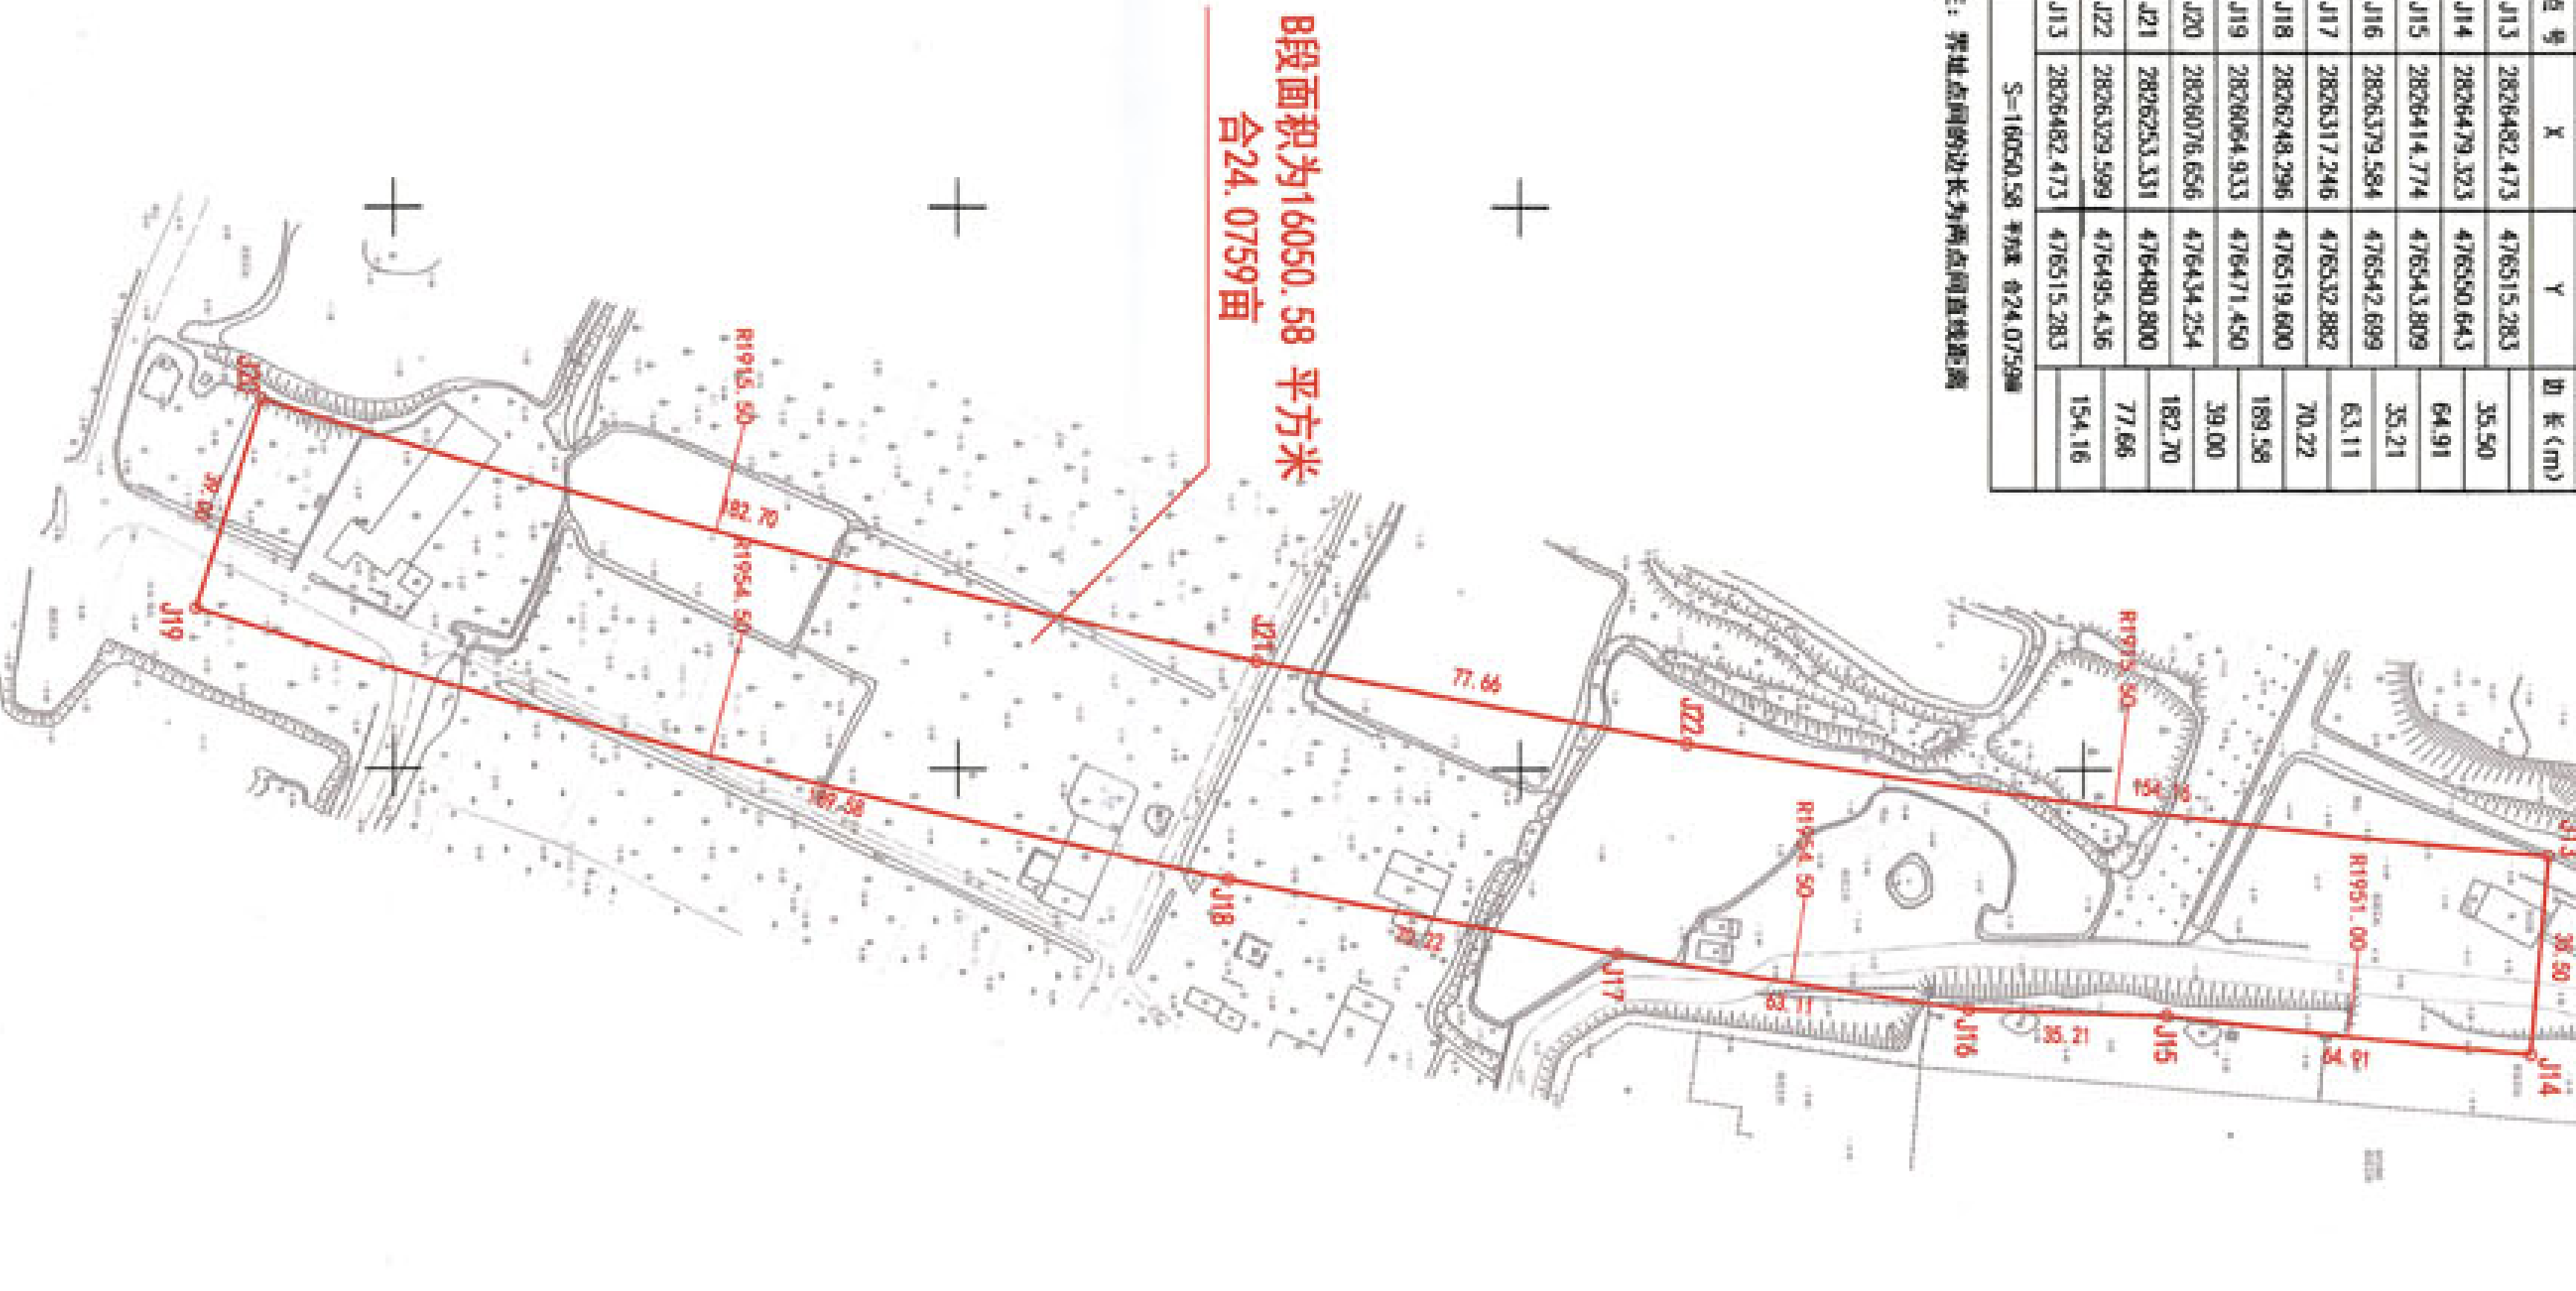

测绘单位：温州市勘测院平测分院

2020年6月27日
2000国家大地坐标系
1985国家高程基准
2009年温州市城市总体规划图式
温州市勘测院提供