


猴研岛旅游基础设施配套工程选址红线图

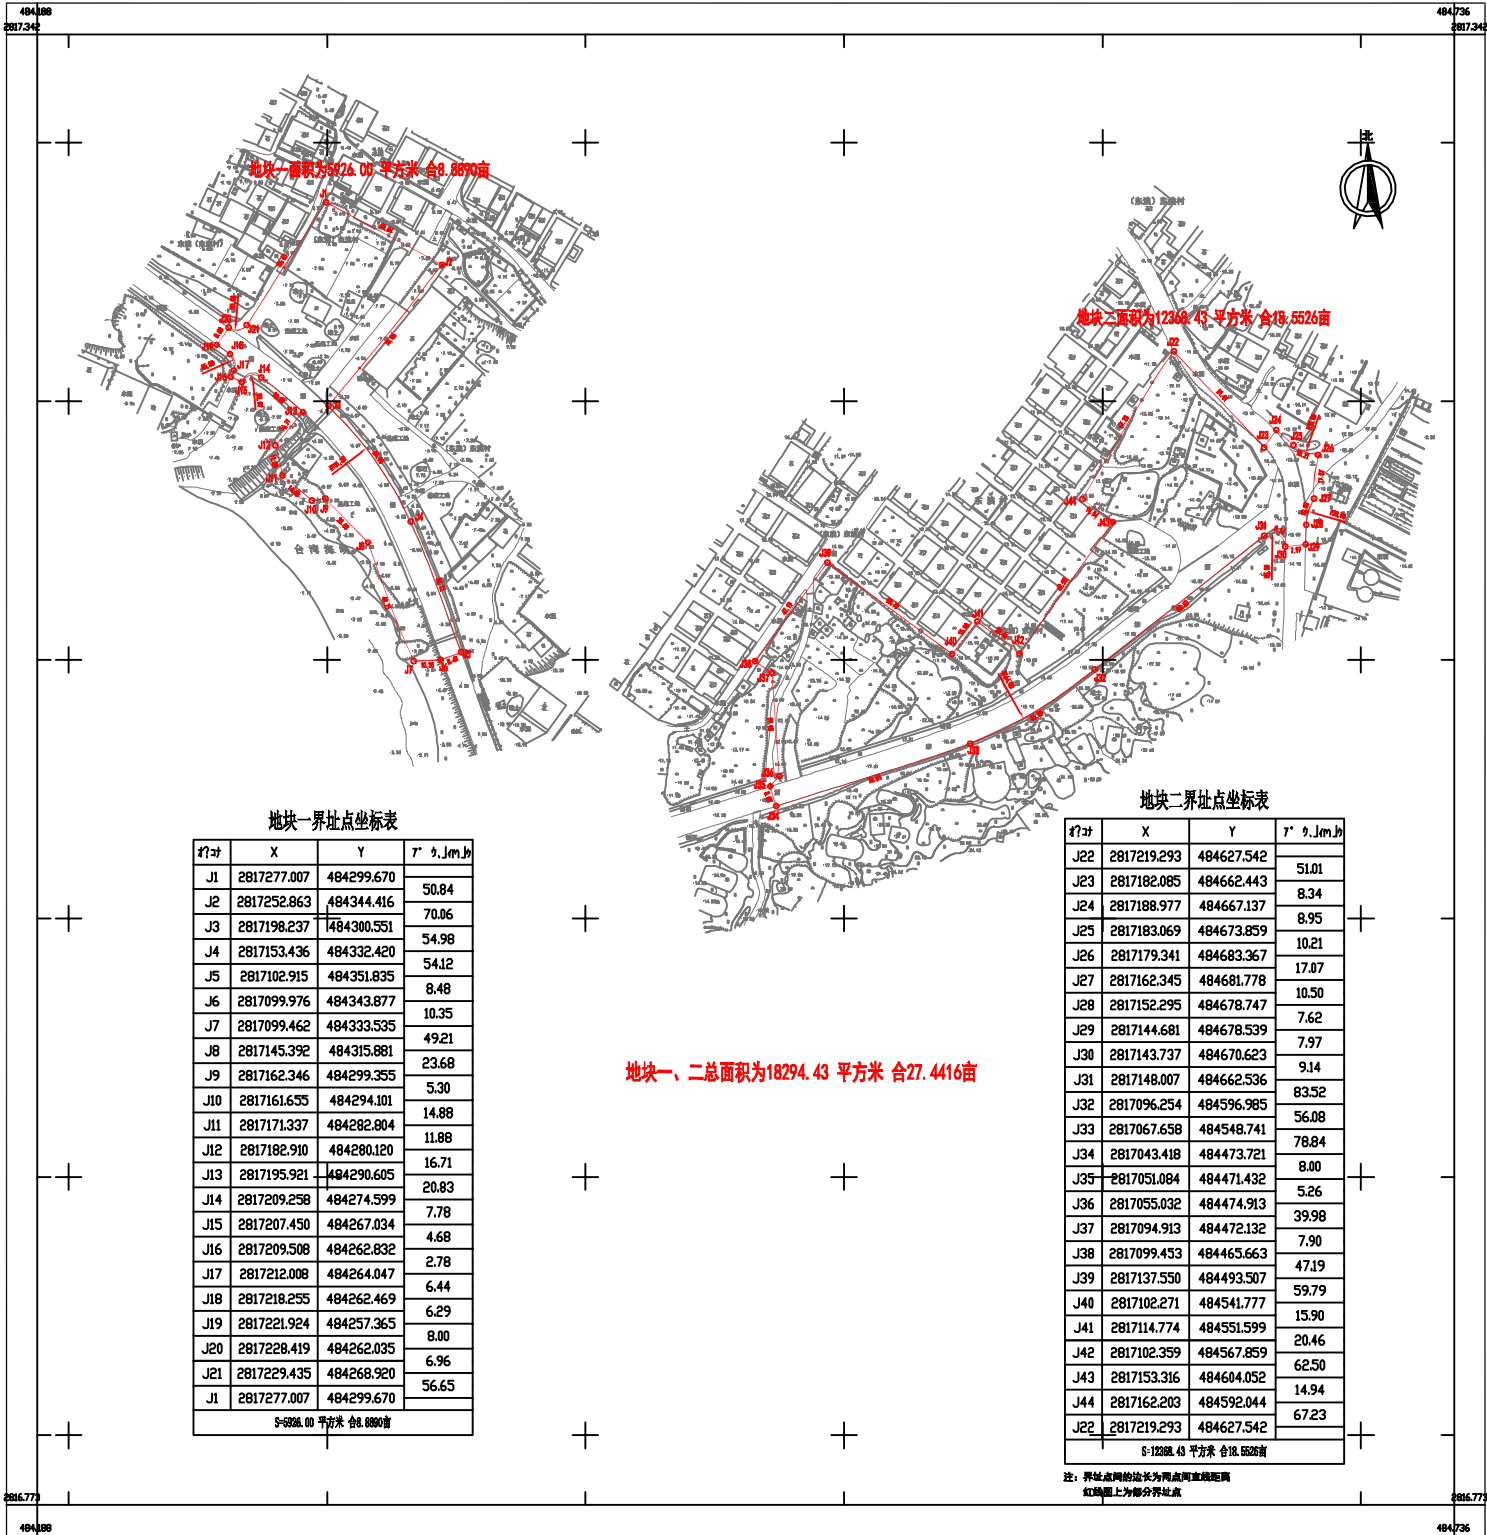

测绘单位：温州市勘测院千禧分院

2018年7月委托成果
2018年7月31日完成
2018年7月31日
2018年7月31日
2018年7月31日
2018年7月31日

1:1000