


南澳二路（环岛路西侧段）选址红线图

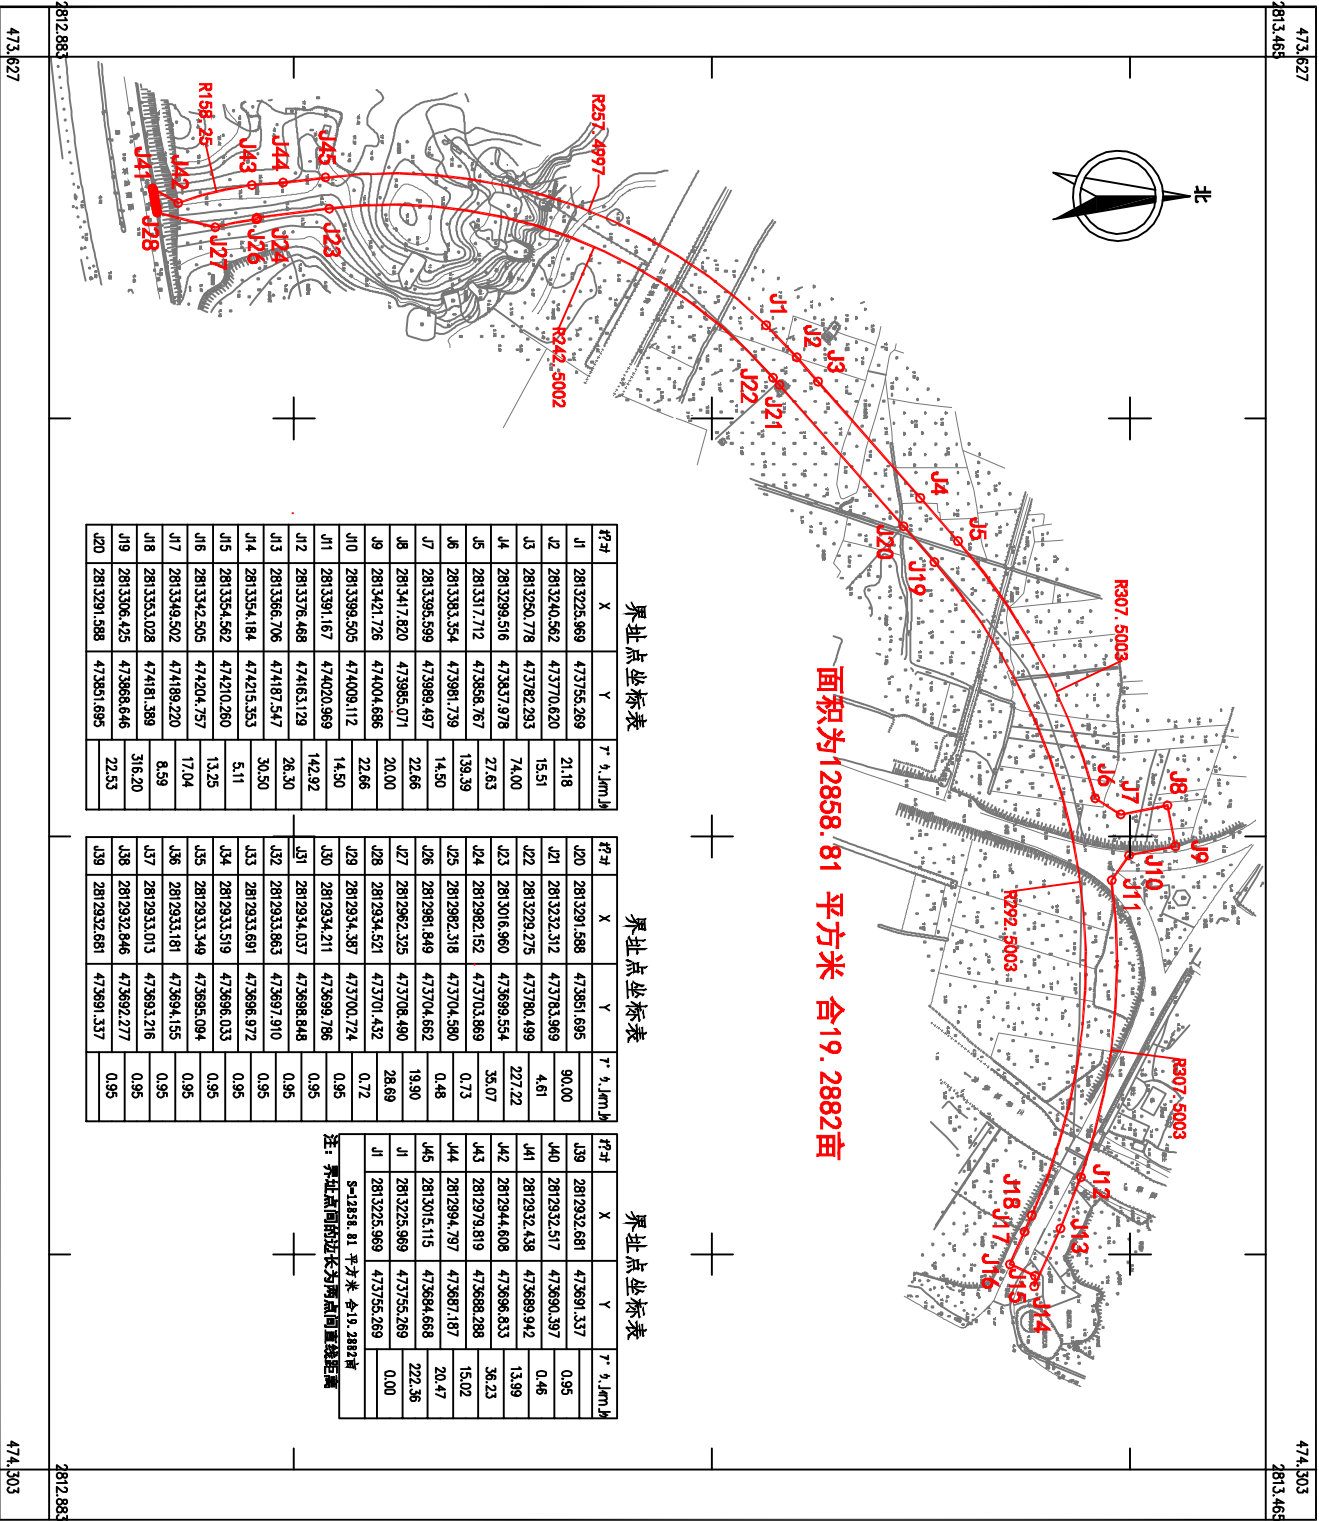

界址点坐标表

点号	X	Y	T° 9.4m.m
J1	2813225.969	473755.269	21.18
J2	2813240.562	473770.620	15.51
J3	2813250.778	473782.293	74.00
J4	2813298.516	473837.978	27.63
J5	2813317.712	473868.767	139.39
J6	2813383.354	473981.739	14.50
J7	2813395.599	473989.497	22.66
J8	2813417.820	473985.071	20.00
J9	2813421.726	474004.696	22.66
J10	2813399.505	474009.112	14.50
J11	2813391.167	474020.969	142.92
J12	2813376.468	474163.129	26.30
J13	2813366.706	474187.547	30.50
J14	2813354.184	474215.353	5.11
J15	2813354.562	474210.260	13.25
J16	2813342.505	474204.757	17.04
J17	2813349.502	474189.220	8.59
J18	2813353.028	474181.389	316.20
J19	2813306.425	473968.646	22.53
J20	2813291.388	473851.695	

界址点坐标表

点号	X	Y	T° 9.4m.m
J20	2813291.388	473851.695	90.00
J21	2813232.312	473783.969	4.61
J22	2813229.275	473780.499	227.22
J23	2813016.960	473699.554	35.07
J24	2812982.152	473703.869	0.73
J25	2812982.318	473704.580	0.48
J26	2812981.849	473704.662	19.90
J27	2812982.325	473708.490	28.69
J28	2813421.521	473701.432	0.72
J29	2812934.387	473700.724	0.95
J30	2812934.211	473699.786	0.95
J31	2812934.037	473698.848	0.95
J32	2812933.963	473697.910	0.95
J33	2812933.691	473696.972	0.95
J34	2812933.549	473696.033	0.95
J35	2812933.181	473694.155	0.95
J36	2812933.013	473693.216	0.95
J37	2812932.846	473692.277	0.95
J38	2812932.681	473691.337	0.95
J39	2812932.516	473690.398	0.95

界址点坐标表

点号	X	Y	T° 9.4m.m
J39	2812932.516	473690.398	0.95
J40	2812932.357	473690.397	0.46
J41	2812932.438	473689.942	13.99
J42	2812944.608	473686.833	36.23
J43	2812979.819	473688.288	15.02
J44	2812984.797	473687.167	20.47
J45	2813015.115	473684.668	222.36
J1	2813225.969	473755.269	0.00

注：界址点间的边长为两面角垂直距离

2010年7月数字化成果
2000国家大地坐标系
1985国家高程基准
2009年福州市勘测院地形图查算，方为正式材料

1:2000