


# 君山路与中山大道交叉口西南侧SC201900062地块红线图

测绘院

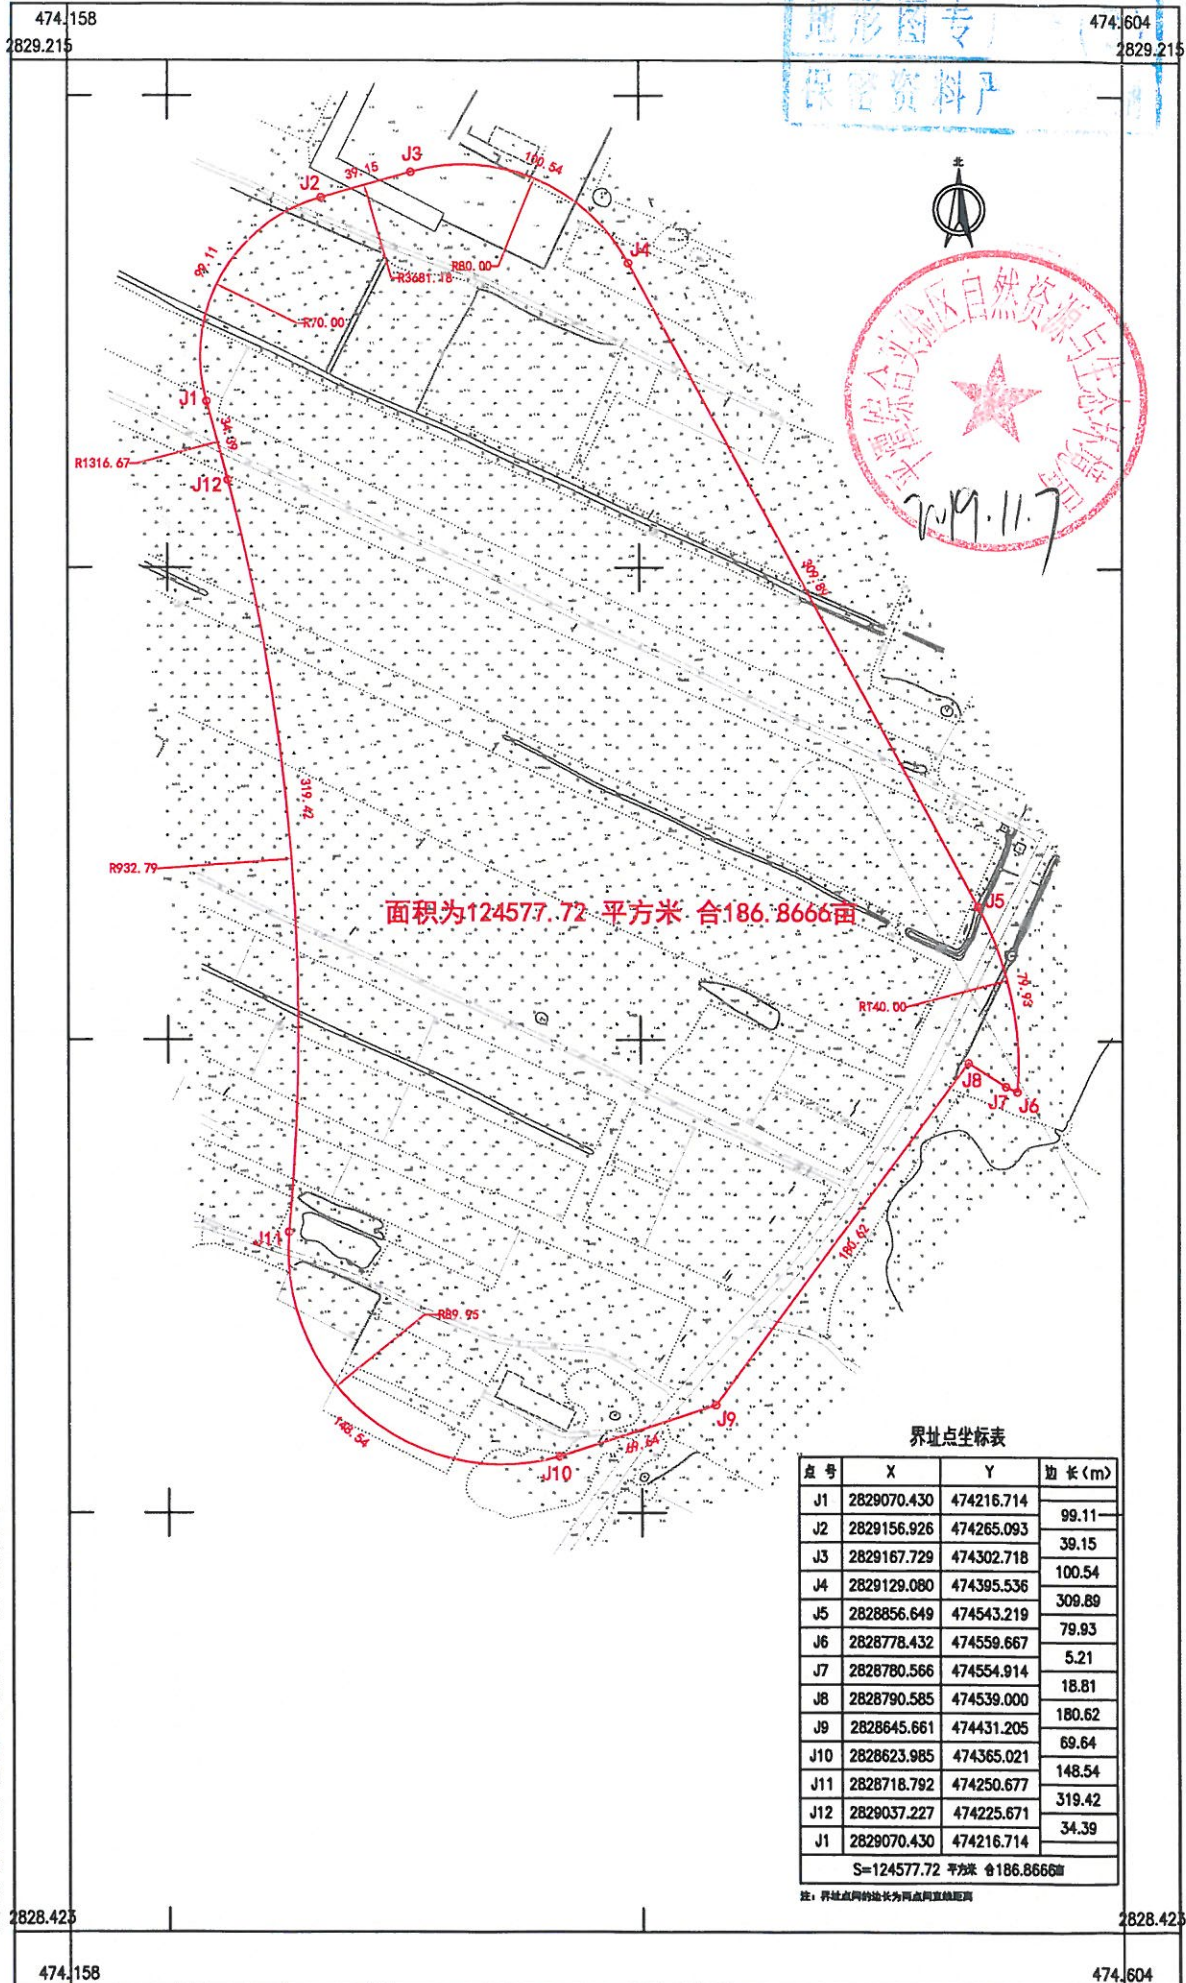

测绘单位：福州市勘测院平潭分院

2010年7月数字化成图  
2000国家大地坐标系  
1985国家高程基准  
2009年福州基础地理信息数据图式  
加盖福州市勘测院地形图蓝章，方为正式材料