


平潭综合实验区自来水厂工程（二期）用地红线图（二）

476.008
2819.734

476.452
2819.734

地块二面积为13247.12 平方米 合19.8707亩

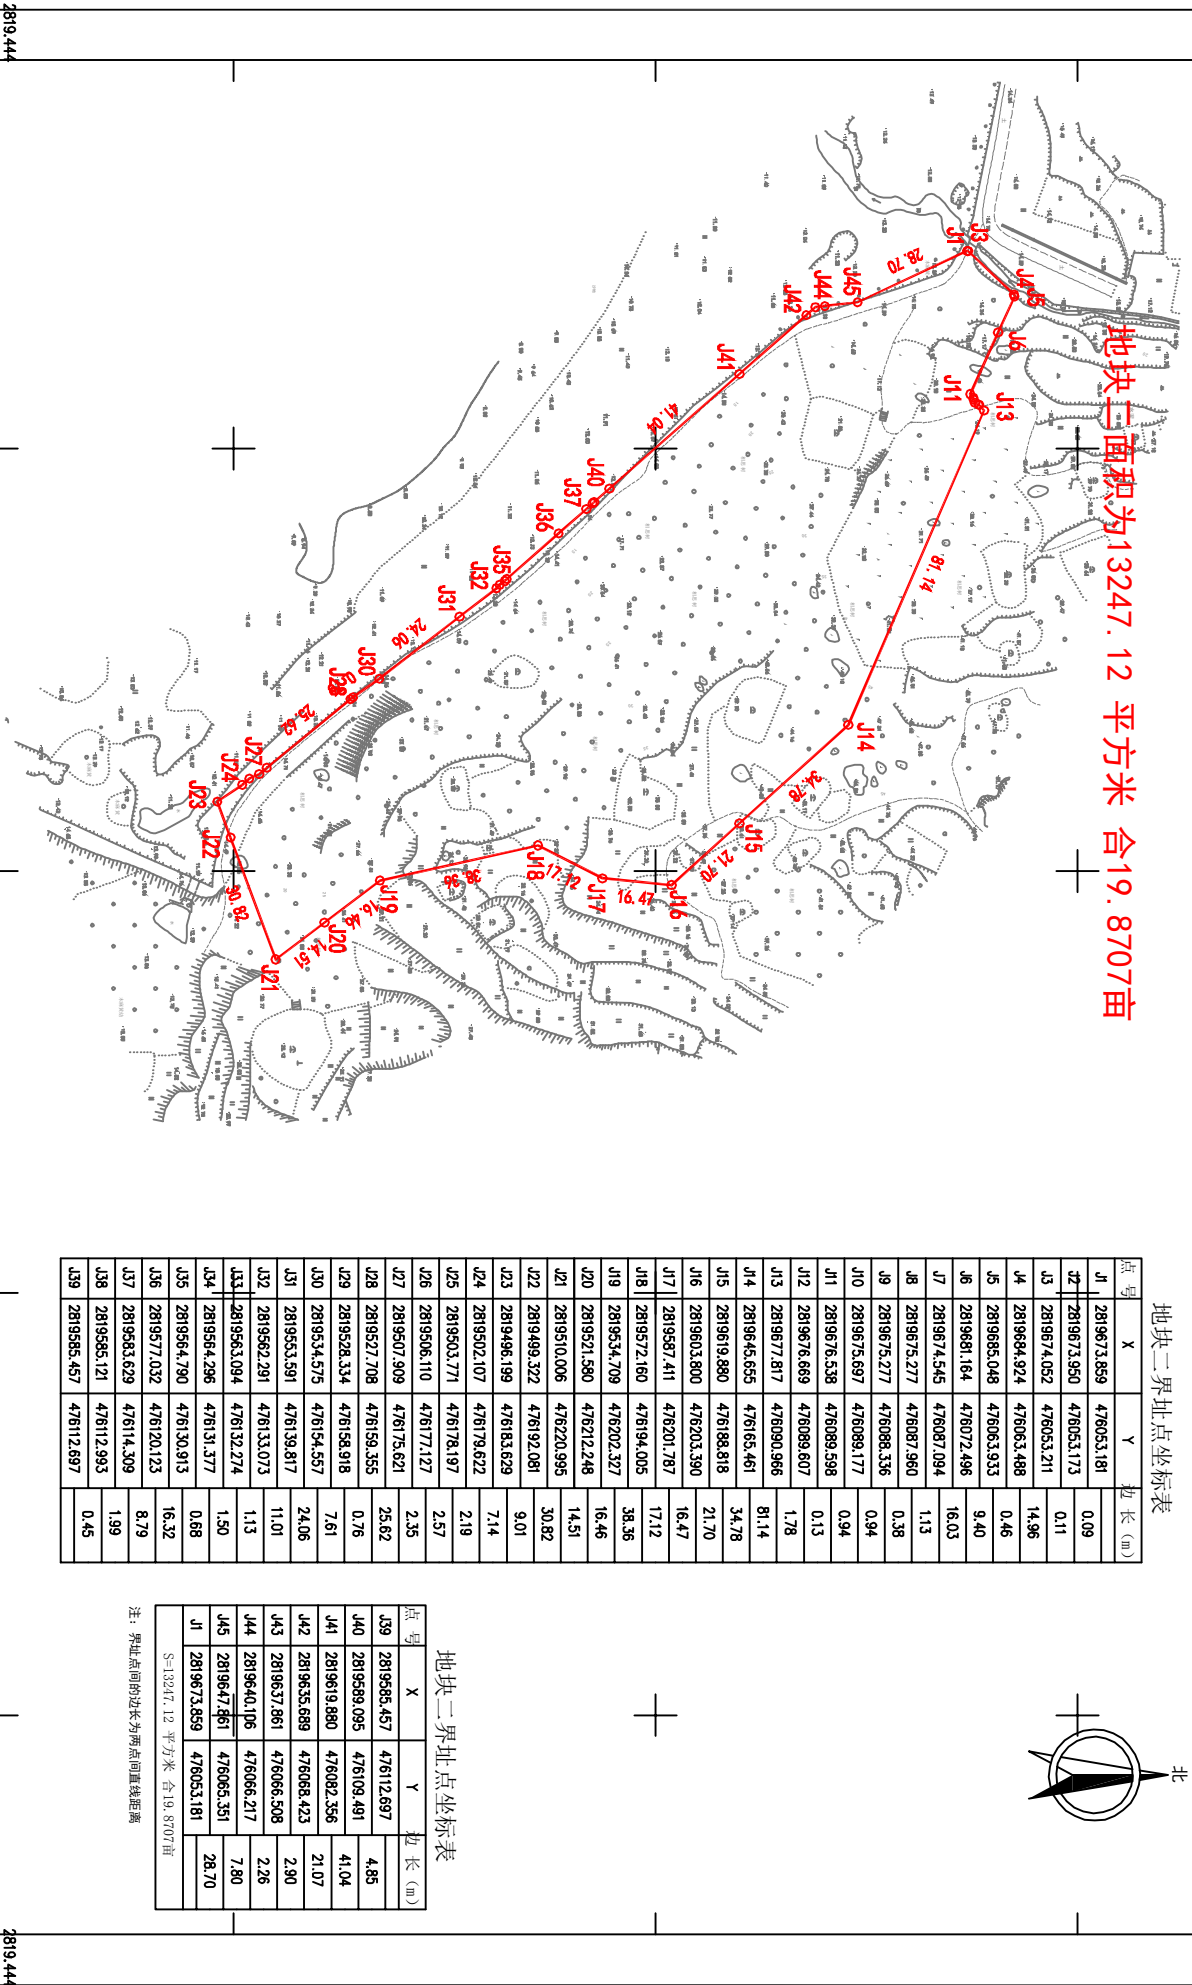

地块二界址点坐标表

点号	X	Y	边长 (m)
J1	2819673.859	476053.181	0.09
J2	2819673.950	476053.173	0.11
J3	2819674.052	476053.211	14.96
J4	2819684.924	476063.488	0.46
J5	2819685.048	476063.933	9.40
J6	2819681.164	476072.496	16.03
J7	2819674.545	476087.094	1.13
J8	2819675.277	476087.960	0.38
J9	2819675.277	476088.336	0.94
J10	2819675.697	476088.177	0.94
J11	2819676.538	476089.598	0.13
J12	2819676.669	476089.607	1.78
J13	2819677.817	476090.966	81.14
J14	2819645.655	476165.461	34.78
J15	2819619.880	476188.818	21.70
J16	2819603.800	476203.390	16.47
J17	2819587.411	476201.787	17.12
J18	2819572.160	476194.005	38.36
J19	2819534.709	476202.327	16.46
J20	2819521.580	476212.248	14.51
J21	2819510.006	476220.995	30.82
J22	2819489.322	476192.081	9.01
J23	2819498.199	476183.629	7.14
J24	2819502.107	476179.622	2.19
J25	2819503.771	476178.197	2.57
J26	2819506.110	476177.127	2.35
J27	2819507.909	476175.621	25.62
J28	2819527.708	476159.355	0.76
J29	2819528.334	476158.918	7.61
J30	2819534.575	476154.557	24.06
J31	2819553.391	476139.817	11.01
J32	2819562.291	476133.073	1.13
J33	2819563.094	476132.274	1.50
J34	2819564.296	476131.377	0.68
J35	2819564.790	476130.913	16.32
J36	2819577.032	476120.123	8.79
J37	2819583.629	476114.309	1.99
J38	2819585.121	476112.993	0.45
J39	2819585.457	476112.697	

地块二界址点坐标表

点号	X	Y	边长 (m)
J39	2819585.457	476112.697	4.85
J40	2819589.095	476109.491	41.04
J41	2819619.880	476092.356	21.07
J42	2819635.689	476088.423	2.90
J43	2819637.861	476086.508	2.26
J44	2819640.106	476086.217	7.80
J45	2819647.861	476065.351	28.70
J1	2819673.859	476053.181	

注：界址点间的边长为两点间直线距离

测绘单位：福州市勘测院平潭分院

2010年7月数字化成图
2000国家大地坐标系
1985国家高程基准
2009年福州市勘测院地形图盖章，方为正式材料

476.008
2819.444

476.452
2819.444

1:1000

476.008 2819.444