


万顺路(海霞东路-龙凤路)选址红线图

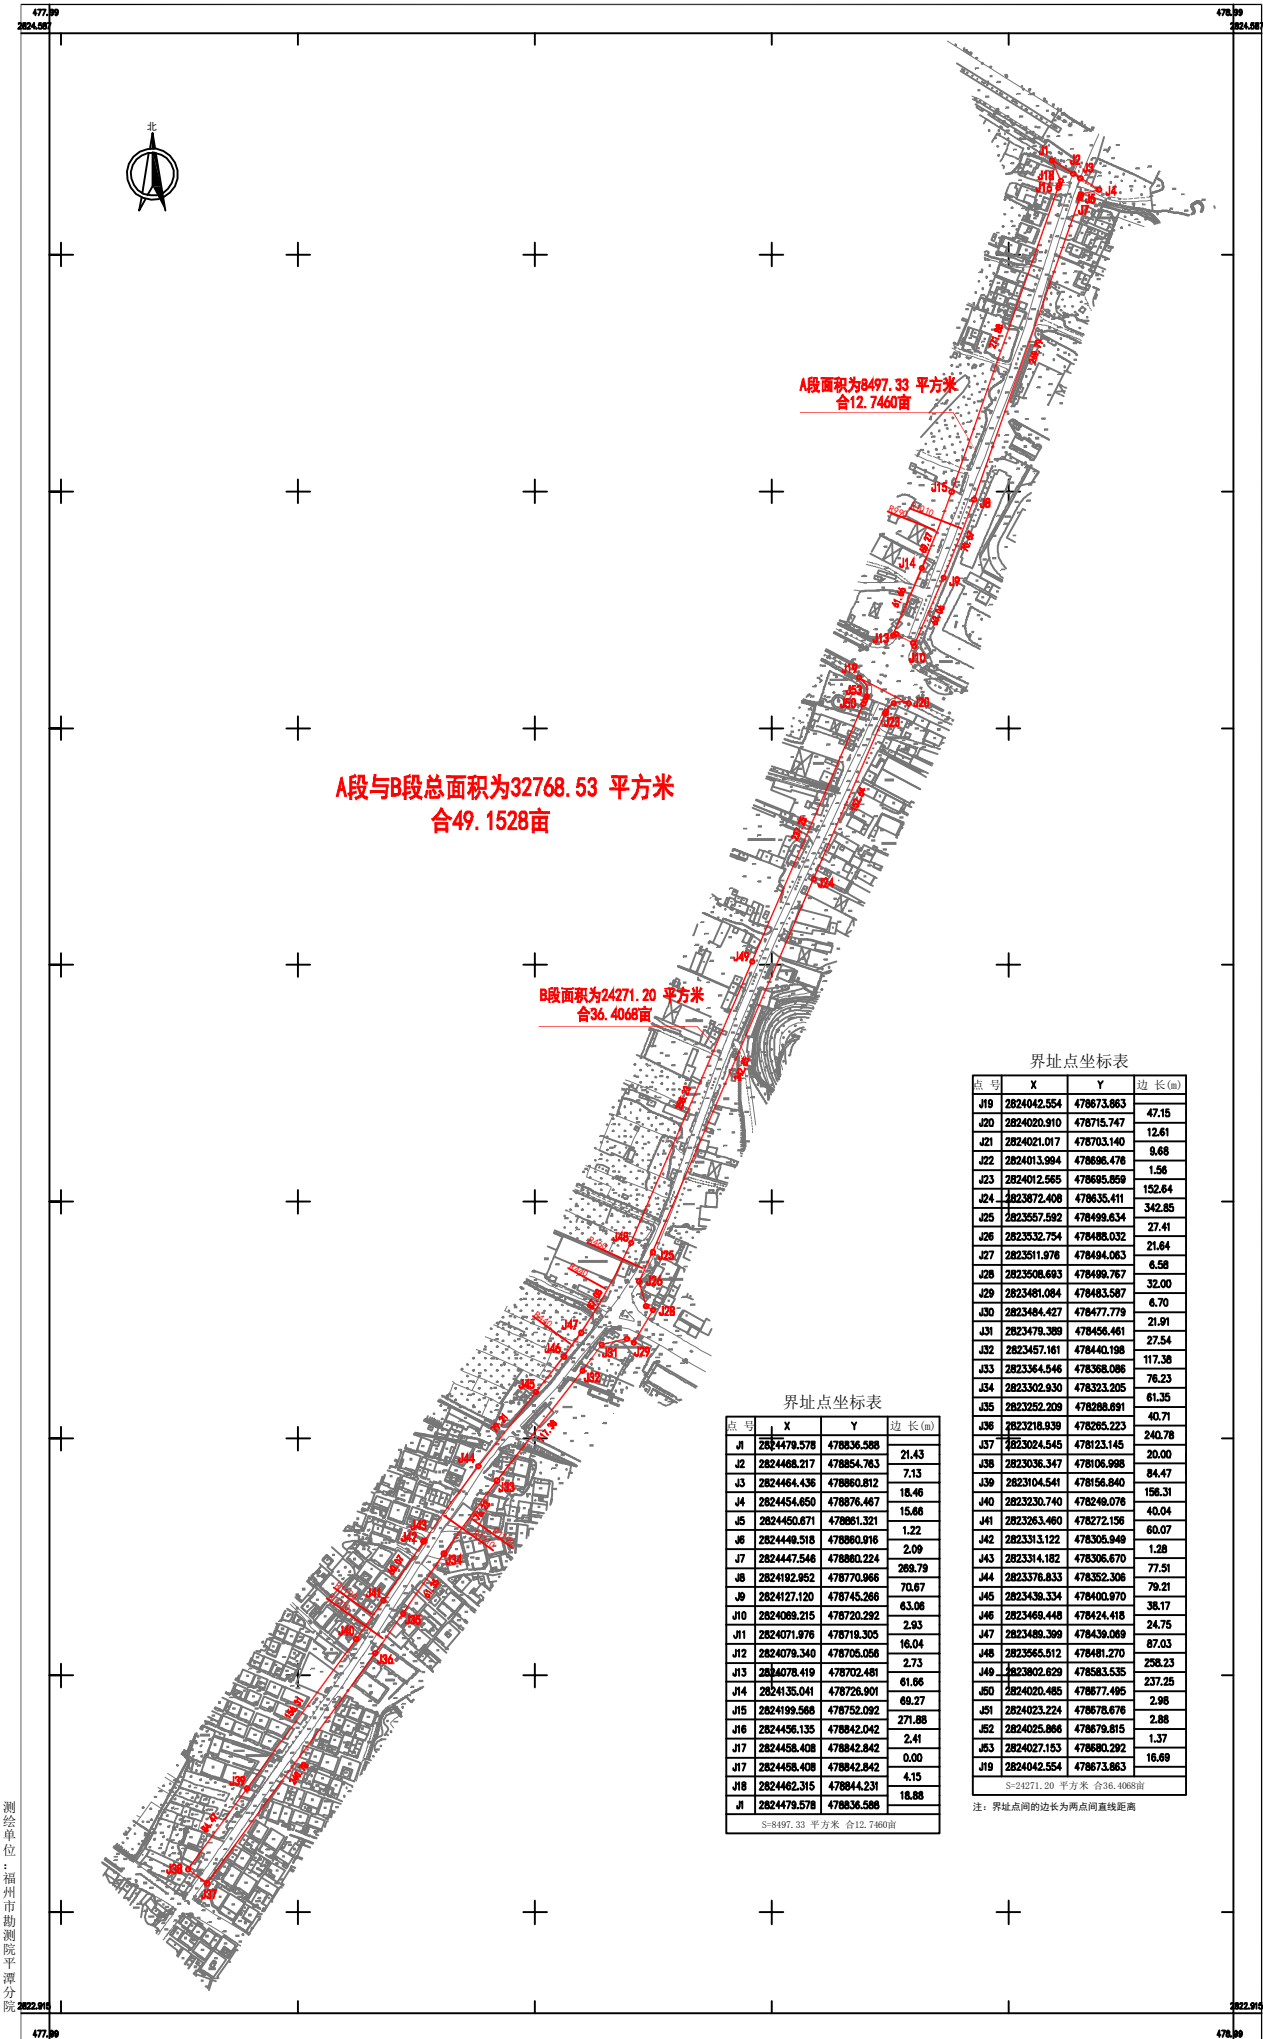

A段与B段总面积为32768.53 平方米
合49.1528亩

A段面积为8497.33 平方米
合12.7460亩

B段面积为24271.20 平方米
合36.4068亩

界址点坐标表

点号	X	Y	边长(m)
J19	2824042.554	478673.863	47.15
J20	2824020.910	478715.747	12.61
J21	2824021.017	478703.140	8.68
J22	2824013.994	478696.478	1.56
J23	2824012.565	478695.859	152.64
J24	2823872.408	478635.411	342.85
J25	2823557.592	478499.634	27.41
J26	2823532.754	478488.032	21.64
J27	2823511.976	478494.063	6.58
J28	2823508.693	478499.767	32.00
J29	2823461.084	478483.587	6.70
J30	2823484.427	478477.779	21.91
J31	2823479.399	478456.461	27.54
J32	2823457.161	478440.198	117.36
J33	2823364.546	478368.086	76.23
J34	2823302.930	478323.205	61.35
J35	2823252.209	478288.891	40.71
J36	2823218.939	478265.223	240.78
J37	2823024.545	478123.145	20.00
J38	2823036.347	478106.998	84.47
J39	2823104.541	478156.840	156.31
J40	2823230.740	478249.078	40.04
J41	2823263.460	478272.156	60.07
J42	2823313.122	478305.949	1.28
J43	2823314.182	478306.670	77.51
J44	2823376.833	478352.308	79.21
J45	2823438.334	478400.970	38.17
J46	2823469.448	478424.418	24.75
J47	2823489.399	478439.069	87.03
J48	2823565.012	478481.270	258.23
J49	2823802.629	478583.535	237.25
J50	2824020.485	478677.495	2.96
J51	2824023.224	478678.676	2.88
J52	2824025.866	478679.815	1.37
J53	2824027.153	478680.292	16.69
J19	2824042.554	478673.863	

S=24271.20 平方米 合36.4068亩
注：界址点间的边长为两点间直线距离

界址点坐标表

点号	X	Y	边长(m)
J1	2824478.578	478836.588	21.43
J2	2824468.217	478854.763	7.13
J3	2824464.436	478860.812	18.46
J4	2824454.650	478876.467	15.68
J5	2824450.671	478881.321	1.22
J6	2824448.518	478880.916	2.09
J7	2824447.546	478880.224	269.79
J8	2824192.952	478770.966	70.67
J9	2824127.120	478745.266	63.06
J10	2824069.215	478720.292	2.83
J11	2824071.976	478719.305	16.04
J12	2824078.340	478705.056	2.73
J13	2824078.419	478702.481	61.66
J14	2824135.041	478726.901	68.27
J15	2824199.568	478752.092	271.88
J16	2824456.135	478842.042	2.41
J17	2824458.408	478842.842	0.00
J18	2824462.315	478844.231	4.15
J1	2824478.578	478836.588	18.88

S=8497.33 平方米 合12.7460亩

测绘单位：福州市勘测院平潭分院