


正旺路（翠园北路-环岛东路）选址红线图

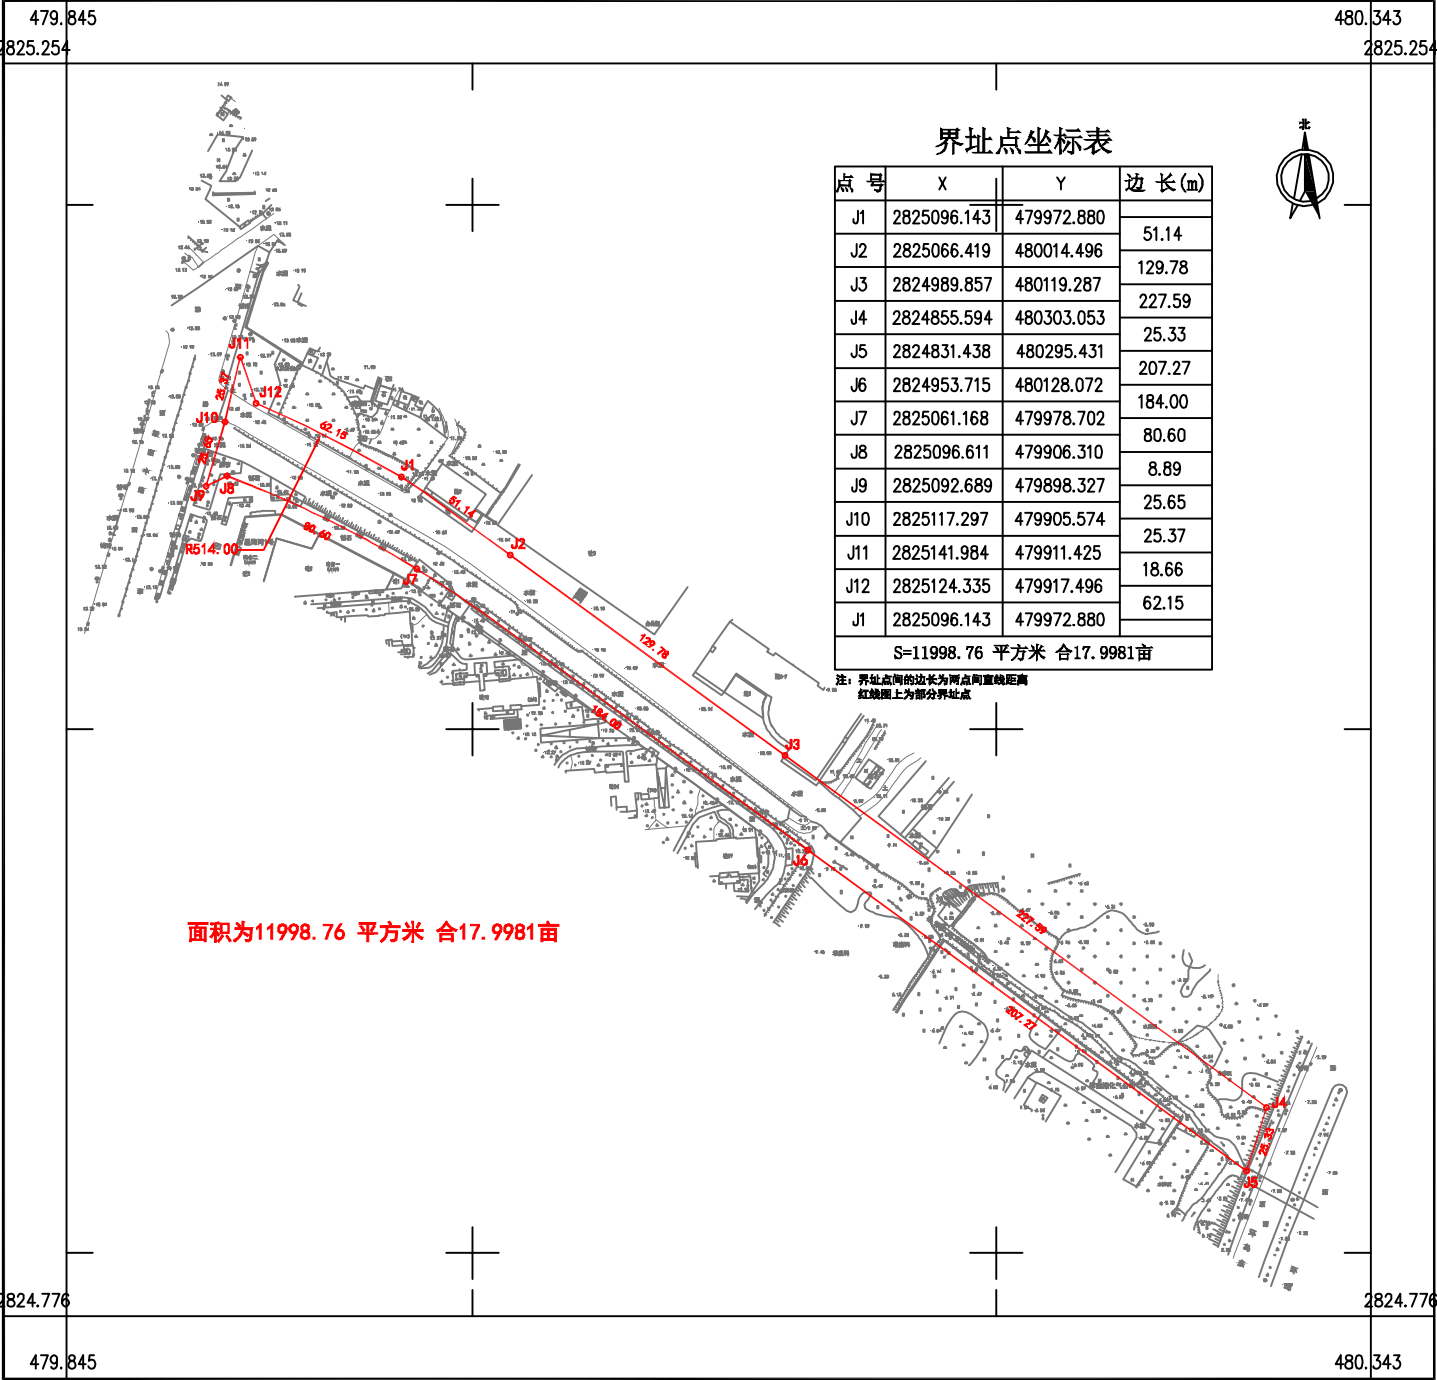

测绘单位：福州市勘测院平潭分院

2010年7月数字化成图
2000国家大地坐标系
1985国家高程基准
2009年福州基础地理信息数据图式
加盖福州市勘测院地形图印章 方为正式材料

1:2000