


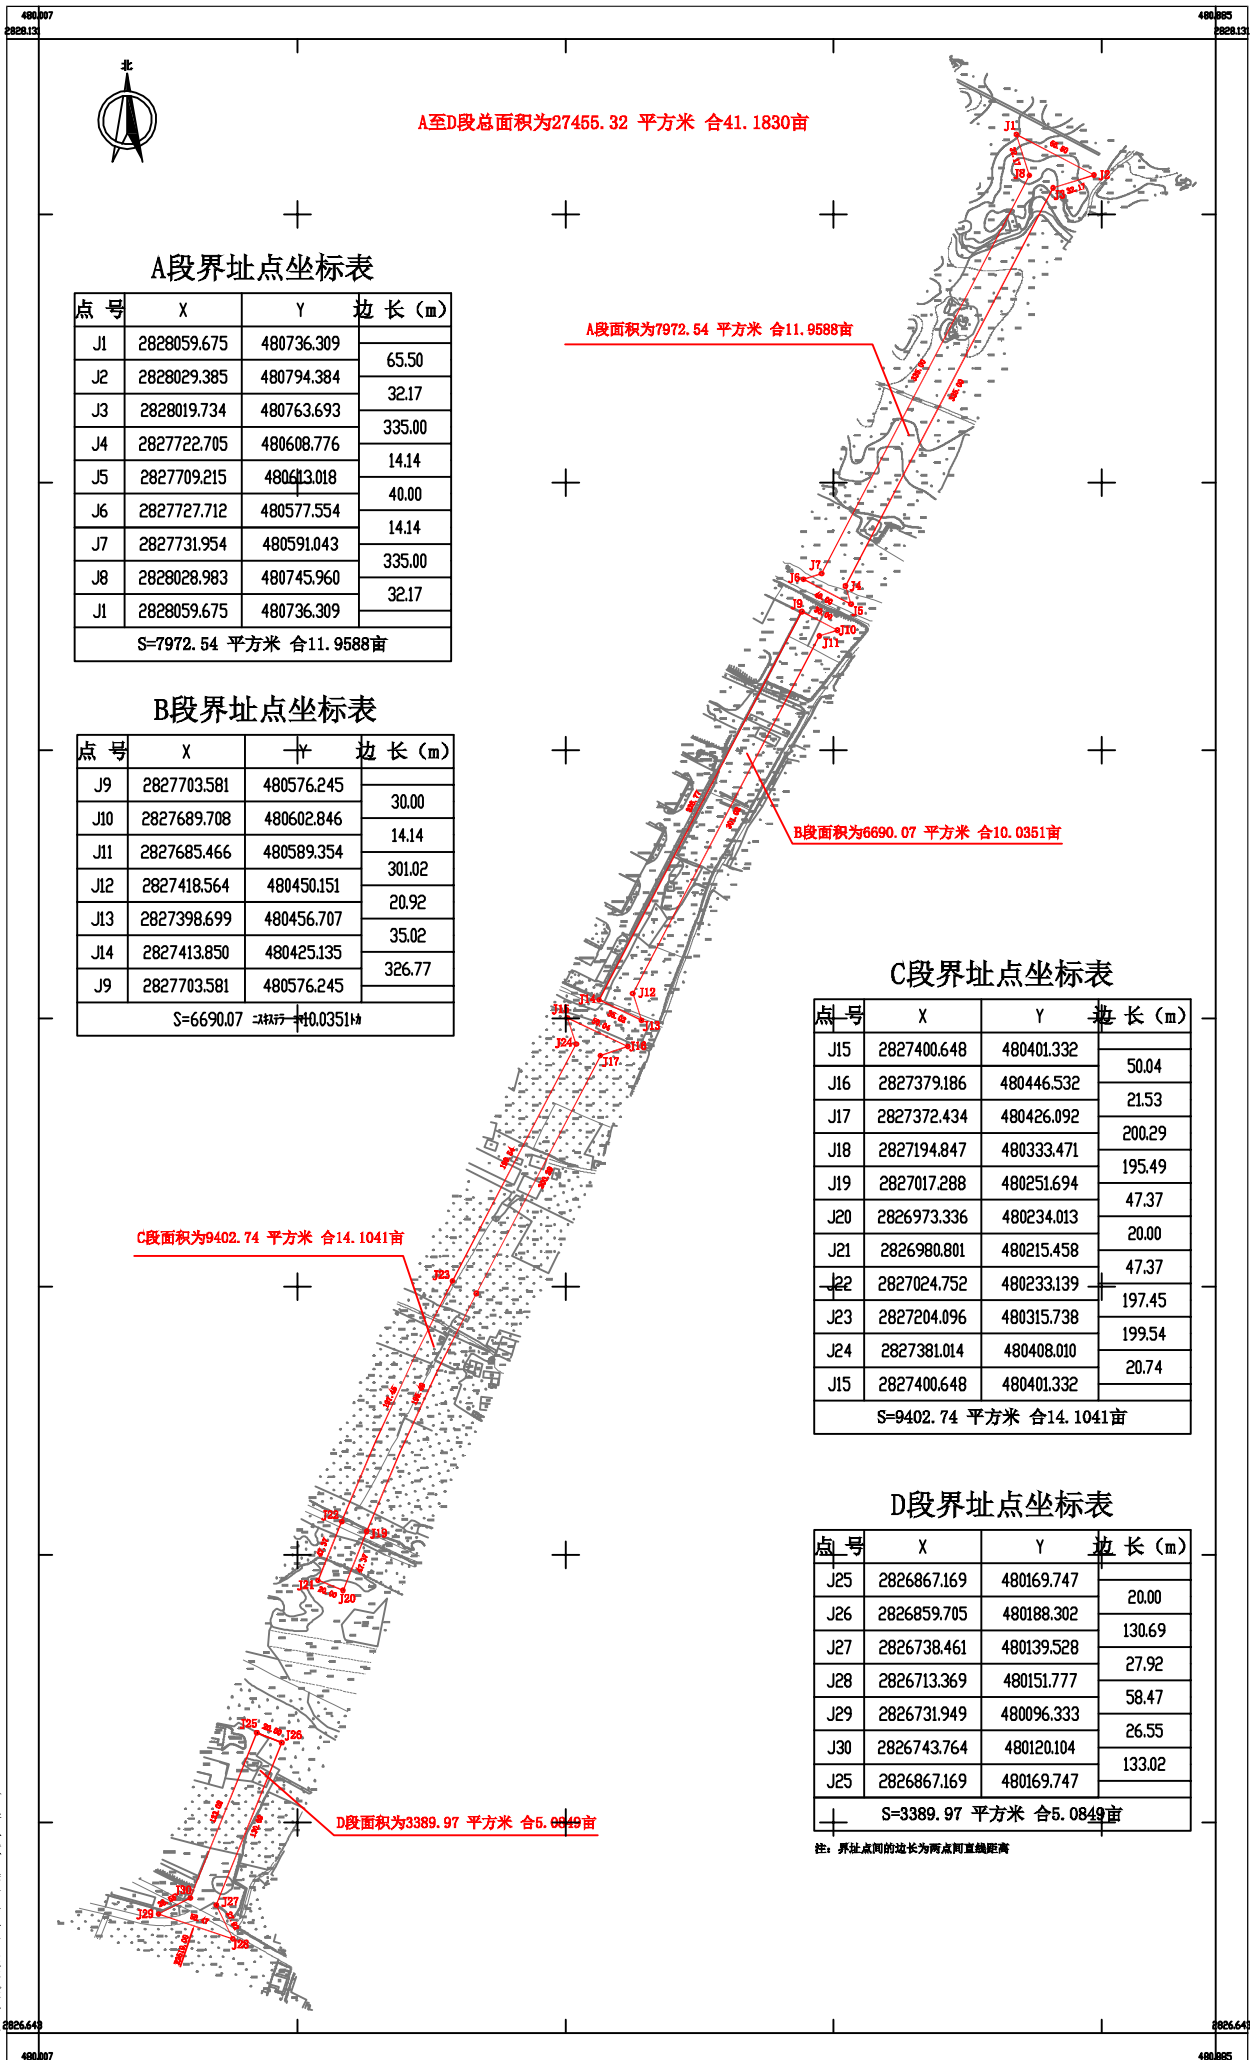

A段界址点坐标表

点号	X	Y	边长 (m)
J1	2828059.675	480736.309	65.50
J2	2828029.385	480794.384	32.17
J3	2828019.734	480763.693	335.00
J4	2827722.705	480608.776	14.14
J5	2827709.215	480613.018	40.00
J6	2827727.712	480577.554	14.14
J7	2827731.954	480591.043	335.00
J8	2828028.983	480745.960	32.17
J1	2828059.675	480736.309	
S=7972.54 平方米 合11.9588亩			

B段界址点坐标表

点号	X	Y	边长 (m)
J9	2827703.581	480576.245	30.00
J10	2827689.708	480602.846	14.14
J11	2827685.466	480589.354	301.02
J12	2827418.564	480450.151	20.92
J13	2827398.699	480456.707	35.02
J14	2827413.850	480425.135	326.77
J9	2827703.581	480576.245	
S=6690.07 平方米 合10.0351亩			

C段界址点坐标表

点号	X	Y	边长 (m)
J15	2827400.648	480401.332	50.04
J16	2827379.186	480446.532	21.53
J17	2827372.434	480426.092	200.29
J18	2827194.847	480333.471	195.49
J19	2827017.288	480251.694	47.37
J20	2826973.336	480234.013	20.00
J21	2826980.801	480215.458	47.37
J22	2827024.752	480233.139	197.45
J23	2827204.096	480315.738	199.54
J24	2827381.014	480408.010	20.74
J15	2827400.648	480401.332	
S=9402.74 平方米 合14.1041亩			

D段界址点坐标表

点号	X	Y	边长 (m)
J25	2826867.169	480169.747	20.00
J26	2826859.705	480188.302	130.69
J27	2826738.461	480139.528	27.92
J28	2826713.369	480151.777	58.47
J29	2826731.949	480096.333	26.55
J30	2826743.764	480120.104	133.02
J25	2826867.169	480169.747	
S=3389.97 平方米 合5.0849亩			

注：界址点间的边长为两点间直线距离