岚城二路（中山大道-滨河路）选址红线图

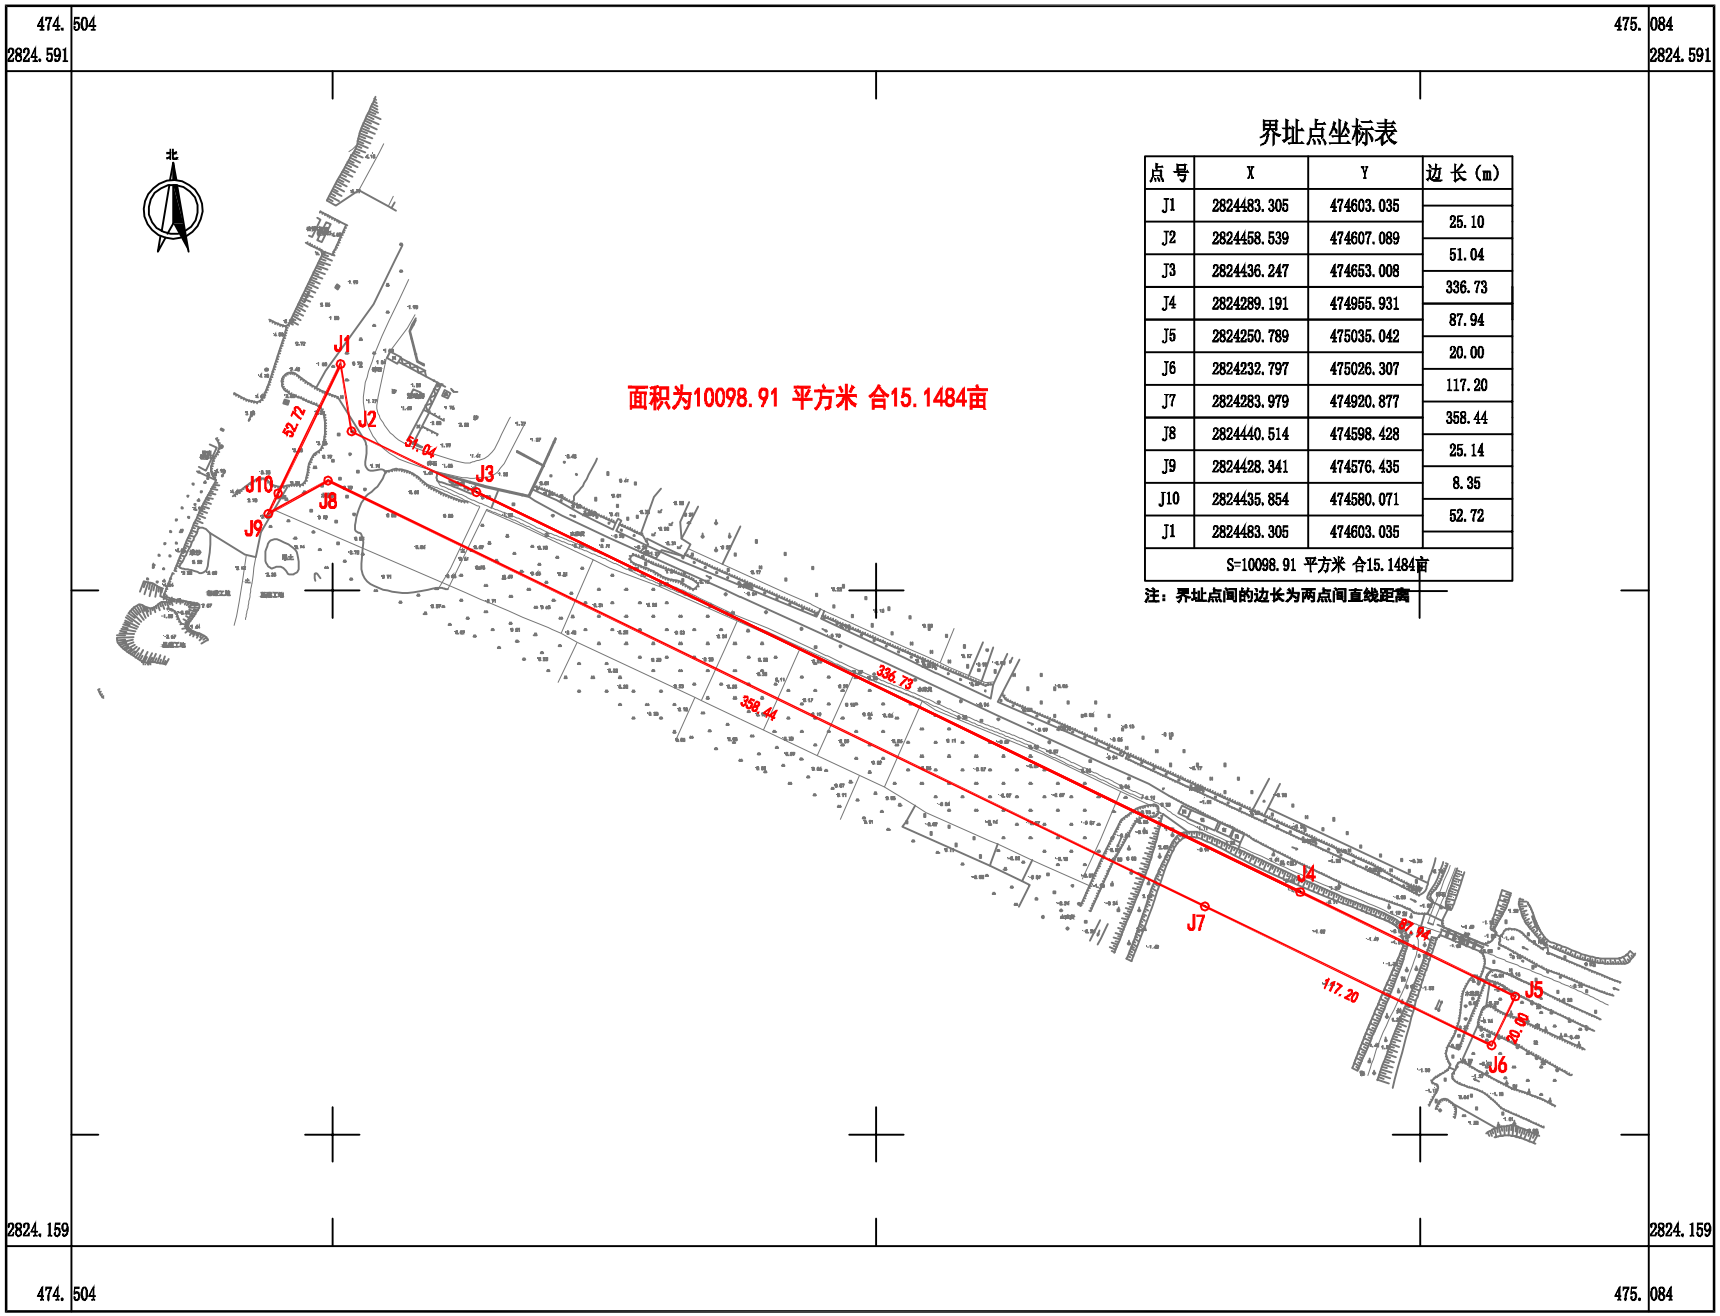

界址点坐标表

点 号	X	Y	边 长（m）
J1	2824483.305	474603.035	
J2	2824458.539	474607.089	25.10
J3	2824436.247	474653.008	51.04
J4	2824289.191	474955.931	336.73
J5	2824250.789	475035.042	87.94
J6	2824232.797	475026.307	20.00
J7	2824283.979	474920.877	117.20
J8	2824440.514	474598.428	358.44
J9	2824428.341	474576.435	25.14
J10	2824435.854	474580.071	8.35
J1	2824483.305	474603.035	52.72
S=10098.91 平方米 合15.1484亩			

注：界址点间的边长为两点间直线距离

测绘单位：福州市勘测院平潭分院

2020年5月全野外数字测量
2000国家大地坐标系
1985国家高程基准
2009年福州基础地理信息数据图式
加盖福州市勘测院地形图蓝章，方为正式材料

1:2000