


坛南湾田美澳公共广场扩建工程选址红线图

由 Autodesk 教育版产品制作

测绘单位：福州市勘测院平潭分院

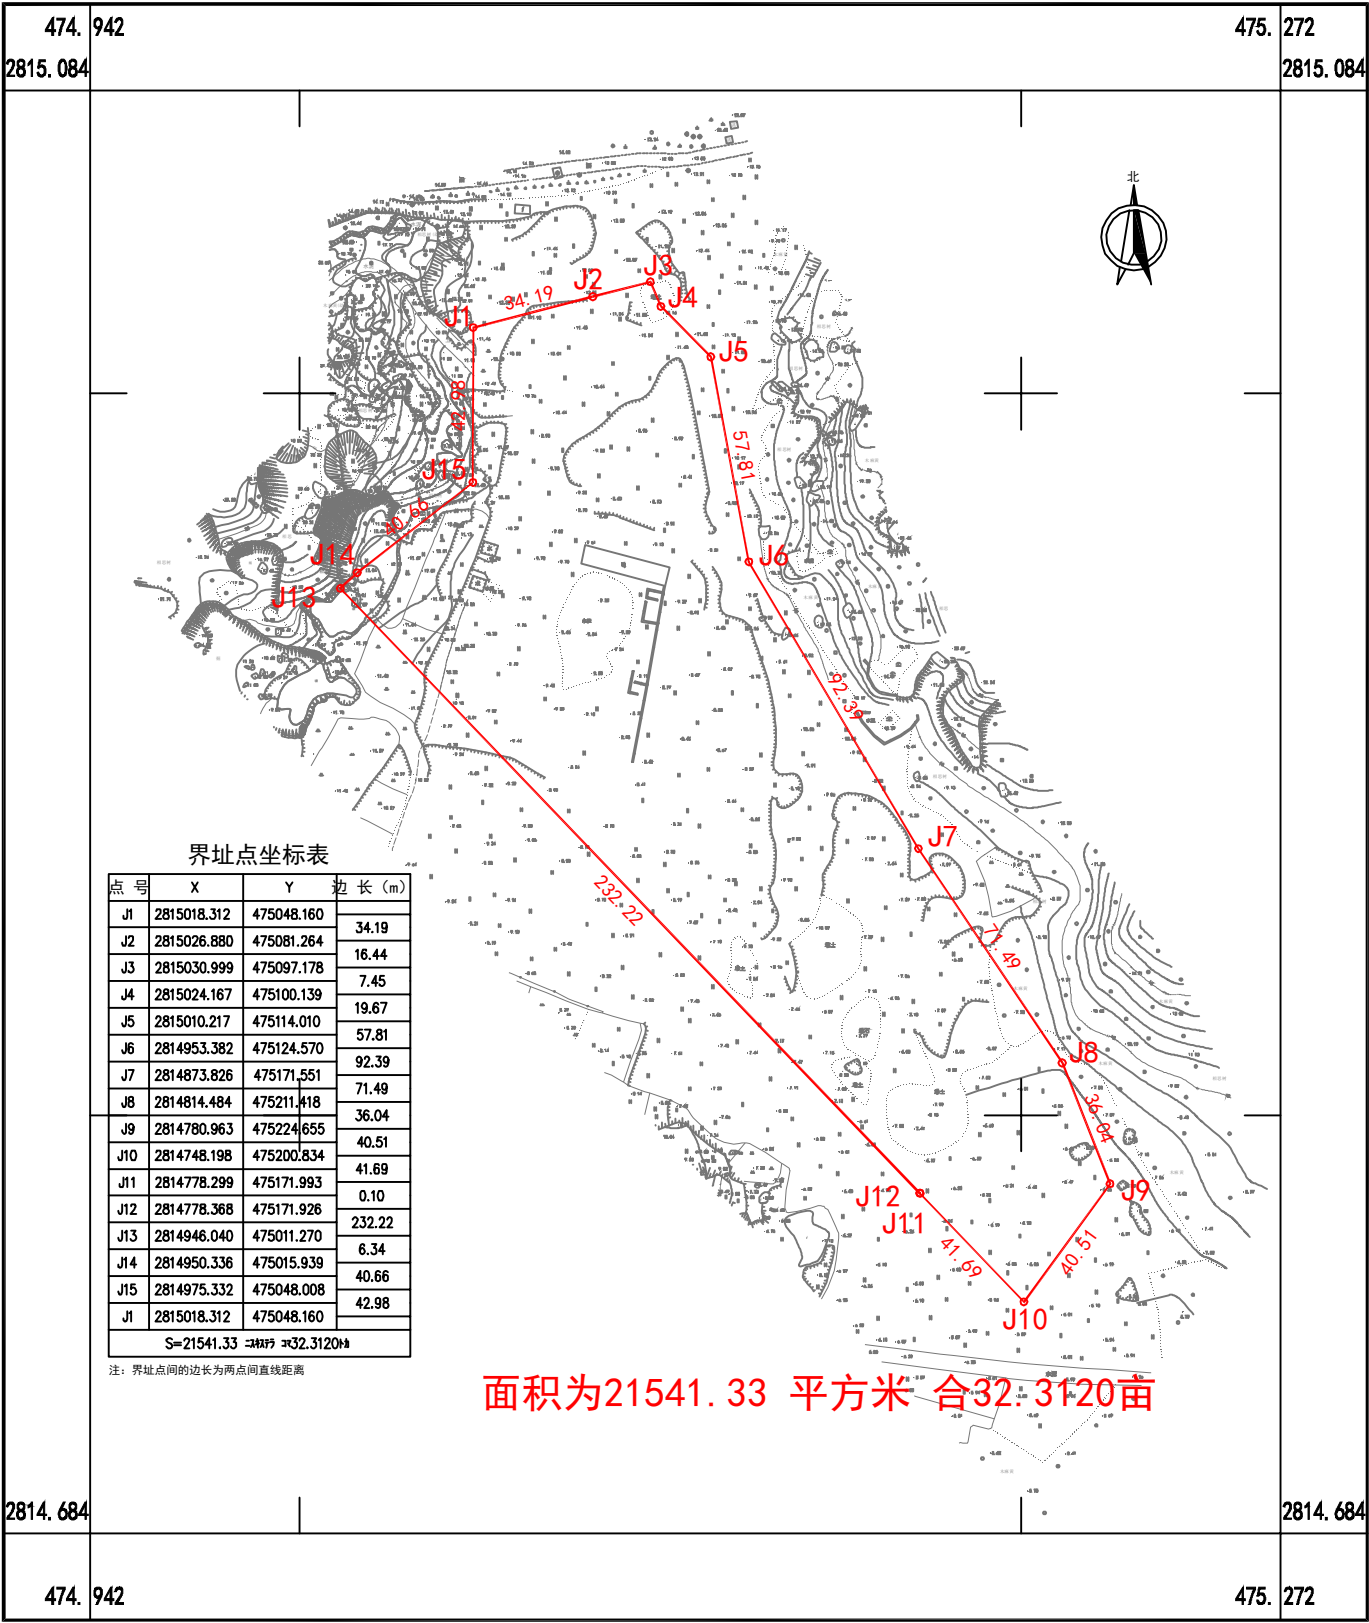

2010年7月数字化成图
2000国家大地坐标系
1985国家高程基准
2009年福州基础地理信息数据图式
加盖福州市勘测院地形图蓝章，方为正式材料

1:2000