


粮食园周边路网工程-松环路（山门路-翠园北路）用地红线图

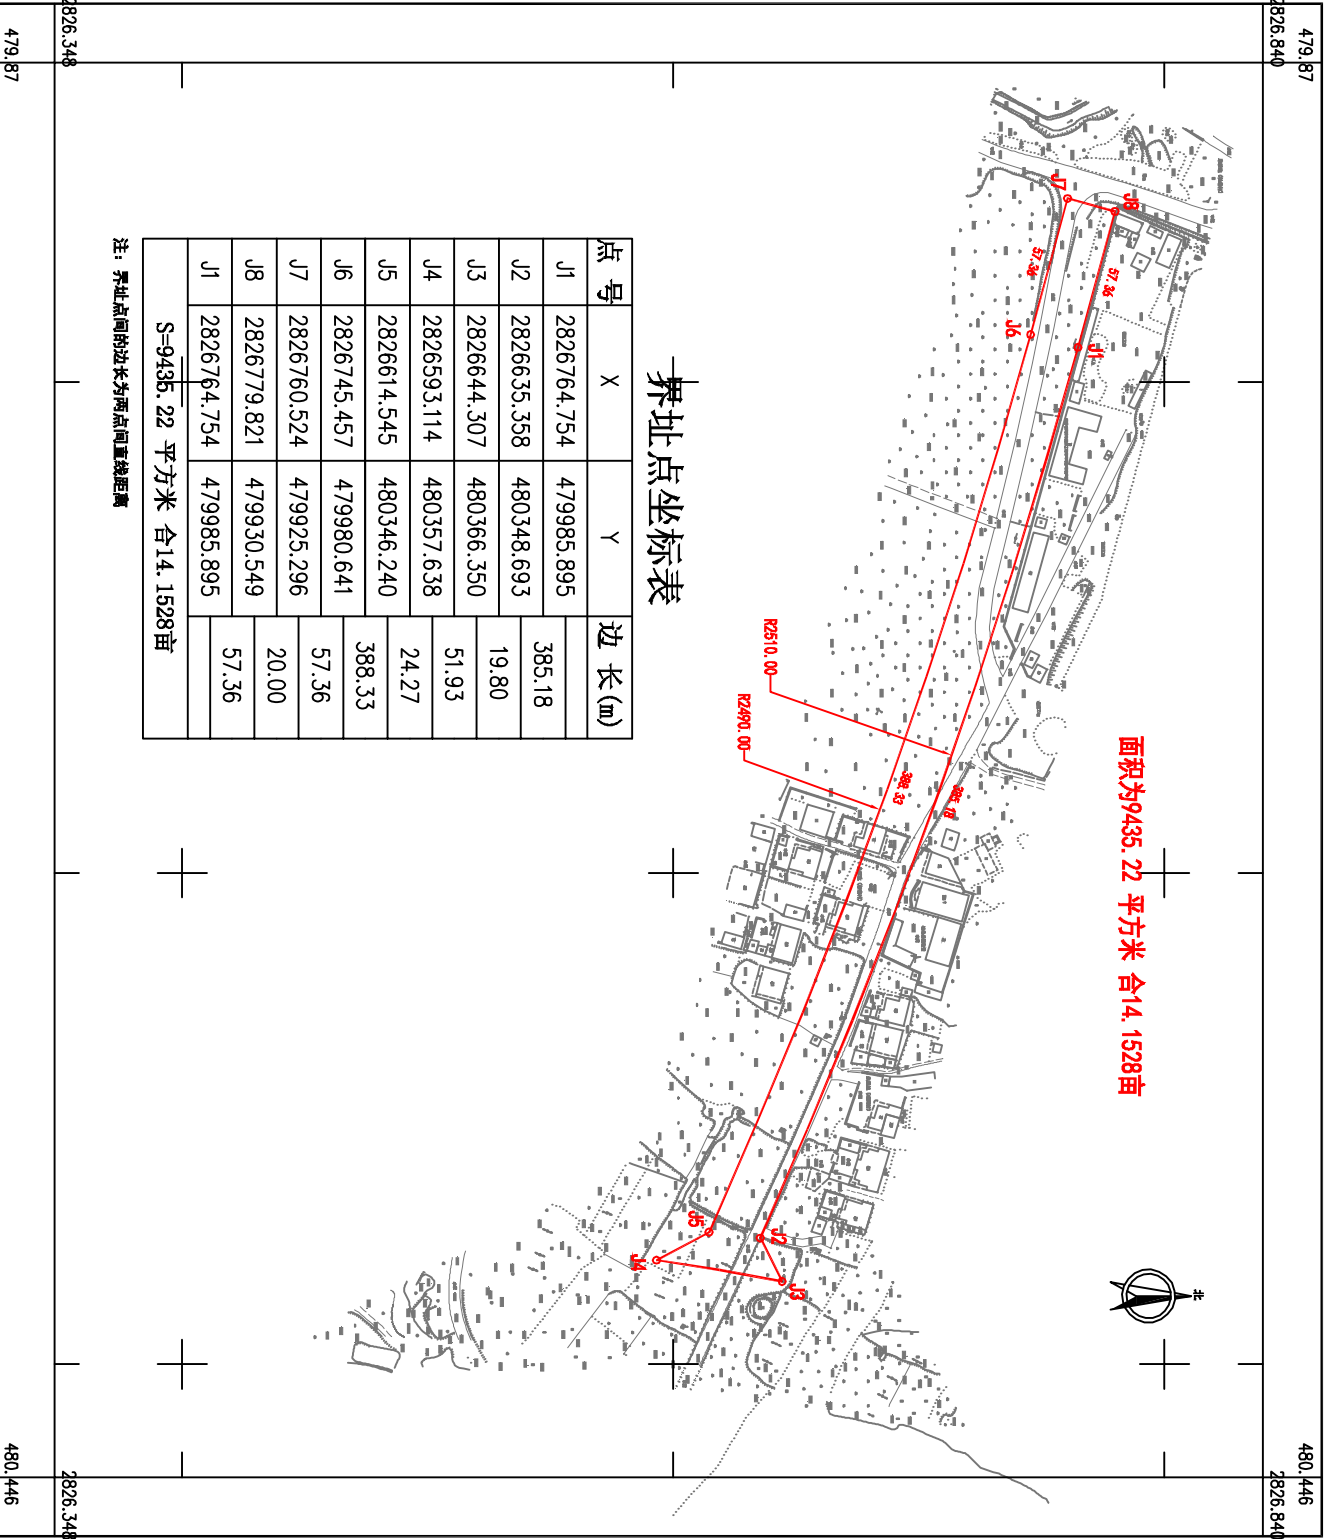

测绘单位：福州市勘测院分院

2018年6月全野外数字测量
2000国家大地坐标系
1985国家高程基准
2009年福州基础地理信息数据图式
加盖福州市勘测院地形图盖章，方为正式材料

1:2000