


西部生态廊道（二期）附属设施配套工程选址红线图（一）

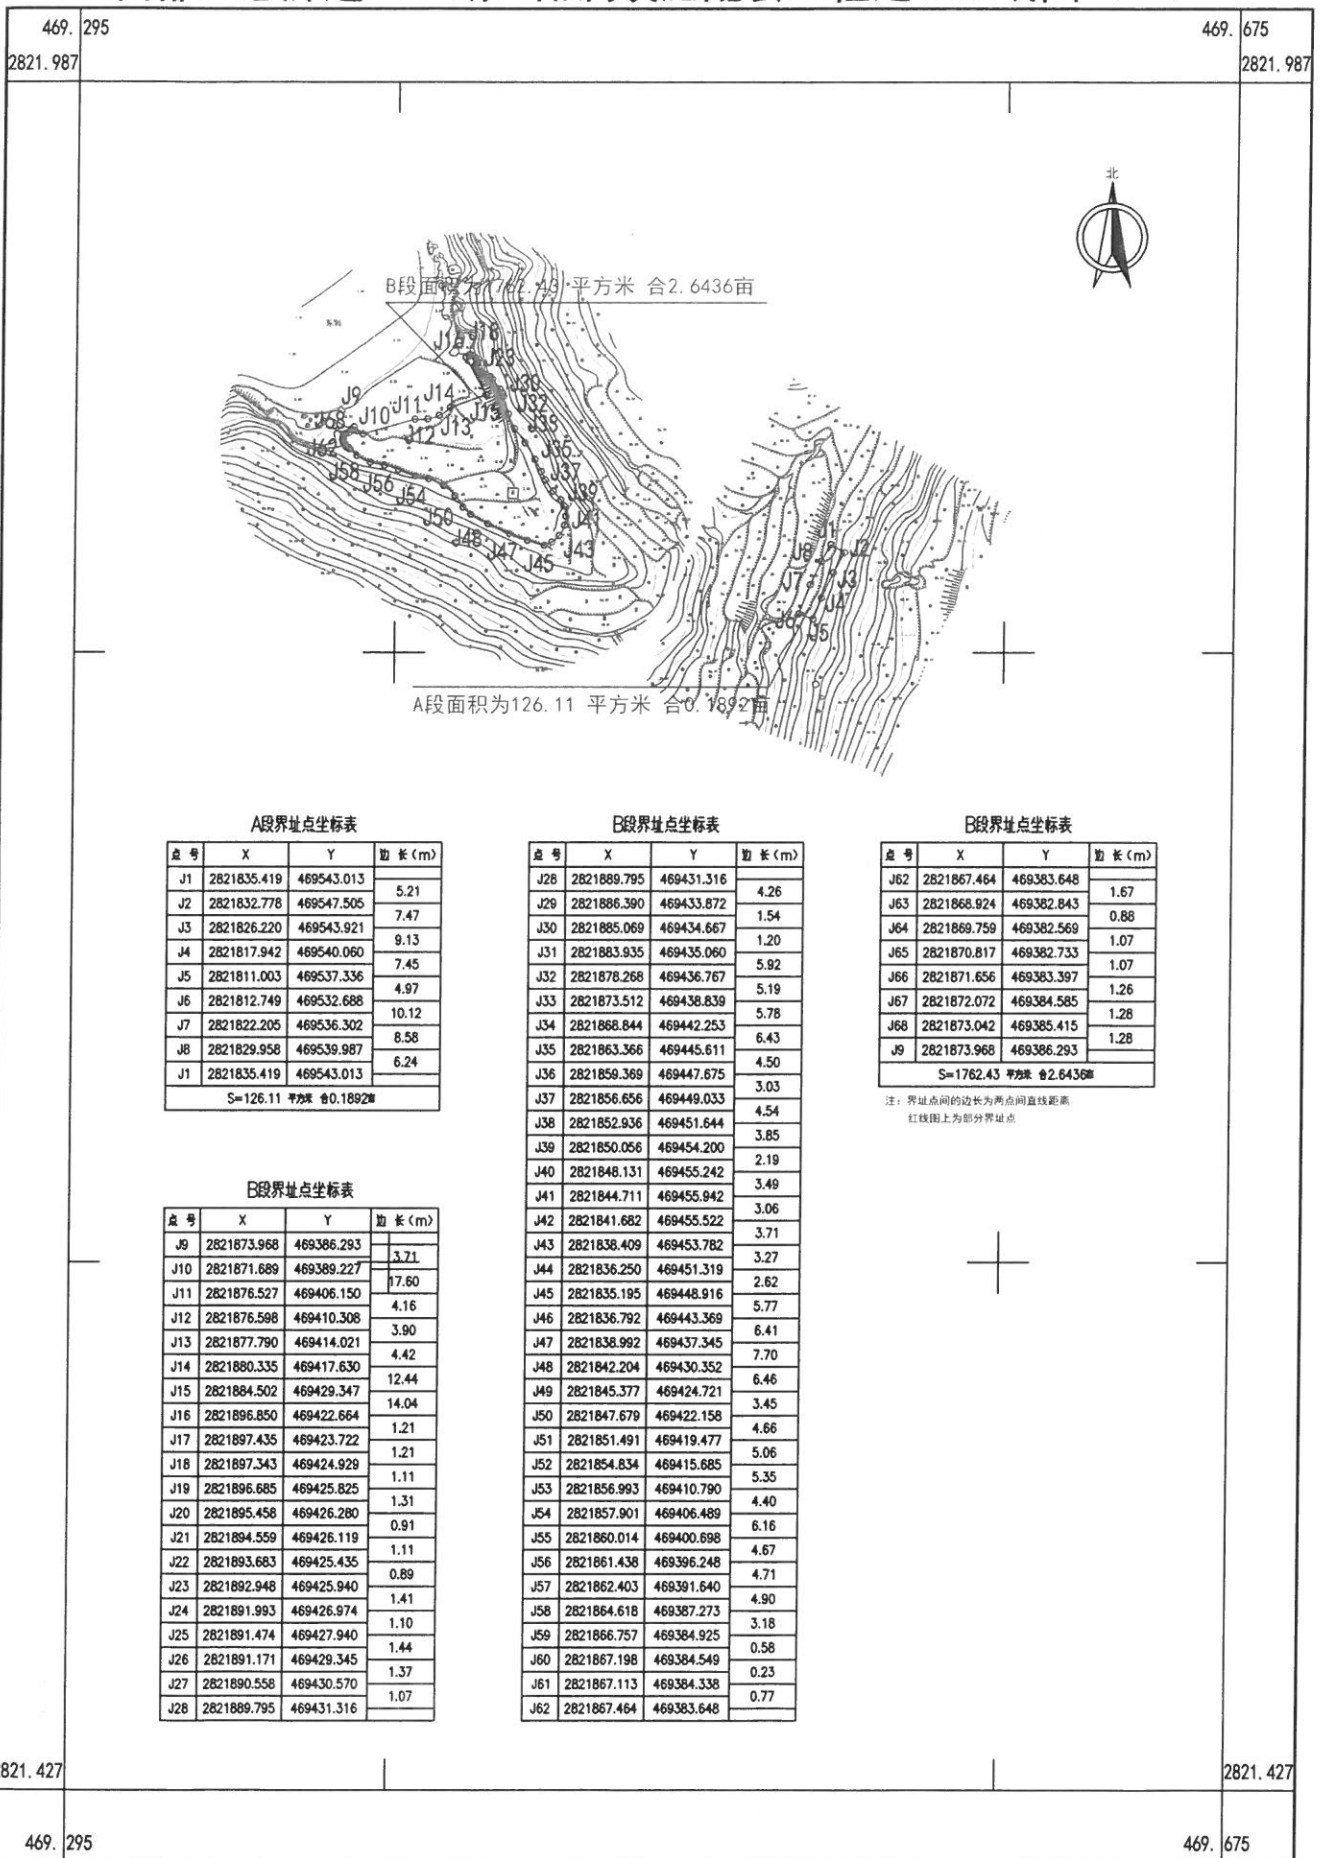


由 Autodesk 教育版产品制作

测绘单位：福州市勘测院平潭分院

由 Autodesk 教育版产品制作

测绘单位：福州市勘测院平潭分院

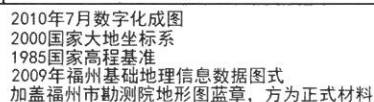

西部生态廊道（二期）附属设施配套工程选址红线图（三）

由 Autodesk 教育版产品制作

由 Autodesk 教育版产品制作



D段界址点坐标表				
点号	X	Y	距离(m)	
J04	282137.343	467514.975	6.90	
J05	282137.219	467521.818	1.81	
J06	282137.024	467522.048	5.33	
J07	282137.101	467527.338	3.23	
J08	282137.188	467530.569	3.23	
J09	282137.025	467533.754	2.94	
J10	282136.572	467536.498	3.54	
J11	282136.760	467539.485	3.67	
J12	282136.157	467542.167	3.18	
J13	282136.327	467545.005	3.40	
J14	282136.356	467546.388	3.92	
J15	282136.302	467552.300	5.12	
J16	282136.129	467557.243	4.22	
J17	282136.766	467560.870	6.20	
J18	282136.540	467565.205	6.81	
J19	282134.577	467568.839	4.41	
J20	282135.594	467573.135	3.78	
J21	282135.102	467576.879	2.84	
J22	282134.836	467579.466	2.13	
J23	282134.615	467583.763	1.29	
J24	282134.752	467577.657	1.75	
J25	282134.801	467577.427	1.92	
J26	282134.303	467577.714	2.09	
J27	282134.026	467578.640	2.06	
J28	282134.538	467580.112	1.87	
J29	282133.487	467581.662	2.47	
J30	282133.722	467583.363	2.69	
J31	282133.368	467584.681	2.69	
J32	282133.747	467585.278	3.13	
J33	282132.624	467585.028	2.02	
J34	282132.727	467584.338	2.08	
J35	282132.675	467583.966	2.55	
J36	282132.323	467584.696	2.55	
J37	282132.140	467586.463	2.86	
J38	282132.071	467589.261	2.64	
J39	282132.127	467591.829	2.31	
J40	282132.322	467593.662	1.50	
J41	282132.563	467594.764	1.41	
J42	282132.048	467596.186	1.77	
J43	282132.863	467597.948	1.64	
J44	282133.001	467599.240	1.91	
J45	282132.374	467600.332		


D段界址点坐标表				
点号	X	Y	距离(m)	
J135	2821321.374	467800.332	1.56	
J136	2821319.825	467800.478	4.25	
J137	2821315.620	467809.842	2.29	
J138	2821313.427	467809.176	4.58	
J139	2821309.297	467807.197	4.25	
J140	2821305.892	467804.650	3.83	
J141	2821303.222	467801.771	2.93	
J142	2821301.600	467809.330	3.72	
J143	2821299.722	467806.127	4.34	
J144	2821296.778	467802.944	4.34	
J145	2821293.184	467800.217	5.87	
J146	2821287.811	467805.667	-10.31	
J147	2821277.765	467805.600	2.42	
J148	2821277.554	467803.192	10.82	
J149	2821288.122	467807.863	12.26	
J150	2821300.245	467809.000	11.39	
J151	2821311.801	467808.154	3.82	
J152	2821315.419	467807.961	2.39	
J153	2821317.745	467807.422	7.04	
J154	2821314.624	467801.111	4.19	
J155	2821318.807	467800.886	6.69	
J156	2821325.471	467801.508	2.08	
J157	2821327.180	467802.698	2.69	
J158	2821326.713	467800.045	2.80	
J159	2821327.119	467807.175	1.87	
J160	2821327.862	467805.461	3.65	
J161	2821325.173	467802.994	6.42	
J162	2821320.836	467807.722	2.20	
J163	2821318.642	467807.841	3.05	
J164	2821318.607	467806.886	4.19	
J165	2821318.449	467805.396	3.05	
J166	2821318.513	467805.444	1.22	
J167	2821318.729	467805.759	7.84	
J168	2821325.027	467806.603	-5.70	
J169	2821329.227	467805.456	5.38	
J170	2821333.321	467809.989	4.82	
J171	2821337.164	467807.426	1.46	
J172	2821338.337	467804.550	1.15	
J173	2821338.897	467804.545		

D段界址点坐标表				
点号	X	Y	距离(m)	
J174	2821338.897	467545.545	1.26	
J175	2821338.907	467544.284	1.30	
J176	2821338.577	467543.057	1.87	
J177	2821338.154	467541.239	2.24	
J178	2821338.235	467536.003	3.42	
J179	2821336.360	467536.139	2.79	
J180	2821336.636	467533.449	2.34	
J181	2821335.734	467531.106	6.79	
J182	2821338.241	467531.815	2.43	
J183	2821343.858	467527.999	1.62	
J184	2821345.778	467529.483	1.32	
J185	2821347.245	467531.417	1.82	
J186	2821347.919	467532.981	2.62	
J187	2821350.044	467533.809	1.87	
J188	2821351.579	467534.870	1.51	
J189	2821353.073	467535.183	1.43	
J190	2821354.341	467534.801	1.30	
J191	2821355.390	467533.927	3.22	
J192	2821357.117	467531.209	3.08	
J193	2821359.536	467529.307	3.08	
J194	2821362.555	467528.681	2.72	
J195	2821365.206	467529.302	1.51	
J196	2821366.643	467529.753	1.22	
J197	2821367.754	467529.237	1.63	
J198	2821368.220	467527.673	5.30	
J199	2821367.547	467522.416	2.19	
J200	2821365.375	467522.694	6.90	
J201	2821364.499	467515.850	6.90	
J204	2821371.343	467514.975		
S=2773.81 面积 4.16078				

G段界址点坐标表				
点号	X	Y	距离(m)	
J223	2821234.656	467512.371	2.15	
J224	2821235.918	467510.631	1.85	
J225	2821237.512	467509.702	1.69	
J226	2821238.185	467508.435	2.64	
J227	2821241.772	467508.963	3.06	
J228	2821244.503	467511.368	2.34	
J229	2821246.069	467513.101	1.27	
J230	2821248.493	467514.303	0.81	
J231	2821248.916	467514.998	0.81	
J232	2821247.597	467515.444	0.81	
J233	2821248.403	467515.558	0.72	
J234	2821249.099	467515.354	1.40	
J235	2821250.409	467514.853	1.31	
J236	2821251.720	467514.895	1.44	
J237	2821253.025	467515.507	1.31	
J238	2821253.896	467516.488	1.44	
J239	2821254.348	467517.857	1.17	
J240	2821254.672	467518.002	1.10	
J241	2821256.601	467518.721	0.77	
J242	2821256.001	467520.373	0.89	
J243	2821256.272	467521.223	0.89	
J244	2821256.316	467522.115	1.02	
J245	2821256.065	467523.107	1.02	
J246	2821255.573	467523.987	4.82	
J247	2821256.782	467527.581	2.00	
J248	2821259.291	467526.515	6.82	
J249	2821252.801	467531.277	3.93	
J250	2821253.662	467535.062	1.41	
J251	2821255.058	467534.847	1.41	
J252	2821256.461	467535.017	0.53	
J253	2821256.866	467535.062	0.63	
J254	2821257.583	467534.866	0.82	
J255	2821258.333	467534.524	1.19	
J256	2821258.506	467534.360	1.45	
J257	2821260.921	467534.675	1.96	
J258	2821262.440	467535.918	1.92	
J259	2821263.159	467537.703	2.17	
J260	2821263.025	467538.872	2.51	
J261	2821261.890	467542.067	2.25	
J262	2821260.034	467543.589	2.25	
J263	2821258.072	467544.869	2.25	
J264	2821255.909	467545.308	2.25	
J265	2821253.662	467545.412	1.81	
J266	2821251.919	467544.921	0.20	
J267	2821251.884	467545.118	0.87	
J268	2821251.021	467545.010	1.12	
J269	2821250.041	467545.559	1.23	
J270	2821249.363	467546.591	0.68	
J271	2821249.234	467547.257	0.33	
J272	2821249.209	467547.581	0.33	
J273	2821249.546	467547.798	0.28	
J274	2821249.820	467547.836	0.28	
J275	2821250.073	467547.727	0.28	
J276	2821249.872	467547.544	0.72	
J277	2821250.652	467547.323	1.02	
J278	2821251.672	467547.372	1.22	
J279	2821252.722	467547.937	1.56	
J280	2821253.566	467549.338	1.44	
J281	2821253.980	467550.724	1.76	
J282	2821253.919	467552.461	1.14	
J283	2821253.541	467553.556	1.77	
J284	2821252.643	467555.080	3.28	
J285	2821250.493	467557.553	2.77	
J286	2821248.261	467558.202	2.27	
J287	2821246.220	467560.197	1.52	
J288	2821244.780	467560.688	0.20	
J289	2821244.728	467560.475	0.85	
J290	2821243.830	467560.775	1.02	
J291	2821243.052	467561.301	1.02	
J292	2821242.295	467561.988	1.02	
J293	2821241.687	467562.811	0.85	
J294	2821241.312	467563.578	2.40	
J295	2821238.526	467565.181	1.58	
J296	2821238.473	467564.008	1.89	
J297	2821237.115	467565.324	2.31	
J298	2821235.142	467566.526	3.14	
J299	2821232.103	467567.326	2.00	
J300	2821230.104	467567.438	1.63	
J301	2821228.539	467568.978	2.59	
J302	2821226.564	467569.382	2.59	
J303	2821225.674	467569.868	1.79	
J304	2821225.827	467569.083	1.99	
J305	2821225.802	467569.083	2.07	
J306	2821226.284	467569.071		

G段界址点坐标表				
点号	X	Y	边长(m)	
06	2821226.284	467557.071	0.66	
07	2821226.220	467556.408	0.75	
08	2821225.805	467555.790	0.83	
09	2821225.041	467555.477	1.96	
10	2821223.142	467554.983	1.80	
11	2821221.880	467553.932	3.23	
12	2821220.274	467551.020	3.86	
13	2821220.786	467547.162	3.52	
14	2821222.666	467544.190	2.85	
15	2821225.061	467542.844	1.42	
16	2821225.601	467541.330	1.08	
17	2821225.283	467540.299	1.18	
18	2821224.704	467536.277	1.62	
19	2821224.533	467537.657	1.78	
20	2821222.872	467537.332	0.77	
21	2821221.129	467536.982	0.24	
22	2821220.896	467537.056	0.32	
23	2821220.779	467537.356	0.77	
24	2821221.135	467536.033	1.02	
25	2821221.362	467536.026	1.27	
26	2821221.224	467540.289	1.15	
27	2821220.715	467541.315	1.85	
28	2821218.470	467542.392	1.67	
29	2821217.867	467542.929	1.97	
30	2821215.922	467542.776	1.95	
31	2821214.158	467541.853	3.18	
32	2821211.745	467539.861	2.97	
33	2821210.226	467537.328	2.25	
4	2821208.336	467536.099	2.25	
5	2821206.414	467534.928	1.86	
6	2821204.994	467536.136	1.71	
7	2821203.399	467535.727	1.40	
8	2821201.990	467536.792	3.19	
9	2821198.983	467535.668	3.72	
0	2821195.908	467533.620	4.25	
1	2821193.177	467530.367	1.80	
2	2821192.422	467528.960	0.66	
3	2821191.983	467528.440	0.53	
4	2821191.508	467528.202	0.07	
5	2821191.452	467528.189	0.09	
6	2821191.418	467528.084	2.16	
7	2821191.432	467525.928	2.16	
8	2821191.435	467523.772	2.16	
9	2821191.431	467521.617	2.16	
0	2821191.414	467518.461	0.91	
1	2821191.147	467518.586	0.96	
2	2821190.413	467517.978	0.84	
3	2821189.610	467517.743	0.84	
4	2821188.672	467517.790	0.89	
5	2821187.815	467518.041	1.57	
6	2821186.256	467518.257	1.97	
7	2821184.296	467518.086	2.36	
8	2821182.062	467517.253	2.36	
9	2821180.232	467515.805	3.20	
0	2821178.534	467513.089	2.48	
1	2821178.361	467510.613	1.73	
2	2821178.677	467508.969	0.71	
3	2821178.867	467508.264	0.71	
4	2821178.828	467507.553	1.07	
5	2821178.533	467506.562	1.97	
6	2821177.193	467505.124	1.59	
7	2821176.196	467503.862	1.91	
8	2821174.800	467502.584	1.43	
9	2821173.790	467501.570	0.48	
0	2821173.462	467501.223	0.16	
1	2821173.615	467501.066	0.17	
2	2821173.651	467501.039	0.32	
3	2821173.886	467501.211	0.53	
4	2821174.404	467501.343	0.38	
5	2821174.785	467501.305	0.79	
6	2821175.554	467501.137	1.57	
7	2821177.115	467500.937	1.05	
8	2821176.184	467500.904	0.79	
9	2821176.951	467500.933	1.70	
0	2821179.119	467499.241	1.00	
1	2821179.219	467498.245	8.24	
2	2821179.994	467490.043		
S=2860.25 面积 4.3354亩				

西部生态廊道（二期）附属设施配套工程选址红线图（四）

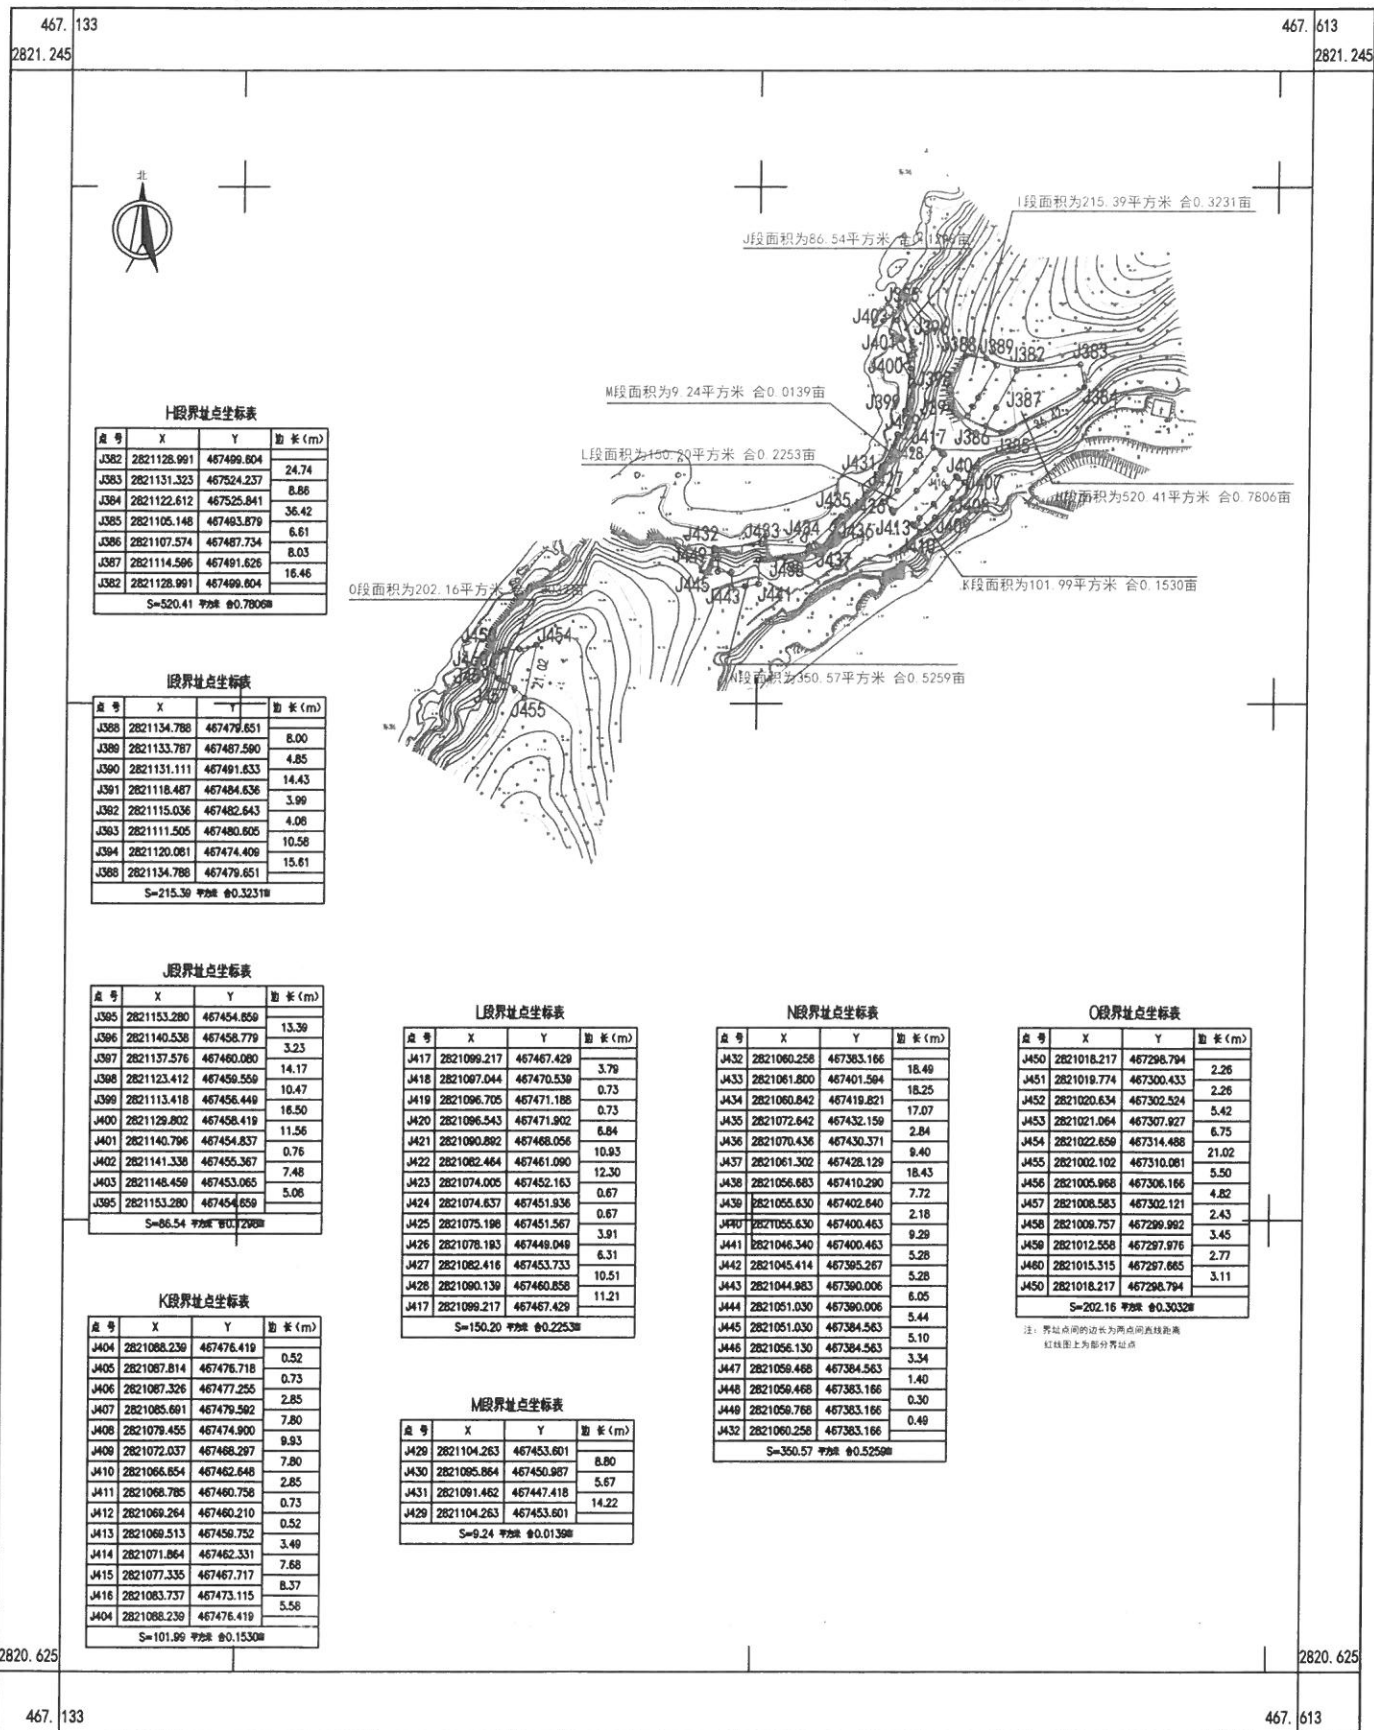

由 Autodesk 教育版产品制作

测绘单位：福州市勘测院平潭分院

由 Autodesk 教育版产品制作

2010年7月数字化成图
2000国家大地坐标系
1985国家高程基准
2009年福州基础地理信息数据图式
加盖福州市勘测院地形图蓝章，方为正式材料

1:2000

共5页，第4页

西部生态廊道（二期）附属设施配套工程选址红线图（五）

由 Autodesk 教育版产品制作

由 Autodesk 教育版产品制作

测绘单位：福州市勘测院平潭分院

