


村域综合规划

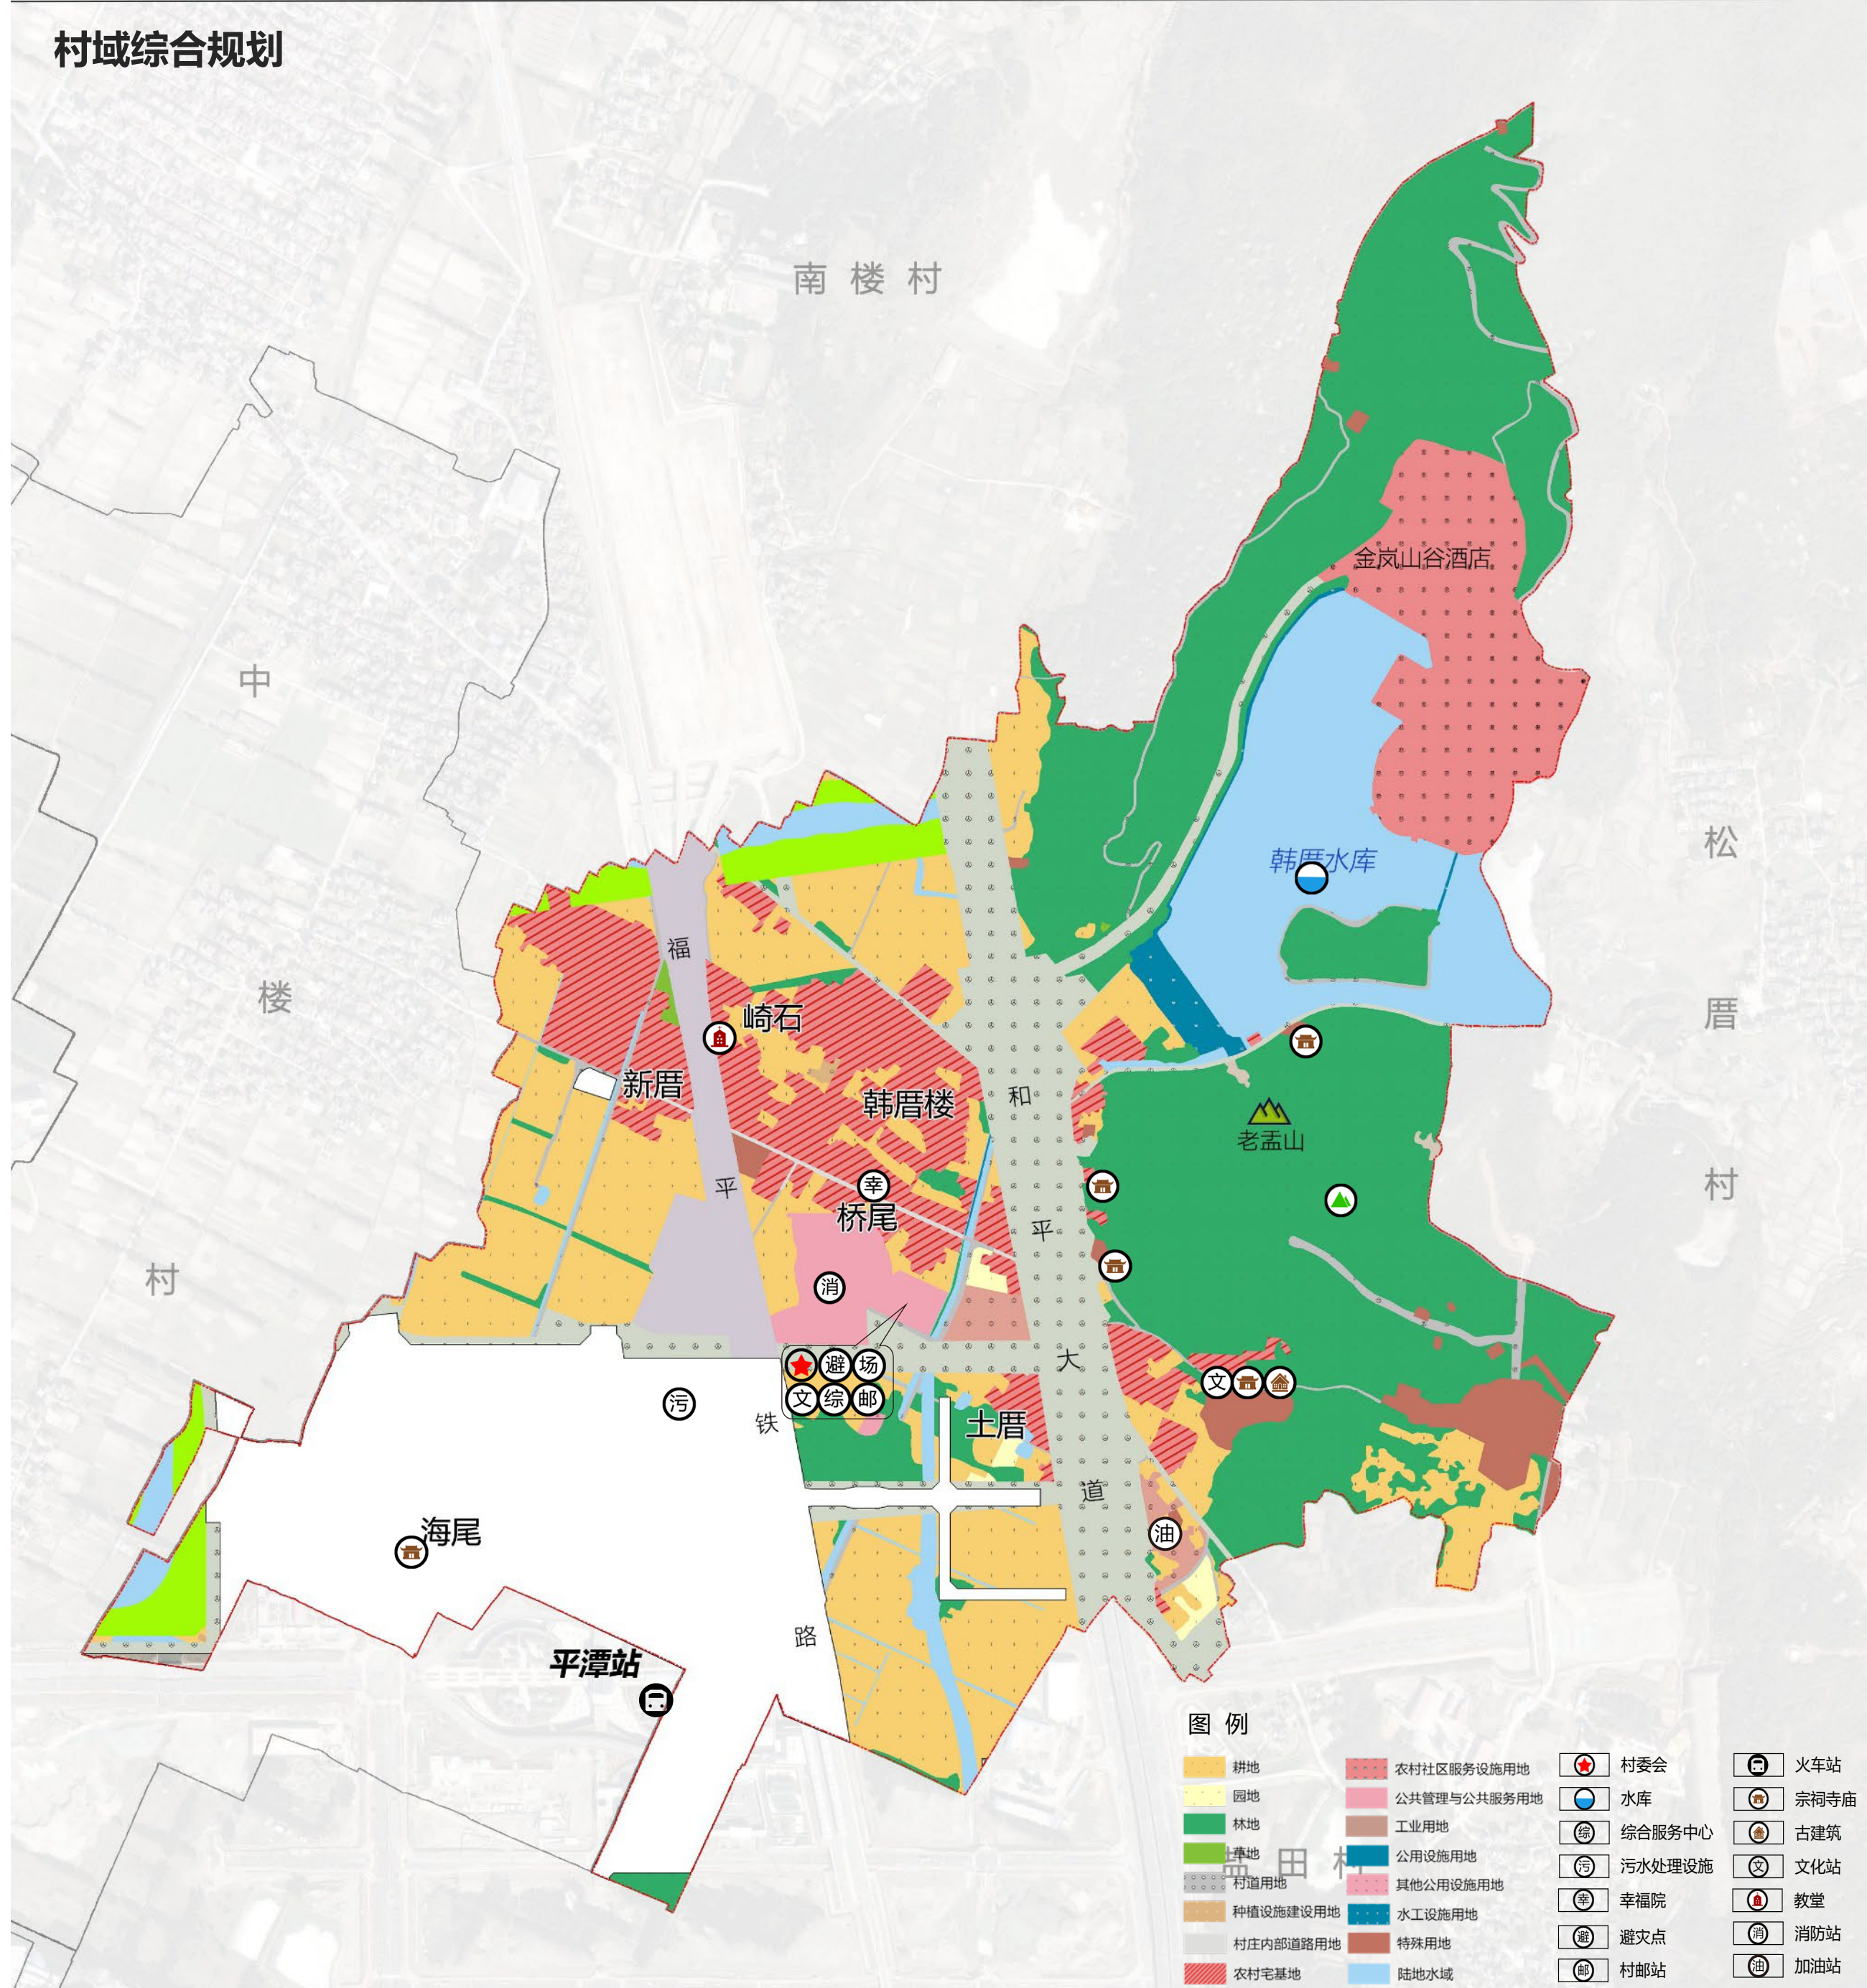


具体变更地块一览表				
项目编码	现状地类	项目	目标年地类	面积 (m²)
HC-A-1	水浇地、村庄道路、沟渠用地	和平大道建设	公路用地	24811.60
HC-A-2	耕地	鹿原路建设	公路用地	191.93
HC-A-3	耕地	城市道路建设	公路用地	1090.00
HC-A-4	耕地、林地	城市道路建设	公路用地	3248.14
HC-B-1	其他林地	规划加油站	公用设施营业网点用地	5658.06
HC-B-2	农村社区服务设施用地	现状加油站迁移腾退	旱地	2050.99
HC-B-3	耕地、林地、宅基地、村道用地	幸福渠绿化	公园绿地	17841.94
HC-B-4	耕地、林地、村道用地	幸福渠建设	河流水面	8559.09
HC-B-5	耕地、宅基地、村道用地	幸福渠绿化	公园绿地	5041.59
HC-B-6	耕地	幸福渠建设	河流水面	7009.83
HC-B-7	耕地、林地	幸福渠绿化	公园绿地	15895.37
HC-C-1	公路用地、林地、其他	产业用地	商业用地	7105.02
HC-C-2	公路用地	农房扩建	农村宅基地	246.38
HC-C-3	耕地	机动建设指标	留白用地	1693.69


规划指标一览表					
序号	指标	属性	单位	现状基期年	规划目标年
二、村庄发展性指标					
1	村域建设用地总面积	约束性	公顷	92.35	108.85
2	村域城乡建设用地面积	约束性	公顷	33.56	76.87
3	村庄建设用地规模	预期性	公顷	33.56	33.22
4	公共管理与公共服务用地规模	预期性	公顷	2.88	2.88
5	公用设施用地规模	预期性	公顷	0.08	0.08
6	人均村庄建设用地面积	预期性	平方米/人	114.74	110.23
三、村庄保护性指标					
7	生态保护红线面积	约束性	公顷	0.30	0.30
8	永久基本农田保护面积	约束性	公顷	27.12	27.12
9	耕地保有量	约束性	公顷	47.37	35.08
10	林地保有量	约束性	公顷	62.57	59.43
11	湿地面积	约束性	公顷	0.00	0.00
12	大陆自然海岸线保有率	约束性	%	—	—
13	自然和文化遗产	预期性	处	—	—

空间结构调整表							
用地类型		现状基期年		规划目标年		变化量 (公顷)	
		面积 (公 顷)	比重 (%)	面积 (公 顷)	比重 (%)		
耕地 (01)		47.37	20.93	35.08	15.50	-12.29	
园地 (02)		0.91	0.40	0.67	0.29	-0.24	
林地 (03)		62.57	27.65	59.43	26.26	-3.14	
草地 (04)		0.14	0.06	0.14	0.06	0.00	
农业设 施建设 用地	村道用地 (060101)		3.63	1.60	3.46	1.53	-0.16
	种植设施建设用地 (0602)		0.10	0.04	0.10	0.04	0.00
村域建 设用地	村庄建 设用地	城镇用地	0.00	0.00	43.64	19.28	43.64
		村庄内部道路用地 (060102)	0.30	0.13	0.30	0.13	0.00
		农村宅基地 (0703)	18.13	8.01	16.64	7.35	-1.48
		农村社区服务设施用地 (0704)	12.08	5.34	11.88	5.25	-0.21
		公共管理与公共服务用地 (08)	2.88	1.27	2.88	1.27	0.00
		商业服务业用地 (09)	0.00	0.00	1.28	0.56	1.28
		工业用地 (1001)	0.09	0.04	0.00	0.00	-0.09
		公用设施用地 (1301-1310, 1313)	0.08	0.04	0.08	0.04	0.00
		留白用地 (16)	0.00	0.00	0.17	0.07	0.17
		小计	33.56	14.83	33.22	14.68	-0.34
	区域基 础设施 用地	铁路用地 (1201)	24.52	10.83	5.90	2.61	-18.62
		公路用地 (1202)	29.48	13.02	21.30	9.41	-8.18
		水工设施用地 (1312)	1.33	0.59	1.33	0.59	0.00
	其他建 设用地	特殊用地 (15)	3.46	1.53	3.46	1.53	0.00
	村域建设用地总面积		92.35	40.80	108.85	48.09	16.51
陆地水域 (17)		19.14	8.46	18.47	8.16	-0.66	
其他土地 (23)		0.13	0.06	0.13	0.06	0.00	
村域总面积		226.34	100	226.34	100	0.00	

国土空间管控

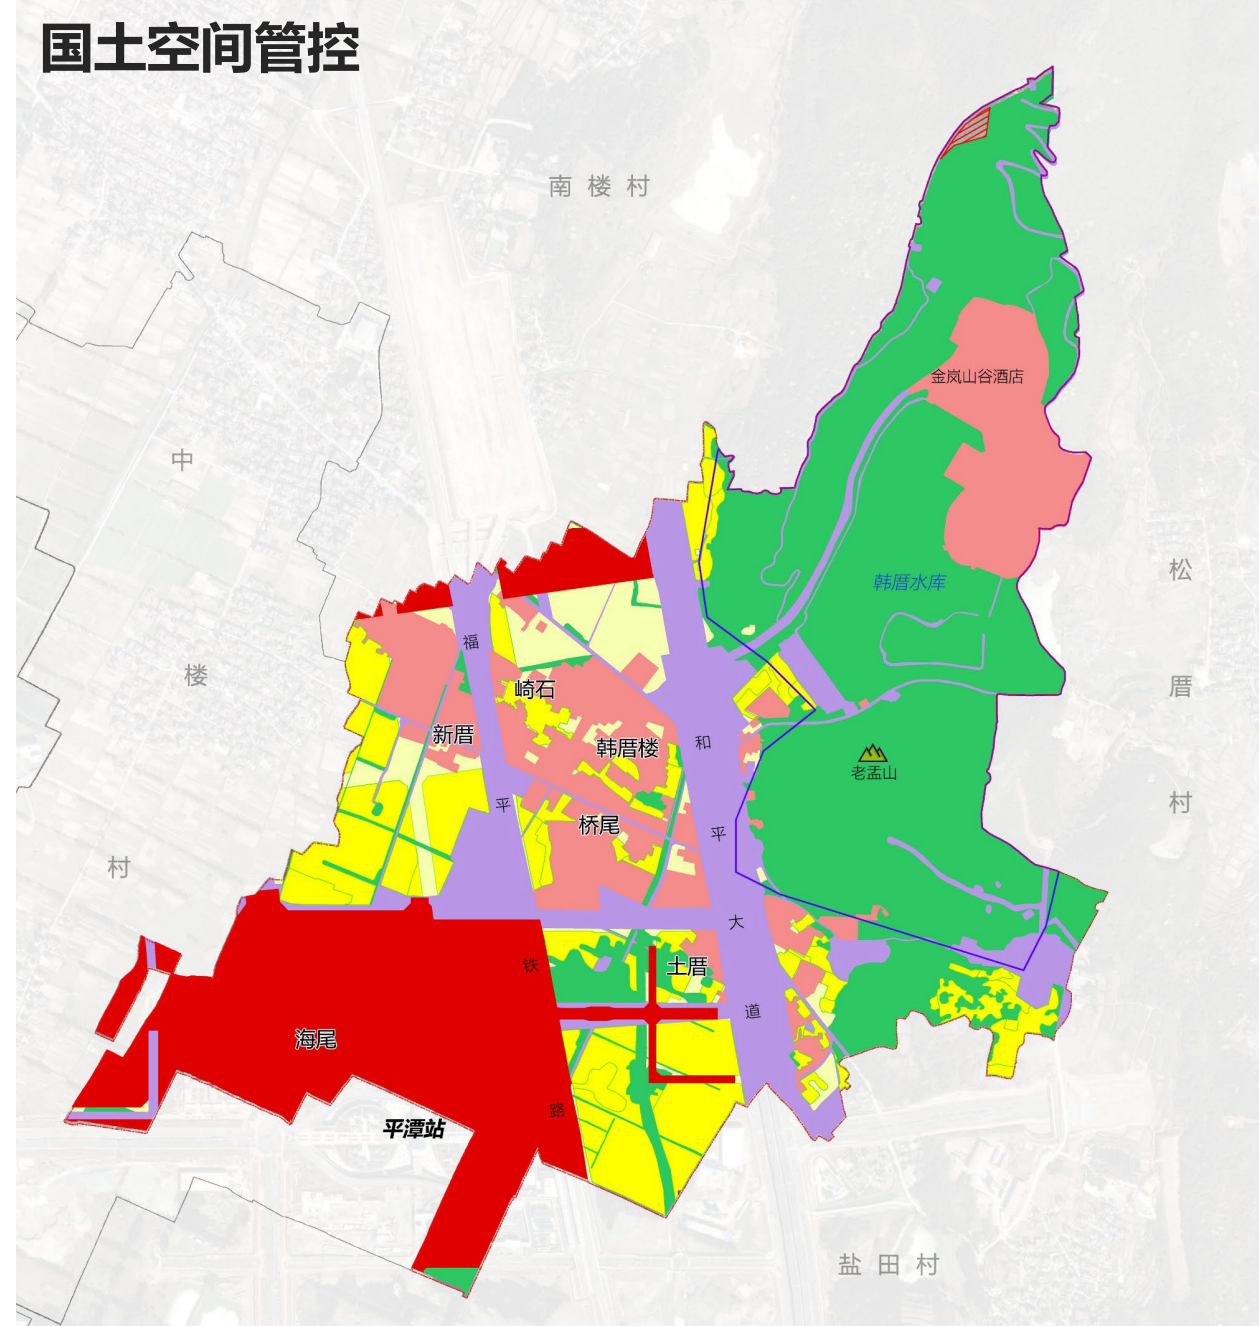

产业空间发展

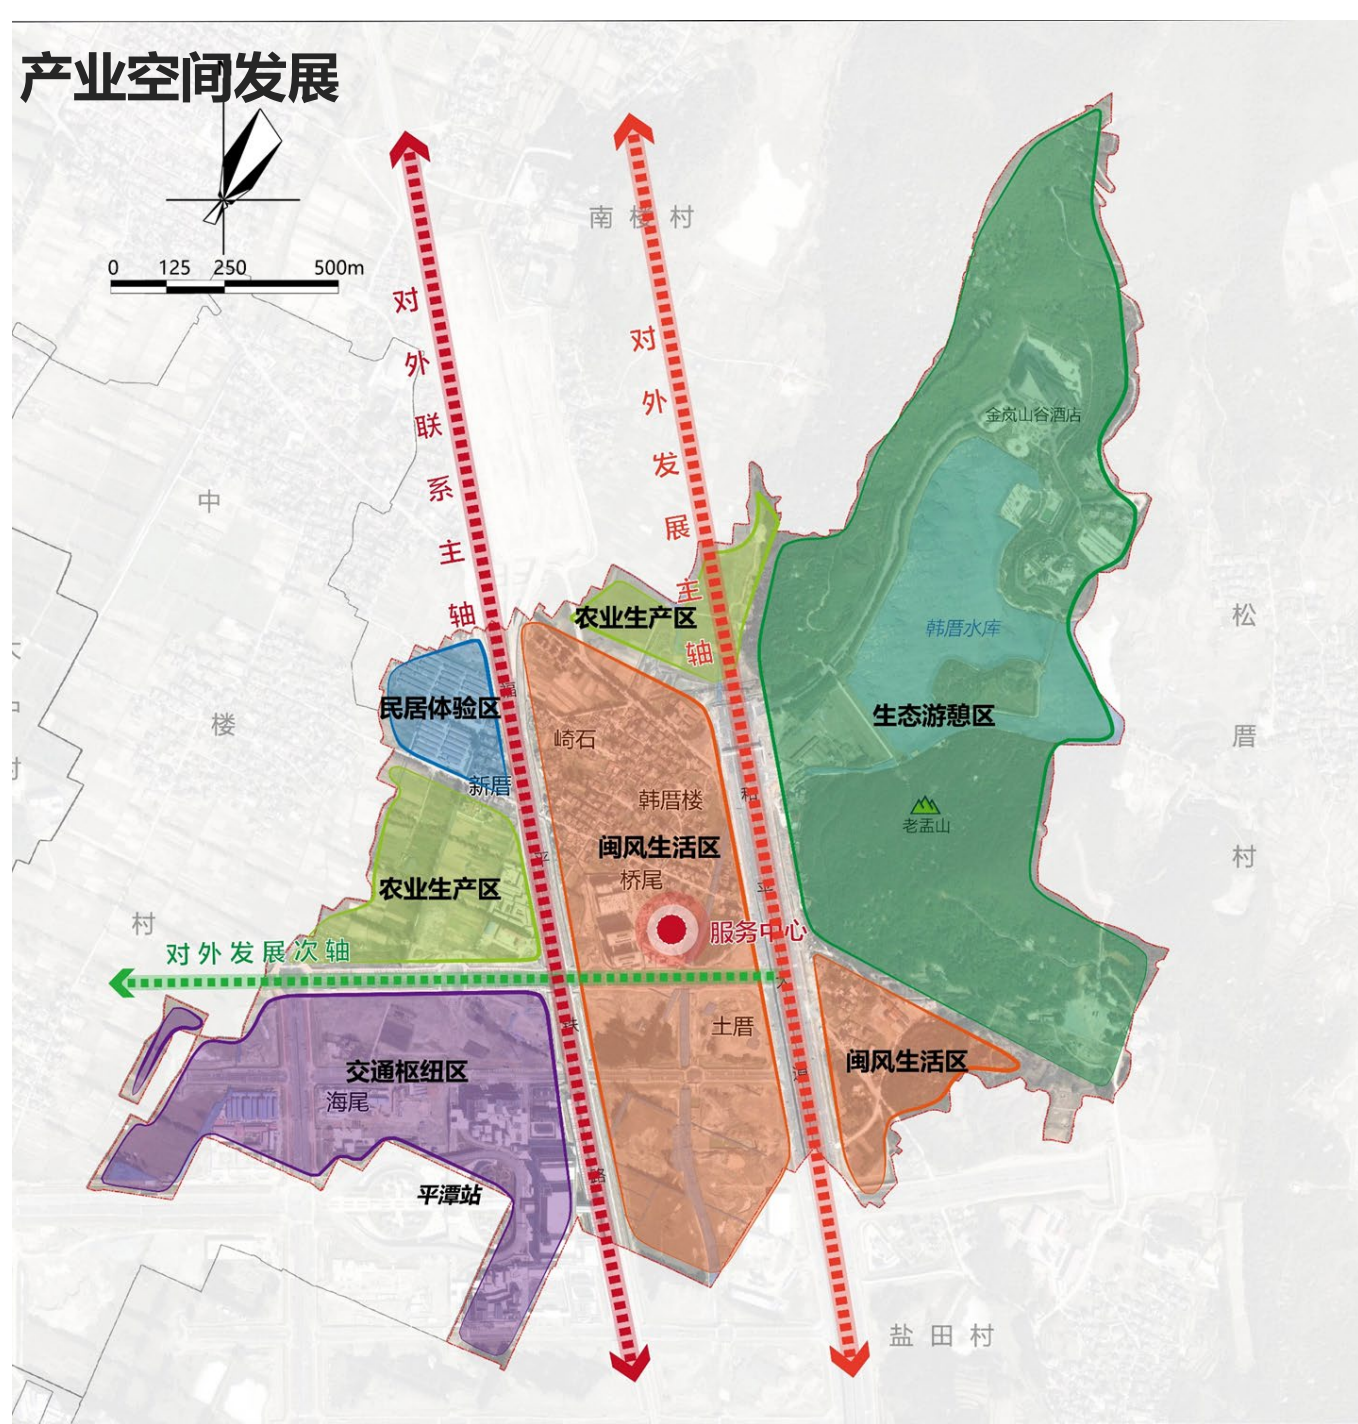

生态保护红线管制规则

严禁不符合主体功能定位的各类开发活动，严禁任意改变用途，确保生态功能不降低、面积不减少、性质不改变。因国家重大基础设施、重大民生保障项目建设等需要调整的，由省级政府组织论证，提出调整方案，经环境保护部门、国家发展改革委会同有关部门提出审核意见后，报国务院批准。

永久基本农田管制规则

从严控非农建设占用永久基本农田。永久基本农田一经划定，任何单位和个人不得擅自占用，或者擅自改变用途。除法律规定的能源、交通、水利、军事设施等国家重点建设项目选址无法避让的外，其他任何建设都不得占用，坚决防止永久基本农田“非农化”。不得多预留一定比例永久基本农田为建设占用留有空间，不得随意改变永久基本农田规划区边界特别是城市周边永久基本农田。符合法定条件的，需占用和改变永久基本农田的，必须经过可行性论证，确实难以避让的，应当将土地利用总体规划调整方案和永久基本农田补划方案一并报国务院批准，及时补划数量相等、质量相当的永久基本农田。

村庄建设区管制规则

规划期内村庄建设边界原则上不得调整，如需调整按规划修改处理，严格论证，报原审批机关批准。有序推进空心村整治和村庄迁并，合理安排农村建设用地，优先满足村民住房和农村基本公共服务设施用地需求

根据村域产业及资源状况，全域规划形成“一心、三轴、五片区”：

“一心”

——服务中心

以村部为核心，打造集政务服务、村民活动、产业发展的综合服务中心，激活村庄活力。

“一横两纵三轴线”

——对外联系主轴

——对外发展主轴

——对外发展次轴

结合和平大道与在建的城市道路，增强村庄对外交通能力，促进产业发展。

“五片区”

——闽风生活区

——交通枢纽区

——民居体验区

——生态游憩区

——农业生产区

近期建设项目

水库环境保护

和平大道建设


韩厝小商城

2#幸福渠

民宿民居

新建村部

加油站建设

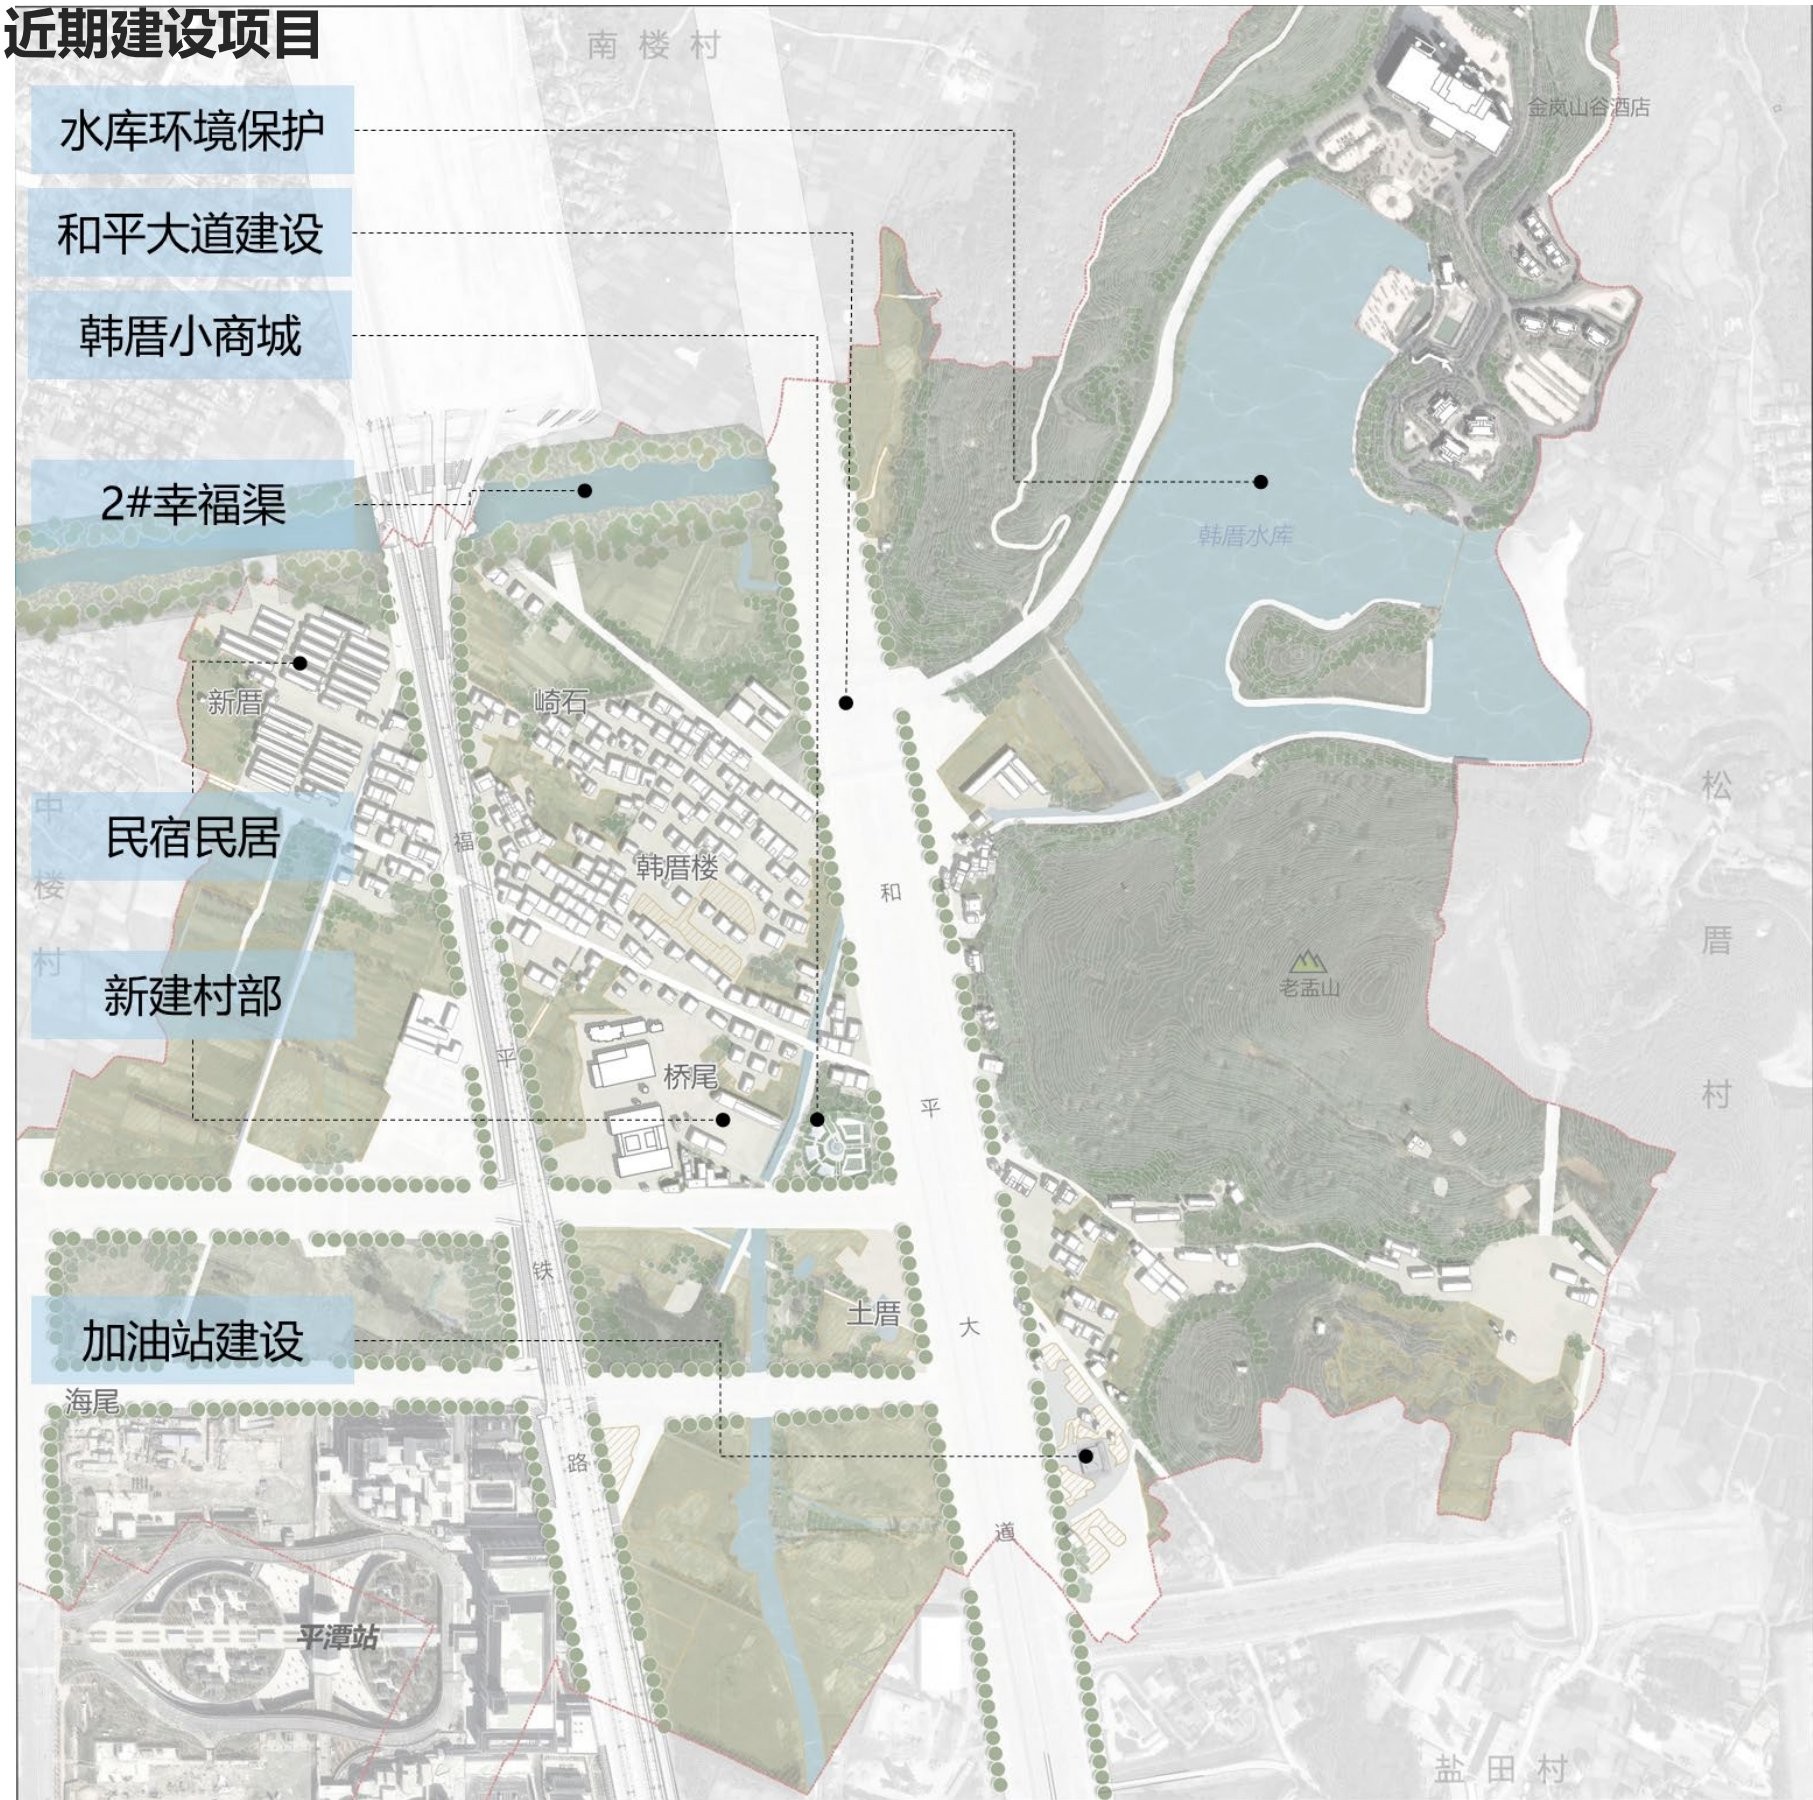

结合村庄发展，韩厝村近期建设项目主要以人居环境提升、产业发展、完善基础设施为主，共3个重点内容，12个近期实施项目。

平潭综合实验区君山片区韩厝村村庄规划建设项目表								
序号	项目类型	项目名称	建设内容	规模	责任主体	建设年限	资金来源	投资估算(万元)
1	人居环境提升	农村生活污水处理	完善污水管线、提升改造污水处理设施	\	村	2023-2025	划拨	30
2		电力电信缆线整治	缆线整治、线路修复	\	村	2023-2025	相关企业	50
3		屋顶平改坡	村庄干道周边的平屋顶民房	\	村	2023-2025	以奖代补	20
4		裸房整治	村庄干道周边的裸房立面整治	\	村	2023-2025	以奖代补	30
5		水系提升	韩厝水库周边环境保护与整治	\	村	2023-2025	划拨	100
6		道路建设	和平大道延伸	约24811.6m ²	交通部门	2023-2025	划拨	-
7		道路提升	村庄支路巷路景观提升	\	村	2023-2025	划拨	80
8	基础设施	新建村部	与村委会合设，配套设置图书室、休闲娱乐场所等	\	村	2023-2025	划拨、筹资	50
9		村邮站	与村委会合设，设置快递服务网点	建筑面积30m ²	村	2023-2025	划拨	5
10		加油站	加油站位置迁移及原址复耕	占地面积约为5658m ²	企业	2023-2025	划拨	400
11		水利设施	2#幸福渠建设	村域内总面积约54348m ²	村	2023-2025	专项资金	-
12		产业发展	韩厝小商城	预留产业发展用地	占地面积约为7105m ²	村	2023-2035	划拨、筹资
合计				\				1065