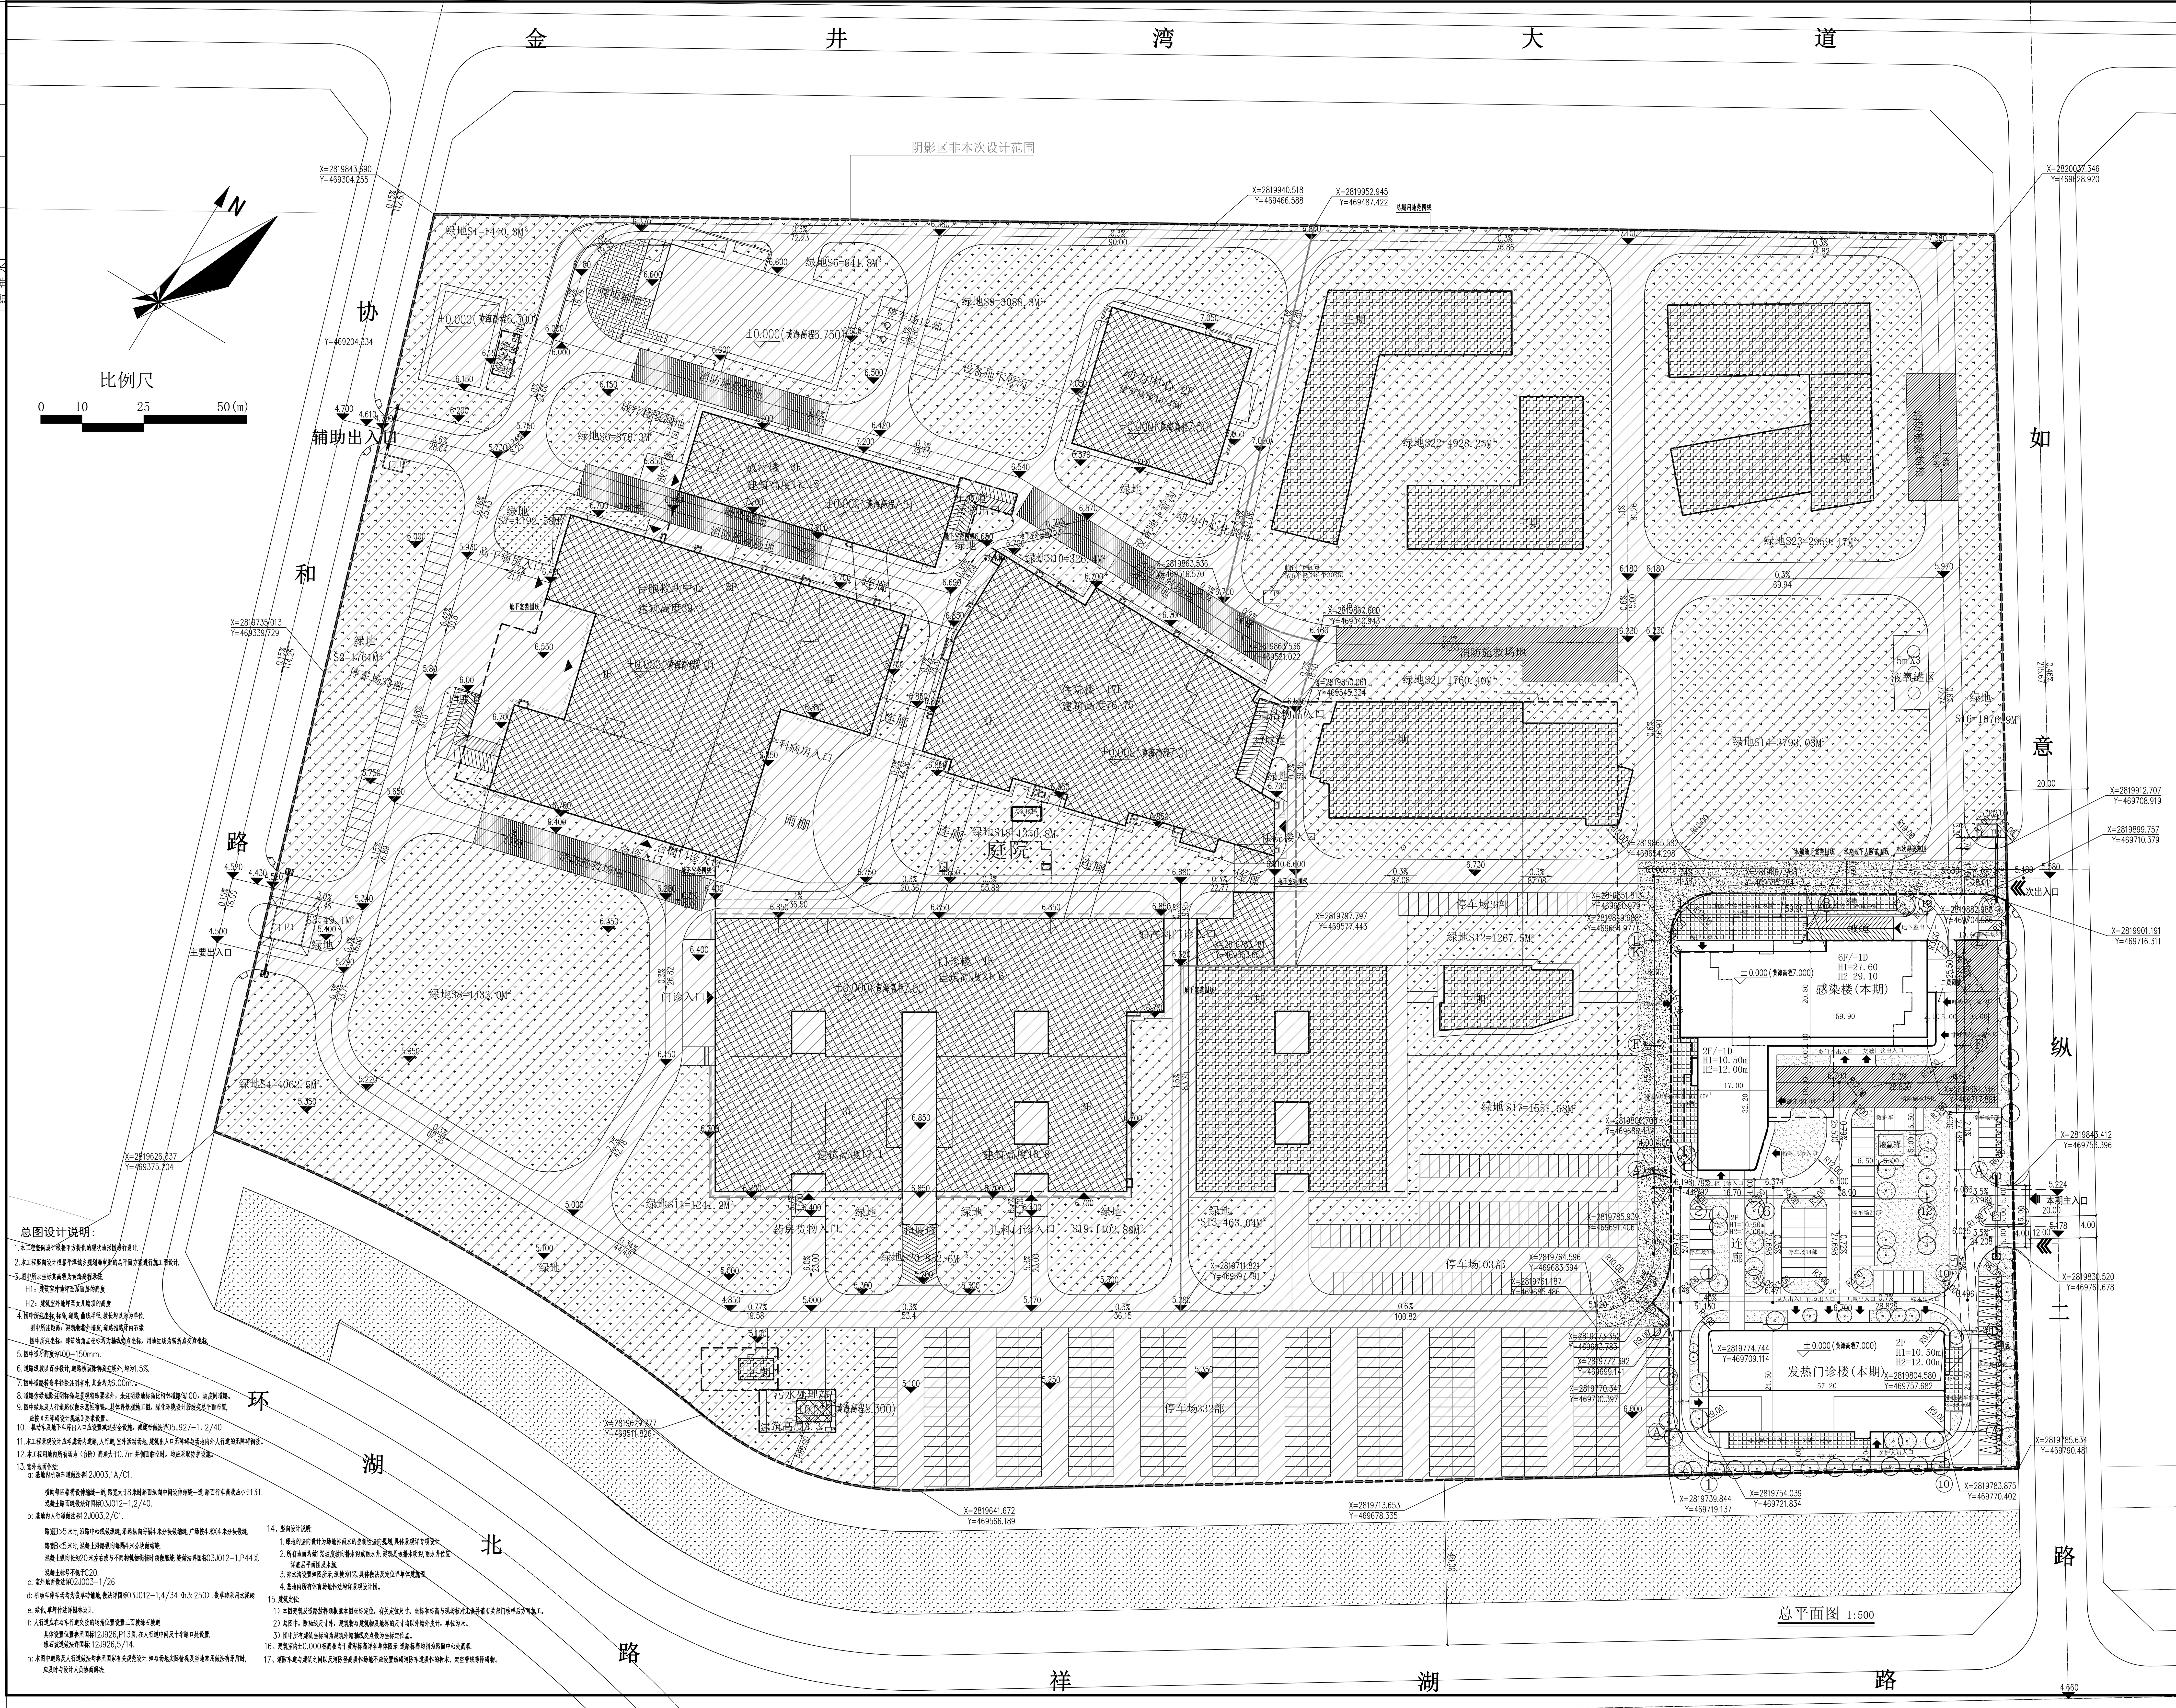

总图设计说明：

1. 本工程竖向设计根据甲方提供的现状地形图进行设计.
2. 本工程竖向设计根据平潭城乡规划局审批的总平面方案进行施工图设计.
3. 图中所示坐标其高程为黄海高程系统.
   H1：建筑室外地坪至屋面层的高度
   H2：建筑室外地坪至女儿墙顶的高度
4. 图中所注坐标, 标高, 道路, 曲线半径, 坡长均以米为单位.
   图中所注距离：建筑物指外墙皮, 道路指路牙内石缘.
   图中所注坐标：建筑物角点坐标均为轴线角点坐标，用地红线为转折点交点坐标.
5. 图中道牙高度为100—150mm.
6. 道路纵坡以百分数计, 道路横坡除特别注明外, 均为1.5%.
7. 图中道路转弯半径除注明者外, 其余均为6.00m..
8. 道路旁绿地除注明标高与景观特殊要求外，未注明绿地标高比相邻道路低100，坡度同道路。
9. 图中绿地及人行道路仅做示意性布置, 具体详景观施工图，绿化环境设计若改变总平面布置，应按《无障碍设计规范》要求设置。
10. 机动车及地下车库出入口应设置减速安全设施，减速带做法详05J927—1、2/40
11. 本工程景观设计应考虑场内道路, 人行道, 室外活动场地, 建筑出入口无障碍与场地内外人行道的无障碍衔接。
12. 本工程用地内所有场地（台阶）高差大于0.7m并侧面临空时，均应采取防护设施。
13. 室外地面作法:
   a: 基地内机动车道做法参12J003,1A/C1.
   横向每四格需设伸缩缝一道, 路宽大于8米时路面纵向中间设伸缩缝一道. 路面行车荷载应小于13T.
   混凝土路面缝做法详国标03J012—1,2/40.
   b: 基地内人行道做法参12J003,2/C1.
   路宽B>5米时, 沿路中心线做纵缝, 沿路纵向每隔4米分块做缩缝. 广场按4米X4米分块做缝.
   路宽B<5米时, 混凝土沿路纵向每隔4米分块做缩缝.
   混凝土纵向长约20米左右或与不同构筑物衔接时须做胀缝. 缝做法详国标03J012—1,P44页.
   混凝土标号不低于C20.
   c: 室外地面做法详02J003—1/26
   d: 机动车停车场均为嵌草砖铺地, 做法详国标03J012—1,4/34 (h3:250). 嵌草砖采用水泥砖.
   e: 绿化, 草坪作法详园林设计.
   f: 人行道应在与车行道交接的转角位置设置三面坡缘石坡道
   具体设置位置参照国标12J926,P13页. 在人行道中间及十字路口处设置.
   缘石坡道做法详国标 12J926,5/14.
   h: 本图中道路及人行道做法均参照国家有关规范设计. 如与场地实际情况及当地常用做法有矛盾时，应及时与设计人员协商解决.
14、竖向设计说明:
   1. 绿地的竖向设计为场地排雨水的控制性竖向规划, 具体景观详专项设计.
   2. 所有地面均做1%坡度坡向排水沟或雨水井. 建筑周边排水明沟, 雨水井位置详底层平面图及水施.
   3. 排水沟设置如图所示, 纵坡为1%. 具体做法及定位详单体建施图.
   4. 基地内所有体育场地作法均详景观设计图。
15. 建筑定位:
   1）本图建筑及道路放样须根据本图坐标定位，有关定位尺寸、坐标和标高与现场核对无误并请有关部门核样后方可施工。
   2）总图中，除轴线尺寸外，建筑物与建筑物及地界的尺寸均以外墙外皮计，单位为米。
   3）图中所有建筑坐标均为建筑外墙轴线交点做为坐标定位点。
16、建筑室内±0.000标高相当于黄海标高详各单体图示. 道路标高均指为路面中心处高程.
17、消防车道与建筑之间以及消防登高操作场地不应设置妨碍消防车道操作的树木、架空管线等障碍物。

说明：
1、本图坐标系统采用2000国家大地坐标系统，高程系统采用黄海高程。建筑物室内地面±0.000绝对标高为黄海高程7.000。
2、图中所注尺寸标注、坐标、标高以米为单位。
3、建筑高度为建筑物室外地坪至女儿墙顶和屋面，具体见图中标注。
4、图中F表示建筑物地上层数，D表示底下层数，H表示建筑高度。

平潭协和总期主要经济技术指标			
项目		单位	数值
用地面积		m²	119704.00
总建筑面积		m²	233987.00
其中	地上建筑面积	m²	170755.00
	地下建筑面积	m²	63232.00
计容建筑面积		m²	170755.00
其中	一期（已建）	m²	114441.00
	二期（本期）	m²	12947.48
	三期（远期）	m²	43366.52
不计容建筑面积		m²	63232.00
其中	一期（已建）	m²	40109.00
	二期（本期）	m²	2439.53
	三期（远期）	m²	20683.47
建筑限高		m	
容积率			1.43
建筑占地面积		m²	29926.00
其中	一期（已建）	m²	22743.76
	二期（本期）	m²	3565.53
	三期（远期）	m²	3616.71
建筑密度		%	25
绿地面积		m²	43006.98
绿地率		%	35
床位数		床	1500
其中	一期（已建）	床	1000
	二期（本期）	床	100
	三期（远期）	床	400
机动车停车车位		辆	1600
其中	一期（已建）	辆	1100
	二期（本期）	辆	107
	三期（远期）	辆	393

平潭协和二期(本期)主要经济技术指标				
项目			单位	数值
用地面积			m²	119704.00
总建筑面积			m²	15387.01
其中	地上建筑面积		m²	12947.48
	地下建筑面积		m²	2439.53
计容建筑面积			m²	12947.48
其中	感染楼		m²	9522.48
	发热门诊楼		m²	3129.36
	连廊		m²	295.64
不计容建筑面积			m²	2439.53
其中	地上面积		m²	0
	地下面积		m²	2439.53
	其中	人防车库面积	m²	999.00
		非人防车库面积	m²	1440.53
建筑限高			m	/
容积率			/	/
建筑占地面积			m²	3565.53
建筑密度			%	/
绿地面积			m²	2188.05
绿地率			%	/
床位数			床	100
机动车停车车位			辆	107
其中	地上机动车位		辆	71
	地下机动车位		辆	36
非机动车停车位			辆	533
其中	地上非机动车位		辆	533
	地下非机动车位		辆	0

备注：
1、机动车位：
12947.48/100*0.8=104辆，实际停车107辆，满足要求。
2、非机动车位：
13281.07/100*4=518辆，实际停车533辆，满足要求。
3、人防应建面积为12947.48（计容面积）*7%=906.32m²，
实际人防面积999.00m²（具体意见以人防部门意见为主）
4、本次仅批复协和医院平潭分院二期（感染楼、发热门诊）"，容积率、建筑密度、绿地率待办理最后一期工程规划许可证时一并计算。

图例：

图例	说明	图例	说明
	用地红线		消防登高操作场地
	地下室轮廓线		绿地
	围墙		地面非机动车停车位
	机动车道		下地下室机动车坡道
±0.000(7.000)	相对标高(绝对标高)		机动车快充停车位
X.XXX	室外场地设计标高		机动车慢充停车位
	消防车出入口		一期建筑(已建)
	院区出入口		二期建筑(本次新建)
	单体建筑出入口		三期建筑(未建)
	地下车库出入口		临时道路
	城市坐标点标注	R12 1.19% 50.5m 77.600	机动车道路 R12表示道路转弯半径，77.600表示路面中心点标高，1.19%表示1.19%的纵坡，50.5m表示变坡点间距离为50.5m
X.XXX	道路设计标高		

设计单位：
千亿设计集团有限公司
QIANYI DESIGN GROUP CO., LTD
建筑设计甲级 公路设计乙级
风景园林甲级 人防工程乙级
房建监理甲级 岩土勘察乙级
城乡规划乙级 市政监理乙级
市政行业乙级 国家高新企业
服务热线：0595-36010855
E-mail：22576477@163.com
网 址：WWW.QYJZSJ.COM
Q Q：1739818713
微信公众号：QYJZSJ
投诉热线：15860336393

备注：详最新版本号图纸，之前作废，不得使用。
本设计图纸未经规划部门同意和审图机构认可，不得用于现场施工，仅供业主建设投资前估算建设造价之参考图。

施工图审查批准单位：

施工图审查批准书证号：

图纸专用章

注册执业章

项目名称：
福建医科大附属协和医院平潭分院二期（感染楼、发热门诊）

子项名称：
福建医科大附属协和医院平潭分院二期（感染楼、发热门诊）

建设单位：
平潭综合实验区医院

审定	黄铭清	(签名)
项目负责人	蔡蓼芸	(签名)
专业负责人	余朋	(签名)
审核	蔡蓼芸	(签名)
校对	杨志群	(签名)
设计	练全胜	(签名)
制图	练全胜	

图名：
总平面图

工程编号		比例	1:500
图别	总建施	图号	01
版本号		日期	2022年08月
升版原因			