

平潭综合实验区自然资源与生态环境局

山边陆岛交通码头项目总平面图批前公示

山边陆岛交通码头项目位于平潭综合实验区流水镇山边村，规划用途为交通场站用地，总用地面积 0.3774 公顷，建设单位为平潭综合实验区旅游客运有限责任公司。

为加强城乡规划公众参与度，规范城乡规划公开公示工作，根据《中华人民共和国城乡规划法》《住房和城乡建设部关于印发<关于城乡规划公开公示的规定>的通知》等相关规定要求，现将山边陆岛交通码头项目总平面图在网站（平潭综合实验区党工委、管委会网 www.pingtan.gov.cn）进行批前公示，征询公众意见。

公示时间为 2023 年 8 月 14 日至 2023 年 8 月 22 日（七个工作日）。公示期间，如有意见，请于公示期内书面反馈至平潭综合实验区自然资源与生态环境局建设工程规划管理处。反馈材料中请注明真实姓名、联系电话、联系地址，如反馈意见信息不准确或不完整，且无法及时进一步核对有关情况的，视为无效意见。反馈超出公示期的，视为无效意见，不予采纳。公示无异议后，我局拟核发该项目建设工程规划许可证。


附注

- 1.附图：总平面图、效果图；最终规划设计方案以核发建设工程规划许可证的附件为准。
- 2.区自然资源与生态环境局办公地点：平潭综合实验区金井湾片区管委会行政中心 7 楼。
- 3.联系人：陈欣一，联系方式：0591-23163344，电子邮箱 zystjjgc@163.com。


平潭综合实验区自然资源与生态环境局

2023 年 8 月 11 日



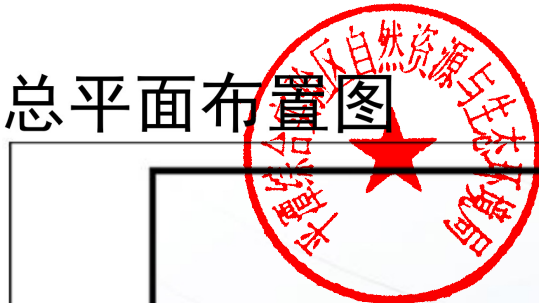

总平面布置图

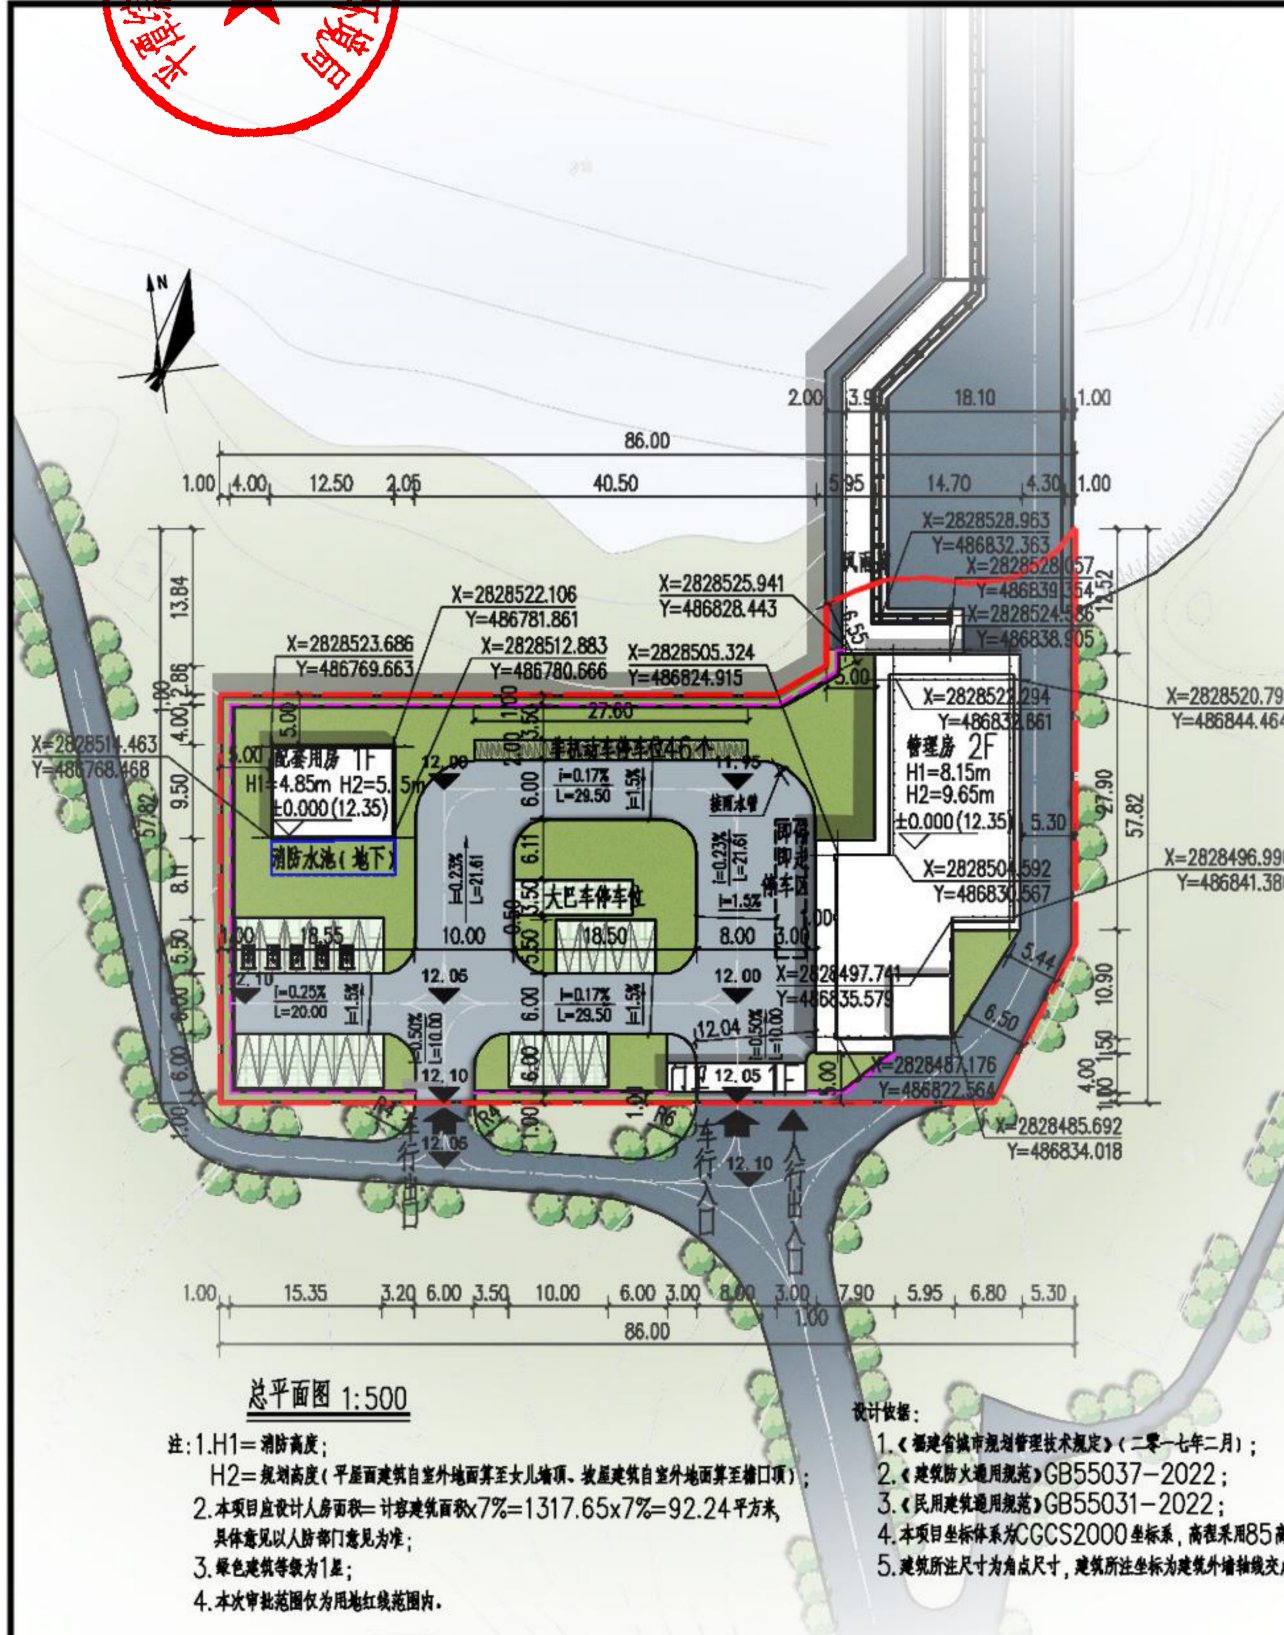

总平面图 1:500

注: 1. H1=消防高度;
H2=规划高度(平屋面建筑自室外地面算至女儿墙顶, 坡屋面建筑自室外地面算至檐口顶);
2. 本项目应设计人防面积=计容建筑面积×7%=1317.65×7%=92.24平方米, 具体意见以人防部门意见为准;
3. 绿色建筑等级为1星;
4. 本次审批范围仅为用地红线范围内。

- 设计依据:
- 《福建省城市规划管理技术规定》(二零一七年二月);
 - 《建筑防火通用规范》GB55037-2022;
 - 《民用建筑通用规范》GB55031-2022;
 - 本项目坐标体系为CGCS2000坐标系, 高程采用85高程基准;
 - 建筑所注尺寸为角点尺寸, 建筑所注坐标为建筑外墙轴线交点坐标。

主要经济技术指标			
项 目	指 标	单 位	备 注
用地面积	3774.00	m ²	
总建筑面积	1402.65	m ²	红线内
其中地上建筑面积	1317.65	m ²	红线内
其中地下建筑面积	85.00	m ²	配套用房地下一层
总计容面积	1317.65	m ²	红线内
管理房	1105.70	m ²	
其中一层面积	488.38	m ²	
其中二层面积	579.76	m ²	
中屋顶层面积	37.56	m ²	
配套用房	119.63	m ²	配套用房地上一层
风雨廊	50.32	m ²	红线内
门卫	42.00	m ²	
不计容面积	85.00	m ²	红线内
建筑占地面积	700.33	m ²	红线内
建筑密度	18.56%		
容积率	0.35		
绿地面积	1038.69	m ²	
绿地率	27.52%		
停车位	67	个	
机动车停车位	21	个	按《福建省城市规划管理技术规定》(二零一七年二月)要求控制, 本地块管理用房按0.8个车位/100m ² 建筑面积计算, 交通建筑(码头)2.0个车位/1000名旅客(最高聚集人数), 本码头最高聚集人数为400人, 经核算需要≥10个车位。
非机动车停车位	46	个	按《福建省城市规划管理技术规定》(二零一七年二月)要求控制, 本地块管理用房按4个车位/100m ² 建筑面积计算, 交通建筑(码头)4个车位/1000名旅客(最高聚集人数), 本码头最高聚集人数为400人, 经核算需要≥46个车位。

注: 1. 本次审批范围仅为用地红线范围内;
2. 充电桩车位数为21×20%=4.2个(取整5个), 快充充电桩车位数为5×10%=0.5个(取整1个), 实际配建充电桩5个, 其中快充充电桩1个。

- 主要图例
- 用地红线
 - 围墙
 - 新建建筑物
 - 车行出入口
 - 绿地
 - 机动车停车位(普通车位)
 - 充电桩停车位
 - 大巴车停车位
 - 非机动车停车位
 - 室外场地标高
 - 室内地坪标高
 - 建筑物定位坐标(轴线交点)

版权所有, 不得复制、套用。
ALL RIGHTS RESERVED, DON'T COPIED, REPRODUCED.

中联合创
ZHONGLIANHECHUANG

中联合创设计有限公司
CHINA UNITED CREATIVE DESIGN CO., LTD.

■ 建筑行业(建筑工程)甲级 A122009183

会签栏 COUNTER SIGNATURE

建 筑	电 气
ARCH.	ELEC.
结 构	暖 通
STRUCT.	HVAC.
给 排 水	
PLUMBING	

签章区 STAMP AREA

版次 NO.	修改内容 DESCRIPTION	日期 DATE

建设单位 CLIENT
平潭综合实验区旅游客运有限责任公司

项目名称 PROJECT
山边陆岛交通码头工程

图纸名称 TITLE

审 定	谢迎林	谢迎林
APPROVED BY		
审 核	徐 彬	徐彬
EXAMINED BY		
项目负责	林锦帆	林锦帆
PROJECT CHIEF		
专业负责	林锦帆	林锦帆
SPECIALITY CHIEF		
校 对	范 浩	范浩
CHECKED BY		
设 计	黄泓斌	黄泓斌
DESIGNED BY		
制 图	黄泓斌	黄泓斌
DRAWING BY		

图号 DRAWING NO.

业务号 JOB NO. ZL-FJD-2254

出图日期 DATE 2023.04

专 业	建 筑	设计阶段	方 案
DISCIPLINE		STAGE	

比 例 1:500 幅 格 A3

SCALE SIZE

条形码, 二维码 BARCODE, QR CODE



