




区位图

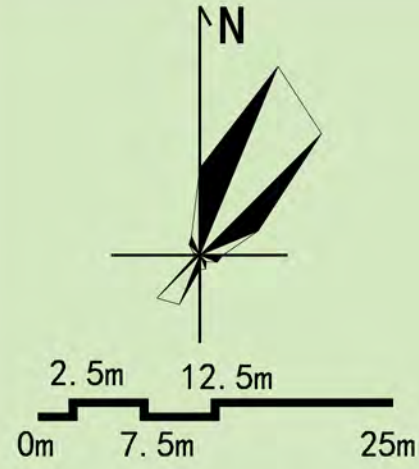


界址点坐标表

点号	X	Y	边长
J1	2830499.936	473844.386	159.30
J2	2830589.513	473976.114	
J3	2830585.986	473993.016	17.27
J4	2830494.708	474050.517	107.88
J5	2830457.425	474042.464	38.14
J6	2830391.047	473968.352	99.49
J7	2830373.642	473947.757	26.97
J8	2830357.449	473926.196	26.97
J9	2830416.766	473884.432	72.54
J10	2830475.416	473841.738	72.54
J11	2830497.788	473846.570	22.89
J1	2830499.936	473844.386	3.06
S=27771.7 平方米 合41.6679亩			

图例

1		规划用地红线
2		规划建筑物
3		外墙外边界线弧墙段两端点的切线相交于一点为角点坐标
4		道路
5		出入口
6		4m宽消防车道
7		消防车登高操作场地
8		地下室边界线
9		无障碍停车位
10		快充停车位 慢充停车位

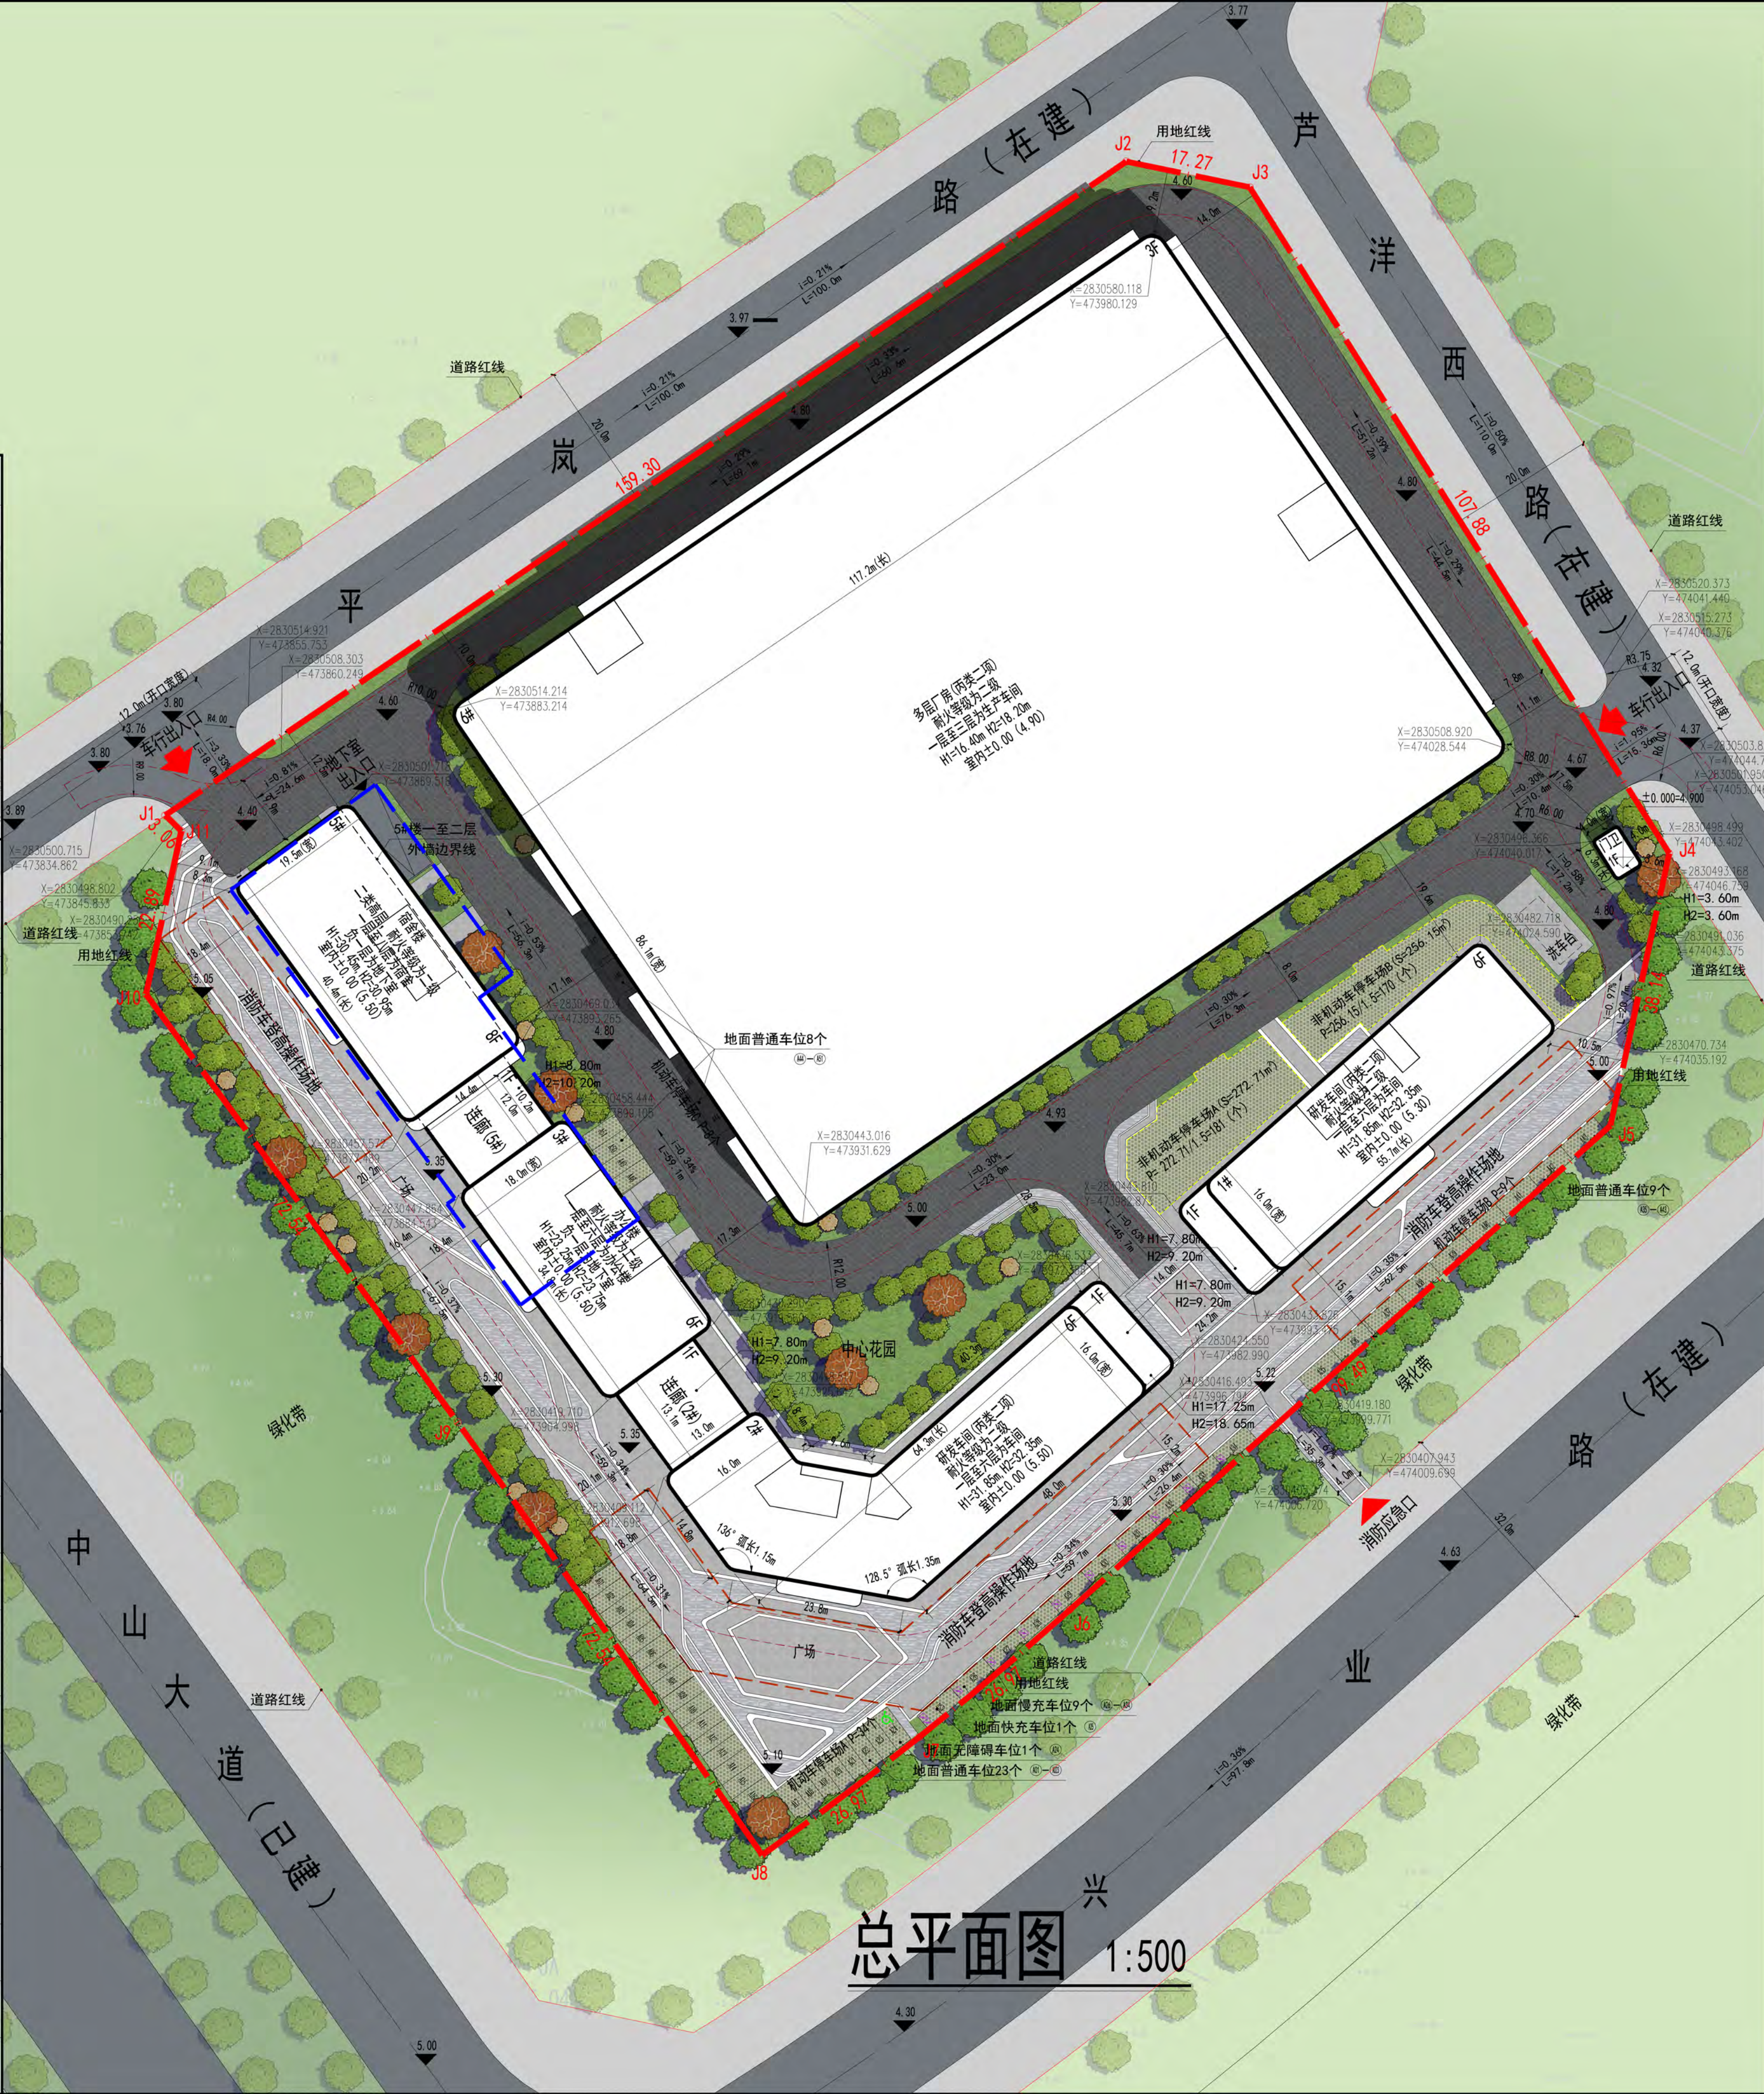

总平面图 1:500

经济技术指标-总表

序号		数量	单位	备注
1	规划用地总面积	27772	m ²	
2	建筑基底面积	13952.07	m ²	
3	总建筑面积	39101.61	m ²	
	地上建筑面积	37593.20	m ²	
	1#研发车间	4996.53	m ²	
	2#研发车间	7046.46	m ²	
	3#办公楼	3483.18	m ²	
	5#宿舍楼	6071.79	m ²	
	6#多层厂房	15970.35	m ²	
4	门卫	24.89	m ²	
	地下建筑面积	1508.41	m ²	地下室车库
5	规划计容总建筑面积	52002.36	m ²	
	地上建筑计容建筑面积	52002.36	m ²	无地上不计容建筑面积
	1#研发车间	4996.53	m ²	
	2#研发车间	7046.46	m ²	
	3#办公楼	3483.18	m ²	
	5#宿舍楼	6071.79	m ²	
	6#多层厂房	30379.51	m ²	
6	门卫	24.89	m ²	
	地下建筑不计容建筑面积	1508.41	m ²	地下室车库
6	容积率	1.9		>1.0; ≤2.0
7	配套设施占地面积	1608.03	m ²	办公、宿舍及门卫
8	配套设施占地面积占用地面积	5.80	%	<7%
9	配套设施建筑面积	9579.86	m ²	办公、宿舍及门卫
10	配套设施建筑面积占计容总建筑面积	18.43	%	<20%
11	建筑密度	50.24	%	>30%
12	绿地率	10.01	%	>10; <20
13	绿地面积	2780	m ²	
14	机动车停车位	79	个	
	其中 地面停车位	51	个	
	地下停车位	28	个	
15	非机动车停车位(地面)	351	个	

注: 1. 坐标及高程说明:
坐标采用2000国家大地坐标系, 高程采用1985国家高程基准。
2. 建筑高度说明:
H1为消防高度, 建筑室外地面标高至屋面面层的高度。
H2为规划高度, 建筑室外地面标高至女儿墙顶高度。
3. 消防说明:
消防道路最小宽度为4m, 消防道路最小转弯半径为12m。
消防车登高操作场地最小宽度为10m, 连续长度大于建筑周边长度的1/4且不小于建筑一个长边长度。
4. 人防说明:
办公楼建筑面积3483.18m², 宿舍楼建筑面积6071.79m², 门卫建筑面积24.89m²。
应建的人防面积为: (3483.18+6071.79+24.89) × 7% = 670.38m²
实建建筑面积893.40m², 设1个乙类常6级二等人员防护单元, 防护单元按要求设置2个出入口, 防化等级为丙级, 掩蔽人数600人。
5. 机动车停车位计算: 办公楼及宿舍楼:
办公机动车: 0.8 × 3483.18 / 100 = 27.8个
宿舍机动车: 0.5 × 6071.79 = 30.4个
机动车合计: 27.8 + 30.4 = 58.2个, 取整为58个。
应配建电动汽车停车位为79 × 20% = 15.8个, 配建快充电动汽车停车位为15.8 × 10% = 1.58个, 即配建快充电动汽车停车位2个, 慢充电动汽车停车位14个。
本项目机动车停车位79个, 其中地面停车位51个, 地下停车位28个, 满足规范要求。
地面停车位设无障碍停车位1个、普通停车位40个、快充停车位1个及慢充停车位9个。
地下室停车位设普通停车位21个、快充停车位1个及慢充停车位6个。
6. 非机动车停车位计算: 办公楼及宿舍楼:
办公非机动车: 4 × 3483.18 / 100 = 139.3个
宿舍非机动车: 2 × 6071.79 = 121.4个
非机动车合计: 139.3 + 121.4 = 260.7个, 取整为261个。
7. 建筑总高度控制在36米以下。
8. 依据《福建省绿色建筑标准》(DBJ/T13-197-2022), 年径流总量控制率不小于75%。
9. 依据《福建省绿色建筑标准》(DBJ/T13-197-2022), 绿色星级目标: 一星级。