

模镜村防浪堤内侧道路及路灯提升项目

施工图

第 1 册 共 1 册

 中城恒业设计集团有限公司

2024年

图纸目录

日期	签名	专业	日期	签名	专业

序号	图号	图纸规格	图纸规格	备注	序号	图号	图纸规格	图纸规格	备注
1		封面	A3		1				
2	00	图纸目录	A3		2				
3	S-01	设计说明一			3				
4	S-02	总平面图			4				
5	S-03	道路硬化总平面图			5				
6	S-04	A区路灯总平面图							
7	S-05	B区路灯总平面图							
8	S-06	A区路灯线路总平面图							
9	S-07	B区路灯线路总平面图							
10	S-08	路灯大样图							
11	S-09	灯具大样图							
12	S-10	路灯基础大样图							
13	S-11	手孔井大样图							
14	S-12	配电箱系统图							
15	S-13	道路硬化做法							
16									
17									
18									
19									
20									
21									
22									

中城恒业设计集团有限公司 ZHONGCHENG HENGYE DESIGN GROUP LIMITED 注册证号: A32012476		工程名称	豫赣村防浪堤内测道路及路灯提升项目	项目负责人	王强	设计	陈奇	图名			建设单位	平潭县君山镇豫赣村村民委员会
		单项名称		专业负责人	陈奇	审核	陈奇	复核	程刚	日期		图号

道路照明设计说明

日期	
签名	
专业	
日期	
签名	
专业	

一、设计依据

- 《城市道路设计规范》
- 《民用建筑电气设计规范》
- 《城市道路照明设计标准》
- 《城市工程管线综合规划规范》
- 供电局、建设单位及其他专业提供的资料和要求。

二、电源

本工程由供电局提供两回单相（50HZ）10kV城市路灯专用电源，并接入箱式变电站的高压室环网柜内，箱式变电站高压室内的10kV电源经专用变压器，降压输出交流单相220V供道路照明用。其中高压部分的设备及二次回路由供电部门整定。

三、照明设计

- 设计标准：城市Ⅲ级道路，平均照度22lx，均匀度0.43。
- 平面布置：路灯沿道路右侧土路肩和桥梁右侧栏杆外侧布置，间距30米，灯杆高10米。
- 箱式变电站：设有高压室、变压器室及低压室的户外成套变电站，外壳为钢板构件，防护等级为IP44，路灯控制箱设于低压室，成套设备应符合电力行业标准SD320—89。
- 路灯控制：采用微电脑路灯自动控制器定时控制，并具有强制降压功能。控制循环时间24小时为一个周期，隔盏控制，在后半夜熄灭半数灯节能。

四、接地


- 线路敷设：由各路灯控制箱引出2回路分别接入各路灯，采用四芯电缆+一根BV—16绝缘电线（PE）供电，并穿路灯专用排管（波纹护套管）直埋地敷设，埋设深700mm。
- 横穿机动车路时采用镀锌水煤气管。
- 路灯高压线路：本工程设置电力排管作为路灯10kV电源进出线管道，并预留部分管道作为其它用电设备的供电管道，10kV进线线型选择及电流整定由供电部门设计。

本工程采用TN—S接地系统。采用人工接地体，接地电阻不大于4欧，路灯人工接地体采用—50×5热镀锌扁钢，沿道路的土路肩通长连接，人工接地体埋深0.8米，每盏路灯必须与接地体可靠连通，所有的金属支架，控制箱，变压器中性点及外壳，电缆金属外壳，电缆保护金属管均应有良好接地。

五、施工及验收应符合国家有关规范。


中城恒业设计集团有限公司 ZHONGCHENG HENGYE DESIGN GROUP LIMITED 注册证号：J32012476	工程名称	濮城镇防浪堤内侧道路及路灯提升项目	项目负责人	王强	设计	陈奇	图名	总平面图		建设单位	平潭县君山镇濮城镇村民委员会	
	单项名称		专业负责人	张强	审核	张强	复核	程刚	日期		图号	S-01

日期	签名	专业
日期	签名	专业

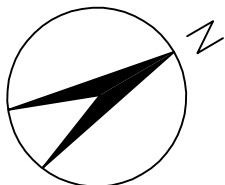


道路照明图例说明

序号	图例	名称	数量
1	⊕⊕	双臂路灯	3
2	⊕	单臂路灯	35

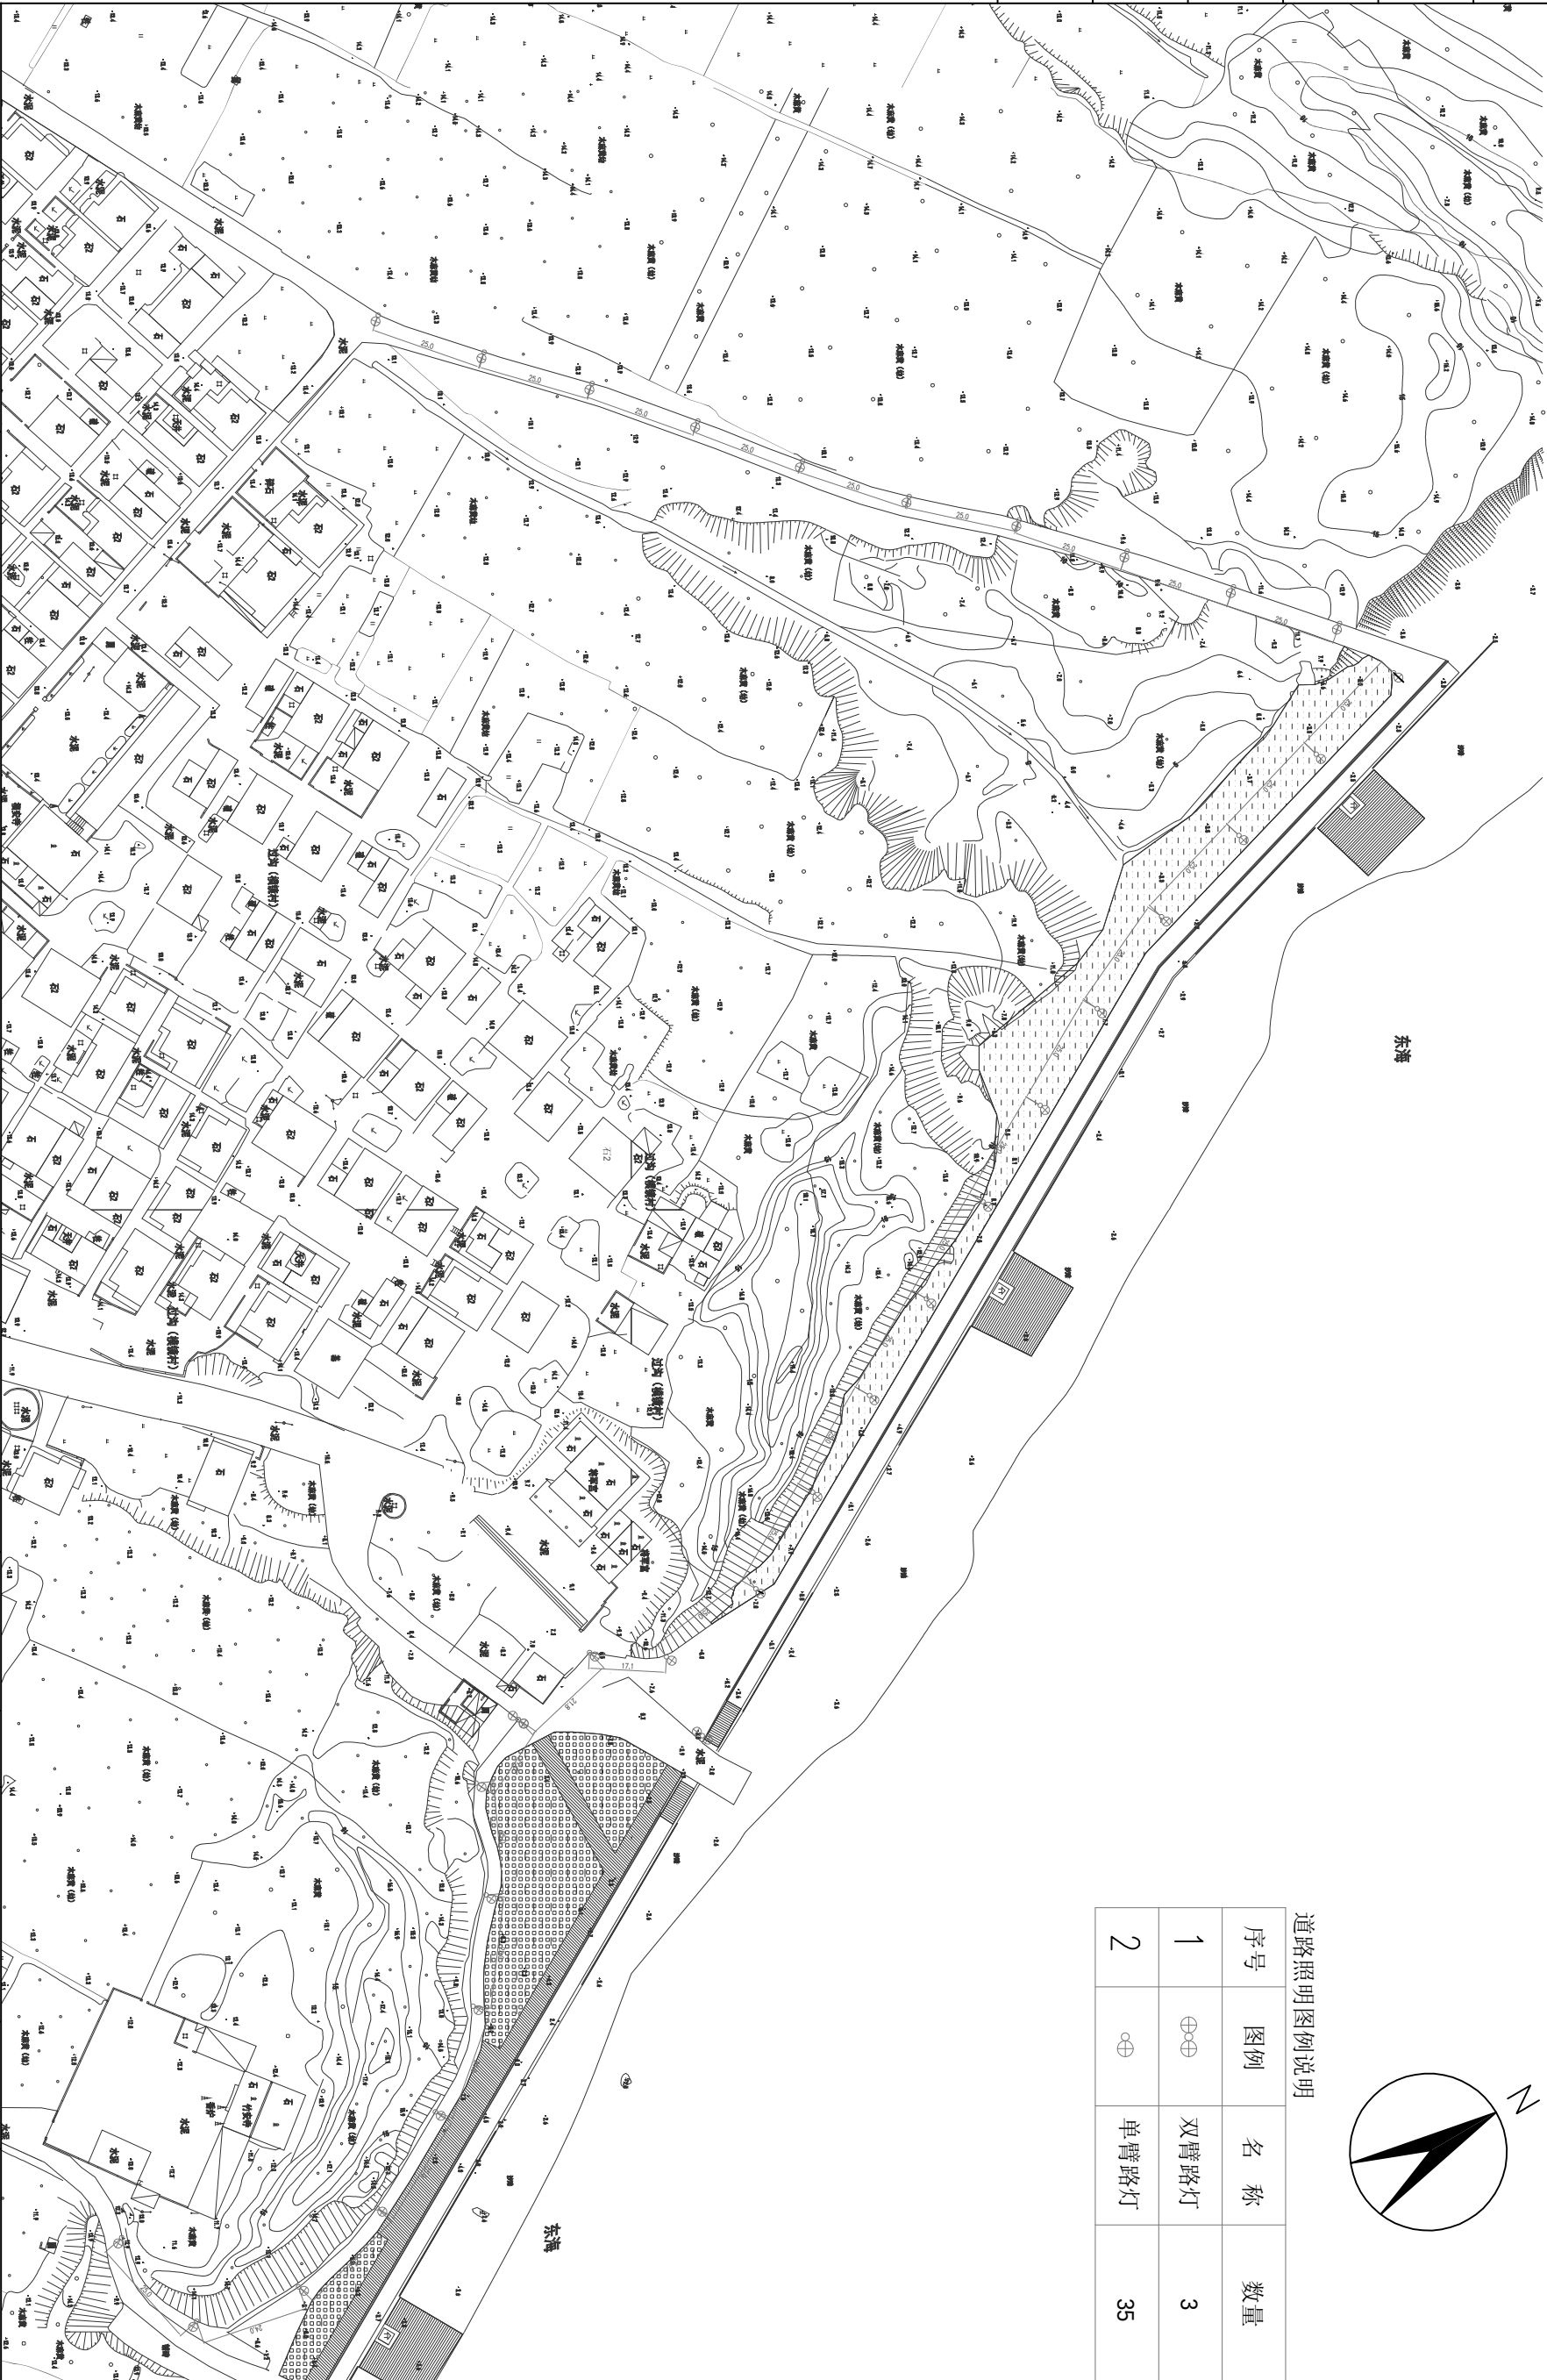

中城恒业设计集团有限公司 ZHONGCHENG HENGYE DESIGN GROUP LIMITED 注册证号: J152012476		工程名称	漠铁村防浪堤内通道路及路灯提升项目		项目负责人	王斌	设计	陈奇	图名	A区路灯总平面图		建设单位	平潭县君山镇漠铁村村民委员会	
		单项名称			专业负责人	陈奇	审核	陈奇	复核	程刚	日期		图号	S-04

日期	签名	专业
日期	签名	专业

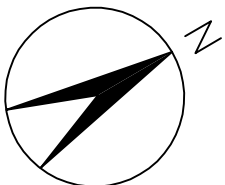


道路照明图例说明

序号	图例	名称
1		路灯控制箱
2		路灯配电箱
3		双臂路灯
4		单臂路灯
5		电缆
6		手孔井




中城恒业设计集团有限公司 ZHONGCHENG HENGYE DESIGN GROUP LIMITED 注册证号: J352012476		工程名称 溪前村防浪堤内通道路及路灯提升项目		项目负责人 王斌		设计 陈奇		图名 A区路灯线路总平面图		建设单位 平潭县君山镇溪前村村民委员会	
项目名称		专业负责人		审核		复核		日期		图号 S-06	


日期	签名	专业
日期	签名	专业

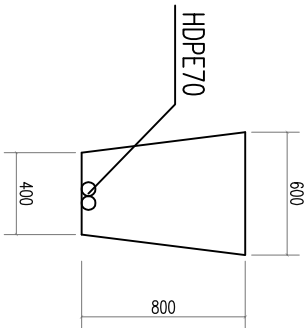


埋设电缆保护管断面

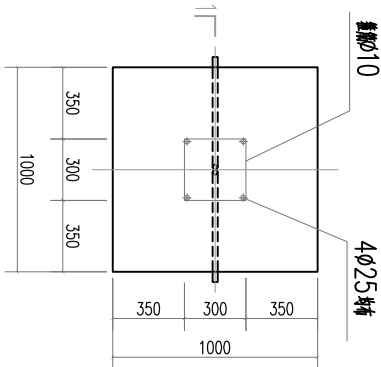


基础平面图

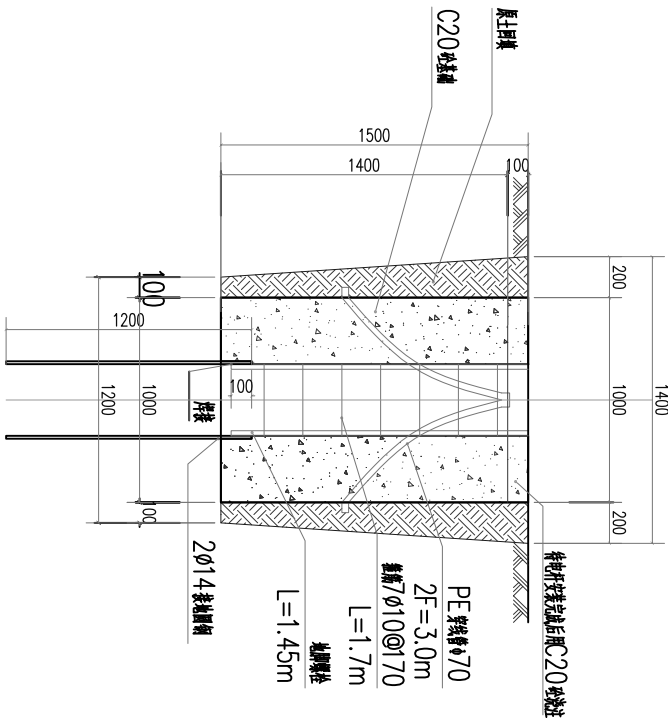

基础1—1 剖面图

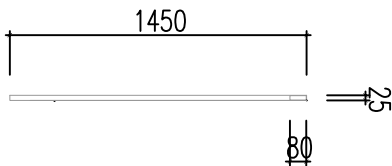

地脚螺栓图

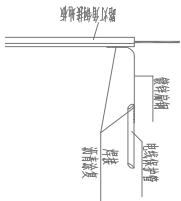


电缆保护管接地做法

序号	名称	规格	备注
1	钢筋	φ25 钢筋 24*1450 根	规格 24
2	钢筋	φ10 钢筋 70 根	规格 10
3	钢筋	C20	规格 20
4	钢筋	φ14, L=1.2m	规格 14

1. 钢筋 1450mm;
2. 钢筋 70mm;
3. 钢筋 70mm, 规格 142.


中城恒业设计集团有限公司 ZHONGCHENG HENGYE DESIGN GROUP LIMITED 注册证号: A32012476		工程名称	豫赣村防浪堤内测道路及路灯提升项目	项目负责人	王斌	设计	王斌	图名	路灯基础大样图	建设单位	平潭县君山镇豫赣村村民委员会
		单项名称		专业负责人	王斌	审核	王斌	复核	程刚	日期	图号 S-10

日期	签名	专业
日期	签名	专业

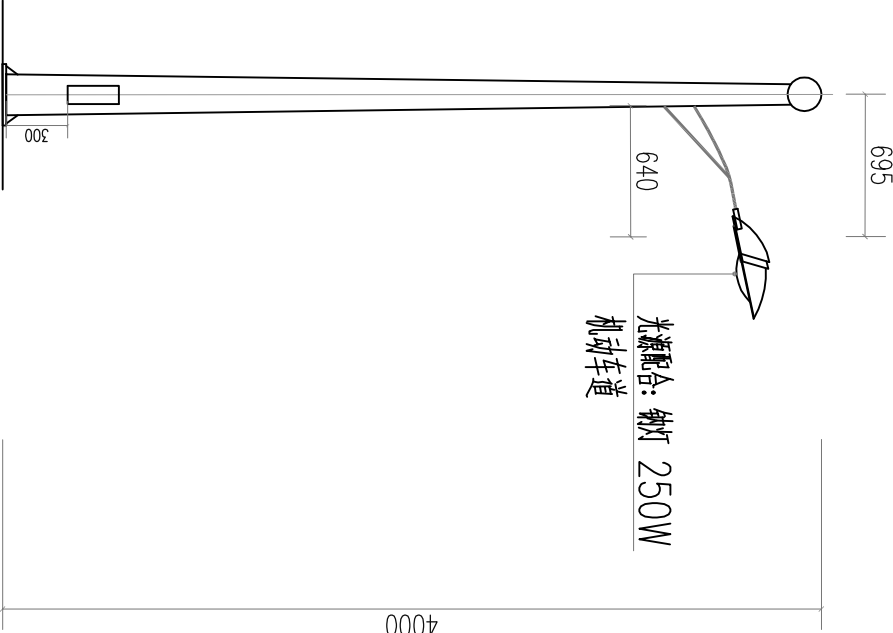

单臂路灯大样图

备注: 路灯样式依据甲方为准

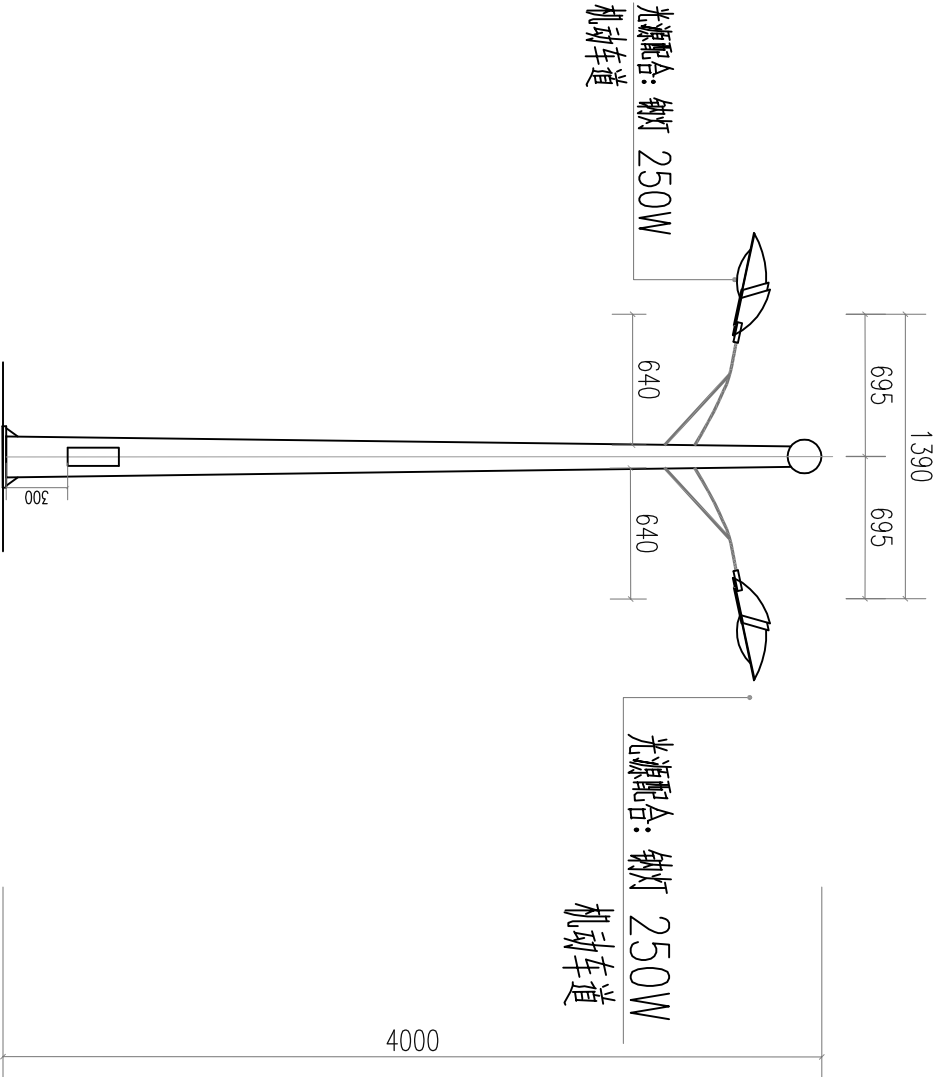


双臂路灯大样图

备注: 路灯样式依据甲方为准

中城恒业设计集团有限公司 ZHONGCHENG HENGYE DESIGN GROUP LIMITED 注册证号: A32012476									
工程名称		豫赣村防浪堤内测道路及路灯提升项目			项目负责人		王斌		
单项名称					专业负责人		王斌		
					设计		王斌		
					审核		王斌		
					复核		程刚		
					日期				
					建设单位		平潭县君山镇豫赣村村民委员会		
					图号		S-08		


日期	签名	专业
日期	签名	专业

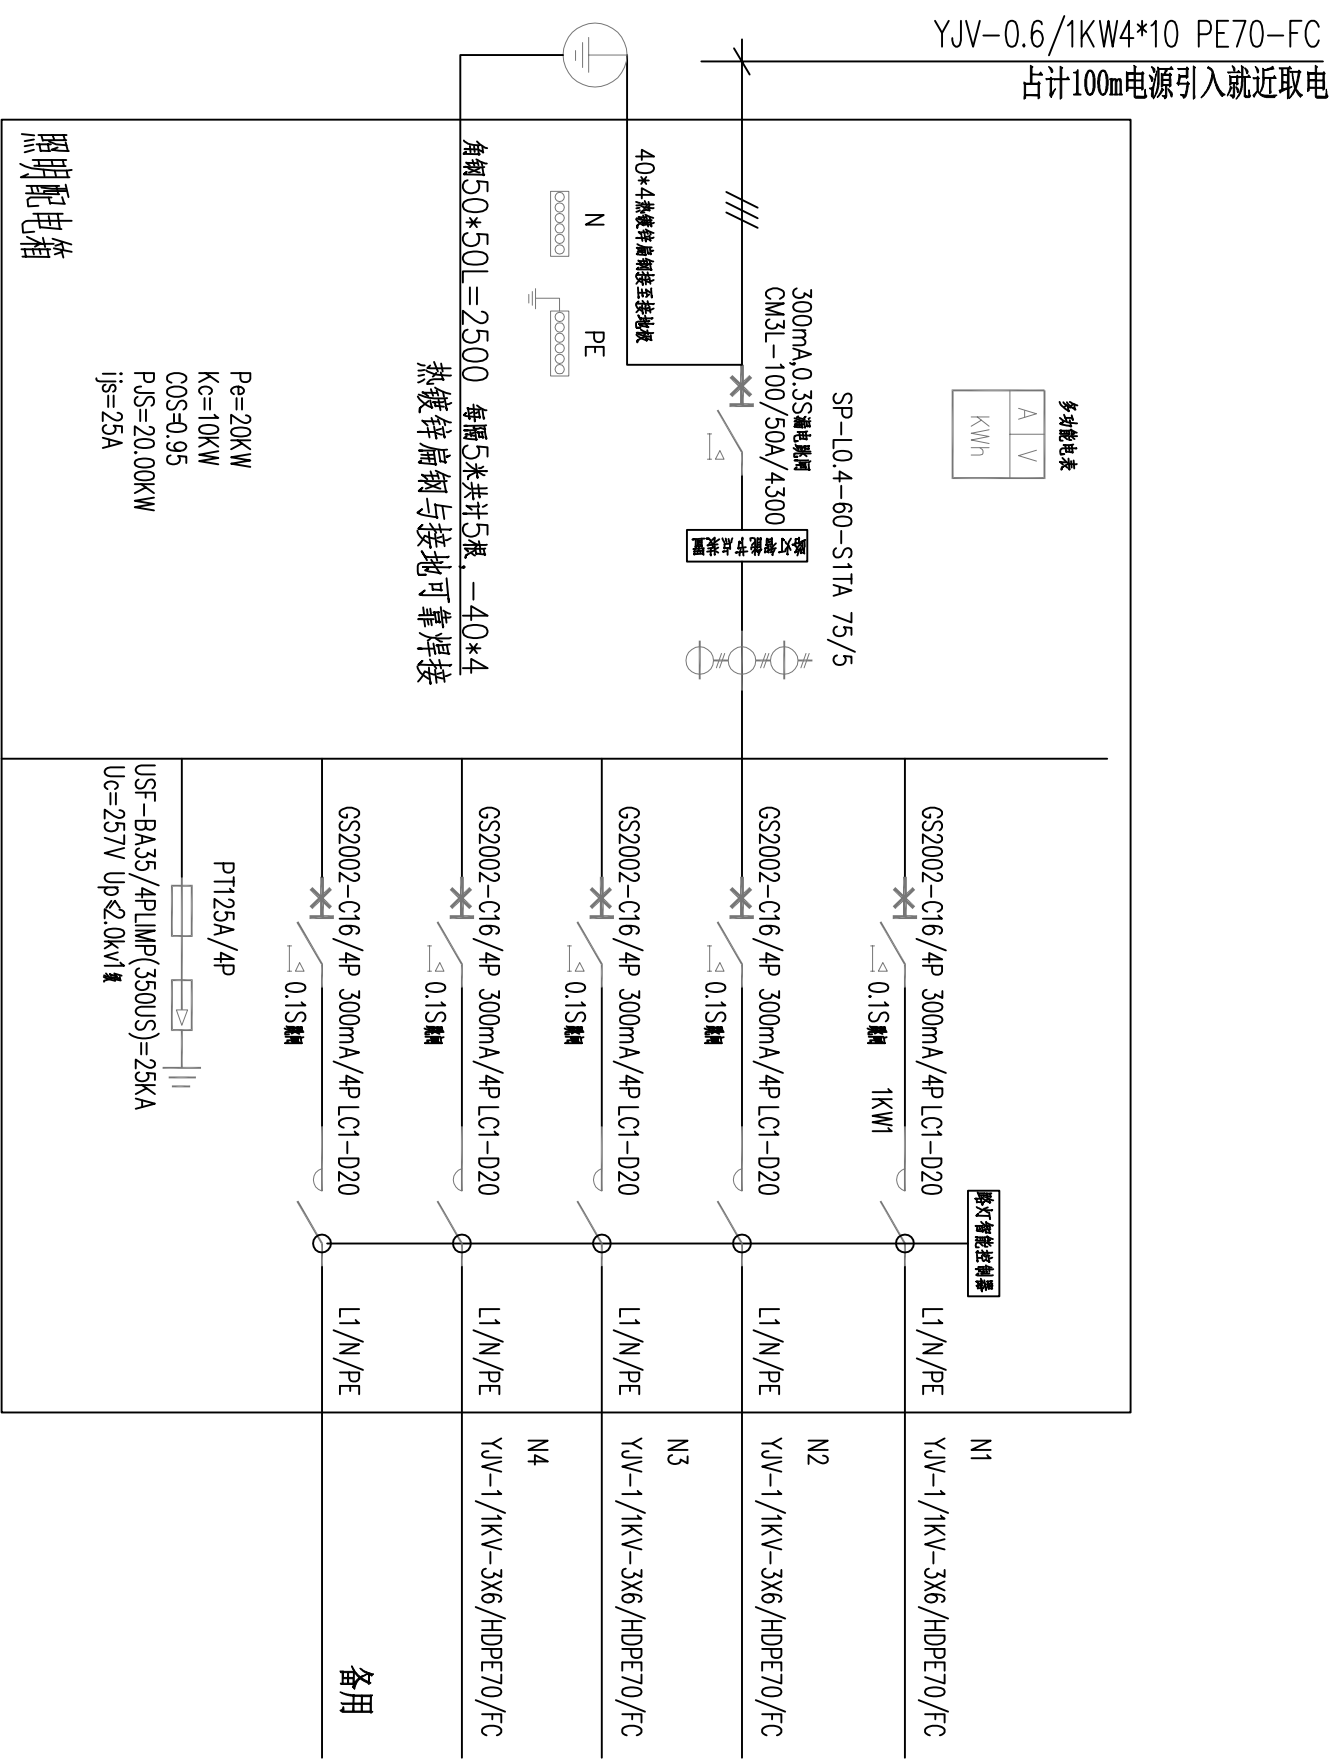

备注: 最终以厂家配电为准。

中城恒业设计集团有限公司 ZHONGCHENG HENGYE DESIGN GROUP LIMITED 注册证号: A32012476																						
工程名称		豫陕村防浪堤内侧道路及路灯提升项目			项目负责人		王瑞云		设计		陈奇		图名		配电箱系统图		建设单位		平潭县君山镇豫陕村村民委员会			
单项名称					专业负责人		陈奇		审核		陈奇		复核		程刚		日期		图号		S-12	

日期	签名	专业
日期	签名	专业

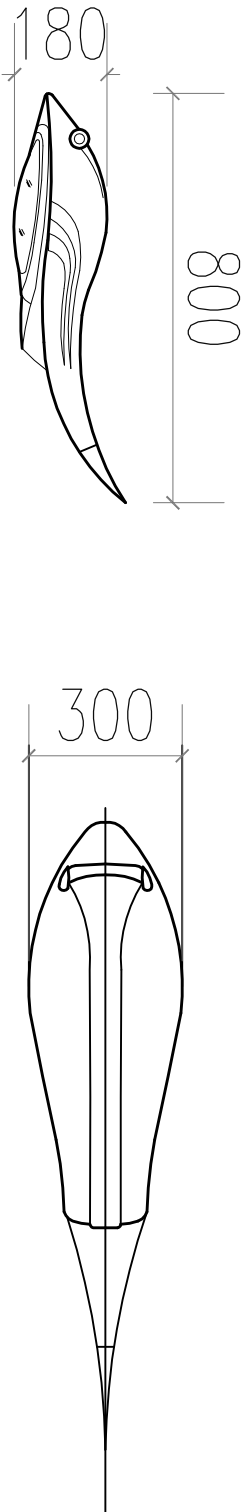


灯具大样图

比例: 1, 尺寸单位: mm;

中城恒业设计集团有限公司 ZHONGCHENG HENGYE DESIGN GROUP LIMITED 注册证书编号: A32012476																						
工程名称		豫赣村防浪堤内侧道路及路灯提升项目			项目负责人		王明杰		设计		陈奇		图名		灯具大样图		建设单位		平潭县君山镇豫赣村村民委员会			
单项名称					专业负责人		陈奇		审核		陈奇		复核		程刚		日期		图号		S-09	

日期	
签名	
专业	
日期	
签名	
专业	

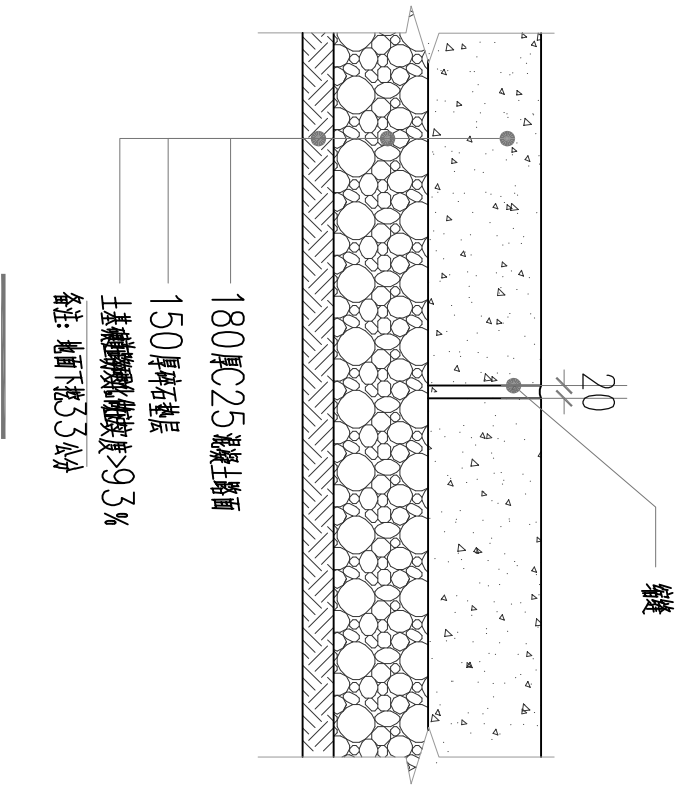

说明:

- 1、本设计除注明外图中尺寸，总图及标高以米(m)为单位，其余均以毫米(mm)为单位。
- 2、一般路肩要求土基回弹模量E0=20Mpa。路基压实度采用重型击实标准，路基填方要求分层压实，松铺厚度不得大于30厘米。
- 3、水泥路面一次铺筑宽度根据各路段和支线的横断面推断，路中心线外应设置纵向施工缝，在路面6米设一道横向缩缝，横向缩缝应及时切缝，不得迟误。在纵缝膨胀及路面自由端部的3条缩缝内，均宜加设传力杆。填缝料应选用与砼板壁粘结牢固，回弹性好，不溶于水，不渗水，高温时不挤出，不流滞，嵌入能力强，耐老化，抗龟裂，低温拉伸量大，低温时不裂，耐久性好材料。路面施工时，强度达到80%后，用刻槽机刻槽，构造深度D≥0.5毫米。

中城恒业设计集团有限公司 ZHONGCHENG HENGYE DESIGN GROUP LIMITED 注册证号: A32012476		工程名称	豫赣村防浪堤内测道路及路灯提升项目	项目负责人	王明杰	设计	王明杰	图名	道路硬化做法		建设单位	平潭县君山镇豫赣村村民委员会	
		单项名称		专业负责人	王明杰	审核	王明杰	复核	程刚	日期		图号	S-13