

五星村风帆运动训练基地交通配套设施及餐饮业态提升
项目（交通配套设施项目）

施工图设计

第一册 共一册

中创合信设计集团有限公司
二〇二四年六月



工 程 设 计 资 质 证 书

证书编号: A352012626

有效 期: 至2026年09月17日

中华人民共和国住房和城乡建设部制

企 业 名 称 : 中创合信设计集团有限公司

经 济 性 质 : 有限责任公司 (自然人投资
或控股)

资 质 等 级 电 力 行 业 (新 能 源 发 电 、 送 电 工 程 、 变 电
工 程) 专 业 乙 级 ; 市 政 行 业 乙 级 ; 水 利 行 业 丙 级 ; 建
筑 行 业 乙 级 ; 风 景 园 林 工 程 设 计 专 项 乙 级 ; 环 境 工 程
(水 污 染 防 治 工 程 、 大 气 污 染 防 治 工 程 、 固 体 废 物 处
理 处 置 工 程) 专 项 乙 级 ; 公 路 行 业 (公 路) 专 业 丙
级。

可承担建筑装饰工程设计、建筑幕墙工程设计、轻型
钢结构工程设计、建筑智能化系统设计、照明工程设
计和消防设施工程设计相应范围的乙级专项工程设计
业务。

发证机关:



2023 年 10 月 30 日

No.AZ 0205331

中创合信设计集团 有限公司		图纸目录						工程编号
		工程名称	五星村风帆运动训练基地交通配套设施及餐饮业态提升项目（交通配套设施项目）					
序号	图纸编号	图纸名称	张数					备注
			A0	A1	A2	A3	A4	
1	ST-01	设计说明				1		
2	ST-02	总平面图				1		
3	ST-03	场地平整平面图				3		
4	ST-04	平面设计图				1		
5	ST-05	平面尺寸图				1		
6	ST-06	排水沟做法详图				1		
7	ST-07	小车停车位做法详图				1		
8								
9								
序号	图纸编号	图纸名称	张数					备注
			A0	A1	A2	A3	A4	
32								
33								
期			
名			
地			
气	电	水	通
排	给	排	暖
期			
名			
地			
构	建	结	

设计说明

一、工程概况

- 1、五星村风帆运动训练基地交通配套设施及餐饮业态提升项目（交通配套设施项目），位于平潭县君山镇五星村。

二、设计依据

- 1、甲方提供的总平、竖向施工图等。
- 2、甲方确认的方案设计。
- 3、《 风景园林图例图示标准》CJJ67-95。
- 4、国家建筑标准设计图集（中国建筑标准设计研究院）。

三、一般说明

- 3.1、除图中有特别标注或说明者外所标尺寸以米为单位，标高以米为单位。
- 3.2、除图中有特别说明外图中标高均为绝对标高。
- 3.3、图中所注距离：建筑指外墙皮；道路指道牙之内缘。

四、土建说明

4.1、材料要求

路面设计根据使用的性质及功能、等级、使用要求及所经地区的气候，水文，地质等自然条件，结合该地区等级路面设计及施工经验，进行设计，并本着技术先进，经济合理，安全适用，环境协调，合理取材，方便施工，利于养路的原则，同时根据对连江地区筑路材料的调查，路面基层及垫层材料可供选择的有碎石、天然砂砾，材料储量丰富。

4.2 路面材料要求及施工要点

（1）水泥：水泥含量为混合料重的5%应选用终凝时间较长（宜在6 小时以上）的水泥，快硬水泥早强水泥以及受潮变质的水泥不得使用。水泥标号为425 号。

（2）砂砾：最大粒径不大于30 毫米，含泥量不大于2.0%，通过试验配定配合比，水泥稳定砂砾用拌合机均匀拌合，用摊铺机摊铺，压实度为98%。加水拌合到碾压终了的延迟时间不超过2.5 小时，水泥稳定砂砾的7 天浸水抗压强度应大 于3.5Mpa。水泥稳定砂砾碾压完成，密实度检验合格后，立即洒水养生，不能延误，洒水时间为上、下午各一次， 用水量为5~6kg /M2。养生期不少于七天，养生期内，应封闭交通。

4.3、水泥混凝土材料技术要求

（1）材料要求

①水泥：采用标号不低于425#，尽量使用强度高、收缩性小、耐磨性强、抗冬性好的水泥，其物理和化学性能满足有关规范的要求。进场的所有水泥必须具有相关的性能证明材料。

②粗骨料：粗骨料采用质地坚硬、耐久、洁净，具有良好级配的碎石或砾石，颗粒接近立方体，最大粒径不得超过40mm。对含有特定活性成分的粗骨料，注意水泥的种类的选择，水泥的碱含量不得超过0.6%。

③细骨料：尽量采用天然砂或人工砂和石屑等作为细骨料，质地坚硬、耐久、洁净，并有良好的级配，满足有关规范的规定。

④水：尽量使用洁净的饮用水，使用非饮用水时要进行检验。施工用水要符合的规定：

A、硫酸盐含量（按照SO42- 计）不得超过2700mg/l；

B、含盐量不得超过5000mg/l；

C、pH 值不得小于4。

⑤钢筋：符合热轧钢筋的有关规定，钢筋顺直，不得有裂缝、断伤、刻痕，表面不得有油污和颗粒状、片状锈蚀。

⑥接缝材料：接缝板尽量采用木板、纤维板、泡沫橡胶板或泡沫树脂板等材料，也可选用其他常温式填缝料。接缝材料的各项性能 要满足接缝板的有关技术要求。

（2）施工配合比设计

路面砼设计包括材料标准实验、砼抗折和抗压强度实验、集料级配、水灰比、坍落度、水泥用量、质量控制等。水泥用量不得小于 300kg/m3，砼的最大水灰比不得大于0.46。

（3）施工要求

①在进行砼面板摊铺之前，要对路面基层表面进行清理，不得残存有浮土杂物，并对不符合要求的地段进行必要的整修。

②模板采用钢模板，混合料摊铺采用摊铺机进行，摊铺时要控制摊铺机的行进速度，确保摊铺连续进行。对于不能采用摊铺机进行 摊铺的地段，经批准以后可以利用人工进行摊铺。摊铺要在整个宽度连续进行，中断施工时要按照规定设施工缝。

③对混合料的振捣注意振捣施工时间，振捣时间应以混合料停止下沉、不再冒气泡并泛出砂浆为准，不得过振，同时利用人工进行 找平，找平时要使用较细的混合料，严禁采用纯水泥浆进行修补找平。

④经找平以后的路面要按照规定进行制纹处理，保证砼路面的抗滑要求。

⑤经找平和制纹处理以后的路面工程要立即进行养护，并严格进行交通管制。

⑥接缝处理：

A、纵向缩缝：采用切缝法进行。在砼强度达到设计强度25%~30%的时候进行切缝作业，纵向缩缝要平行于线路中心线。

B、纵向施工缝：纵向施工缝要平行于线路中心，采用涂沥青进行保护。

C、横向缩缝：横向缩缝要和线路中心垂直，采用切缝法进行施工，在砼的强度达到设计强度的25%~30%时进行切缝作业。

D、胀缝：胀缝要和线路中心垂直，胀缝的宽度必须一致，上部浇注填缝料，下部设置胀缝板。多车道胀缝要作成一条连续缝。

E、横向施工缝：横向施工缝的设置要按照有关的规定进行设置，一般要求横向施工缝要和胀缝和缩缝设计位置吻合，与线路中心 垂直。对于多车道路面的施工缝要设置在一个断面上。

F、填缝：所有的接风均要按照规定进行缝的填料施工。（4）施工注意事项

①当室外温度连续5 天低于5℃时，水泥砼板要按照冬季进行施工组织；当砼的温度在30℃~35℃时，要按照夏季进行施工组 织。

②砼的试验取样要严格按照有关的规定进行取样，养生条件要与现场砼的条件相同。

③完工的砼路面要进行必要的检查，其标准要达到规定的要求，不符和规定时要进行砼的移除及更换。

④完工以后的路面边线直顺，曲线满足设计的要求。



中创合信设计集团有限公司

ZHONGCHUANG HEXIN DESIGN GROUP CO., LTD

资质证书编号：A352012626

市政行业、建筑行业乙级资质

风景园林、照明工程、幕墙、环境工程乙级

图纸专业章：

注册执业章:

备注:

- 1.本图纸若未加盖本院出图资质章，则属无效图纸，本院不予承认，并禁止在施工中使用。
- 2.本图纸中，若出现使用笔（刀）具在重图上直接进行篡改、涂改的行为，均不是本院设计人员所为，本院不予负责。
- 3.本院都有本图纸的法定知识产权，任何单位或个人未经授权不得使用本图纸（包括电子文件）进行施工，或进行套用、复制、传播、出版。
- 4.本图纸须经相关部门审查或审批通过后方可实施。
- 5.本院都有本图纸的最终解释权。

工程名称:

五星村风帆运动训练基地交通配套设施及餐饮业态提升项目（交通配套设施项目）

建设单位:


平潭县君山镇五星村村民委员会

审 定	罗 浩	罗浩
工程负责人	李 擎	李擎
专业负责人	张 聪	张聪
审 核	李 擎	李擎
校 对	罗 浩	罗浩
设 计	张 聪	张聪
制 图	张 聪	张聪

图名：

设计说明

工程编号	
图 别	园 建
图 号	ST-01
日 期	2024.06

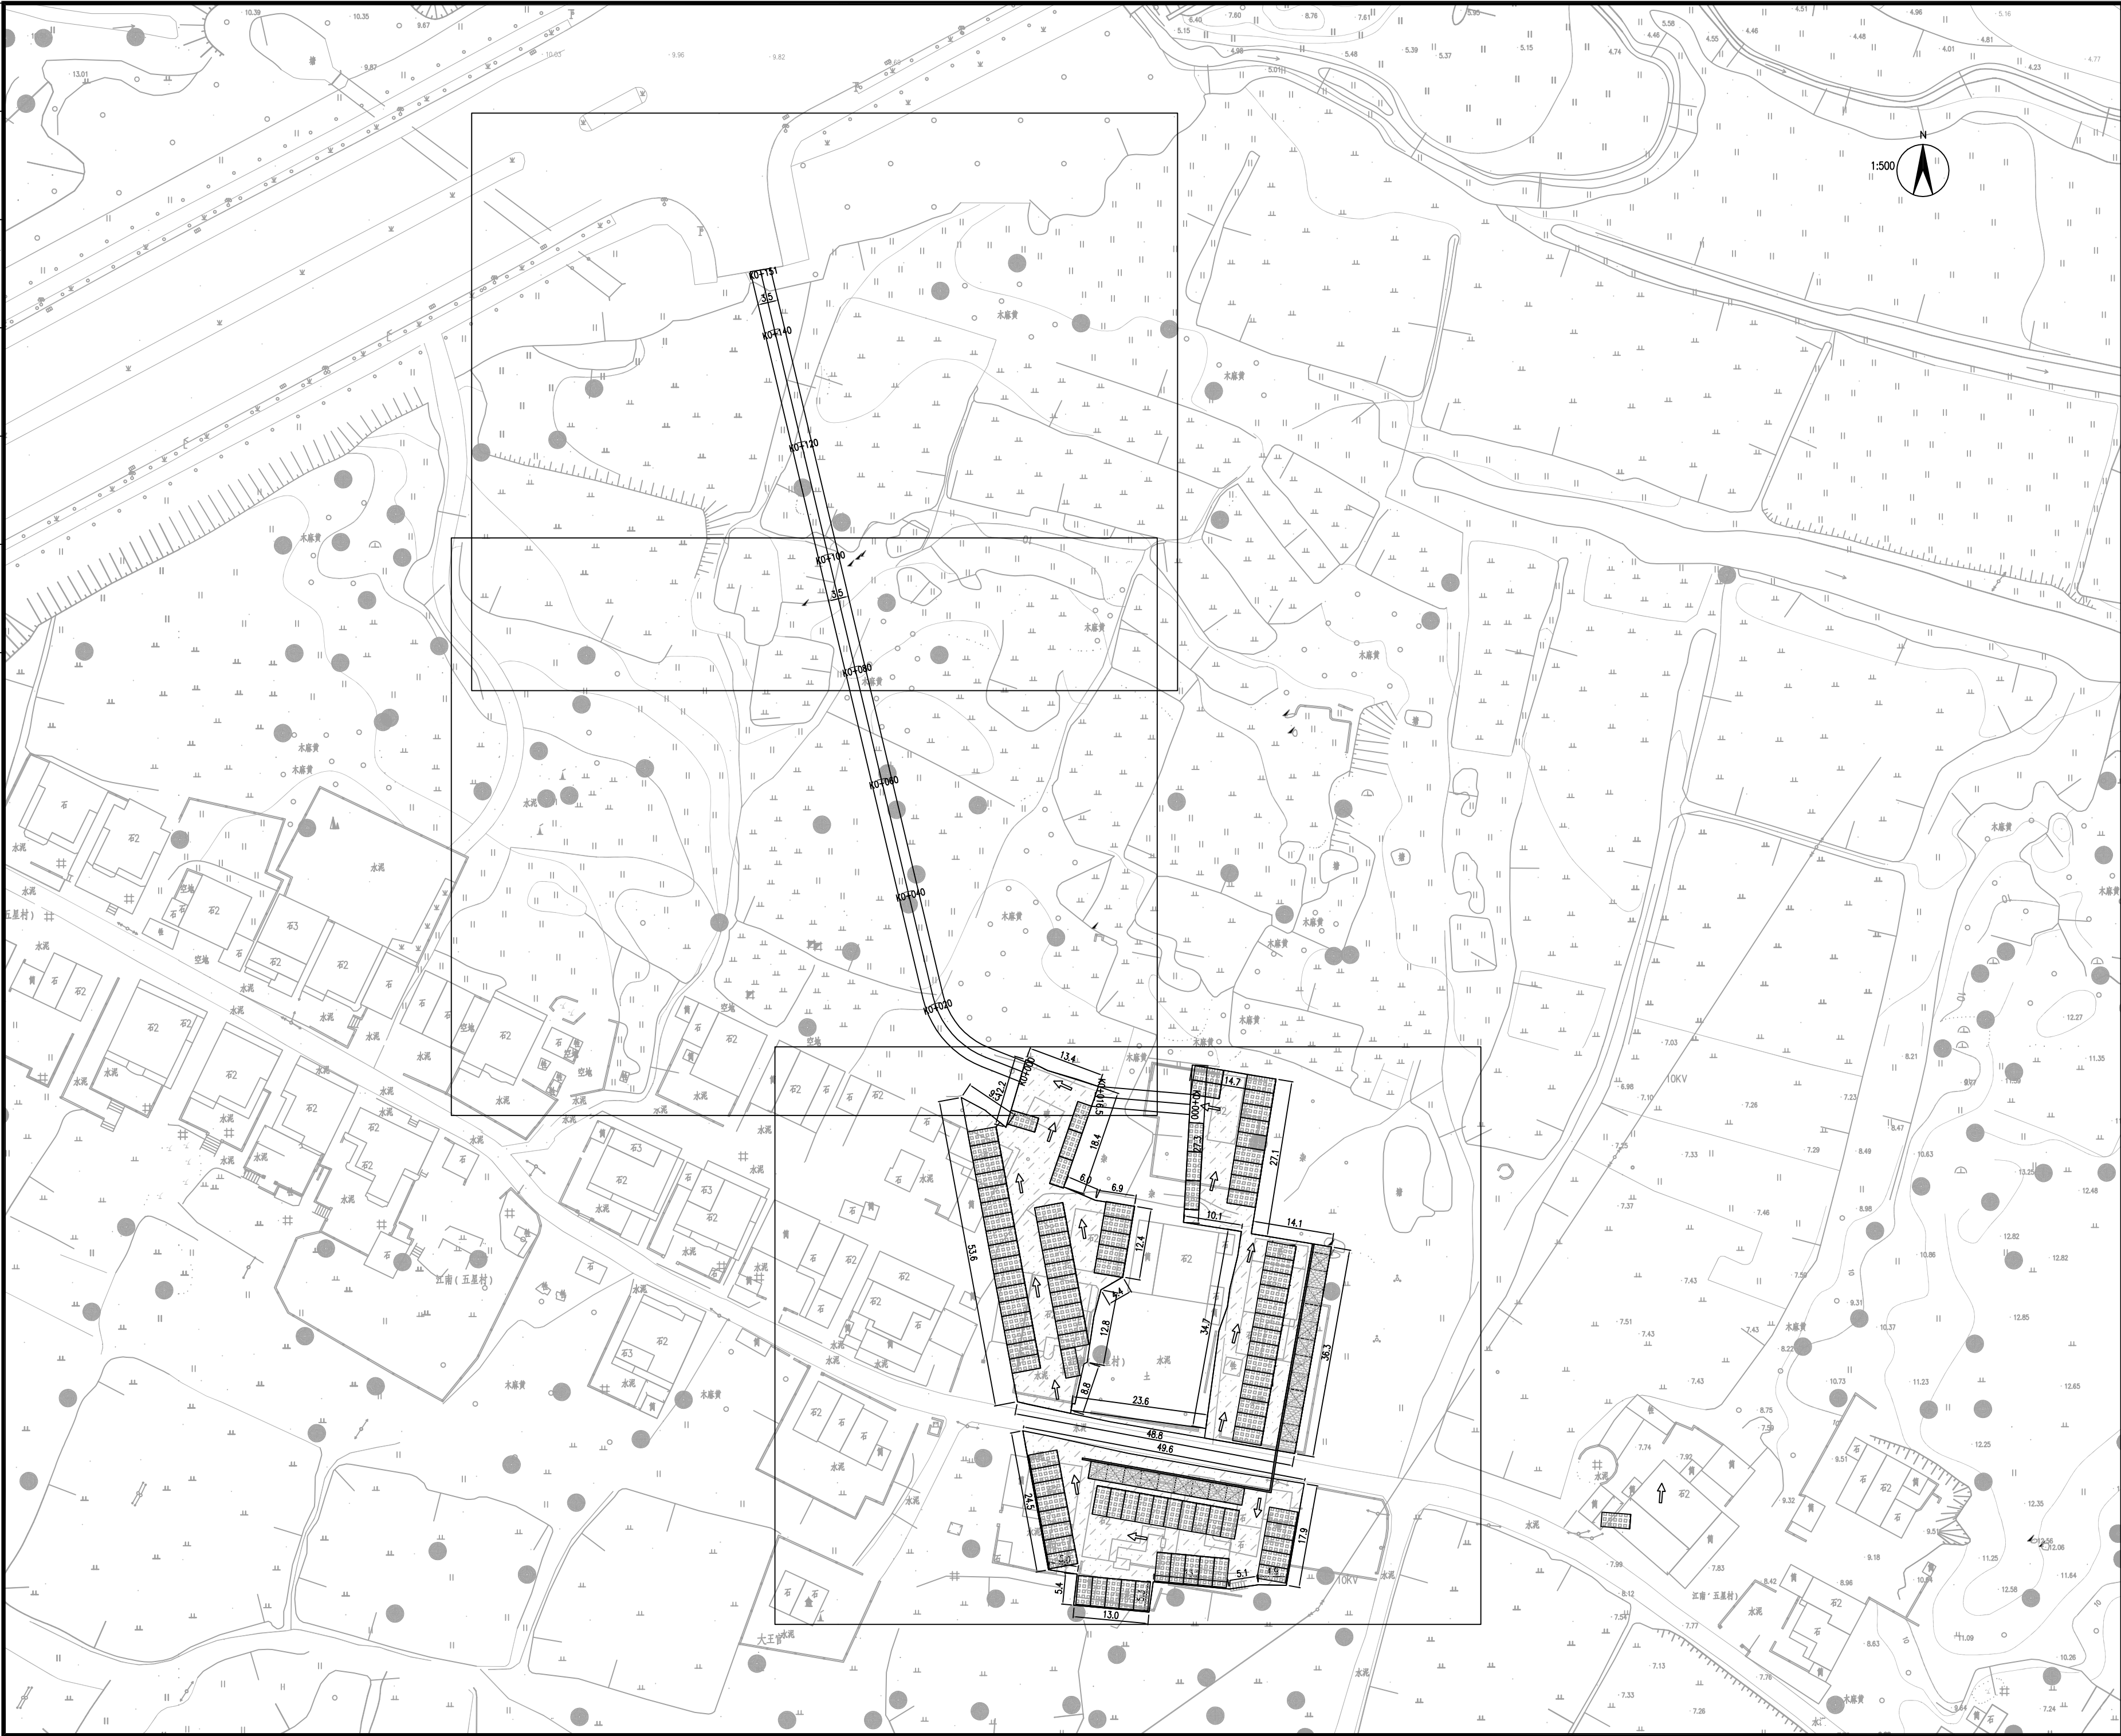[illegible]

中创合信设计集团有限公司

ZHONGCHUANG HEXIN DESIGN GROUP CO., LTD

资质证书编号：A352012626

市政行业、建筑行业乙级资质

风景园林、照明工程、幕墙、环境工程乙级

图纸专业章:

注册执业章:

备注:

- 1.本图纸若未加盖本院出图章者,属无效图纸,本院不予承认,并禁止在施工中使用
2.本图纸中,若由现场用笔(刀)直接在图上直接进行涂改、涂饰的行为,均不是本院设计人员所为,本院不予负责。
3.本院拥有本图纸的法定知识产权,任何单位或个人未经授权不得使用本图纸(包括电子文件)进行施工、或进行套用、复制、传播、出版。
4.本图纸须经相关部门审查审批通过后方可实施。
5.本院拥有本图纸的最终解释权。

工程名称:

五星村风帆运动训练基地交通配套设施及
餐饮业态提升项目（交通配套设施项目）

建设单位:

平潭县君山镇五星村村民委员会

审 定	罗 浩	罗浩
工程负责人	李 擎	李擎
专业负责人	张 聪	张聪
审 核	李 擎	李擎
校 对	罗 浩	罗浩
设 计	张 聪	张聪
制 图	张 聪	张聪

图名:

总平面图

工程编号	
图 别	园 建
图 号	ST-02
日 期	2024.06

专业名称	道路工程
专业名称	给排水工程
专业名称	电气工程
专业名称	暖通工程
专业名称	结构工程
专业名称	建筑专业



中创合信设计集团有限公司

ZHONGCHUANG HEXIN DESIGN GROUP CO., LTD

资质证书编号：A352012626

市政行业、建筑行业乙级资质

风景园林、照明工程、幕墙、环境工程乙级

图纸专业章：

注册执业章：

备注：

- 1.本图纸若未加盖本院出图章，则属无效图纸，本院不予承认，并禁止在施工中使用。
- 2.本图纸中，若出现使用笔（刀）具在重图上直接进行修改，涂改的行为，均不是本院设计人员所为，本院不予负责。
- 3.本院拥有本图纸的法定知识产权，任何单位或个人未经授权不得使用本图纸（包括电子文件）进行施工，或进行复制、复制、传播、出版。
- 4.本图纸须经相关部门审查或审批通过后方可实施。
- 5.本院拥有本图纸的最终解释权。

工程名称：

五星村风帆运动训练基地交通配套设施及
餐饮业态提升项目（交通配套设施项目）

建设单位：

平潭县君山镇五星村村民委员会

审 定	罗 浩	罗浩
工程负责人	李 擎	李擎
专业负责人	张 聪	张聪
审 核	李 擎	李擎
校 对	罗 浩	罗浩
设 计	张 聪	张聪
制 图	张 聪	张聪

图名：

场地平整平面图

工程编号	
图 别	园 建
图 号	ST-03
日 期	2024.06

工程名称	五星村风帆运动训练基地交通配套设施及餐饮业态提升项目
建设单位	平潭县君山镇五星村村民委员会
设计单位	中创合信设计集团有限公司
项目负责人	李擎
专业负责人	张聪
审核人	李擎
校对人	罗浩
设计人	张聪
制图人	张聪
日期	2024.06





中创合信设计集团有限公司
ZHONGCHUAN HEXIN DESIGN GROUP CO., LTD
资质证书编号: A352012626
市政行业、建筑行业乙级资质
风景园林、照明工程、幕墙、环境工程乙级
图纸专业章:

注册执业章:

备注:

- 1.本图纸若未加盖本院出图章,则属无效图纸,本院不予承认,并禁止在施工中使用。
- 2.本图纸中,若出现使用笔(刀)具在重图上直接进行修改、涂改的行为,均不是本院设计人员所为,本院不予负责。
- 3.本院拥有本图纸的知识产权,任何单位或个人未经授权不得使用本图纸(包括电子文件)进行施工,或进行复制、传播、出版。
- 4.本图纸须经相关部门审查或审批通过后方可实施。
- 5.本院拥有本图纸的最终解释权。

工程名称:
五星村风帆运动训练基地交通配套设施及餐饮业态提升项目(交通配套设施项目)

建设单位:
平潭县君山镇五星村村民委员会

审 定	罗 浩	罗浩
工程负责人	李 擎	李擎
专业负责人	张 聪	张聪
审 核	李 擎	李擎
校 对	罗 浩	罗浩
设 计	张 聪	张聪
制 图	张 聪	张聪

图名:
场地平整平面图

工程编号	
图 别	园 建
图 号	ST-03
日 期	2024.06

规划	道路	名称	备注
市政	给水	名称	备注
电气	排水	名称	备注
暖通	采暖	名称	备注
结构	建筑	名称	备注



中创合信设计集团有限公司

ZHONGCHUANG HEXIN DESIGN GROUP CO., LTD

资质证书编号: A352012626

市政行业、建筑行业乙级资质

风景园林、照明工程、幕墙、环境工程乙级

图纸专业章:

注册执业章:

备注:

- 1.本图纸若未加盖本院出图章,则属无效图纸,本院不予承认,并禁止在施工中使用。
- 2.本图纸中,若出现使用笔(刀)具在蓝图上直接进行修改、涂改的行为,均不是本院设计人员所为,本院不予负责。
- 3.本院拥有本图纸的知识产权,任何单位或个人未经授权不得使用本图纸(包括电子文件)进行施工,或进行复制、修改、传播、出版。
- 4.本图纸须经相关部门审查或审批通过后方可实施。
- 5.本院拥有本图纸的最终解释权。

工程名称:

五星村风帆运动训练基地交通配套设施及
餐饮业态提升项目(交通配套设施项目)

建设单位:

平潭县山山镇五星村村民委员会

审 定	罗 浩	罗浩
工程负责人	李 擎	李擎
专业负责人	张 聪	张聪
审 核	李 擎	李擎
校 对	罗 浩	罗浩
设 计	张 聪	张聪
制 图	张 聪	张聪

图名:

平面设计图

工程编号	
图 别	园 建
图 号	ST-04
日 期	2024.06

[illegible]

中创合信设计集团有限公司

ZHONGCHUANG HEXIN DESIGN GROUP CO., LTD

资质证书编号: A352012626

市政行业、建筑行业乙级资质

风景园林、照明工程、幕墙、环境工程乙级

图纸专业章:

注册执业章:

备注:

- 1.本图纸若未加盖本学院出图章者, 则属无效图纸, 本学院不予承认, 并禁止在施工现场使用。
- 2.本图纸中, 若出现使用(刀)具在本图上直接进行划线、涂改的行为, 均不是本学院设计人员所为, 本学院不负责。
- 3.本学院拥有本图纸的法定知识产权, 任何单位或个人未经授权不得使用本图纸(包括电子文件)进行施工、或进行复制、复制、传播、出版。
- 4.本图纸须经相关部门审查或审批通过后方可实施。
- 5.本学院拥有本图纸的最终解释权。

工程名称:

五星村风帆运动训练基地交通配套设施及
餐饮业态提升项目(交通配套设施项目)

建设单位:

平潭县君山镇五星村村民委员会

审 定	罗 浩	罗浩
工程负责人	李 擎	李擎
专业负责人	张 聪	张聪
审 核	李 擎	李擎
校 对	罗 浩	罗浩
设 计	张 聪	张聪
制 图	张 聪	张聪

图名:

平面尺寸图

工程编号	
图 别	园 建
图 号	ST-05
日 期	2024.06



市政行业、建筑行业乙级资质

图纸专业章:

注册执业章:

备注:

1. 本图纸若未加盖本院出图资质章, 属属无效图纸, 本院不予承认, 并禁止在施工中使用。
2. 本图纸中, 若出现使用笔(刀)具在蓝图上直接进行涂改、涂擦的行为, 均不是本院设计人员所为, 本院不予负责。
3. 本院都有本图纸的法定知识产权, 任何单位或个人未经授权不得使用本图纸(包括电子文件)进行施工、或进行套图、复制、传播、出版。
4. 本图纸须经相关部门审查或审图通过后方可实施。
5. 本院都有本图纸的最终解释权。

工程名称:

五星村风帆运动训练基地交通配套设施及餐饮业态提升项目(交通配套设施项目)

建设单位:


平潭县君山镇五星村村民委员会

审 定	罗 浩	罗浩
工程负责人	李 擎	李擎
专业负责人	张 聪	张聪
审 核	李 擎	李擎
校 对	罗 浩	罗浩
设 计	张 聪	张聪
制 图	张 聪	张聪

图名:

小车停车位做法详图

工程编号	
图 别	园 建
图 号	ST-07
日 期	2024.06

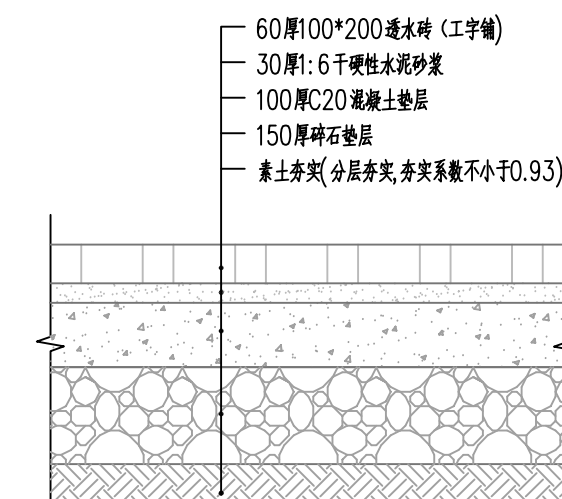

① 小车停车位做法平面图 1:20



② 停车位做法铺装 A-A 剖面图 1:20