

出图专用章

REGISTERED SEAL

注册印章

REGISTERED SEAL

注册执业栏

REGISTERED ARCHITECT/ENGINEER

姓名

NAME

注册印章号

REGISTERED SEAL NO.

注册证书号

REGISTERED CERTIFICATE NO.

建设单位

CLIENT

工程名称

PROJECT TITLE

子项名称

SUB ITEM

项目总负责人

PROJECT NO.

审定

APPROVED BY

审核

AUDIT

专业负责人

DISCIPLINE CHIEF

校对

CHECKED BY

设计

DESIGNED BY

图名

DRAWING TITLE

实践站三楼原始平面

设计号

JOB NO.


图别

TYPE

图号

NO.

注: 所有图纸需经审查机构审查合格后方可施工

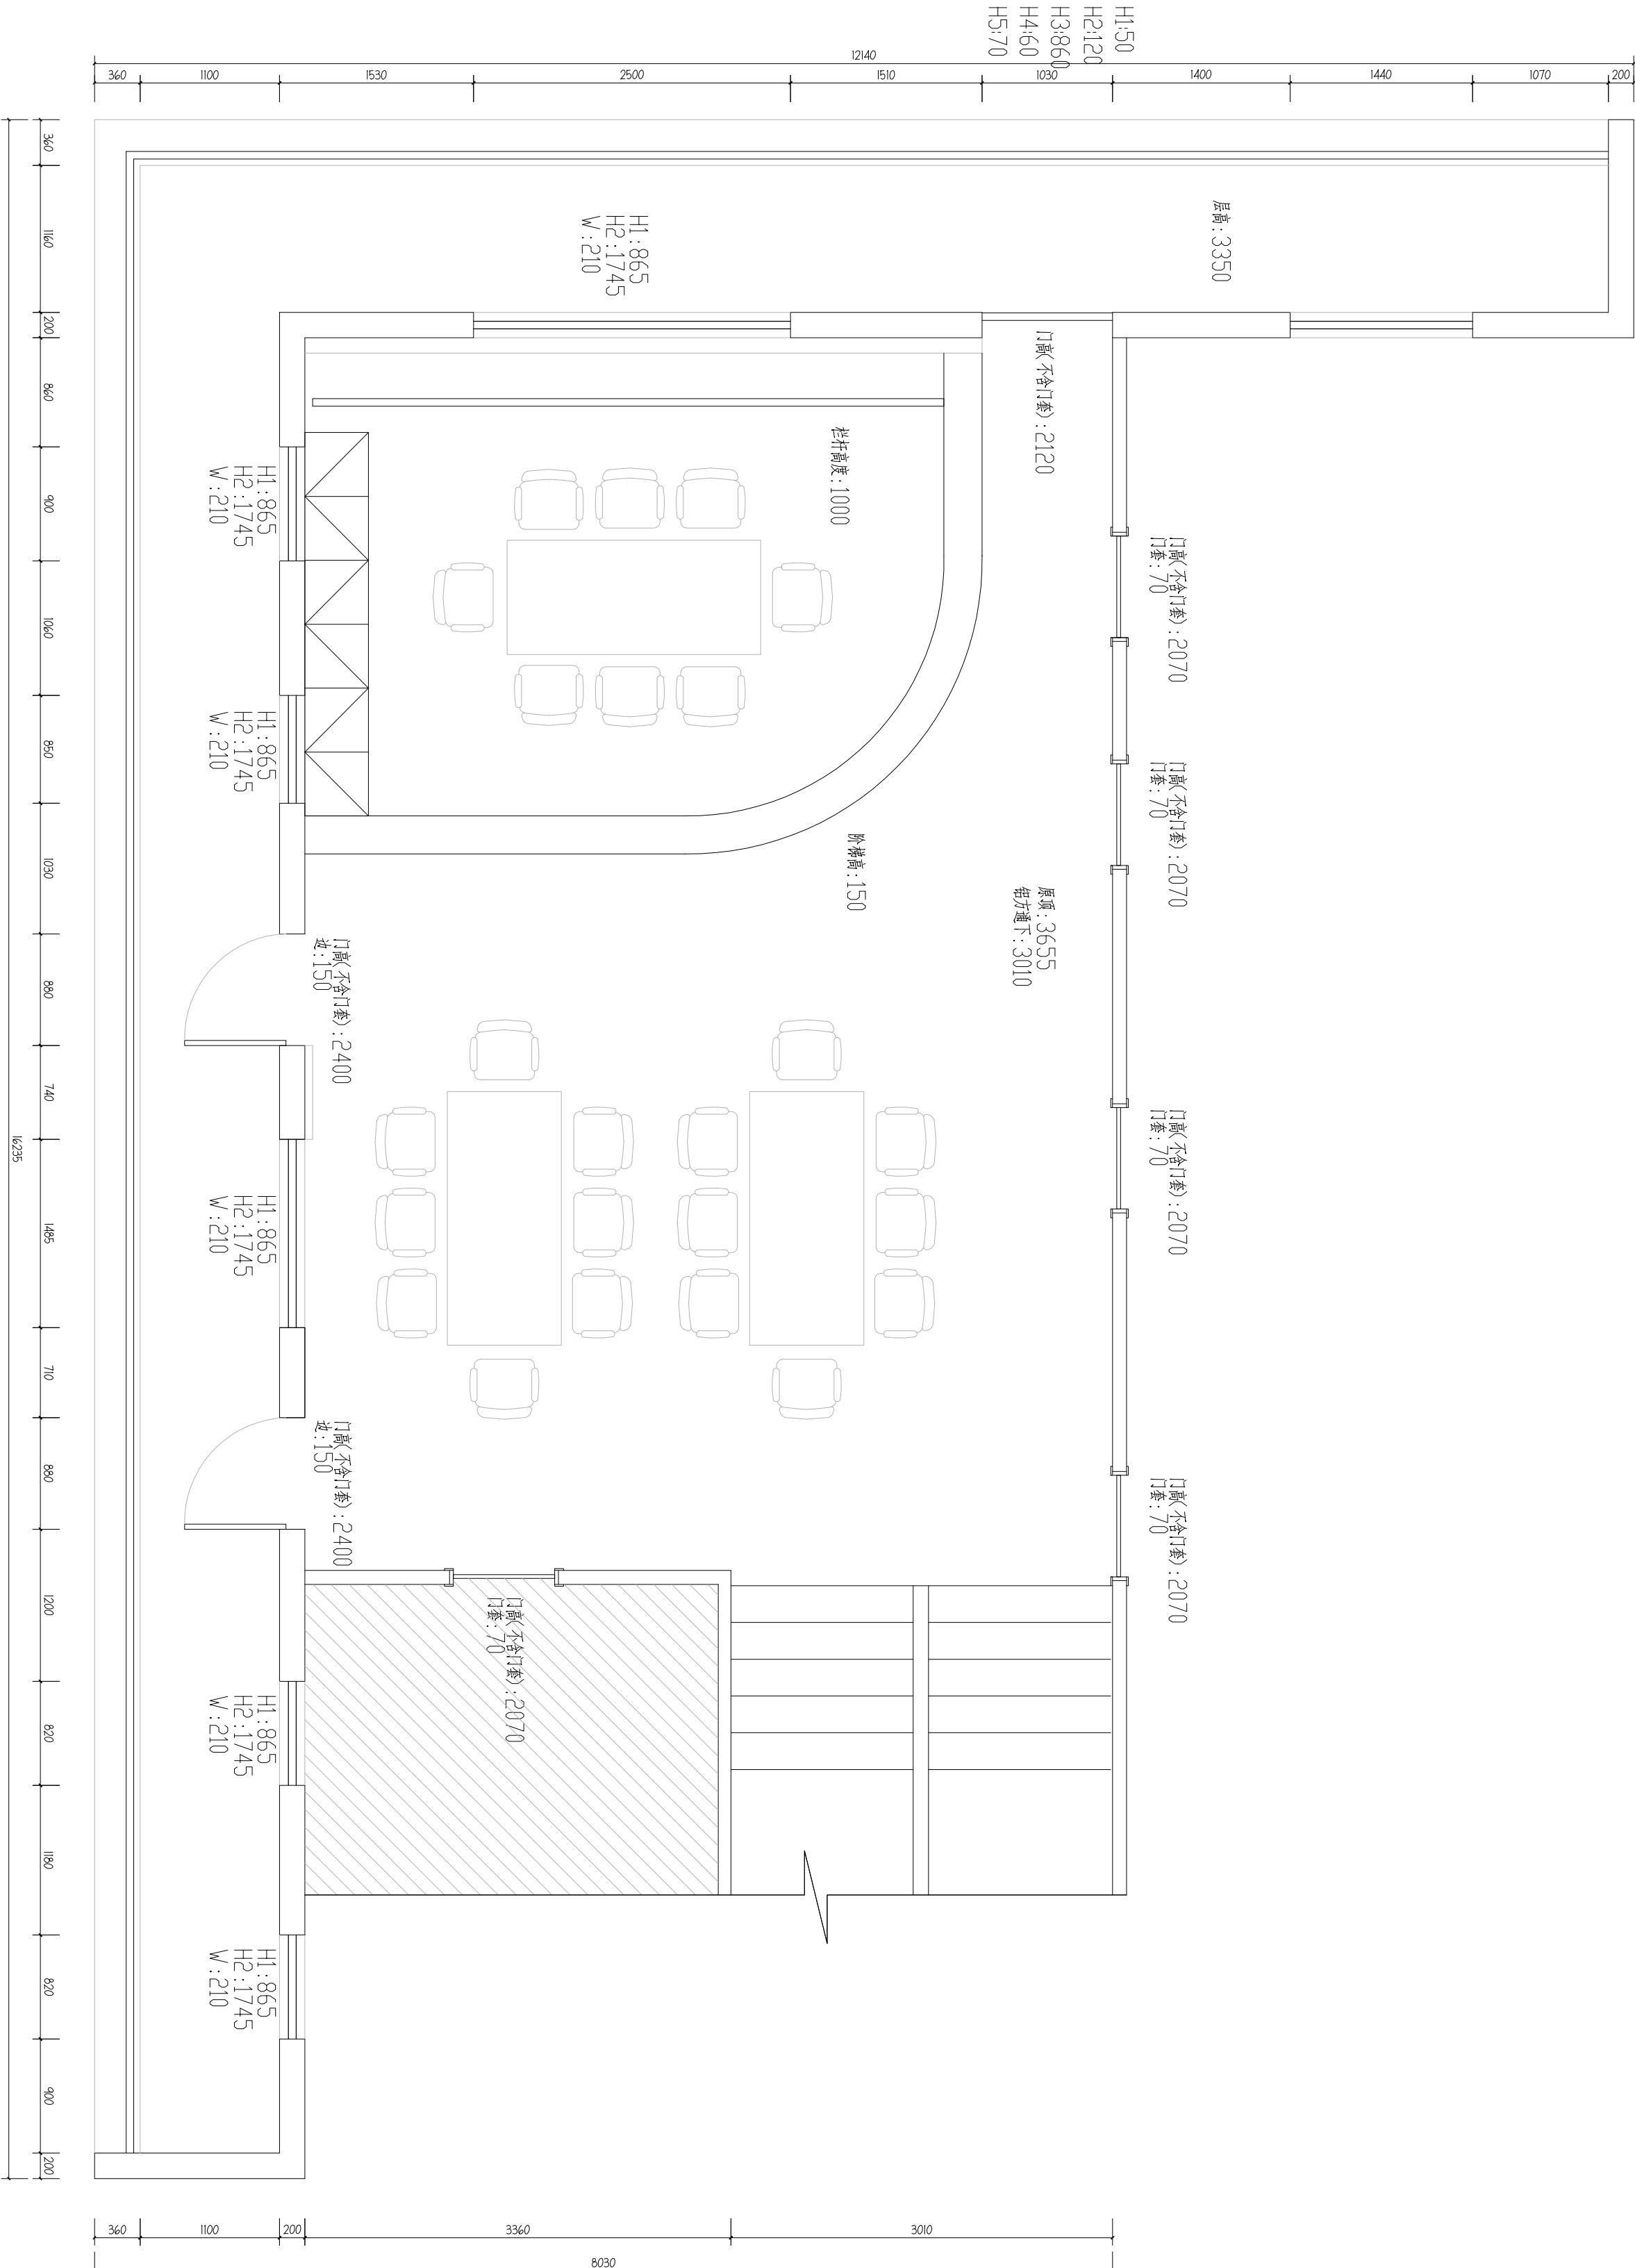

3F

实践站三楼原始平面

SCALE 1:40

EXISTING PLAN

出图专用章 EXISTING SPECIAL SEAL

注册印章 REGISTERED SEAL

注册执业栏
REGISTERED ARCHITECT/ENGINEER

姓名 NAME 注册执业人

注册印章号 REGISTERED SEAL NO. 5103062-001

注册证书号 REGISTERED CERTIFICATE NO. 215000941

建设单位：中懿勘察设计有限公司 CLIENT

工程名称：大坪村示范党群服务中心 PROJECT TITLE

子项名称：SBS ITEM

项目总负责人 PROJECT NO. 邓成

审定 APPROVED BY 徐斌

审核 AUDIT 徐斌

专业负责人 DISCIPLINE CHIEF 邓成

校对 CHECKED BY 邓成


设计 DESIGN BY 邹泉

图名：DESIGN TITLE

实践站三楼原始解构拆除图

设计号 JOB NO.		版本号 VER. NO.	第一版
图例 SYM. CATEGORY	建设	日期 DATE	202408
图号 JOB NO.	JPL 02		


注：所有图纸需经审查机构审查合格后方可施工

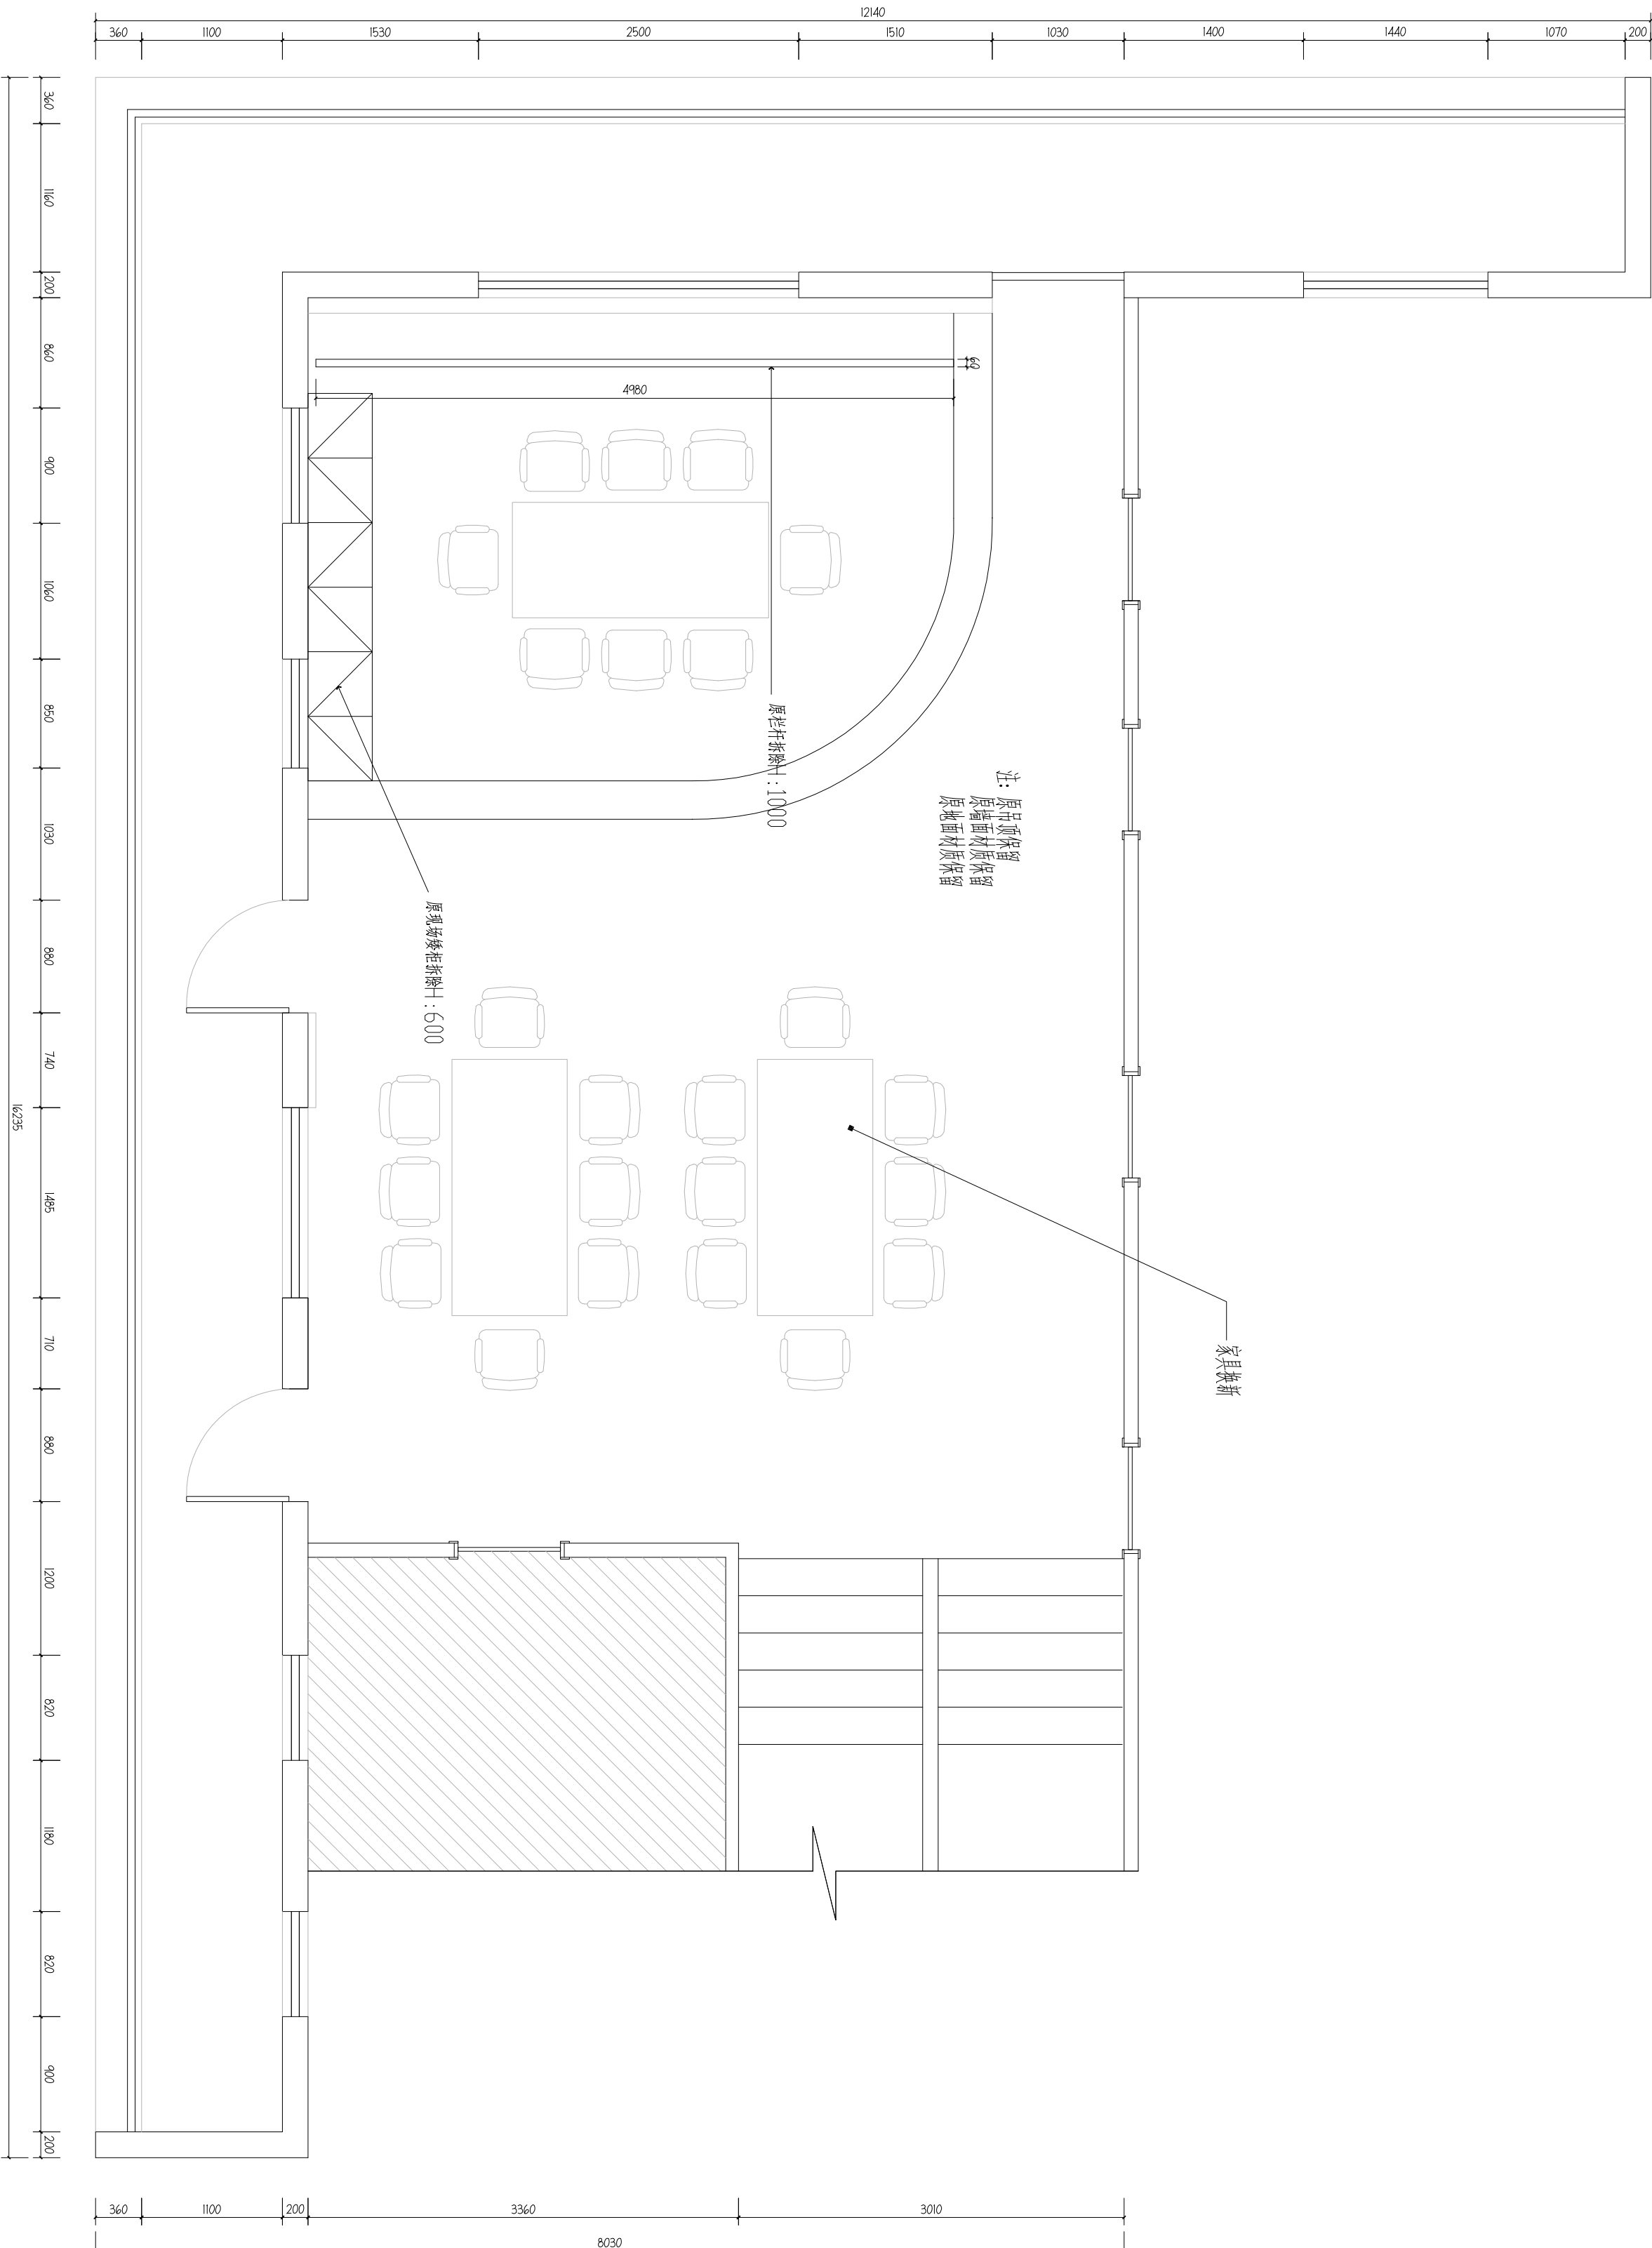

EXISTING PLAN

3F

实践站三楼原始解构拆除图 SCALE 1:40

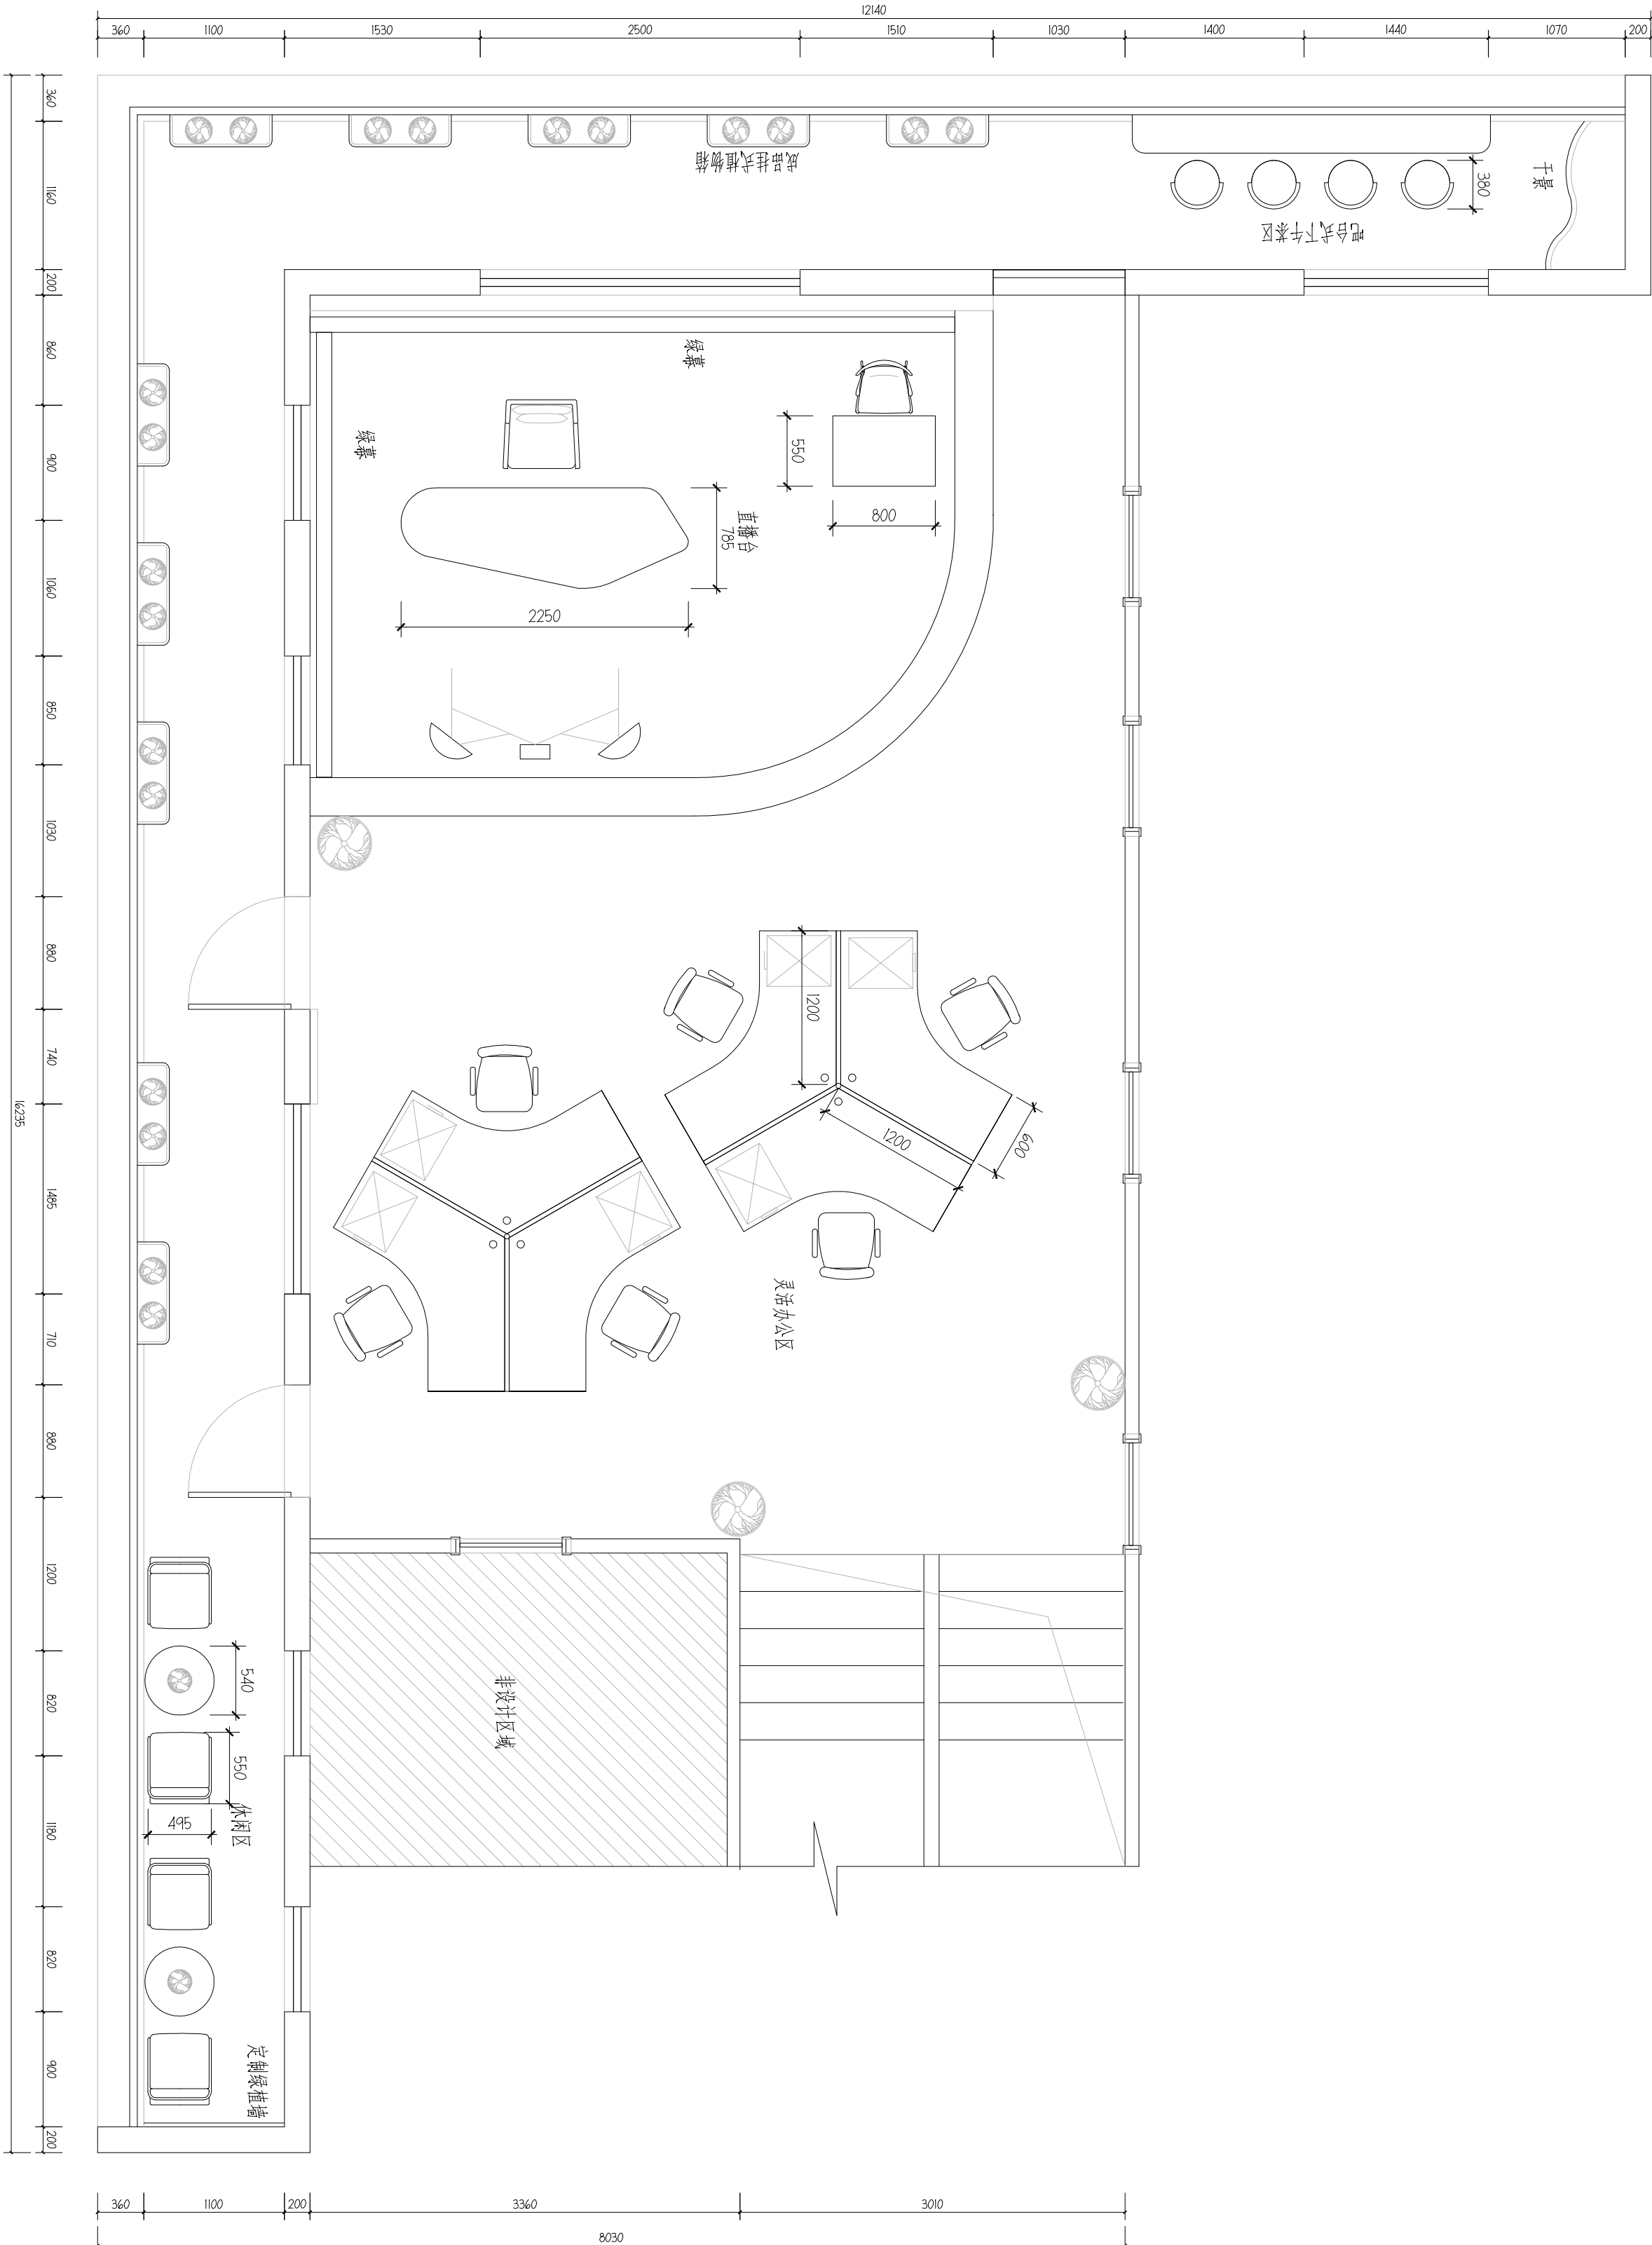


95.5平方米

3F

企业培育中心改后平面图

EXISTING PLAN

SCALE 1:40

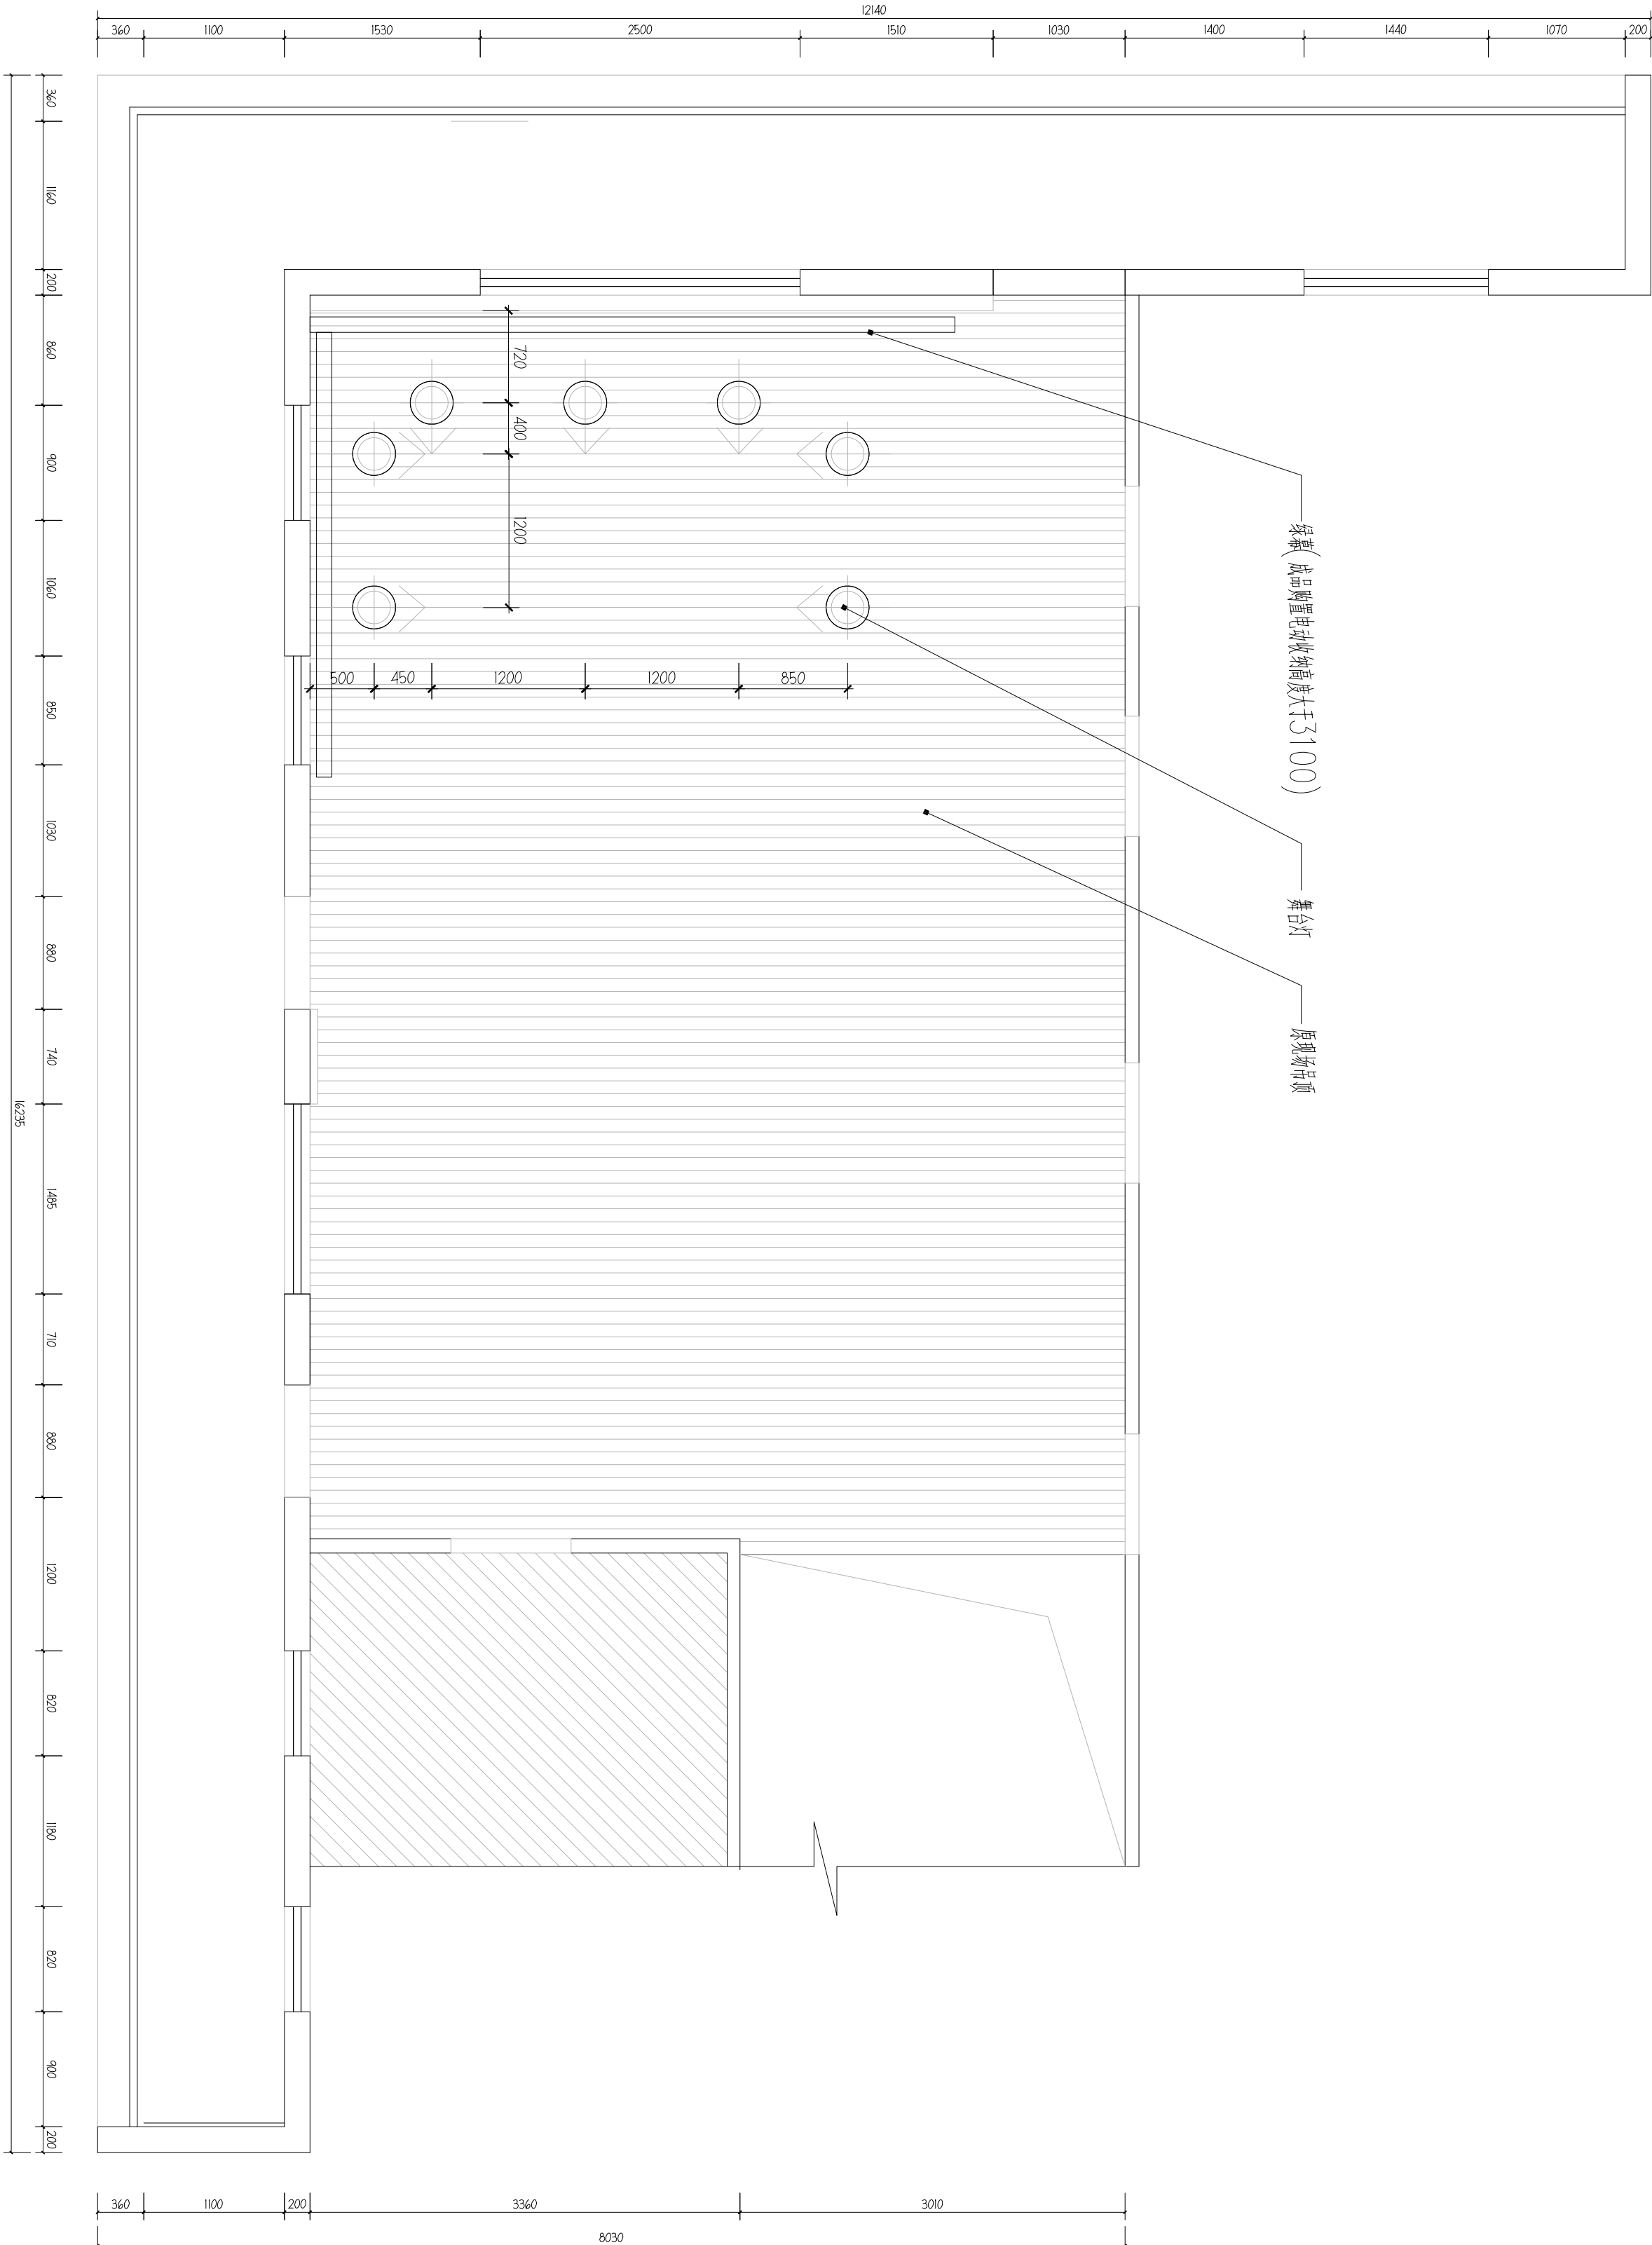



甲级工程设计证书编号: A151030621
乙级工程设计证书编号: A251023438

CASE NOT

DRAWING SPECIAL SEA

REGISTERED SEAL

注册执业栏
REGISTERED ARCHITECT/ENGINEER

234

5103062-00

215000941

墨勘察设计有限公司

PROJECT TITLE

大坪村示范党群服务中心

SUB ITEM

邓成

徐斌

邓 成

邓 成

鄧泉

--	--

图原始楼一楼活动场所组织

建施	版本号
----	-----

日期 DATE

注：所有图纸需经审查机构审查合格后方可施工

注册印章 REGISTERED SEAL

出图专用章

注册印章 REGISTERED SEAL

注册执业栏 REGISTERED ARCHITECT/ENGINEER

姓名 NAME 注册印章号 REGISTERED SEAL NO. 注册证书号 REGISTERED CERTIFICATE NO.

建设单位：中懿勘察设计有限公司 CLIENT

工程名称：大坪村示范党群服务中心 PROJECT TITLE

子项名称：SSB 115M

项目总负责人 PROJECT NO. 邓 成

审 定 APPROVED BY 徐 斌

审 核 AUDIT 邓 成

专业负责人 DISCIPLINE CHIEF 邓 成

校 对 CHECKED BY 邓 成


设 计 DESIGNED BY 邹 泉

图 名：组织活动场所一樓原始解构拆除图 DRAWING TITLE

组织活动场所一樓原始解构拆除图

设计号 JOB NO.		版本号 VER. NO.	第一版
图 则 DRAWING	建施	日期 DATE	202408
图 号 JOB NO.	2PL 02		

注：所有图纸需经审查机构审查合格后方可施工

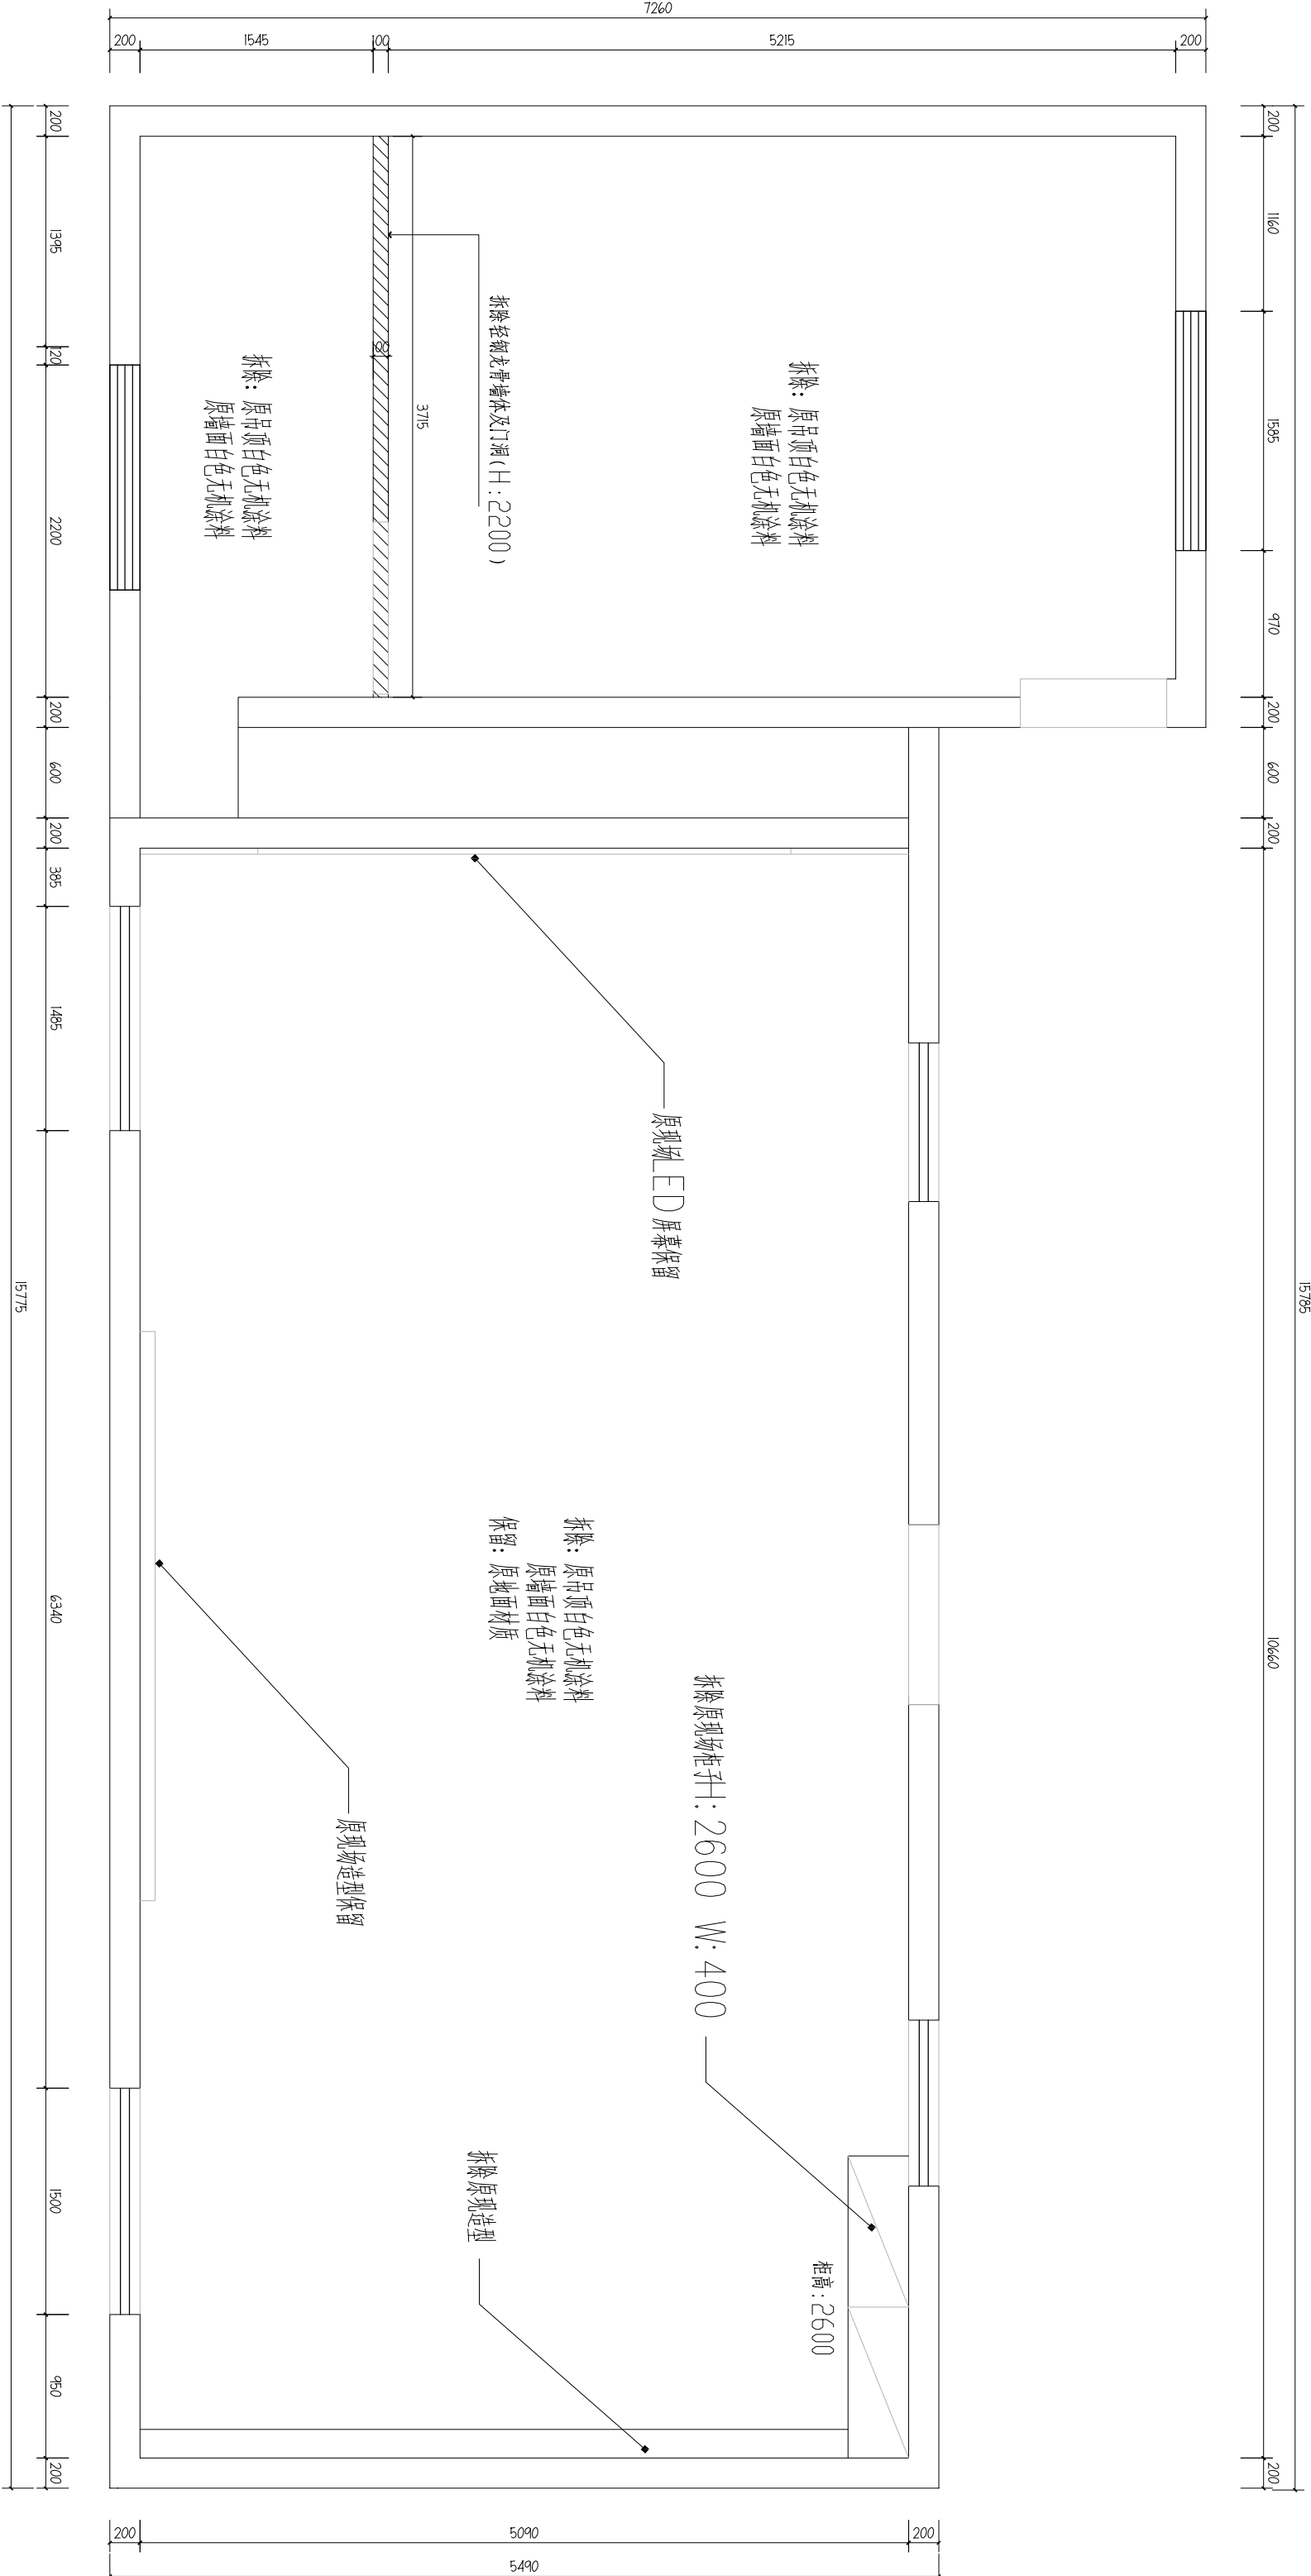

注: 无需拆除部分说明

图例

图示 说明

拆除加气砖墙体

备注: 1. 门洞拆除高度为2200mm, 门宽度估计平面图门尺寸往两边延伸30mm。

2. 现场拆除与平面图功能不符合位置, 根据平面图功能进行拆除。

1F

组织活动场所一樓原始解构拆除图

EXISTING PLAN

SCALE 1:40



甲级工程设计证书编号: A151030621
乙级工程设计证书编号: A251023438

CASE NOTE

DRAWING SPECIAL SEAL

REGISTERED SEAL

注册执业栏
REGISTERED ARCHITECT/ENGINEER

NAME 姓名

5103062-001

215000941

中睦勘察设计有限公司

工程名称:	PROJECT TITLE

大坪村示范党群服务中心

SUB ITEM	子項名稱
	..

项目总负责人	邓威	
PROJECT NO.		

APPROVED BY

徐斌

专业负责人
DISCIPLINE CHIEF

邓成

邓成

校對
CHECKED BY

鄭成

2017/12/1

设计部

圖名: _____



组织活动场所一楼新砌墙体图

设计号 JOB NO.	
----------------	--

图 别 建 施 版 本 号 第 一 版

圖書號 2PL 03 日期 202408

三：所有图纸需经审查机构审查合格后方可施工

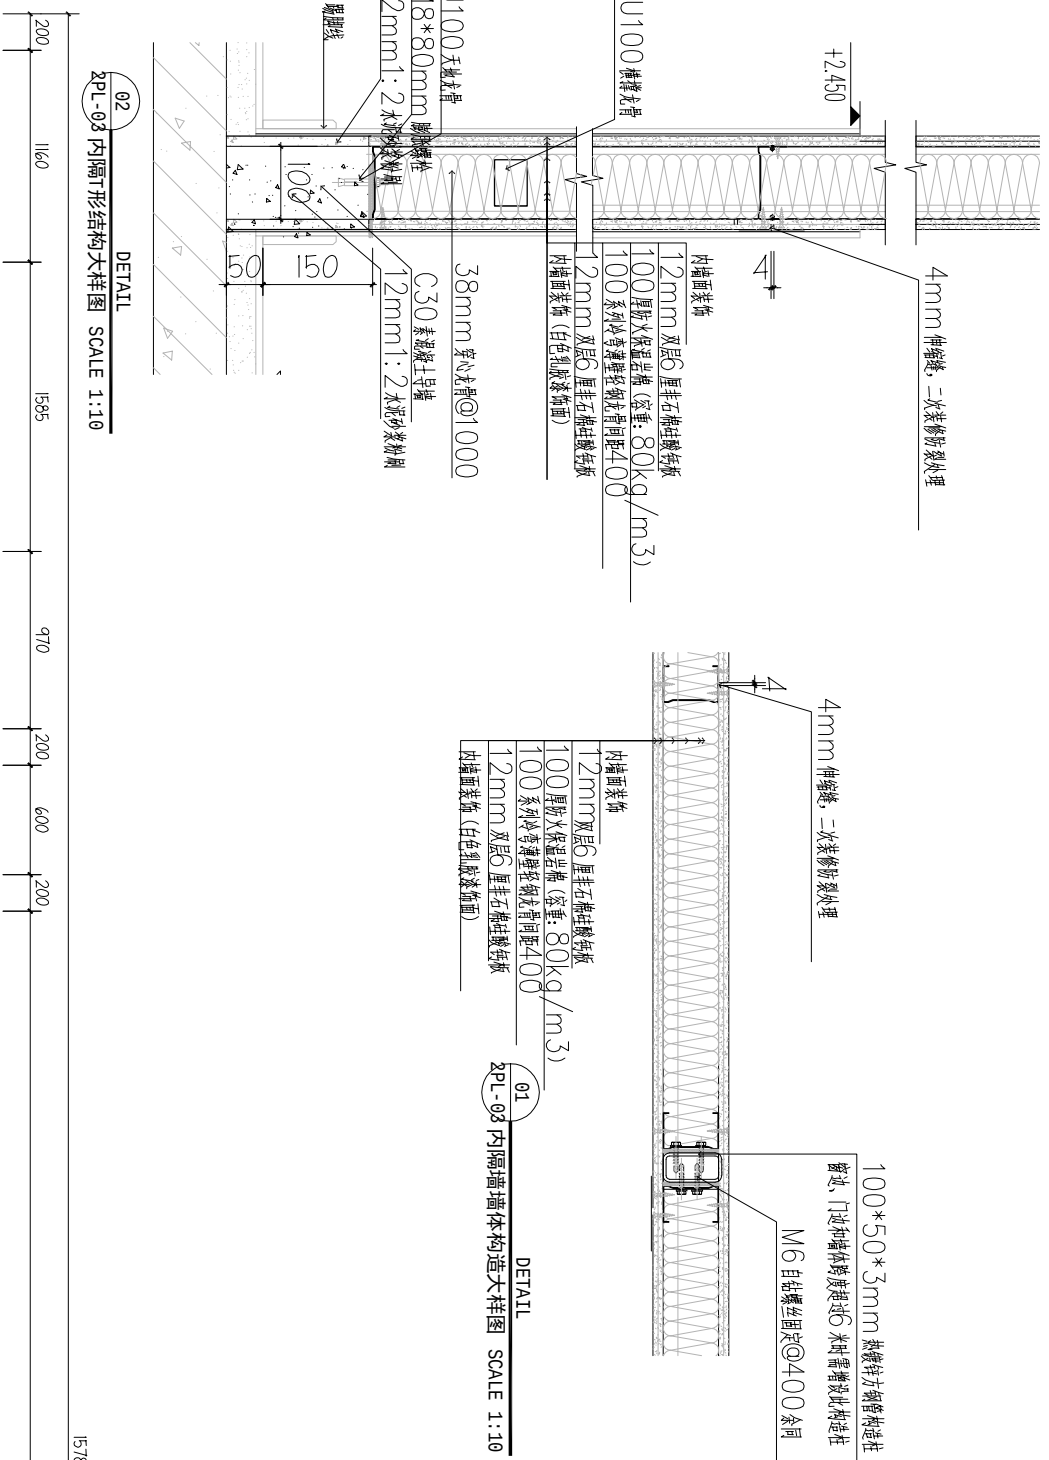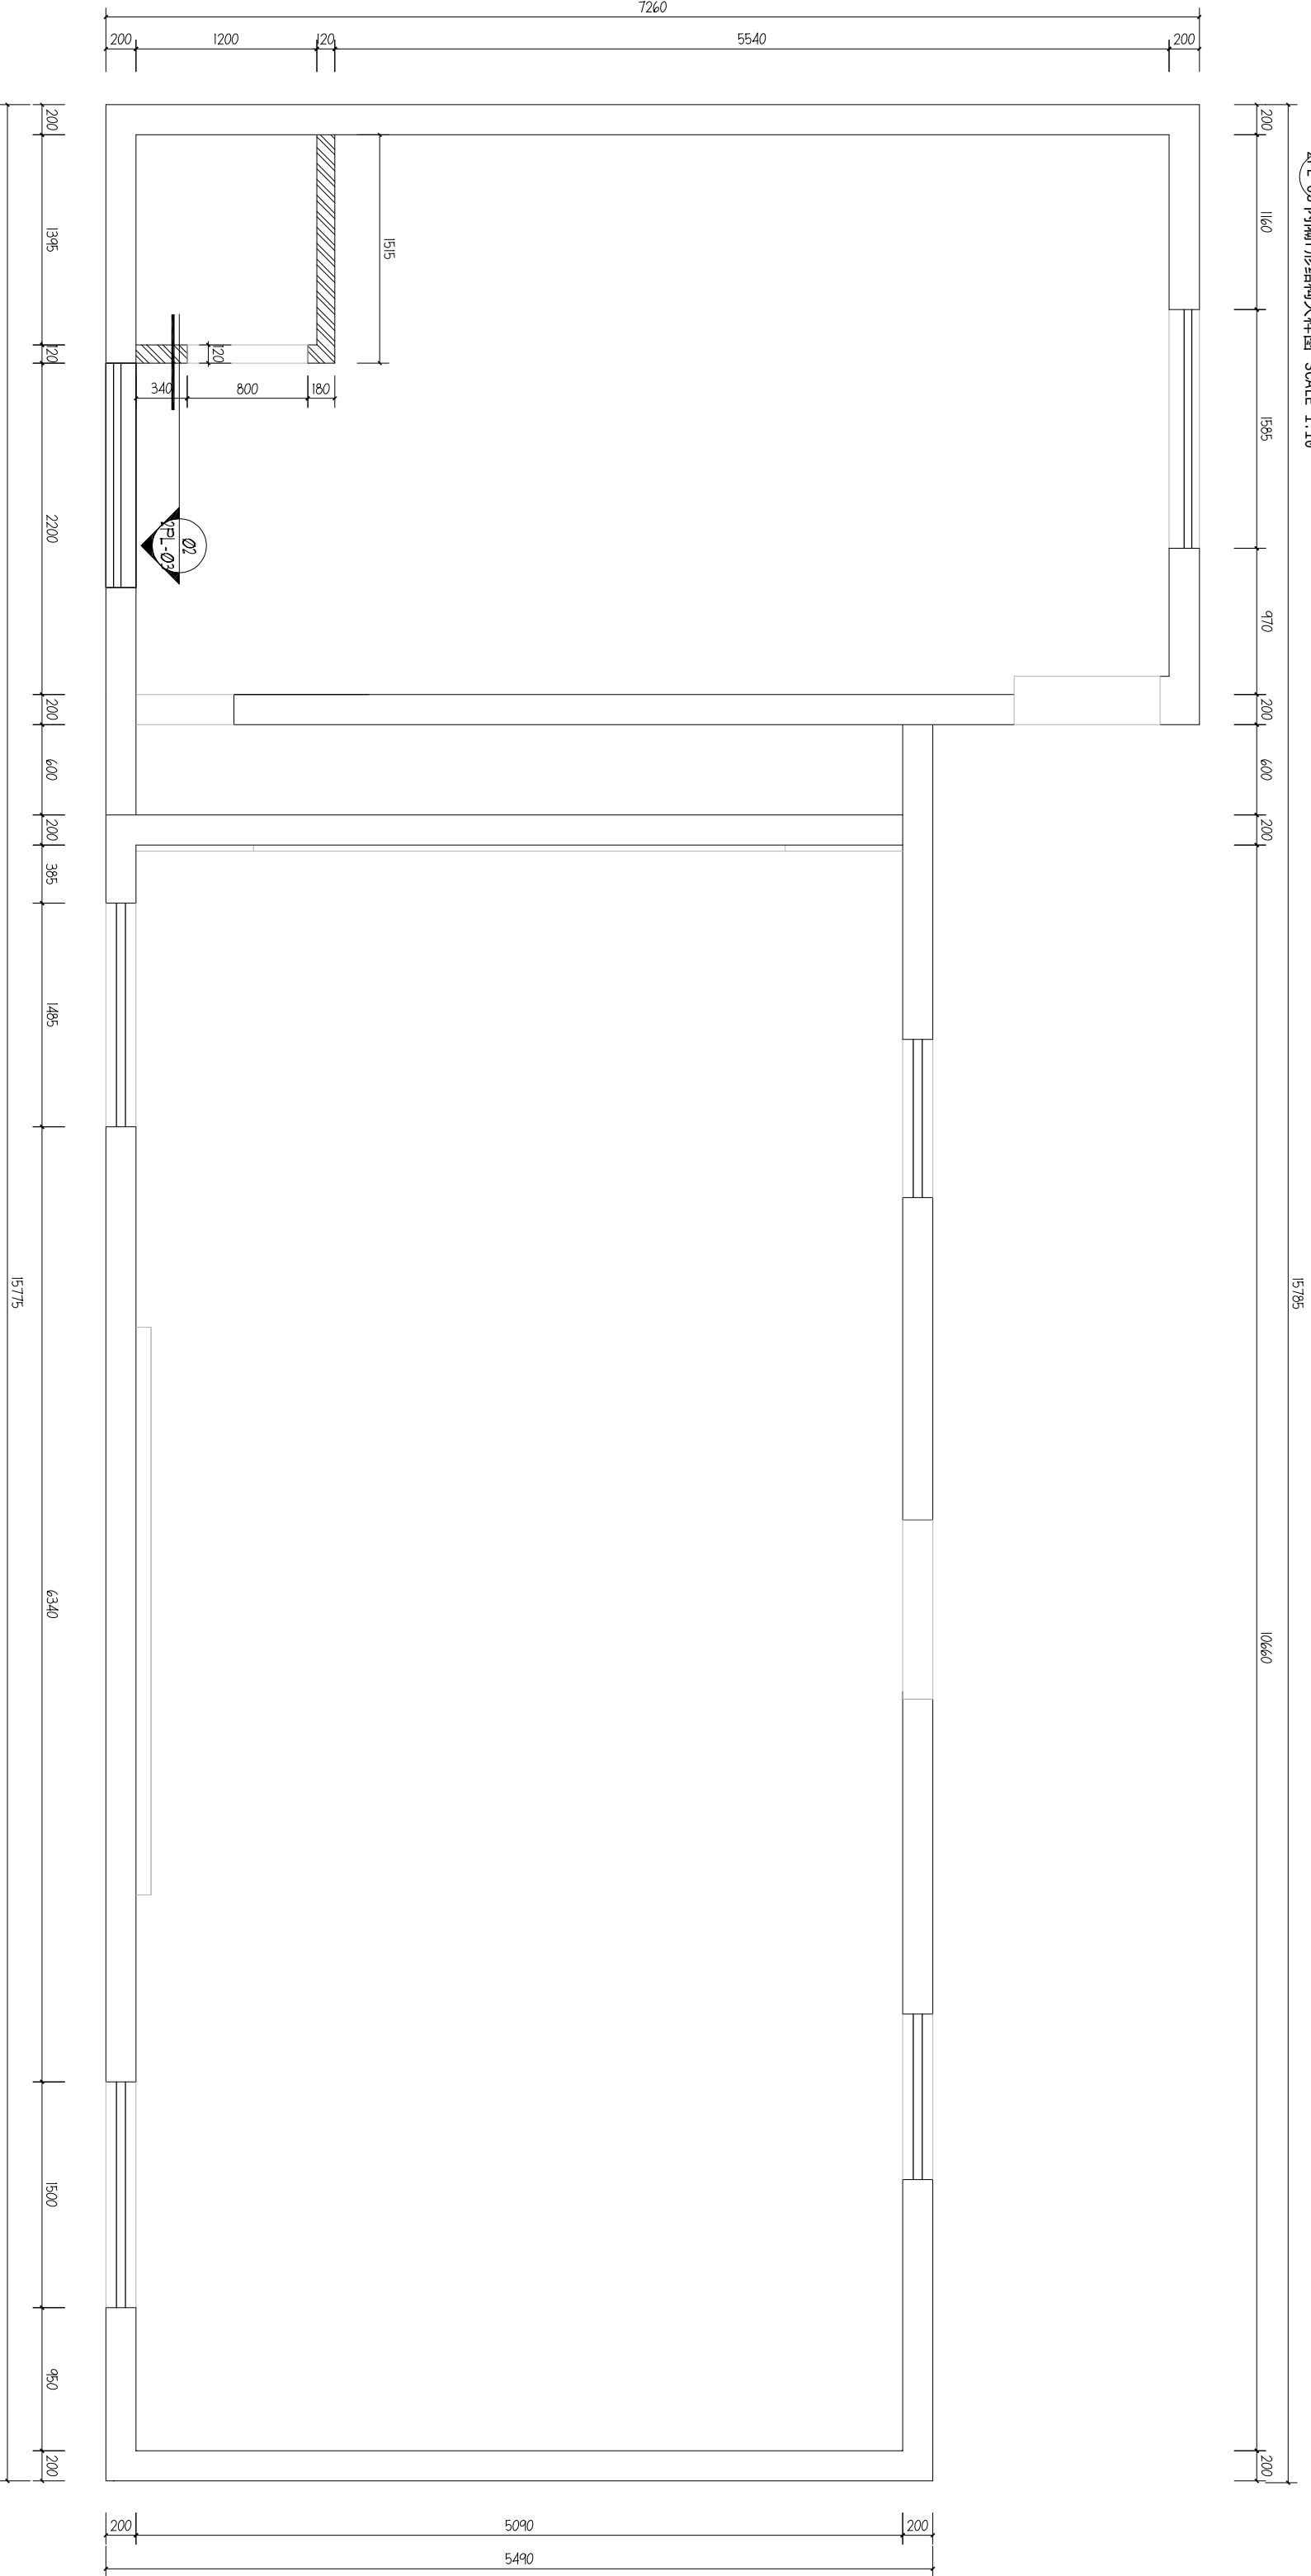

	钢结构构造柱 (热镀锌方钢管 立柱100*100*3mm)
	混凝土
	原建筑墙体
	新砌加气砖墙 (高度285mm)
	底部是200*200/100*100的C20素砼反口
	轻钢龙骨隔墙

注:1、砌体墙的转角处、丁字处、十字交叉处和门窗洞口两侧,墙体长度大于5米处设置构造柱(详参大样图DY-02-GL01)。

2、未特殊标明门洞净高 $\geq 200\text{MM}$ ，宽度见图内尺寸标注


3、新砌加气混凝土砖墙水泥砂浆找平,加气混凝土专用界面剂,挂钢丝网,18厚1:2.5水泥砂浆打底。

4、现场砌墙与平面图功能不符合位置,根据平面图功能进行砌墙。

11

组织活动场所一楼新砌墙体图 SCALE 1:40

EXISTING PLAN

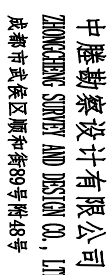

甲级工程设计证书编号: A151030621
乙级工程设计证书编号: A251023438

CASE NOTE

DRAWING SPECIAL SEAL

REGISTERED SEAL

注册执业栏
REGISTERED ARCHITECT/ENGINEER

23

5103062-00

215000941

勘察设计院有限公司

PROJECT TITLE

大坪村示范党群服务中心

SUB TITLE

邓 威

徐斌

邵 威

戚 邨

鄧景


--	--

组织活动场所一楼改后平面

版本号	YJ09-M0
建设	

PL 04 DATE 202408

注: 所有图纸需经审查机构审查合格后方可施工

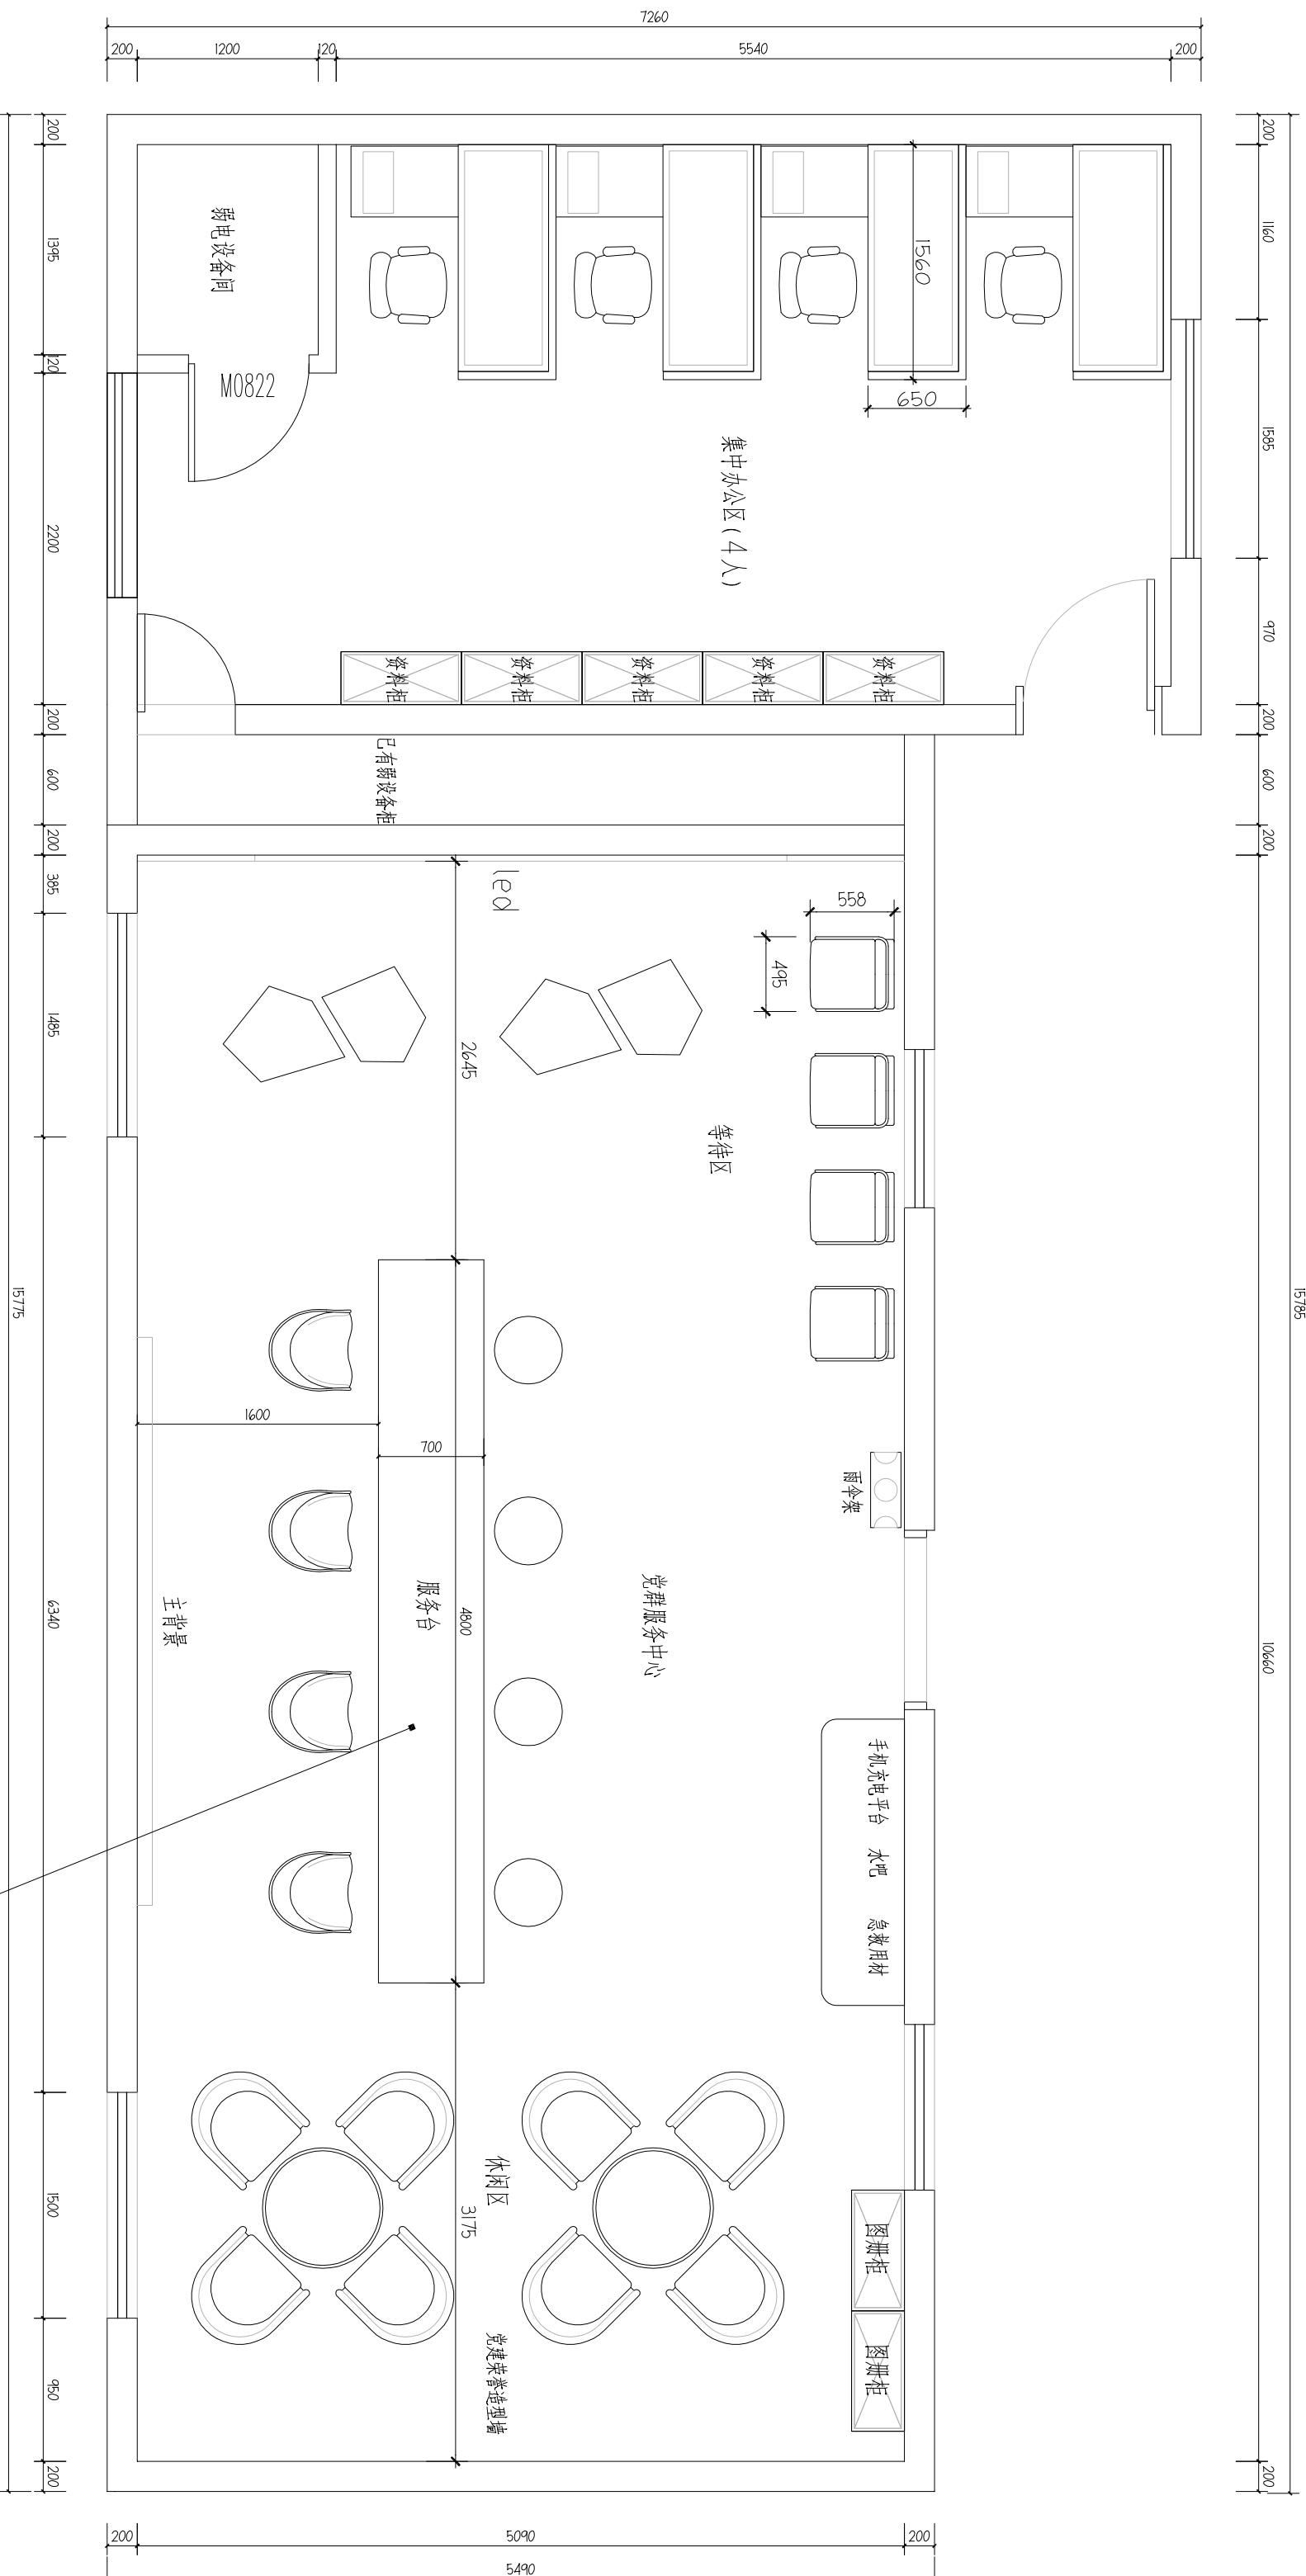

EXISTING PLAN

二

组织活动场所一楼改后平面 SCALE 1:40

注册印章 REGISTERED SEAL

注册印章 REGISTERED SEAL

注册执业栏
REGISTERED ARCHITECT/ENGINEER

姓名 NAME 注册印章号 REGISTERED SEAL NO. 5103062-001

注册证书号 REGISTERED CERTIFICATE NO. 215000941

建设单位：中德勘察设计有限公司

工程名称：大坪村示范党群服务中心

子项名称：SBS 115M

项目总负责人 PROJECT NO. 邓 成

审 定 APPROVED BY 徐 斌

审 核 AUDIT 邓 成

专业负责人 DISCIPLINE CHIEF 邓 成

校 对 CHECKED BY 邹 泉

设 计 DESIGNED BY 邹 泉

图 名：组织活动场所一楼吊顶布置图


设计号 JOB NO.

图 则 DRAWING TITLE

图 号 2PL 05 版本号 第一版

图 号 2PL 05 日期 202408

注：所有图纸需经审查机构审查合格后方可施工

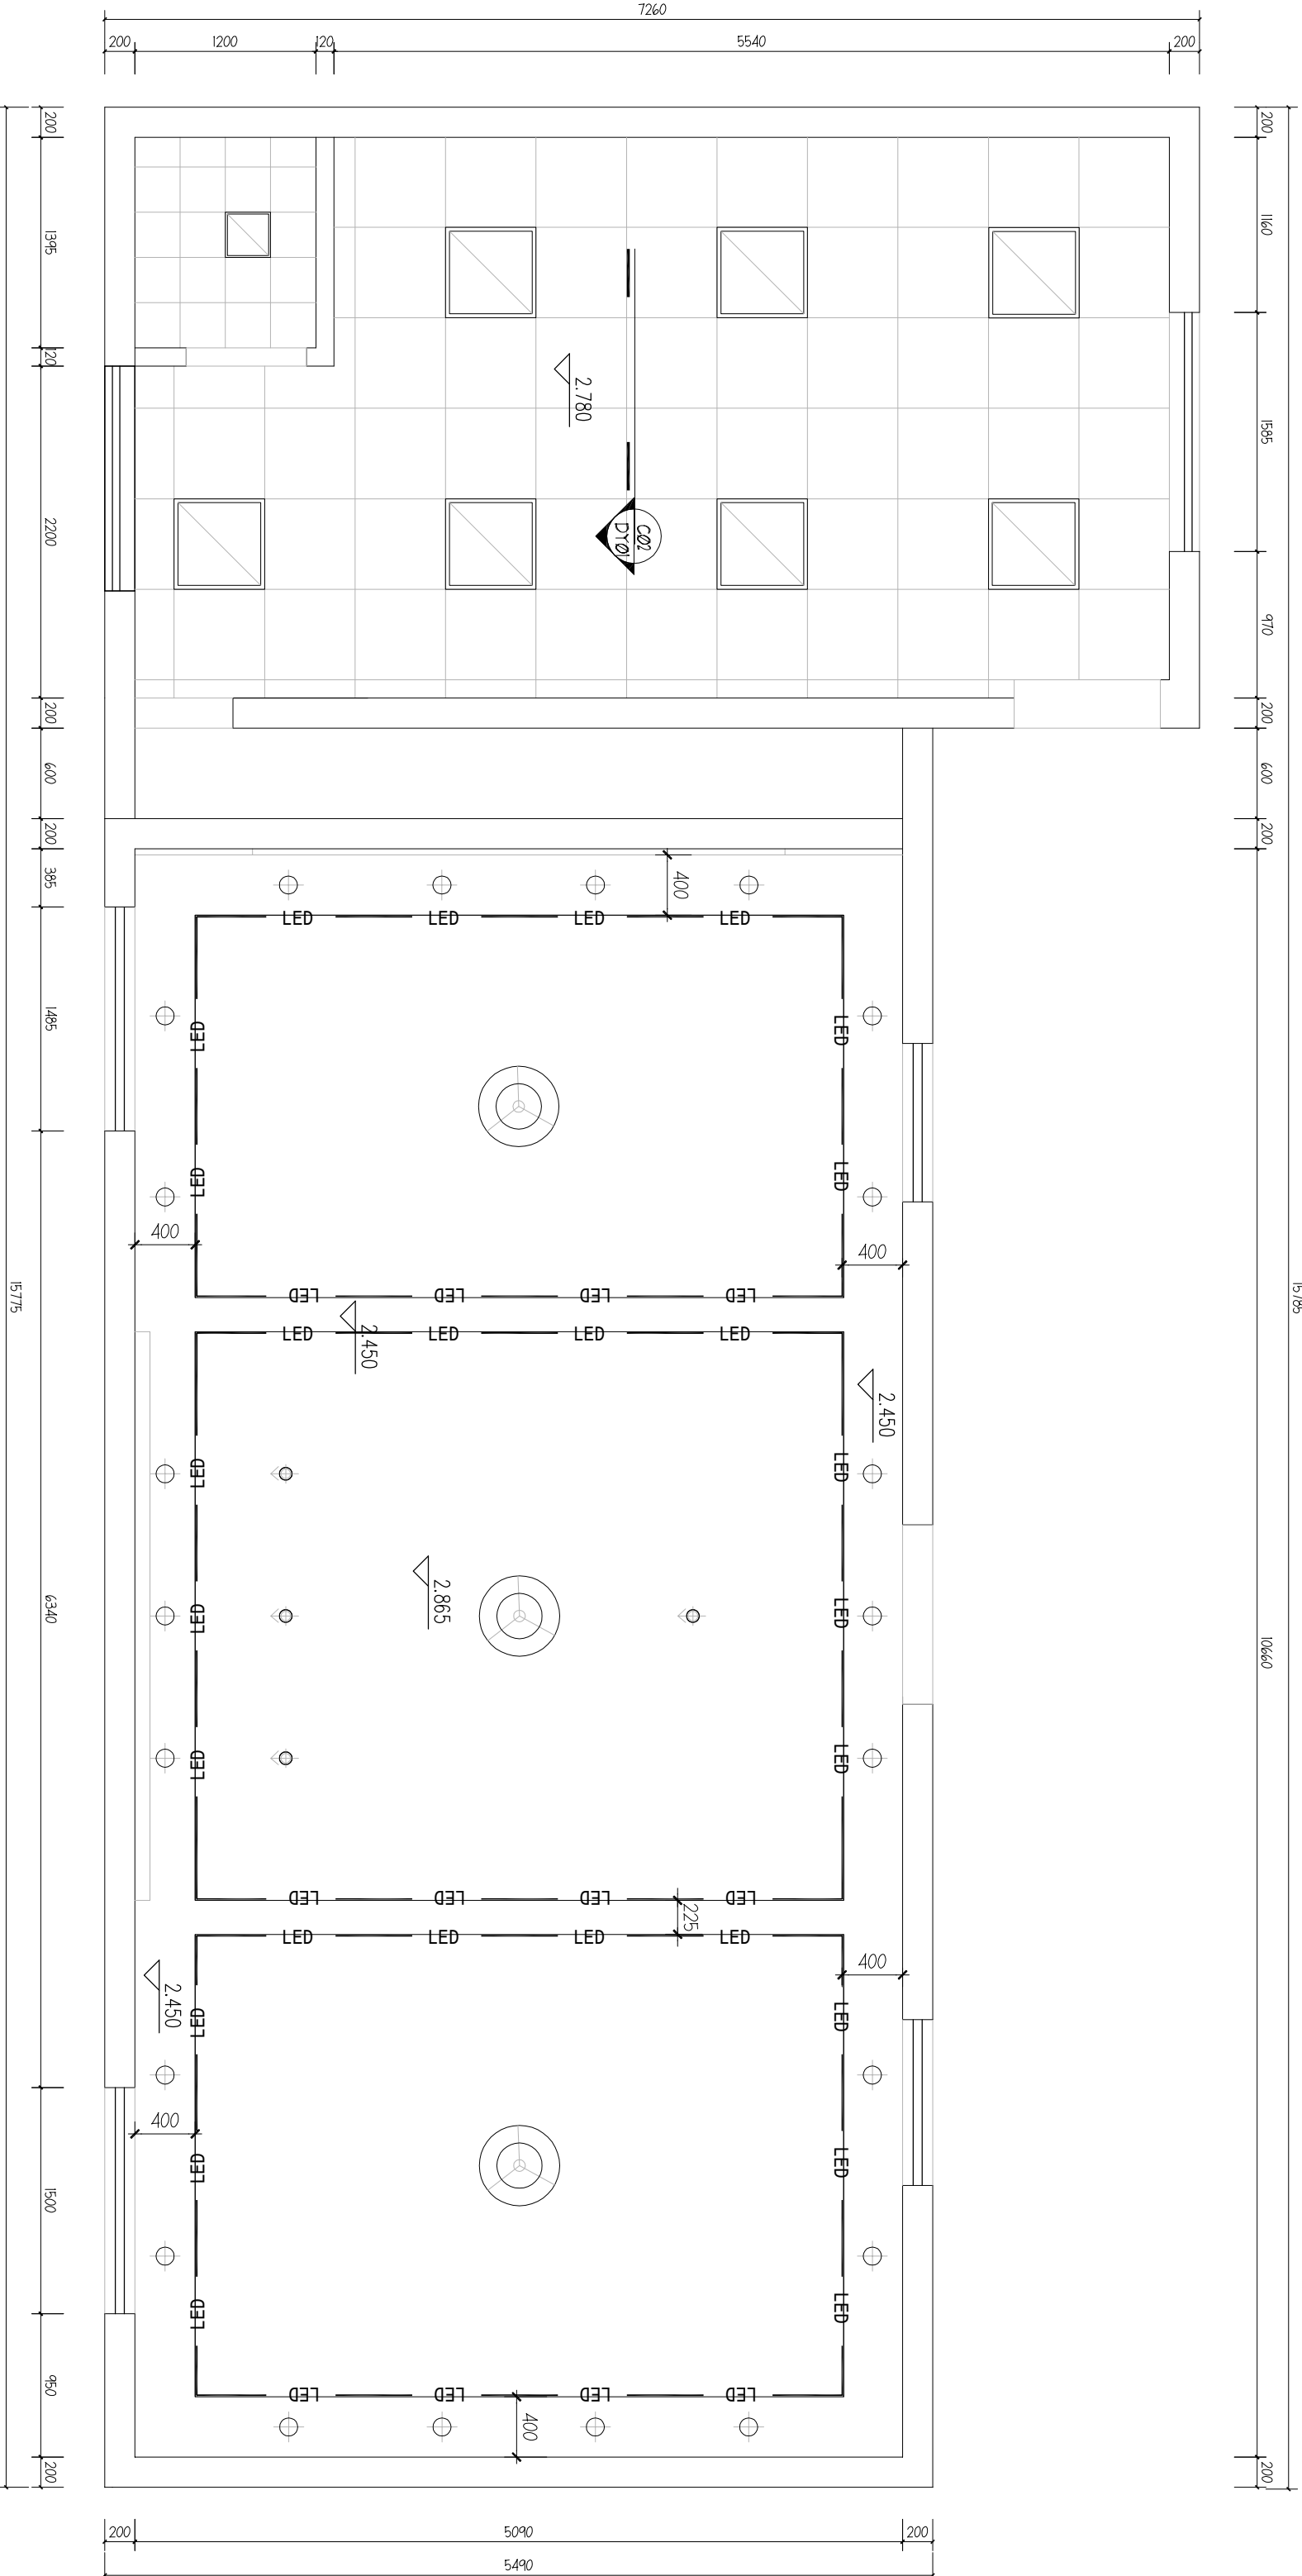

LEGEND: 图例			
⊕	嵌入式筒灯开孔 100mm LED/15W 4000K	☒	300*300新风口
□	600X600平板灯 220V/LED/35W/m ² , 4000K	—	LED灯带 220V/LED/12W/m, 4000K
○	吊灯 220V/LED/35W/m ² , 4000K	○	明装射灯 LED/15W 4000K

1F

组织活动场所一楼吊顶布置图 SCALE 1:40

EXISTING PLAN



甲级工程设计证书编号: A15103062
乙级工程设计证书编号: A251023438

CASE NO.

DRAWING SPECIAL SEA

TERED SEA

注册执业栏
REGISTERED ARCHITECT/ENGINEER

34

5103062-00

215000941

墨勘察设计有限公司

PROJECT TITLE

村示范党群服务中心

SUB ITB

邓 成

徐斌

邓成

邓 威

鄧泉


动物场所一楼灯具尺寸图

—

建德

06

注：所有图纸需经审查机构审查合格后方可施工

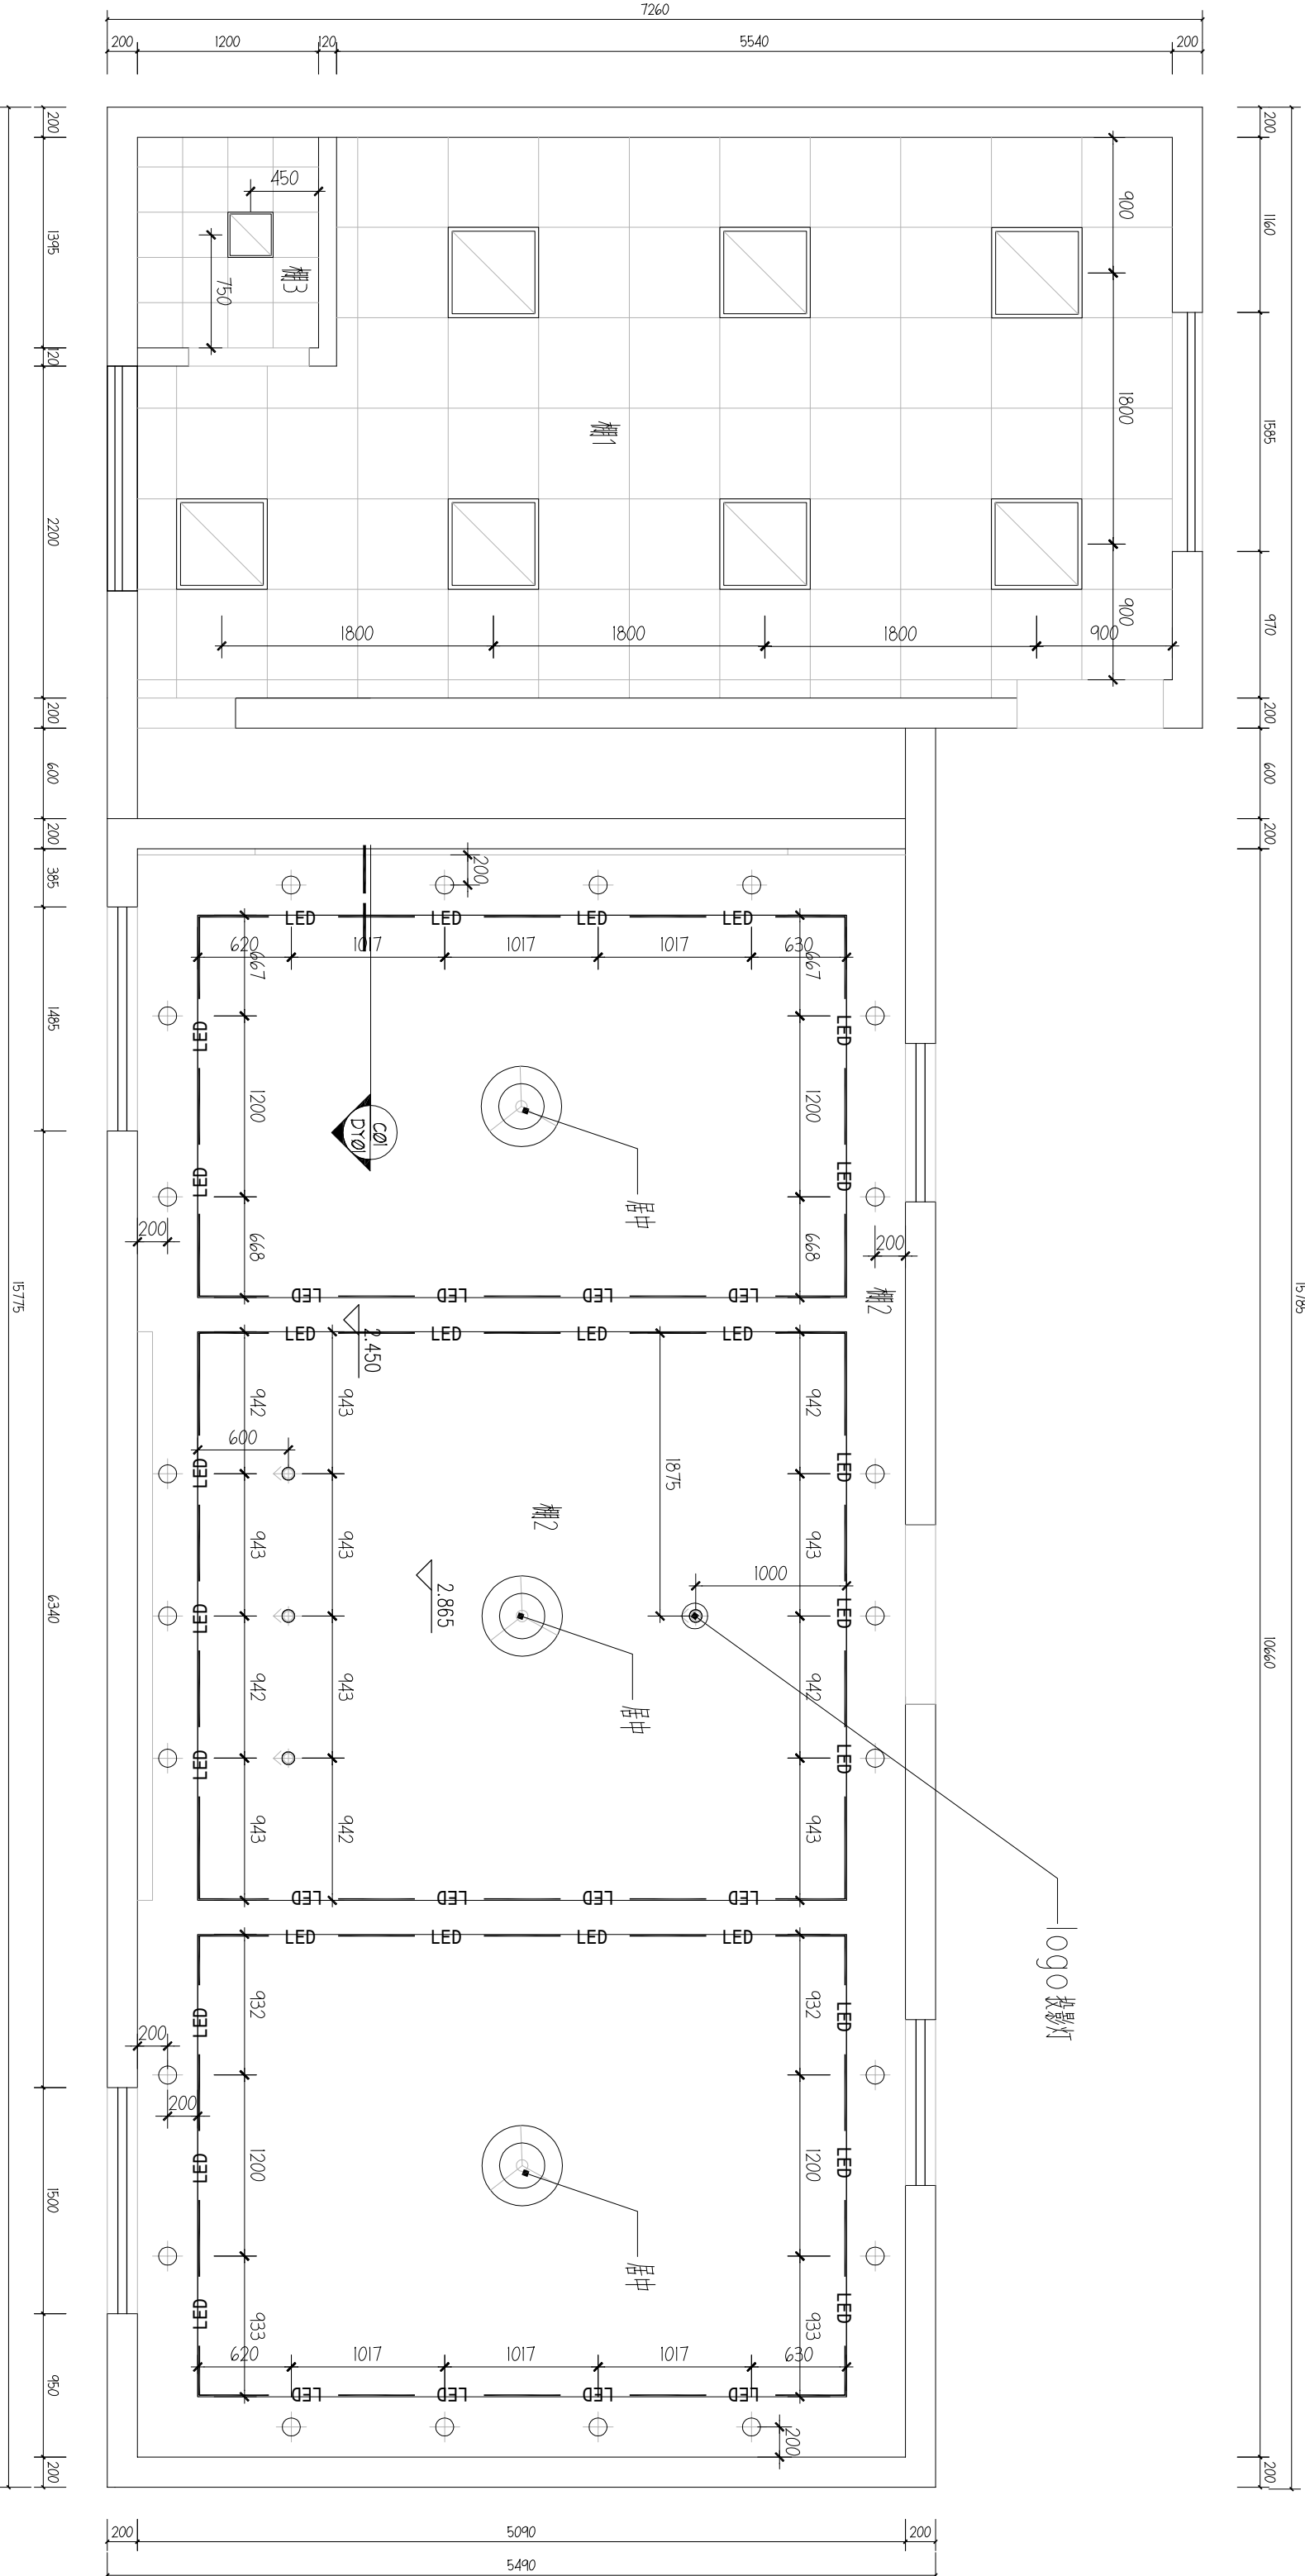

LEGEND: 图例

嵌入式筒灯开孔100mm

LED/15W 4000K

600X600平板灯, 300X300平板灯

220V/LED/35W/m	4000K	220V/LED/12W/m	4000K
----------------	-------	----------------	-------

	吊灯		明装射灯
---	----	---	------

220V/LED/35W/m . 4000K

LED/15W 4000K

ה

组织活动场所一楼灯具尺寸图 SCALE 1:40

EXISTING PLAN



甲级工程设计证书编号: A151030621
乙级工程设计证书编号: A251023438

CASE NOTE

DRAWING SPECIAL SEAL

草案專用圖印

REGISTERED SEAL

注册印章

REGISTERED ARCHITECT/ENGINEER

NAME 姓名

REGISTERED SIGNATURE

注册证书

建设单位

工程名称

子顶名称

SUB ITEM#

規則

定章

审核

专业负责

年

DESIGNED BY

E
D
.

12

TOP NO
41181

圖別

40

注：所有图纸经审查机构审查合格后方可施工

出图专用章
DRAWING SPECIAL SEAL

注册印章
REGISTERED SEAL

注册执业栏
REGISTERED ARCHITECT/ENGINEER

姓名
NAME

注册印章号
REGISTERED SEAL NO.

注册证书号
REGISTERED CERTIFICATE NO.

建设单位：
CLIENT

中懿勘察设计有限公司

工程名称：
PROJECT TITLE

大坪村示范党群服务中心

子项名称：
SUB ITEM

项目总负责人
PROJECT NO.

审定
APPROVED BY

审核
AUDIT

专业负责人
DISCIPLINE CHIEF

校对
CHECKED BY

设计
DESIGNED BY

图名：
DRAWING TITLE


一楼大会议室原始图

设计号
JOB NO.

图别
DRAWING CATEGORY

图号
DRAWING NO.

注：所有图纸需经审查机构审查合格后方可施工

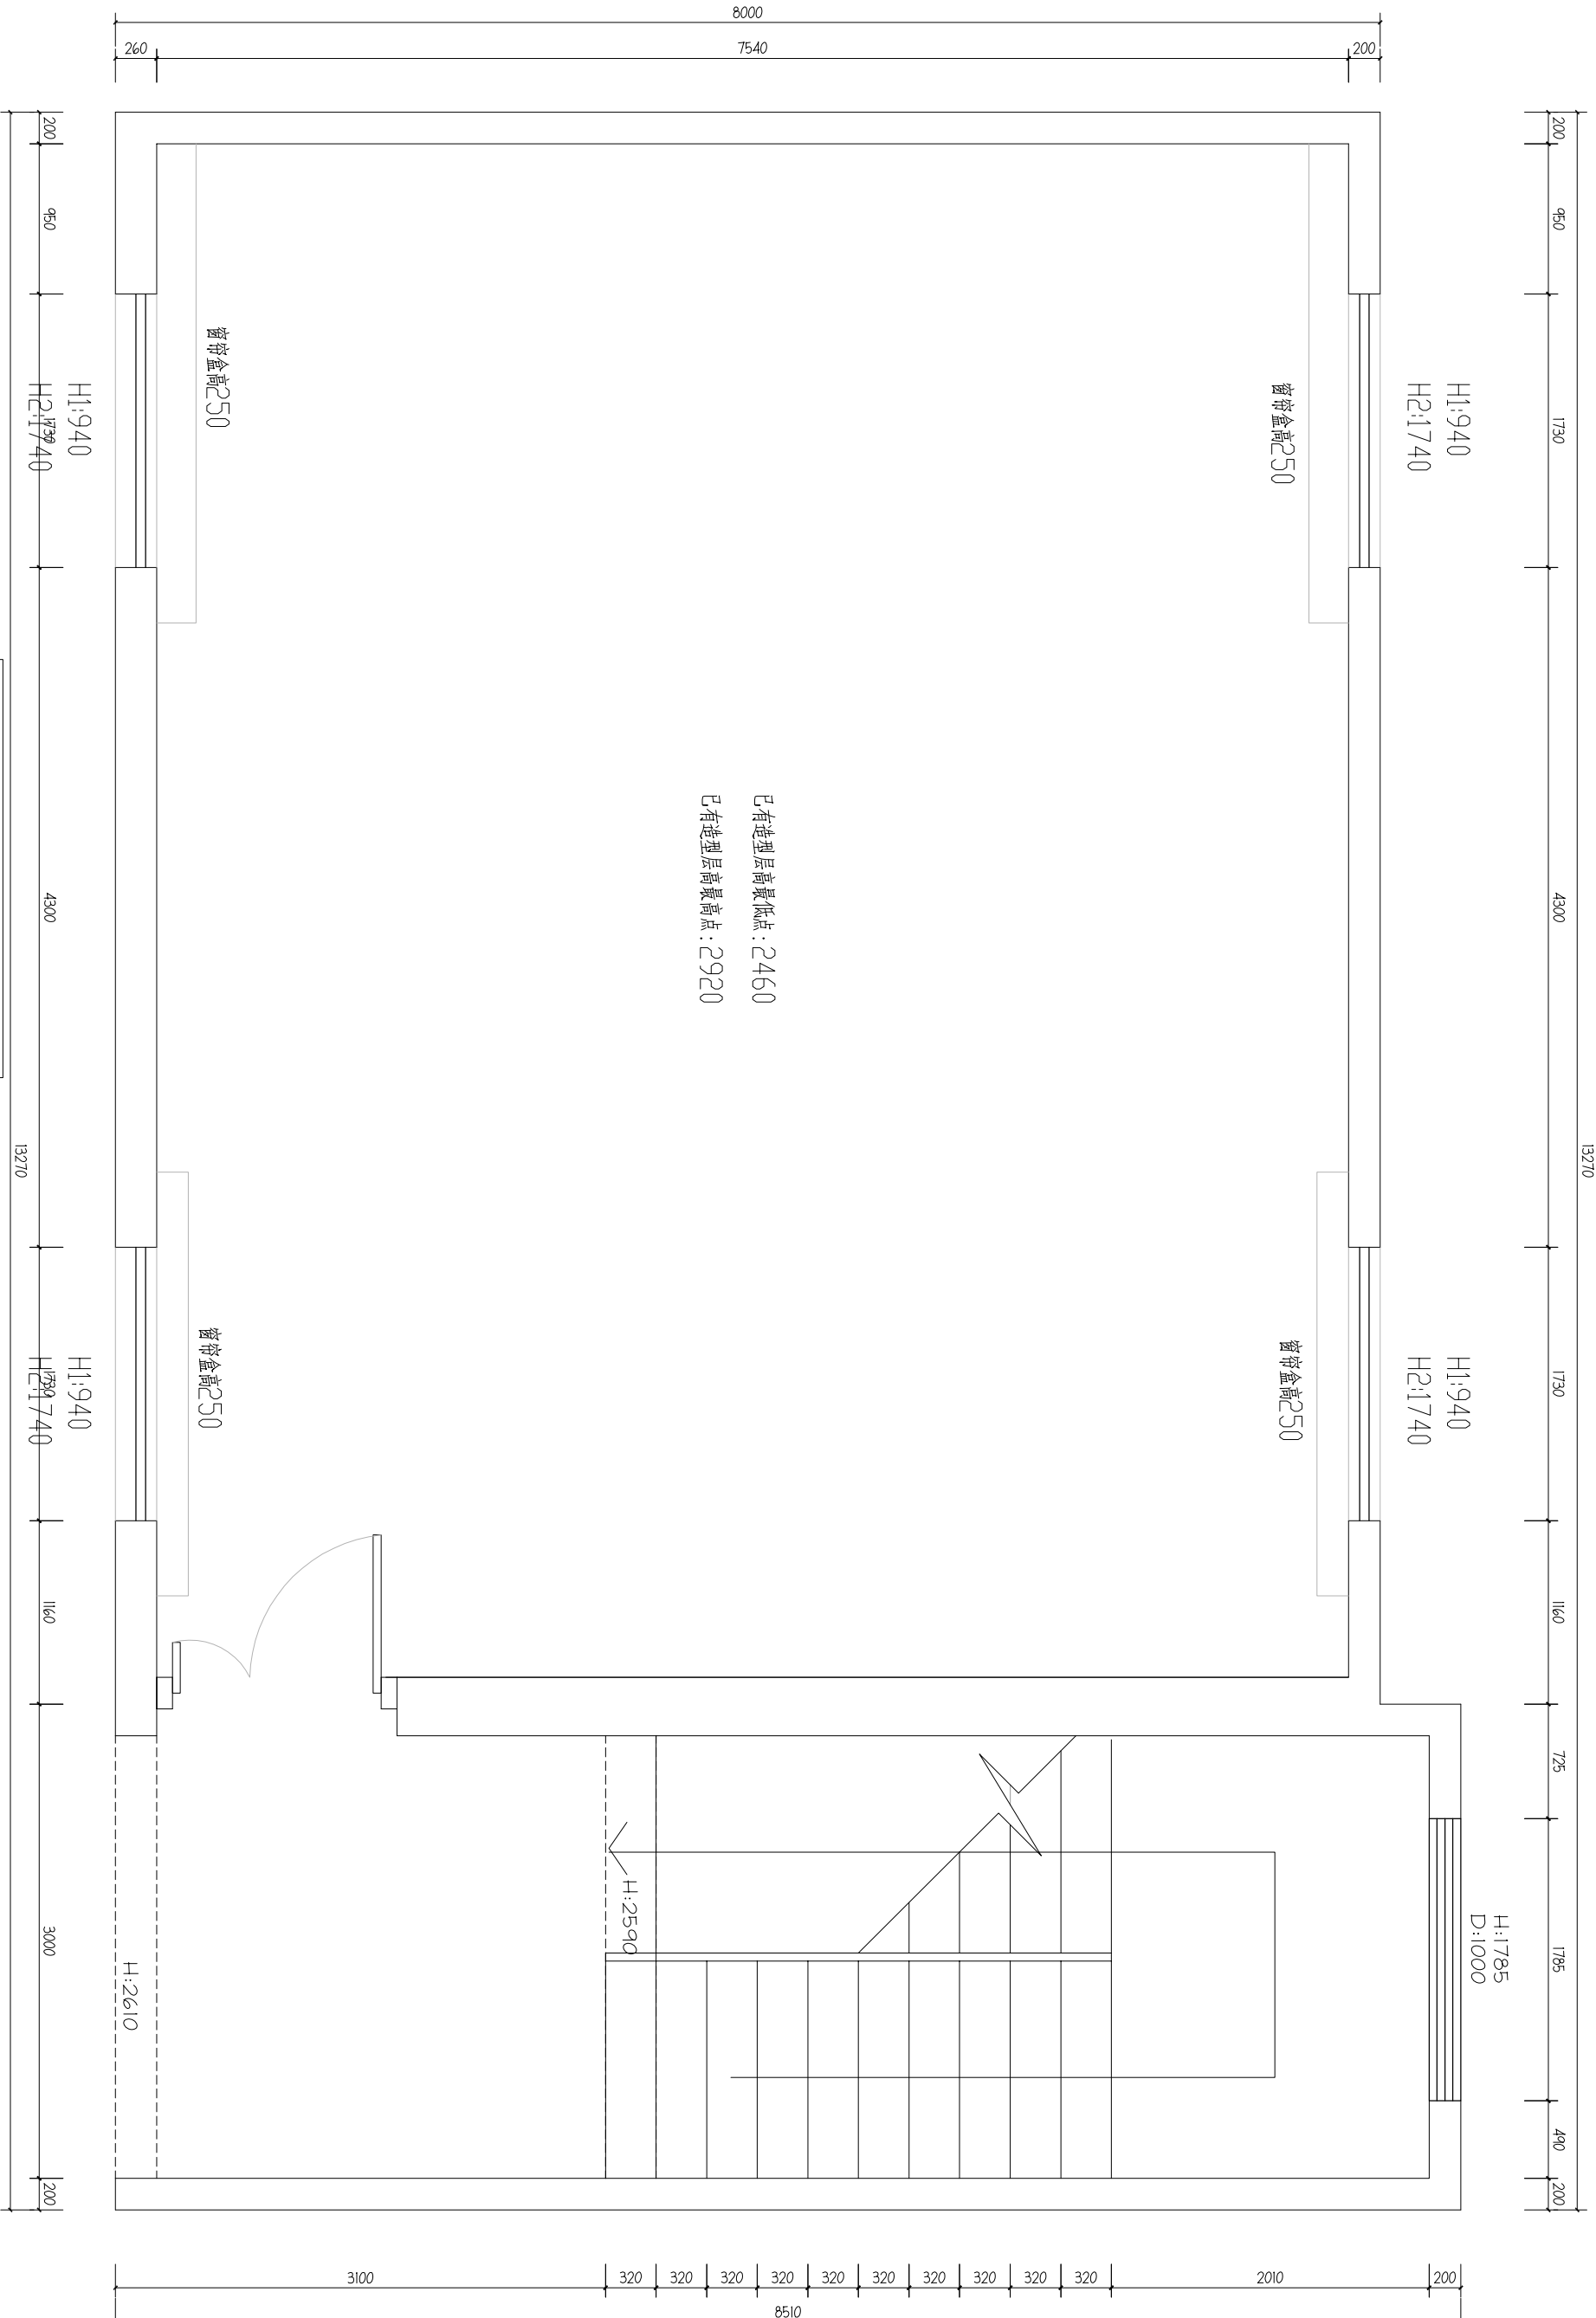

1F
EXISTING PLAN
一楼大会议室原始图
SCALE 1:40



甲级工程设计证书编号: A151030621
乙级工程设计证书编号: A251023438

CASE NOT

DRAWING SPECIAL SEAL

REGISTERED SEAL

注册执业栏
REGISTERED ARCHITECT/ENGINEER

姓名 NAME	
	2014

注册编号 REGISTERED SIGNET NO.	510306Z-001
-------------------------------	-------------

REGISTERED CERTIFICATE NO.	215000941
----------------------------	-----------

中睦勘察设计有限公司

工程名称:	PROJECT TITLE:

大坪村示范党群服务中心

SUB ITEM	子項名稱
1	1. 總則
2	2. 計畫目標
3	3. 計畫範圍
4	4. 計畫內容
5	5. 計畫經費
6	6. 計畫成效
7	7. 計畫檢討
8	8. 計畫附件
9	9. 計畫其他事項
10	10. 計畫其他事項
11	11. 計畫其他事項
100	100. 計畫其他事項

项目总负责人	邓 威	
PROJECT NO.		

APPROVED BY

徐斌

DISCIPLINE CHIEF
鄭 威

校 人 CHECKED BY	王 成	2017.12.12
-------------------	-----	------------

设计	邵永	邵永
----	----	----

BOOK REVIEW

一楼大会议室改后平面

设计号	TOP NO.
-----	---------

图 别 施 建 版 本 号 第 一 版

DATE NO. 3PL / 03 DATE 202408

注：所有图纸需经审查机构审查合格后方可施工



甲级工程设计证书编号: A15103062
乙级工程设计证书编号: A251023438

CASE NO.

H1:960
H2:179
W:180

H1:960
H2:179
W:180

H1:900
H2:1790
W:180

H1:600
H2:1750
W:210

DRAWING SPECIAL SECT

THE UNIVERSITY OF CHICAGO

注册 注册执业栏
REGISTERED ARCHITECT/ENGINEER

37

5103062-00

215000941

CLIENT

PROJECT TITLE

118

邓 展

徐 方

邓 展

邓 后

鄒 吳

二樓西側原始平面圖

第一版

日期 20240801

注：所有图纸需经审查机构审查合格后方可施工

出图专用章
DRAWING SPECIAL SEAL

注册印章
REGISTERED SEAL

注册执业栏
REGISTERED ARCHITECT/ENGINEER

姓名
NAME

注册印章号
REGISTERED SEAL NO.

注册证书号
REGISTERED CERTIFICATE NO.

建设单位：
中懿勘察设计有限公司

工程名称：
大坪村示范党群服务中心

子项名称：
SBS 173M

项目总负责人
PROJECT NO.

审定
APPROVED BY

审核
AUDIT

专业负责人
DISCIPLINE CHIEF

校对
CHECKED BY

设计
DESIGNED BY

图名：
二樓西侧原始解构拆除图

设计号
JOB NO.

图例
DME: CHINESE

图号
DME NO.

图号
DME NO.

注：所有图纸需经审查机构审查合格后方可施工

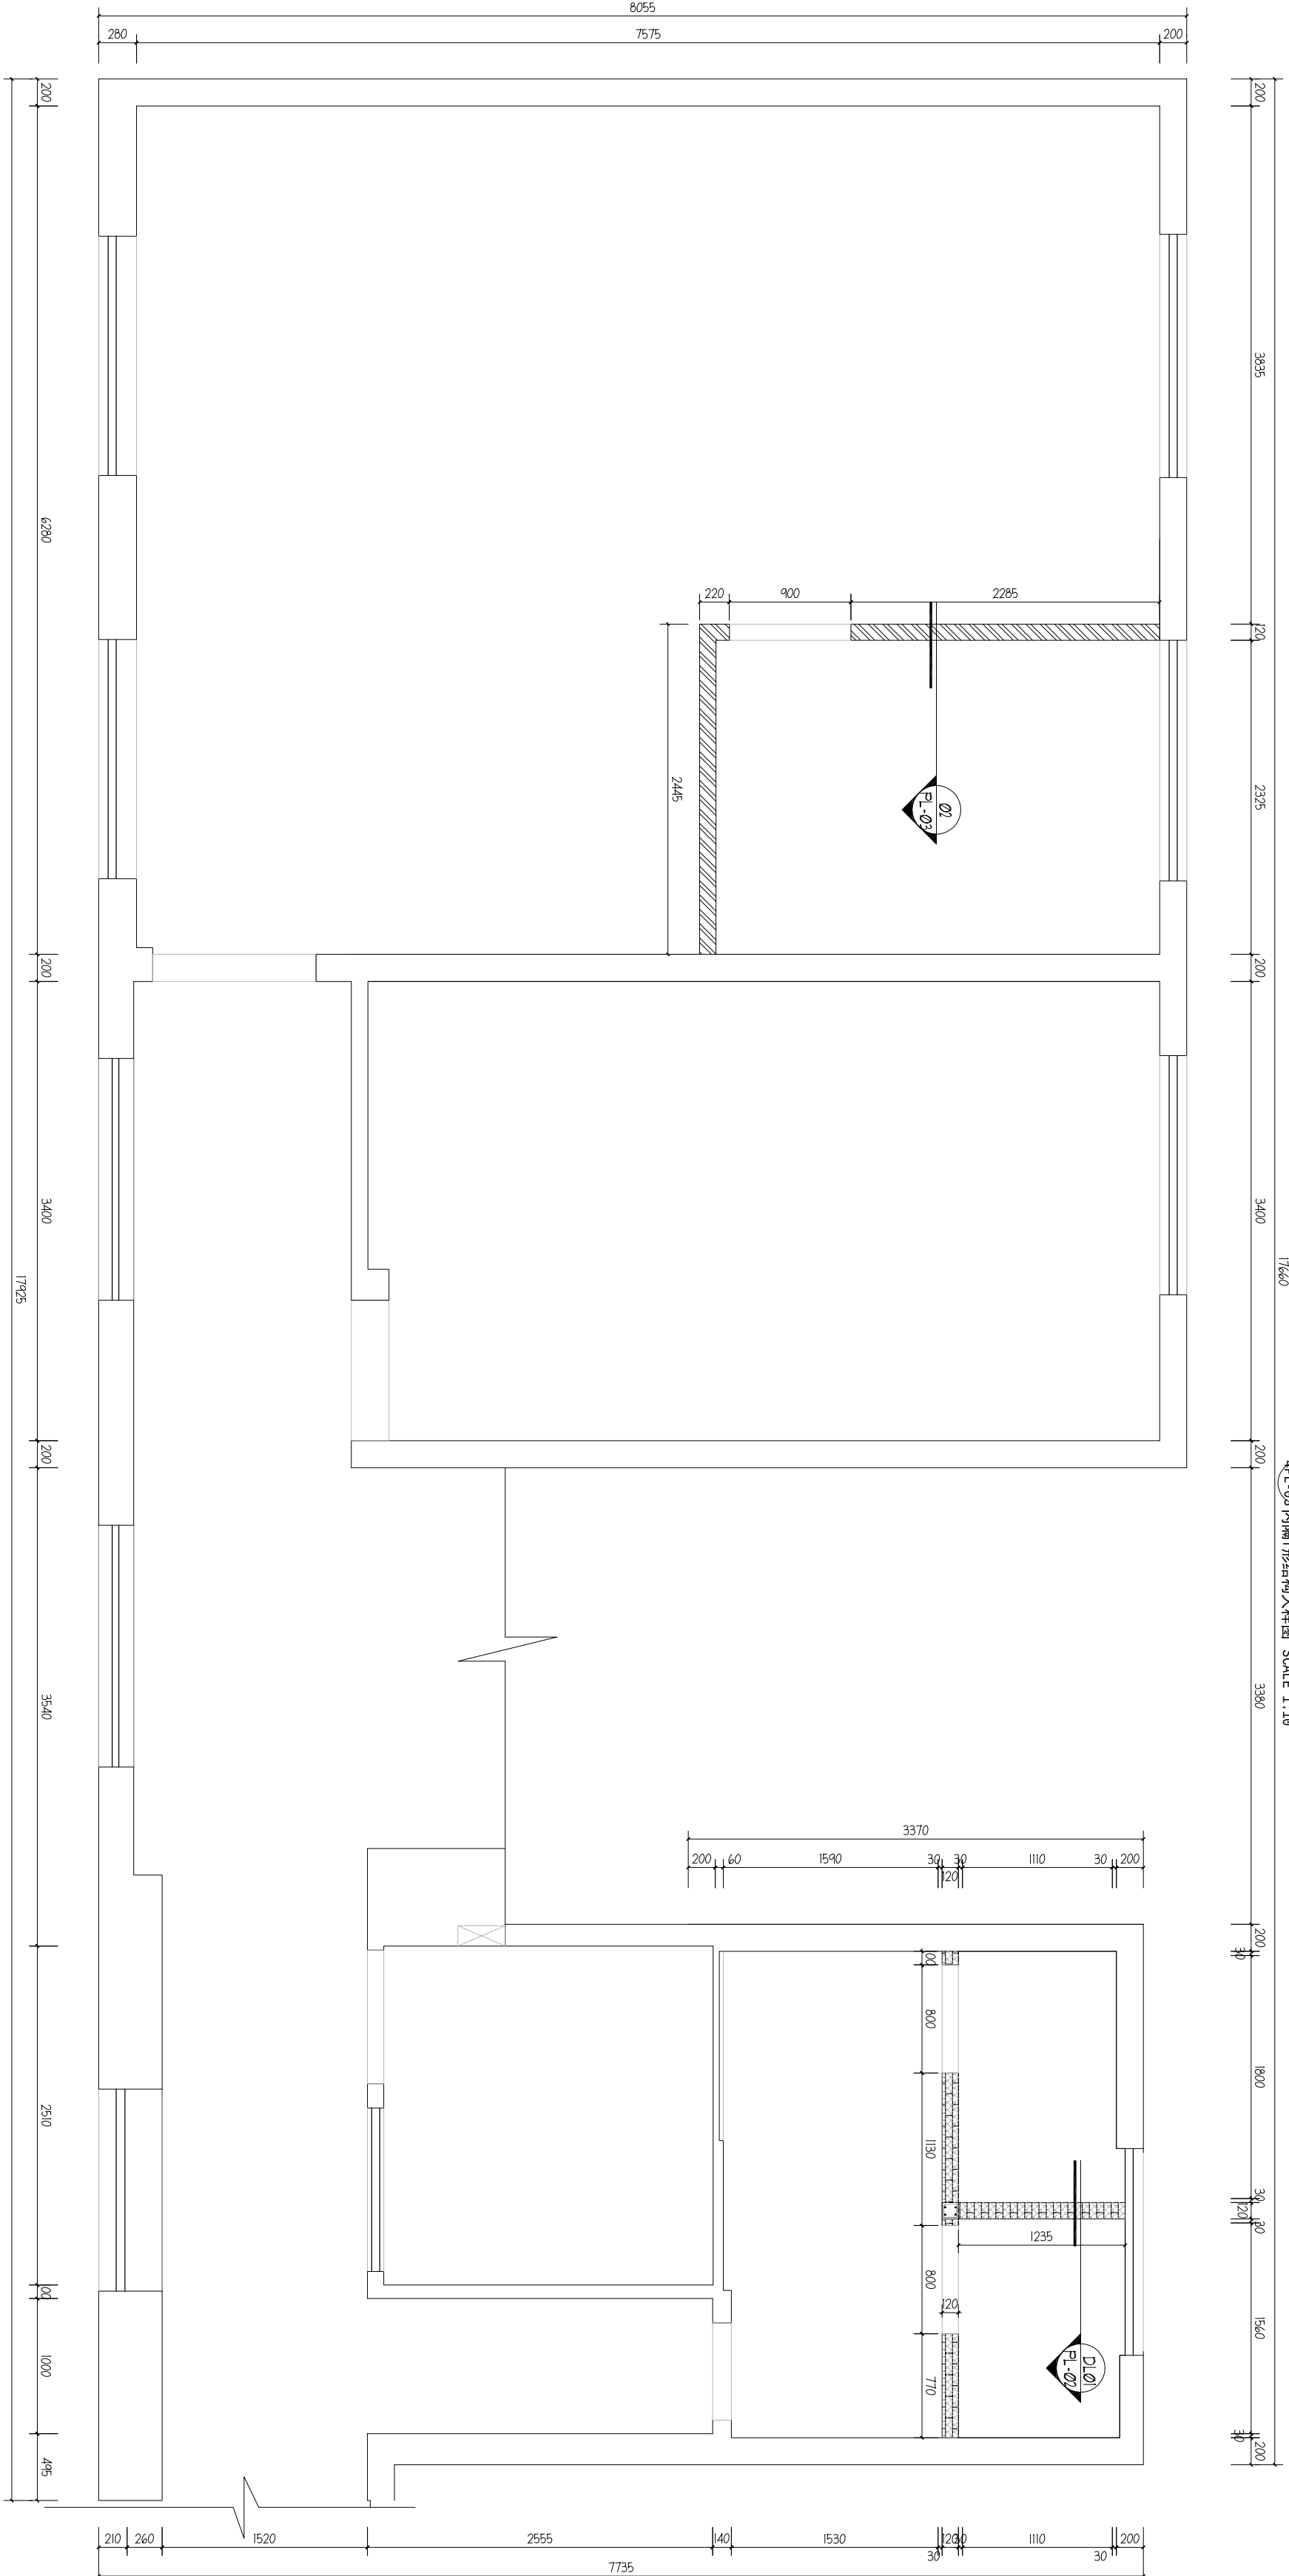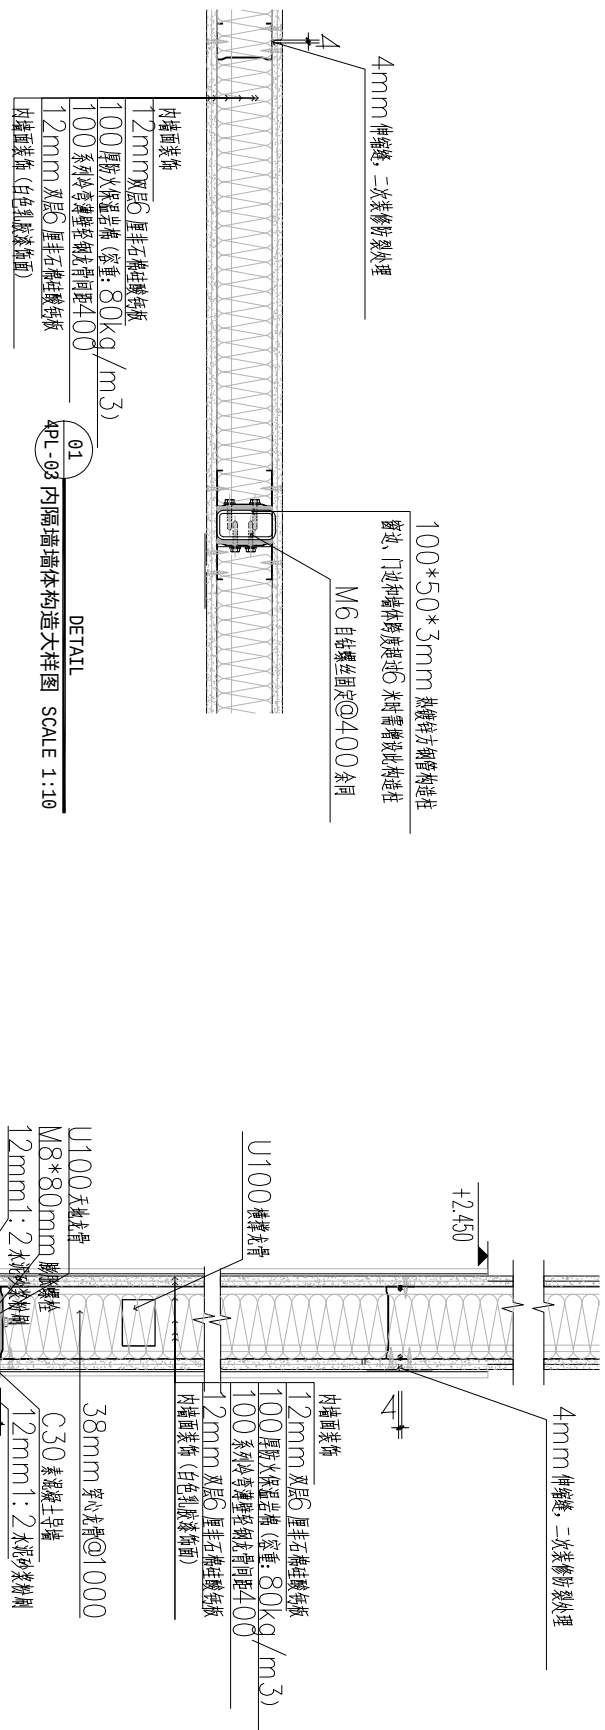

图例

	钢结构构造柱 (热镀锌方钢管立柱 100*100*3mm)
	混凝土
	原建筑墙体
	新砌加气砖墙 (高度 4085mm)
	底部设 200*200/100*200 的 C20 素砼反口
	轻钢龙骨隔墙

注: 1、砌体墙转角处、丁字处、十字交叉处和门窗口两侧, 墙体长度大于 5 米设置构造柱 (见大样图 D-Y-04-GL01)。

2、未特殊注明时, 墙厚为 220MM, 宽度以图内尺寸标注


3、新砌加气混凝土墙体必须找平, 加气混凝土专用密封胶、挂钢丝网、18 厘: 2.5 水泥砂浆打底。

4、砌体墙与平面图不符时, 根据平面图进行补墙。

2F

二楼西侧新砌墙体图 SCALE 1:40

EXISTING PLAN

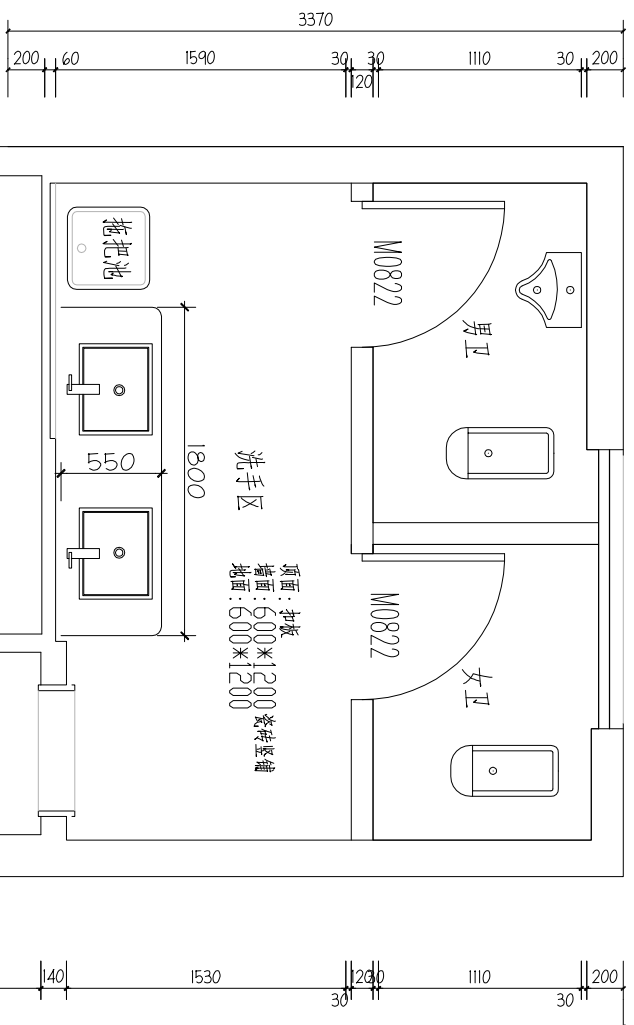

2F 二楼西侧改后平面图 SCALE 1:40

EXISTING PLAN

设计号 JOB NO.		图 别 DRAWING CATEGORY	图 号 DRAWING NO.	4PL	04	日期 DATE	202408
审 定 APPROVED BY	徐 斌	审 核 CHECKED BY	邓 成	邓 成	邓 成	邓 成	邓 成
专业负责人 DISCIPLINE CHIEF	邓 成	校 对 CHECKED BY	邓 成	邓 成	邓 成	邓 成	邓 成
设计 DESIGNED BY	邹 泉	设计 DESIGNED BY	邹 泉	邹 泉	邹 泉	邹 泉	邹 泉

图 名:

二楼西侧改后平面图

工程名称: 大坪村示范党群服务中心

子项名称: 中懿勘察设计有限公司

项目总负责人: 邓 成

审 定: 徐 斌

审 核: 邓 成

专业负责人: 邓 成

校 对: 邓 成

设计: 邹 泉

注: 所有图纸需经审查机构审查合格后方可施工



甲级工程设计证书编号: A151030621
乙级工程设计证书编号: A251023438

PLEASE NOTE

DRAWING SPECIAL SEAL

注册印章

REGISTERED SEAL

注册执业栏
REGISTERED ARCHITECT/ENGINEER

NAME 姓名

2

REGISTERED SIGNET NO.

103062-00

REGISTERED CERTIFICATE

215000941

中睦勘察设计有限公司

CULTURE

工程名称

PROJECT TITLE

大坪村示范党群服务中心

子項名稱：

HELLY HAN:

PROJECT NO. 日志更人 邓 成

邓 成

APPROVED BY

AUDIT

你 烟

DISCIPLINE CHIEF

113

CHECKED BY _____

1000

DESIGNED BY

圖名:

图 2 西侧地面铺装

DRAWING TITLE

设计号

EXISTING PLAN

27

SCALE 1:40

注: 所有图纸需经审查机构审查合格后方可施工



甲级工程设计证书编号: A151030621
乙级工程设计证书编号: A251023438

CASE NOTE

DRAWING SPECIAL SEAL

REGISTERED SEAL

注册印章

REGISTERED ARCHITECT/ENGINEER

NAME _____

注册编号
REGISTERED SIGNET NO.

215000941

中庭勘察设计有限公司

PROJECT TITLE: 工程名称:

大坪村示范党群服务中心

SUB ITEM

寸與名稱：

PROJECT NO. 8101

APPROVED BY

于必 AUDIT		徐 姐
-------------	--	--------

DISCIPLINE CHIEF
鄭 威

CHECKED BY 彭成

景 鄧

圖名

图 3 布置吊钩西侧图


DRAWING TITLE

JOB NO.	

DMC, CATEGORY	延地	VER. NO.	第一版
1		1.0	
2		1.0	
FILE NO.	06	DATE	202408
----------	----	------	--------

注：所有图纸经审查机构审查合格后方可施工

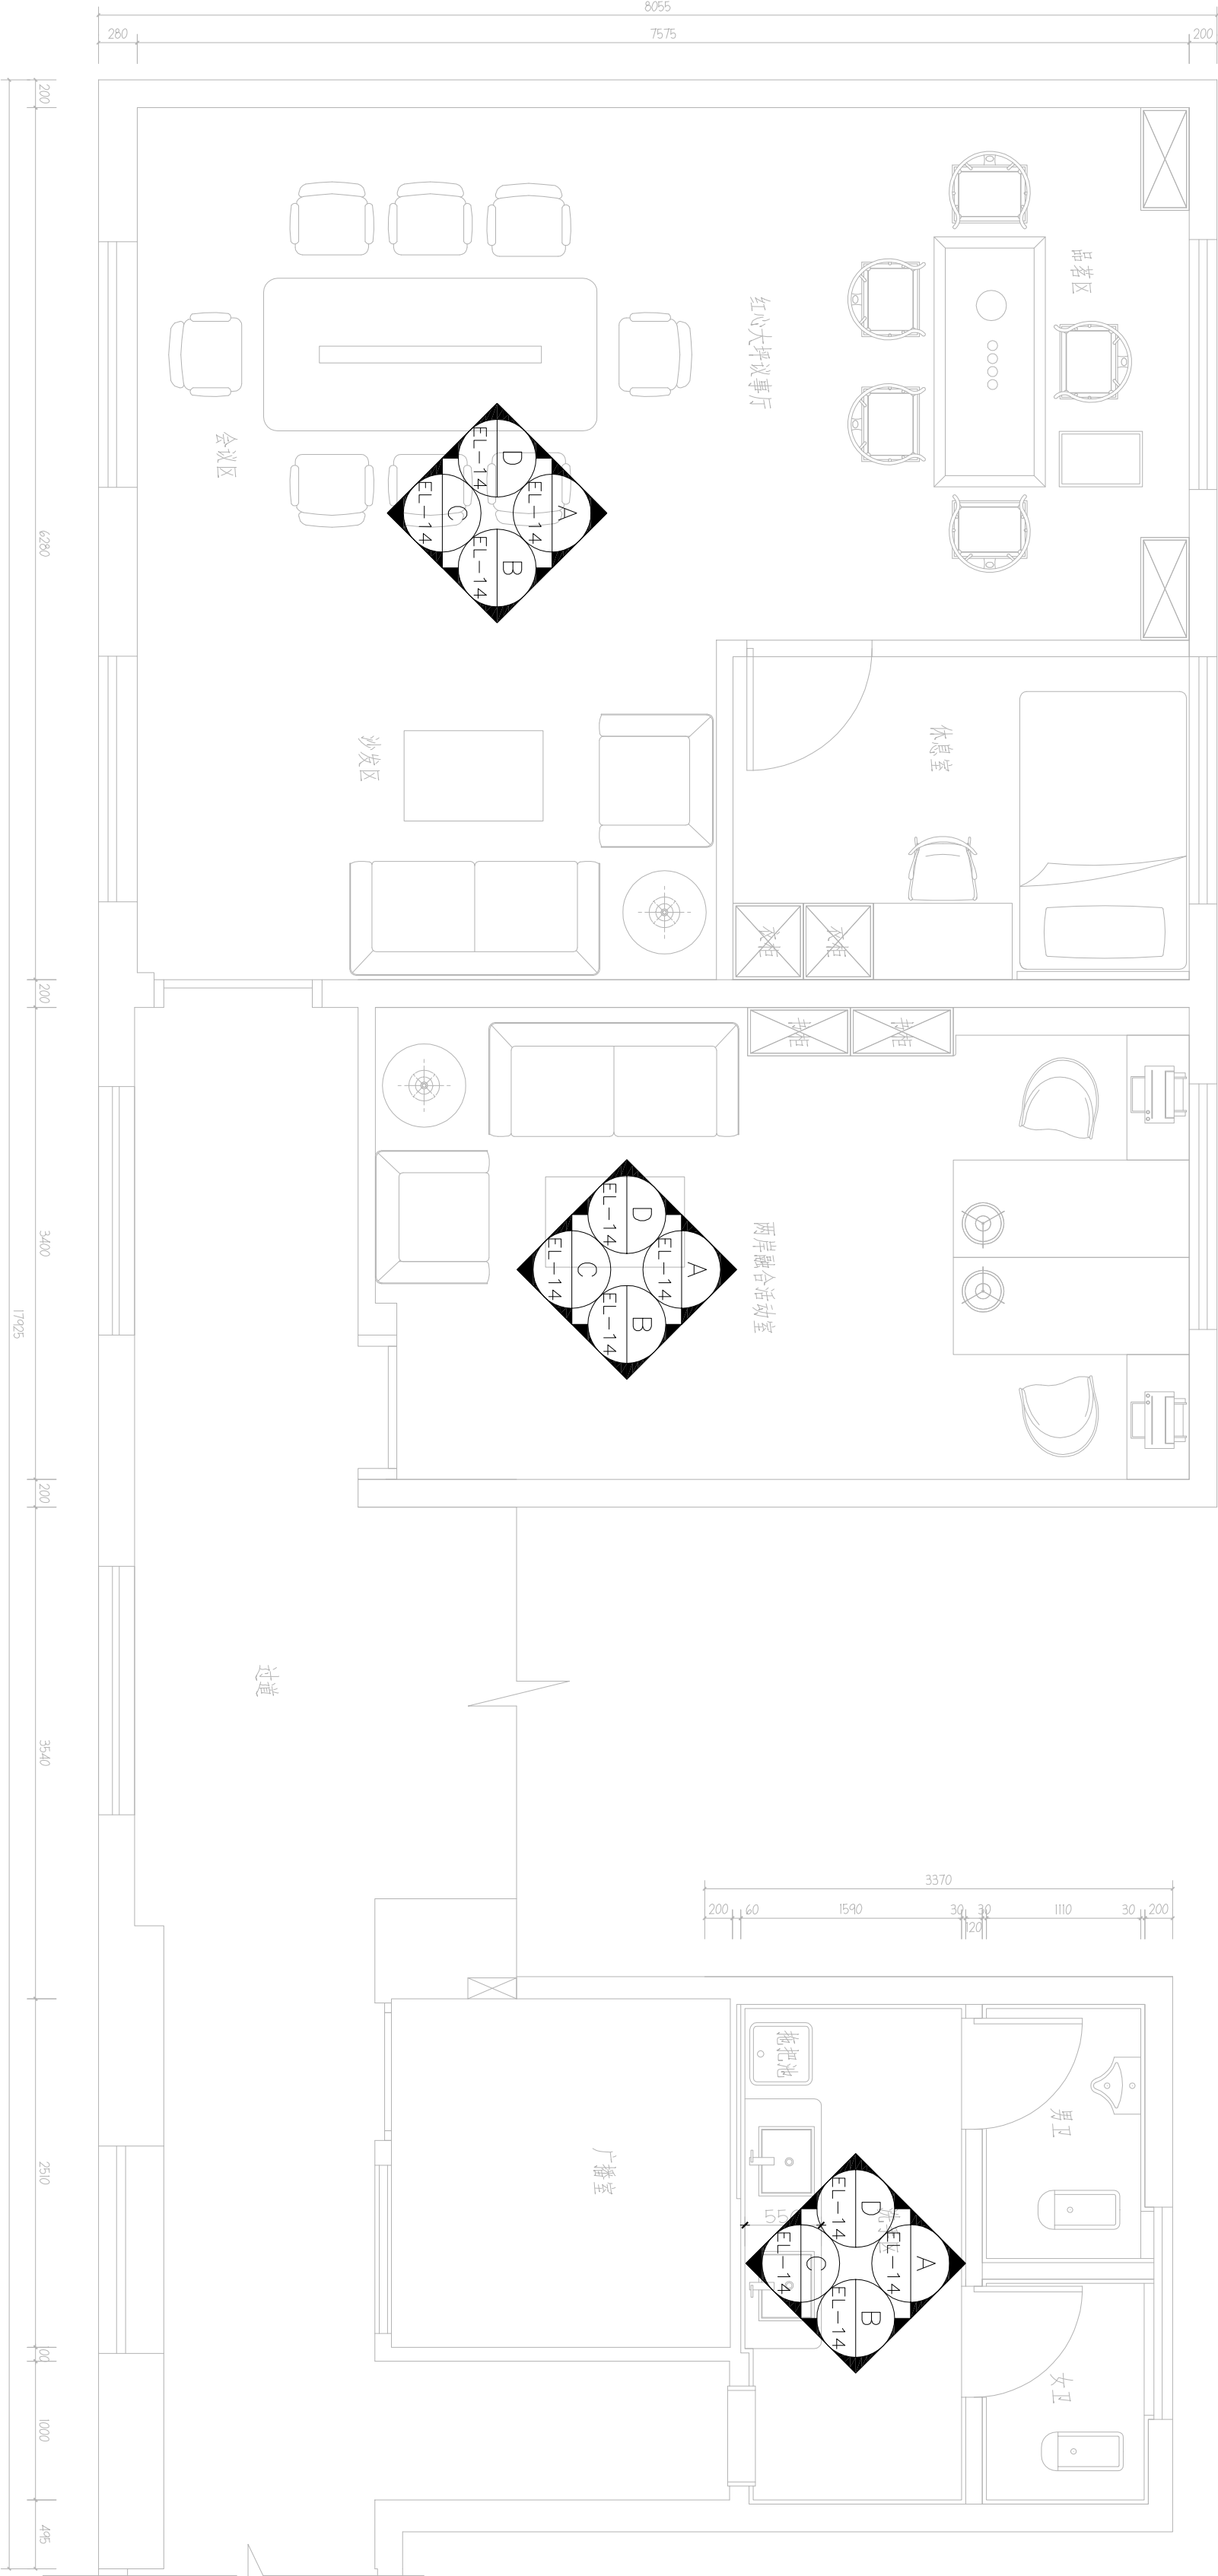

131.2平方米

2F 二楼西侧面索引图 SCALE 1:40

EXISTING PLAN

设计号	JOB NO.	图 别	图 号	图 号	图 号
		建筑	4PL	07	202408
图 别	JOB NO.	图 号	图 号	图 号	图 号
建筑	4PL	07	202408		

注：所有图纸需经审查机构审查合格后方可施工



甲级工程设计证书编号: A151030621
乙级工程设计证书编号: A251023438

CASE NOT

DRAWING SPECIAL SEAL

REGISTERED SEA

注册执业
REGISTERED ARCHITECT/ENGINEER

A 13

5103062-00

215000941

中睦勘察设计有限公司

PROJECT TITLE

大坪村示范党群服务中心

SUB ITR

43

10

陈

42

✓

分

1000

DRAFTING TITLE


二楼东侧原始平面图

设计号
JOB NO.

图别	JMC CATEGORY
建筑施	
版本号	VER. NO.
第一版	

図号
Dwg. NO. 5PL / 01
日付
DATE 202408

注：所有图纸需经审查机构审查合格后方可施工

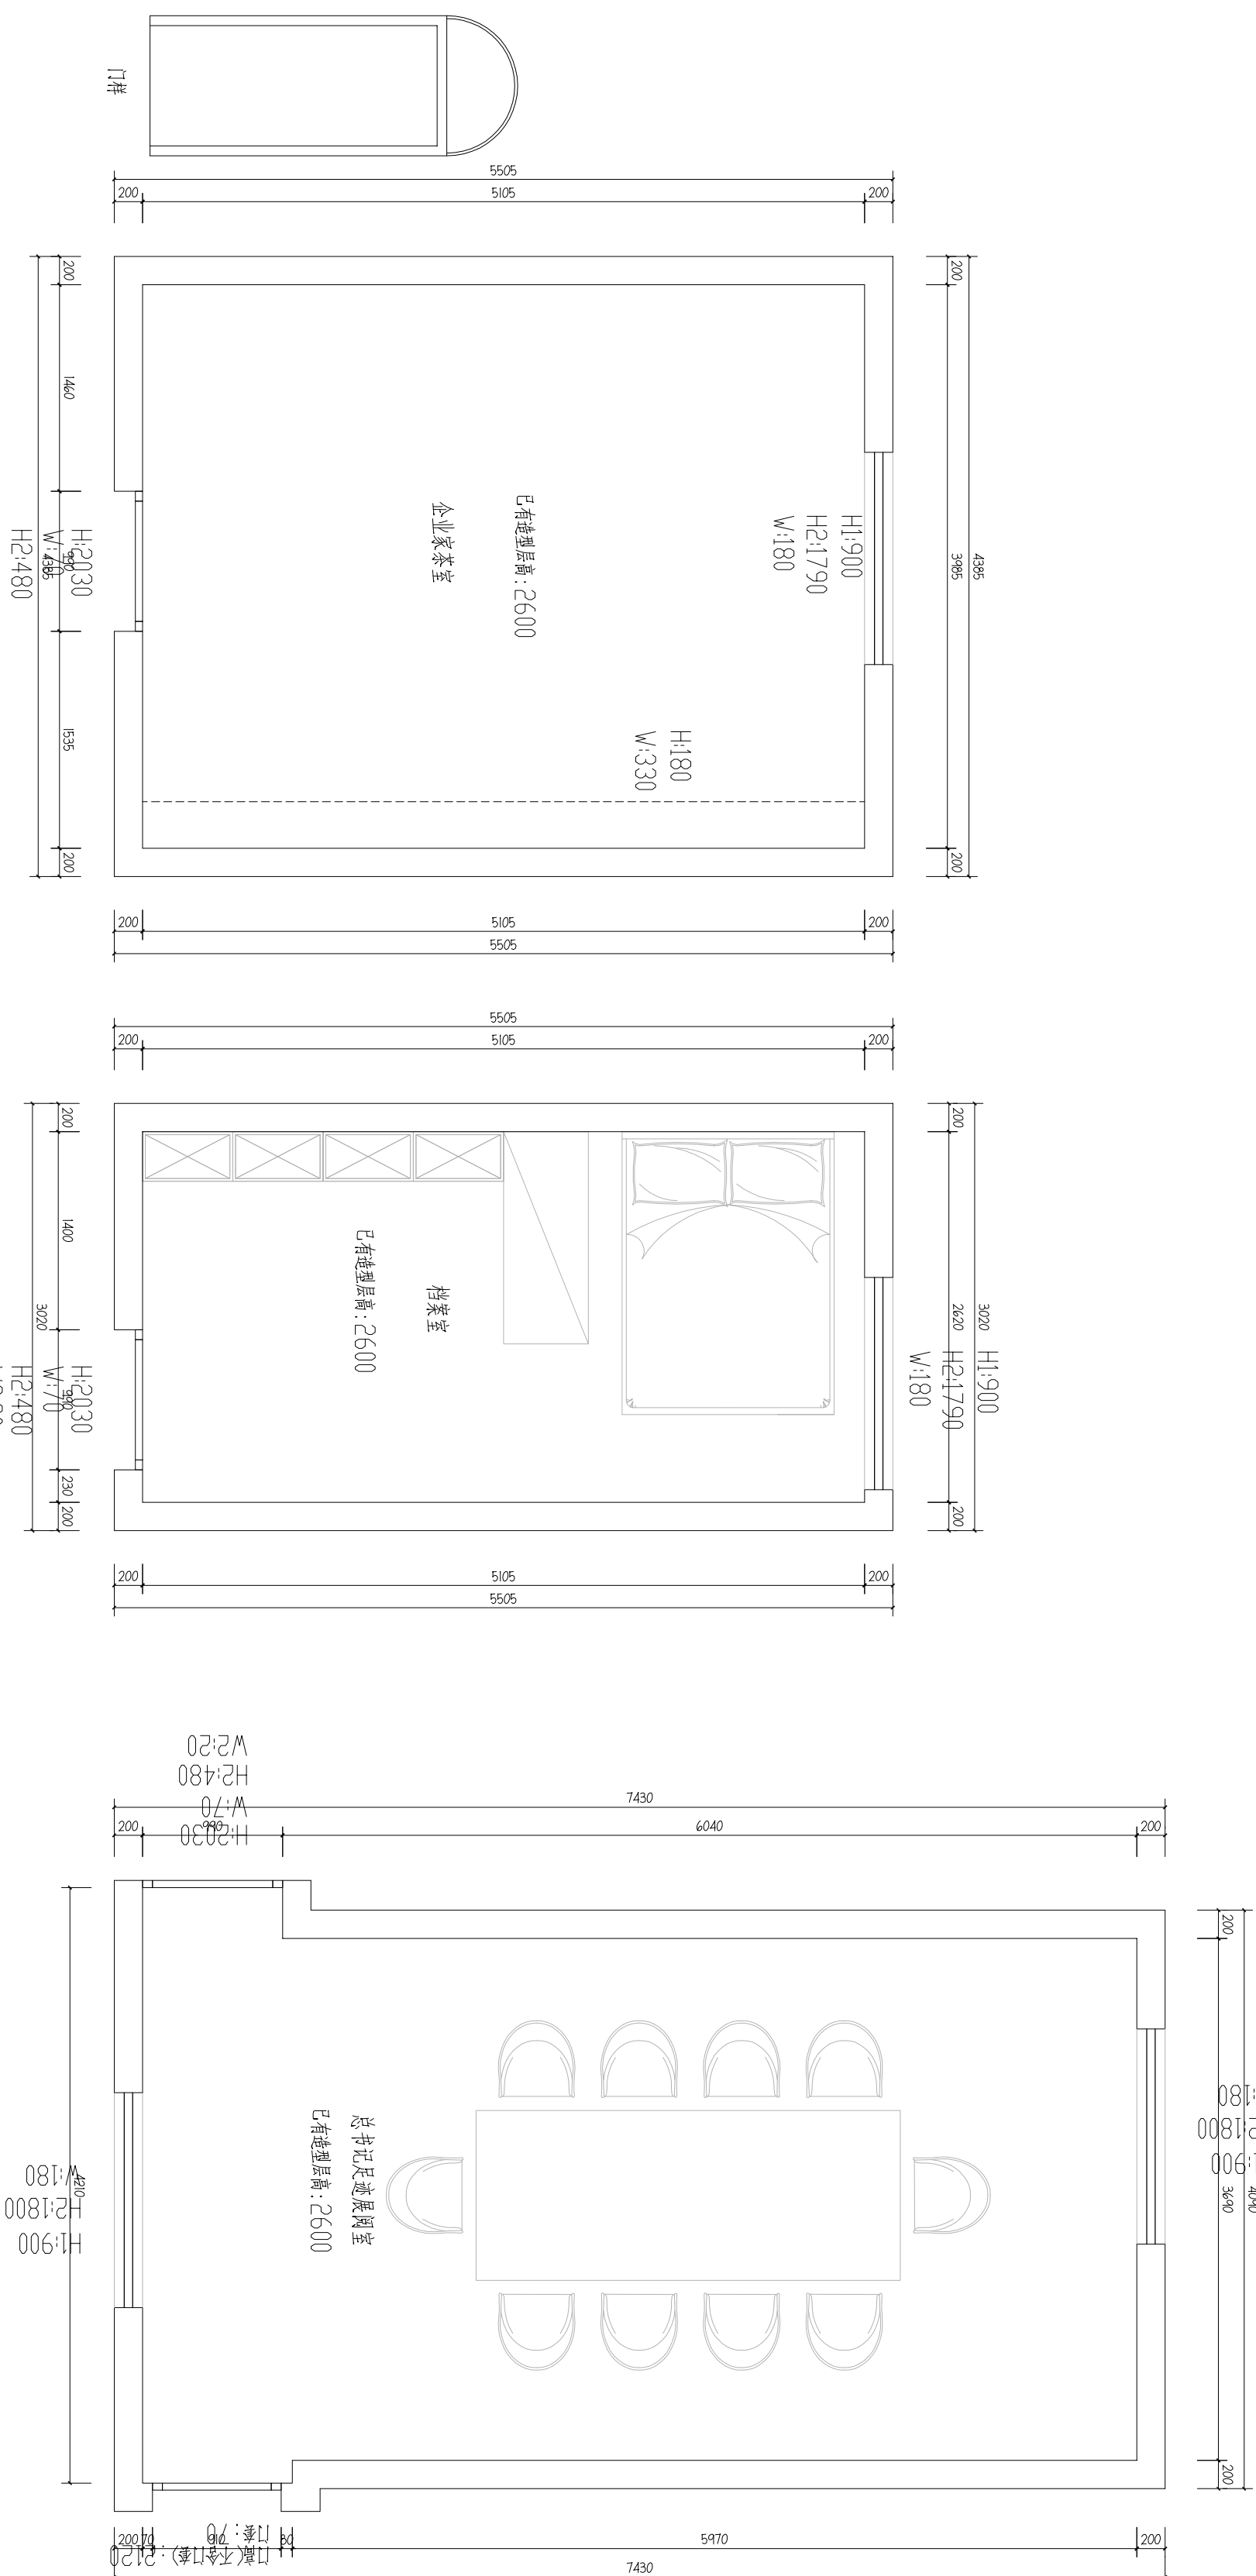

EXISTING PLAN

24



二楼东侧原始平面图 SCALE 1:40

SCALE 1:4G

4190
3690
200

4385
3985
200

3020
2620
200

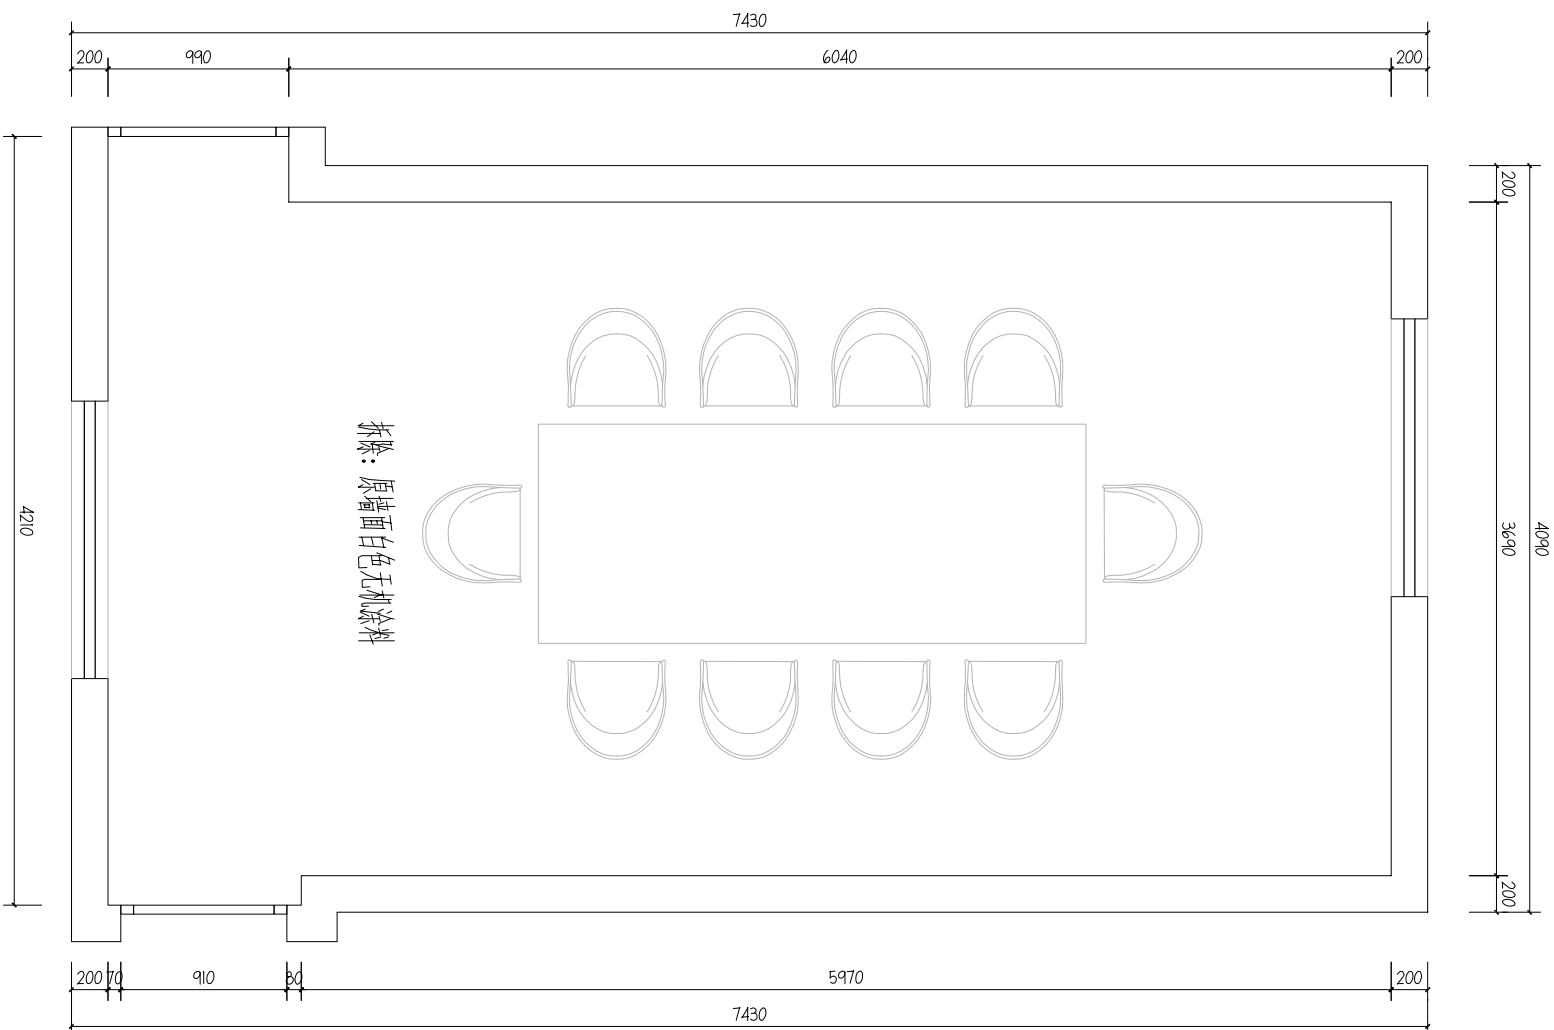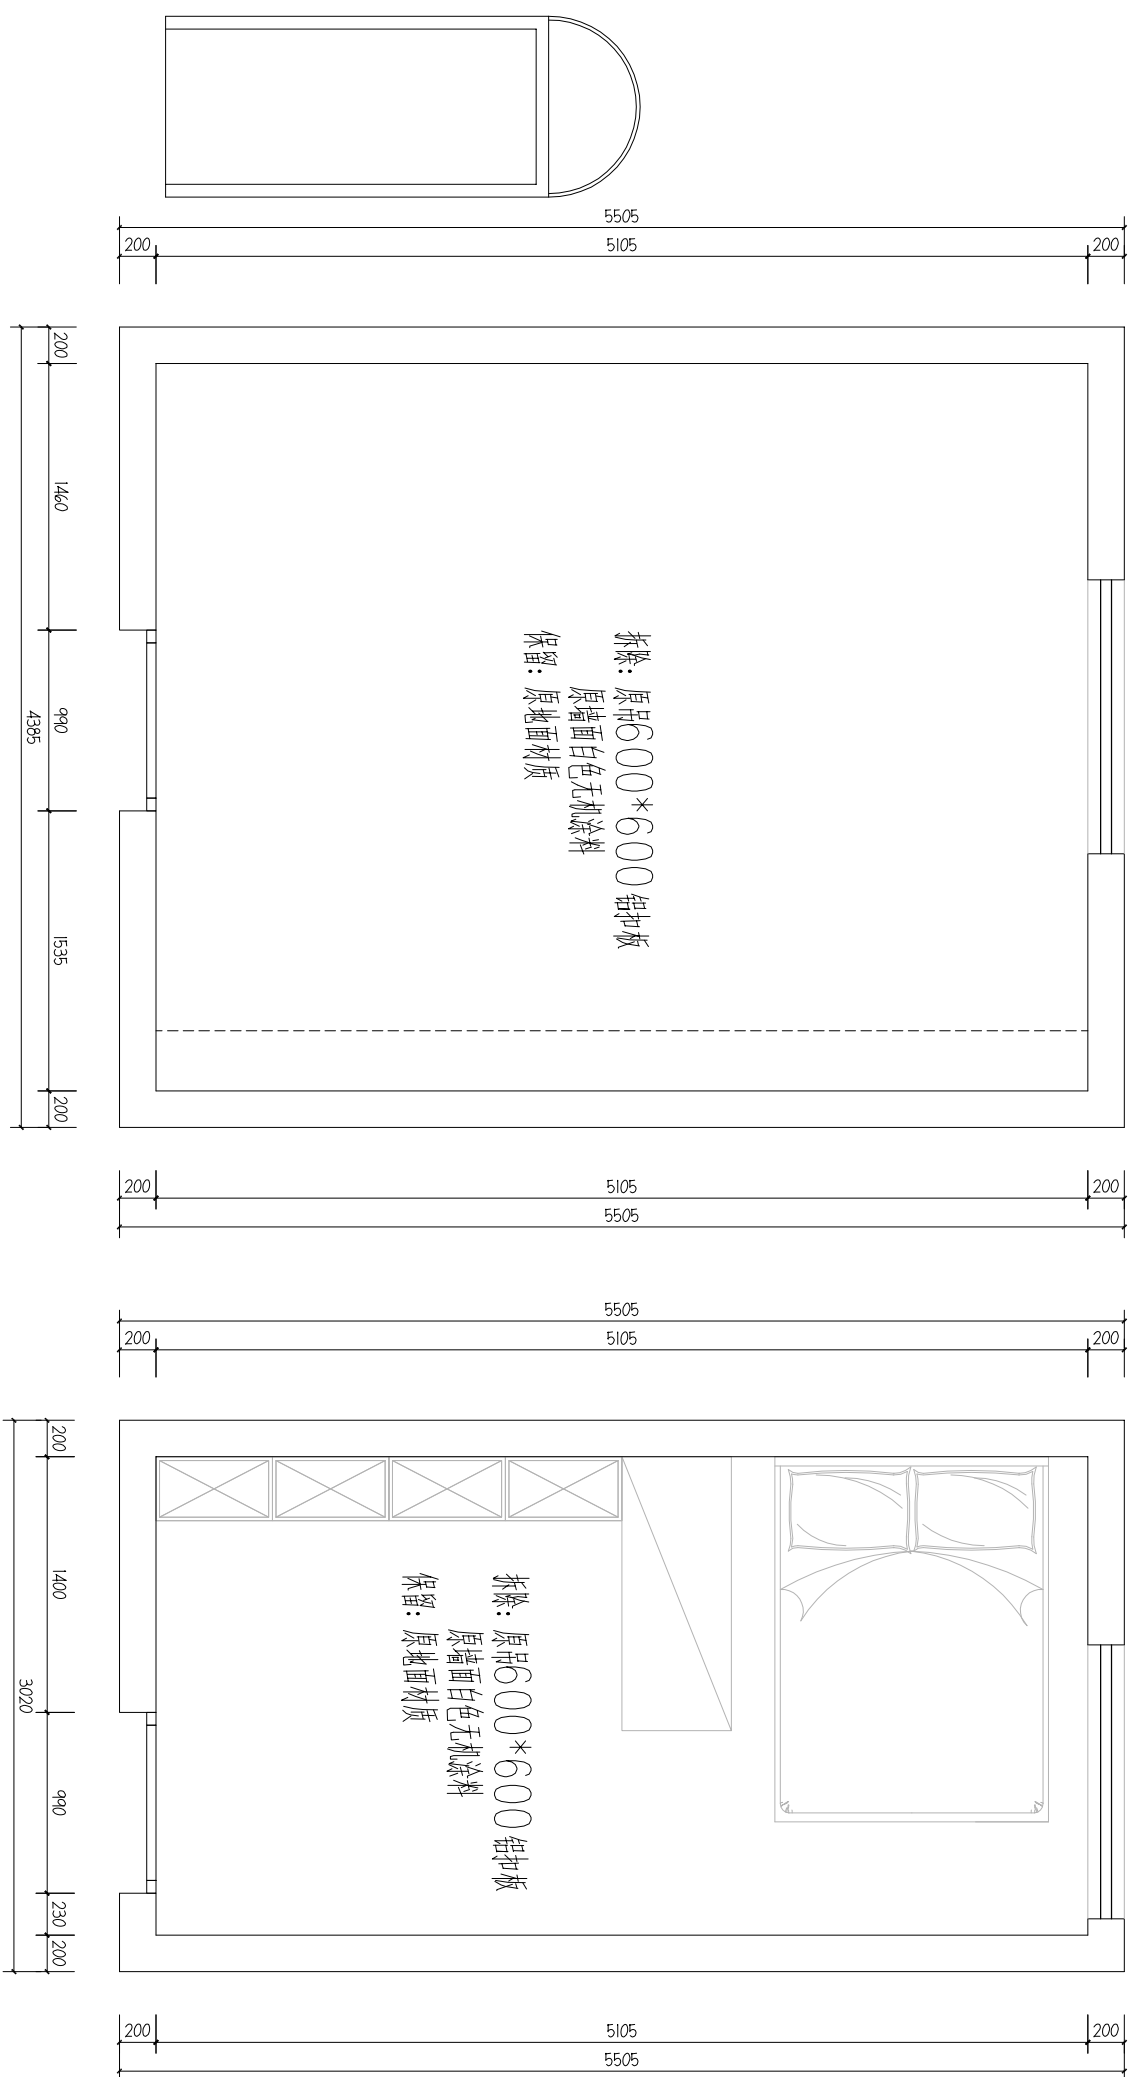

2F

EXISTING PLAN
二楼东侧拆除平面图 SCALE 1:40

 中德勘察设计有限公司 ZHMCK DESIGN SURVEY AND DESIGN CO., LTD 成都市武侯区簇锦中街69号附48号	
甲级工程设计证书编号: A151030621 乙级工程设计证书编号: A251023438	
CASE NOTE	
注册印章	
REGISTERED SEAL	
注册执业栏	
REGISTERED ARCHITECT/ENGINEER	
姓名 NAME	邓成
注册印章号 REGISTERED SEAL NO.	5103062-001
注册证书号 REGISTERED CERTIFICATE NO.	215000941
建设单位: CLIENT	中德勘察设计有限公司
工程名称: PROJECT TITLE	大坪村示范党群服务中心
子项名称: SUB ITEM	
项目总负责人 PROJECT NO.	邓成
审定 APPROVED BY	
审核 AUDIT	徐斌
专业负责人 DISCIPLINE CHIEF	邓成
校对 CHECKED BY	邓成
设计 DESIGNED BY	邹泉
图名: DRAWING TITLE	二楼东侧拆除平面图
设计号 JOB NO.	
图别 JOB CATEGORY	建造
图号 JOB NO.	SPL 02
版本号 JOB NO.	第一版
日期 DATE	202408

注: 所有图纸需经审查机构审查合格后方可施工

注册印章 REGISTERED SEAL

注册印章 REGISTERED SEAL

注册印章 REGISTERED SEAL

注册印章 REGISTERED SEAL

姓名 注册执业栏
NAME REGISTERED ARCHITECT/ENGINEER

注册印章号 5103062-001
REGISTERED SEAL NO.

注册证书号 215000941
REGISTERED CERTIFICATE NO.

建设单位：中睦勘察设计有限公司
CLIENT

工程名称：大坪村示范党群服务中心
PROJECT TITLE

子项名称：SSB 1704

项目总负责人 邓成

审定 徐斌

审核 徐斌

专业负责人 邓成

校对 邓成

设计 邹泉


图名：二楼东侧改后平面图
DRAWING TITLE

二楼东侧改后平面图

EXISTING PLAN

2F

二楼东侧改后平面图 SCALE 1:40

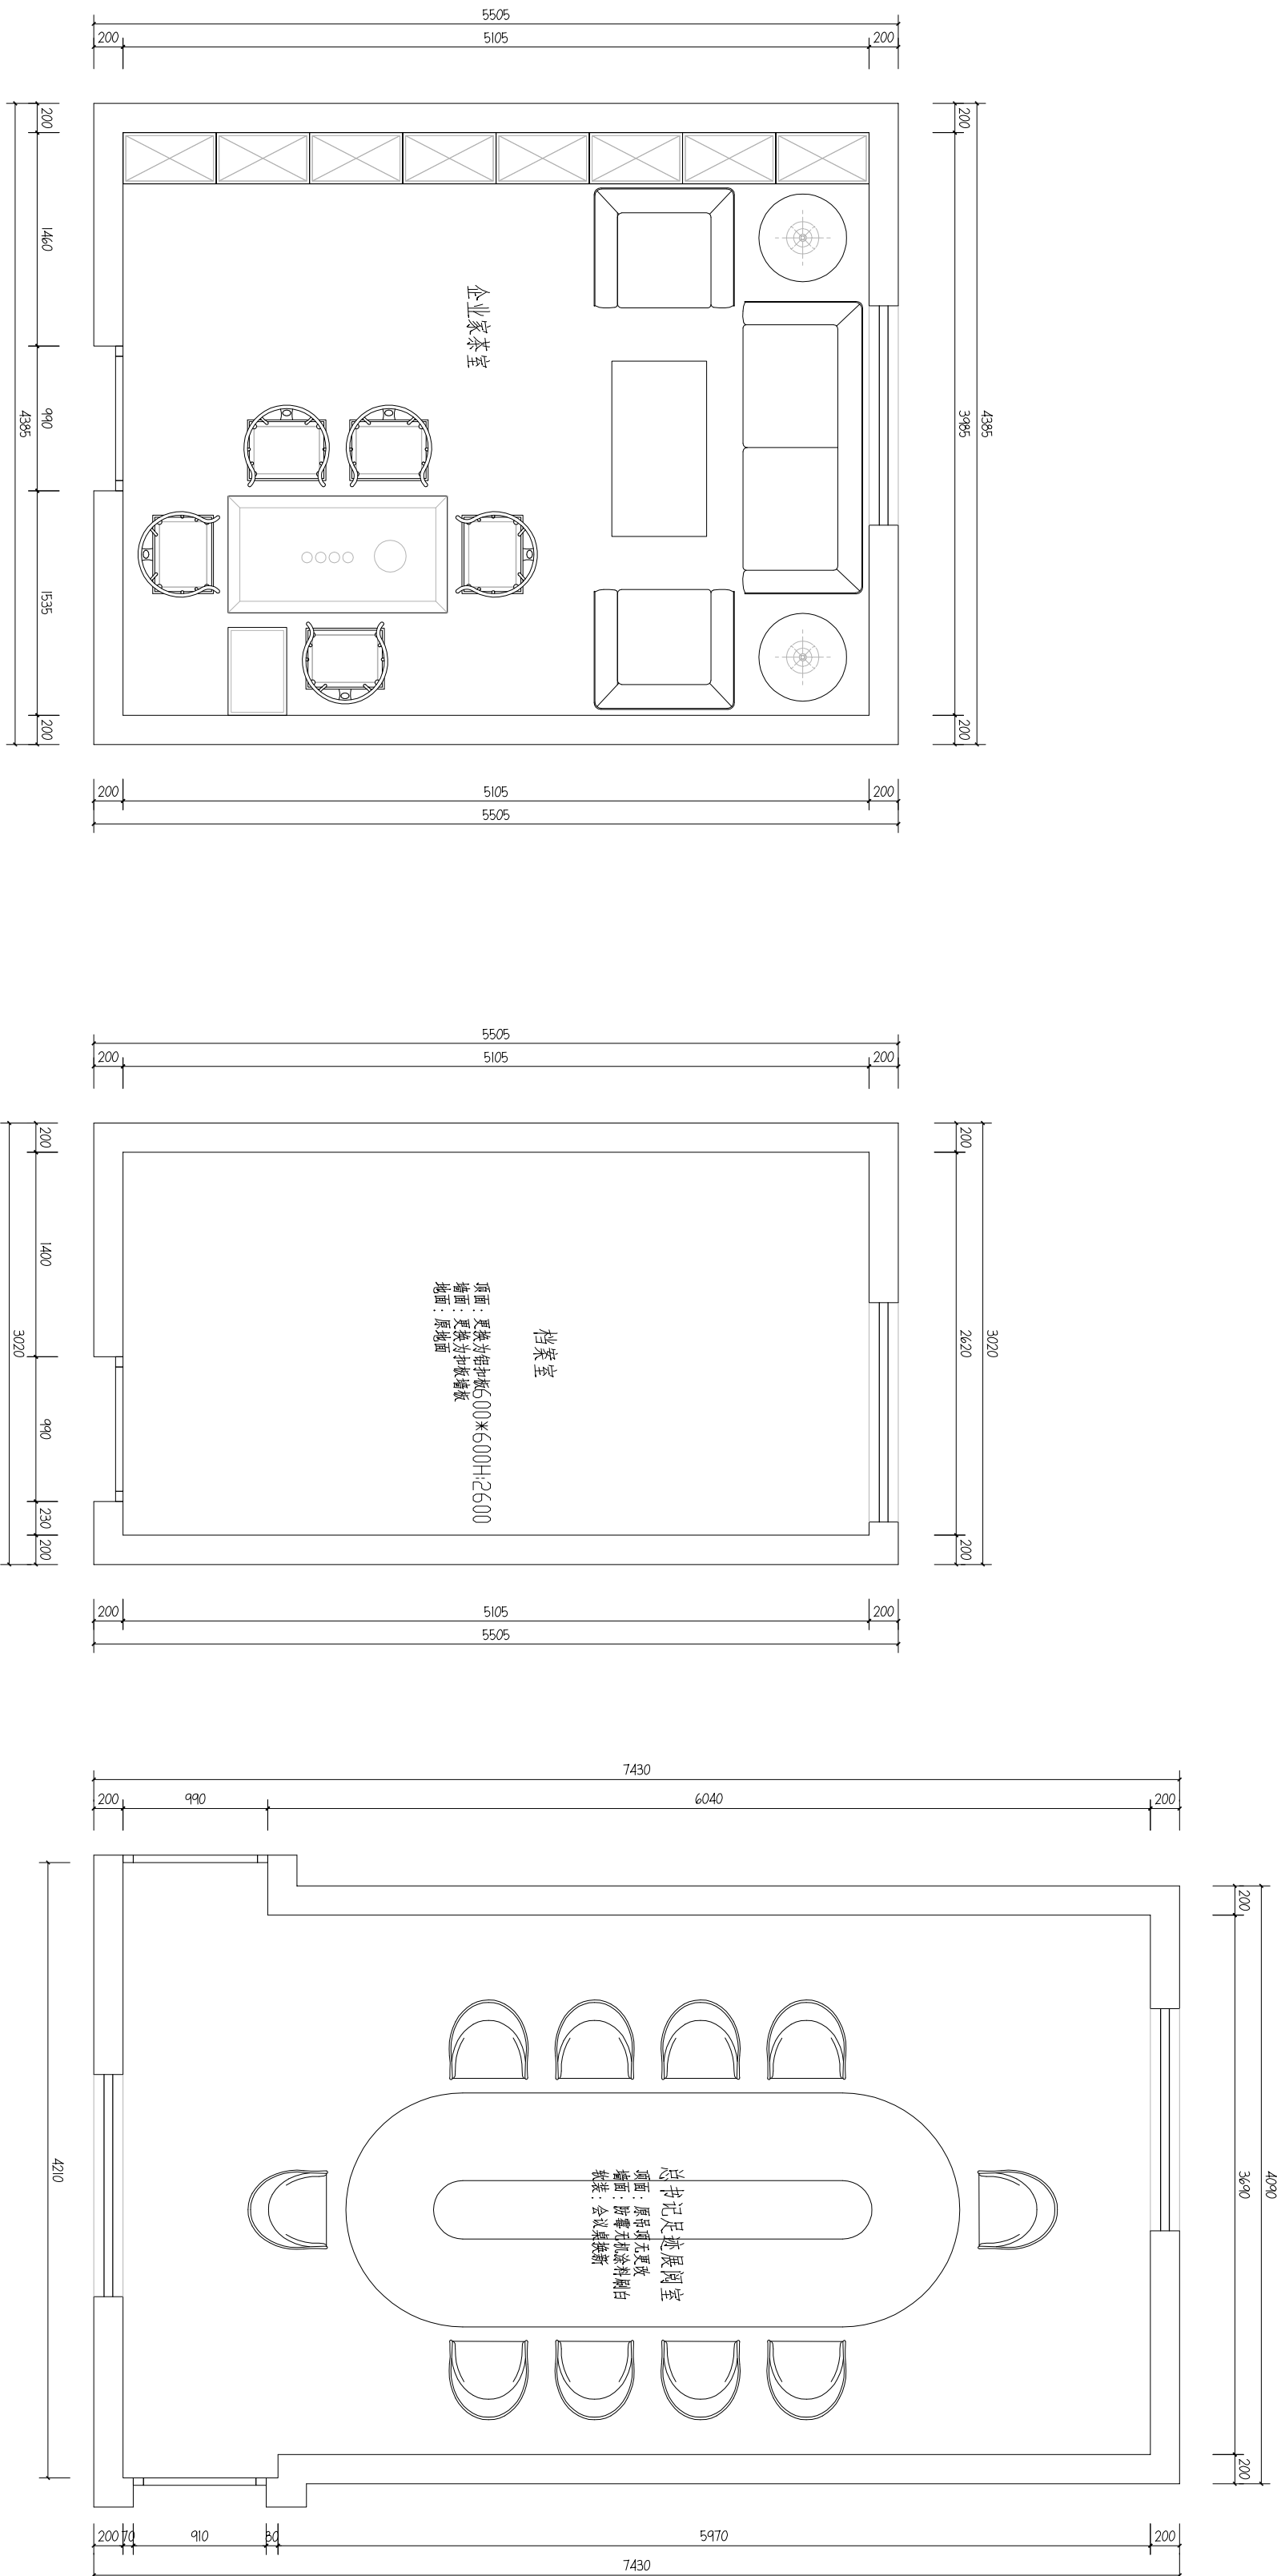

20.4平方米

13.4平方米

26.5平方米

注册印章
REGISTERED SEAL

注册印章
REGISTERED SEAL

姓名
注册执业栏
REGISTERED ARCHITECT/ENGINEER

注册印章号
REGISTERED SEAL NO.

注册证书号
REGISTERED CERTIFICATE NO.

建设单位：
中睦勘察设计有限公司

工程名称：
大坪村示范党群服务中心

子项名称：
SBS 113M

项目总负责人
PROJECT NO.

审定
APPROVED BY

审核
AUDIT

专业负责人
DISCIPLINE CHIEF

校对
CHECKED BY





设计
DESIGNED BY

图名：
SBS 113M

二楼东侧吊顶布置图

设计号 JOB NO.		版本号 VER. NO.	第一版
图别 JOB CATEGORY	建筑	日期 DATE	202408
图号 JOB NO.	SPL 04		

注：所有图纸需经审查机构审查合格后方可施工

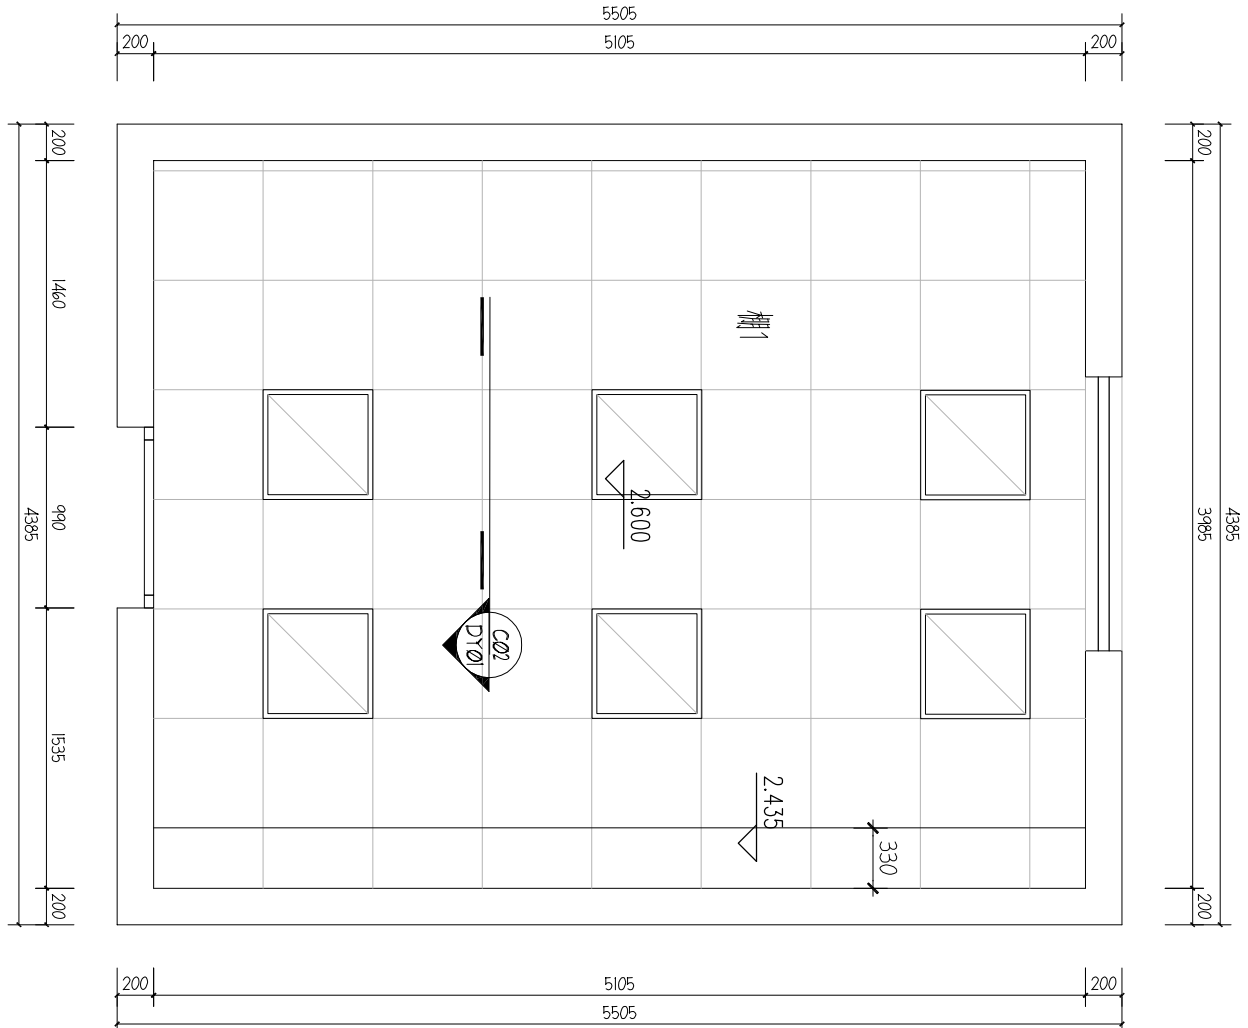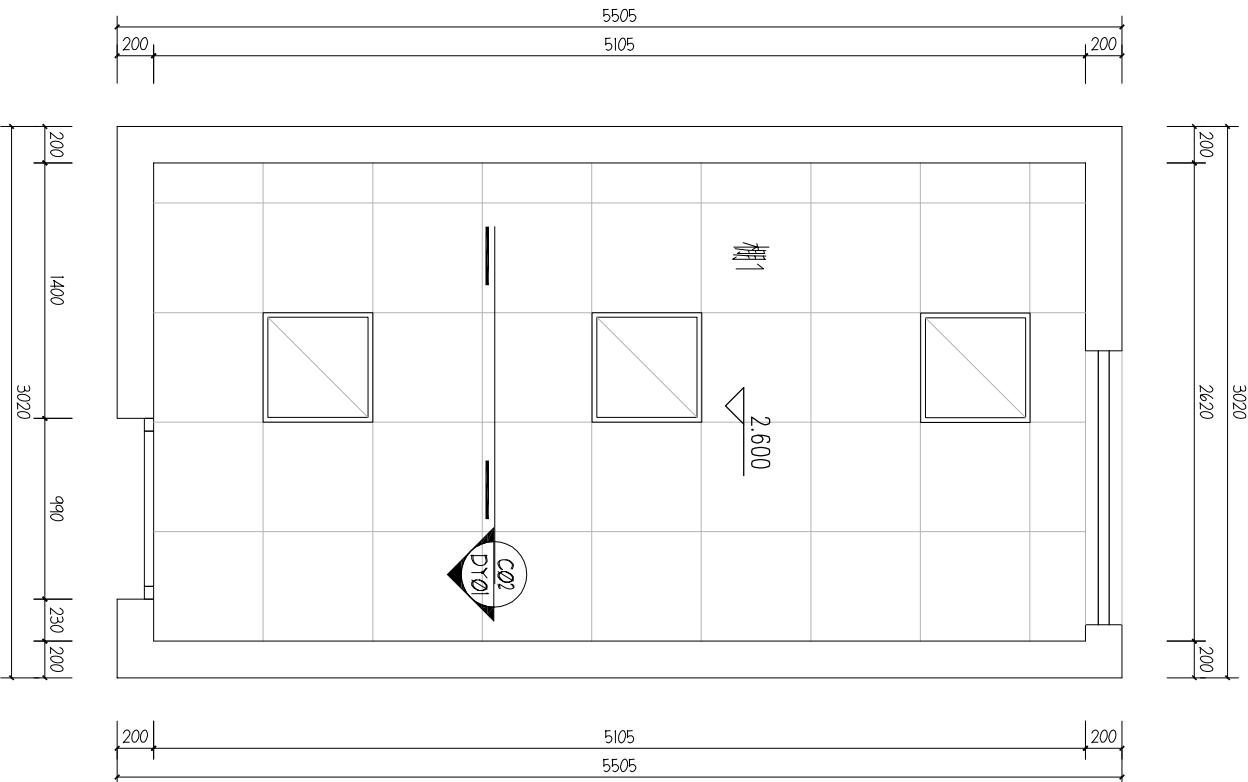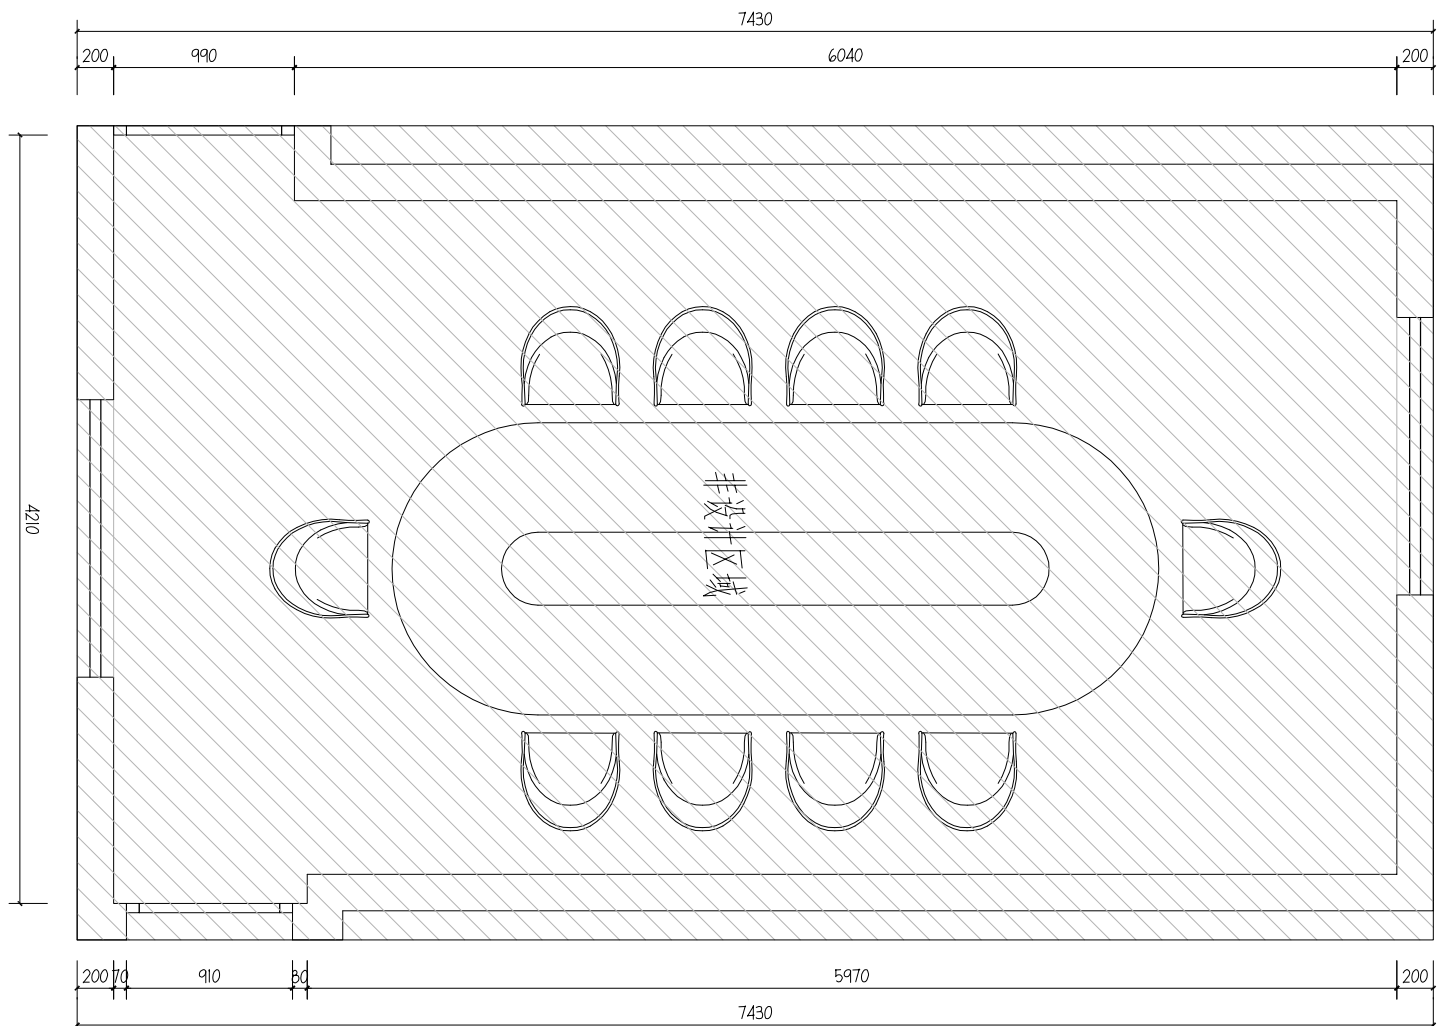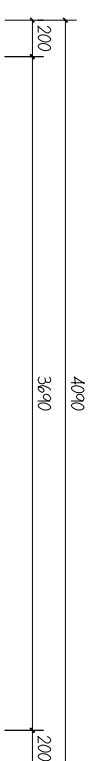

LEGEND: 图例
☒ 600X600/300X300平板灯
☐ 220V/LED/35W/m 4000K

2F
EXISTING PLAN
二楼东侧吊顶布置图
SCALE 1:40



甲级工程设计证书编号: A151030621
乙级工程设计证书编号: A251023438

CAS: NITE

出图专用章

IMAGING SPECIAL SEAL

注册印章

REGISTERED SEAL

注册执业栏
REGISTERED ARCHITECT/ENGINEER

姓名
NAME

注册印章号
REGISTERED SEAL NO.

注册证书号
REGISTERED CERTIFICATE NO.

建设单位: 中德勘察设计有限公司
CLIENT

工程名称: 大坪村示范党群服务中心
PROJECT TITLE

子项名称: 20.4平方米
SUB ITEM

项目总负责人
PROJECT MGR.

审定
APPROVED BY

审核
AUDIT

专业负责人
DISCIPLINE CHIEF

校对
CHECKED BY

设计
DESIGNED BY


图名: 二楼东立面索引图
DRAWING TITLE

2F 二楼东立面索引图

EXISTING PLAN

2F

二楼东立面索引图 SCALE 1:40

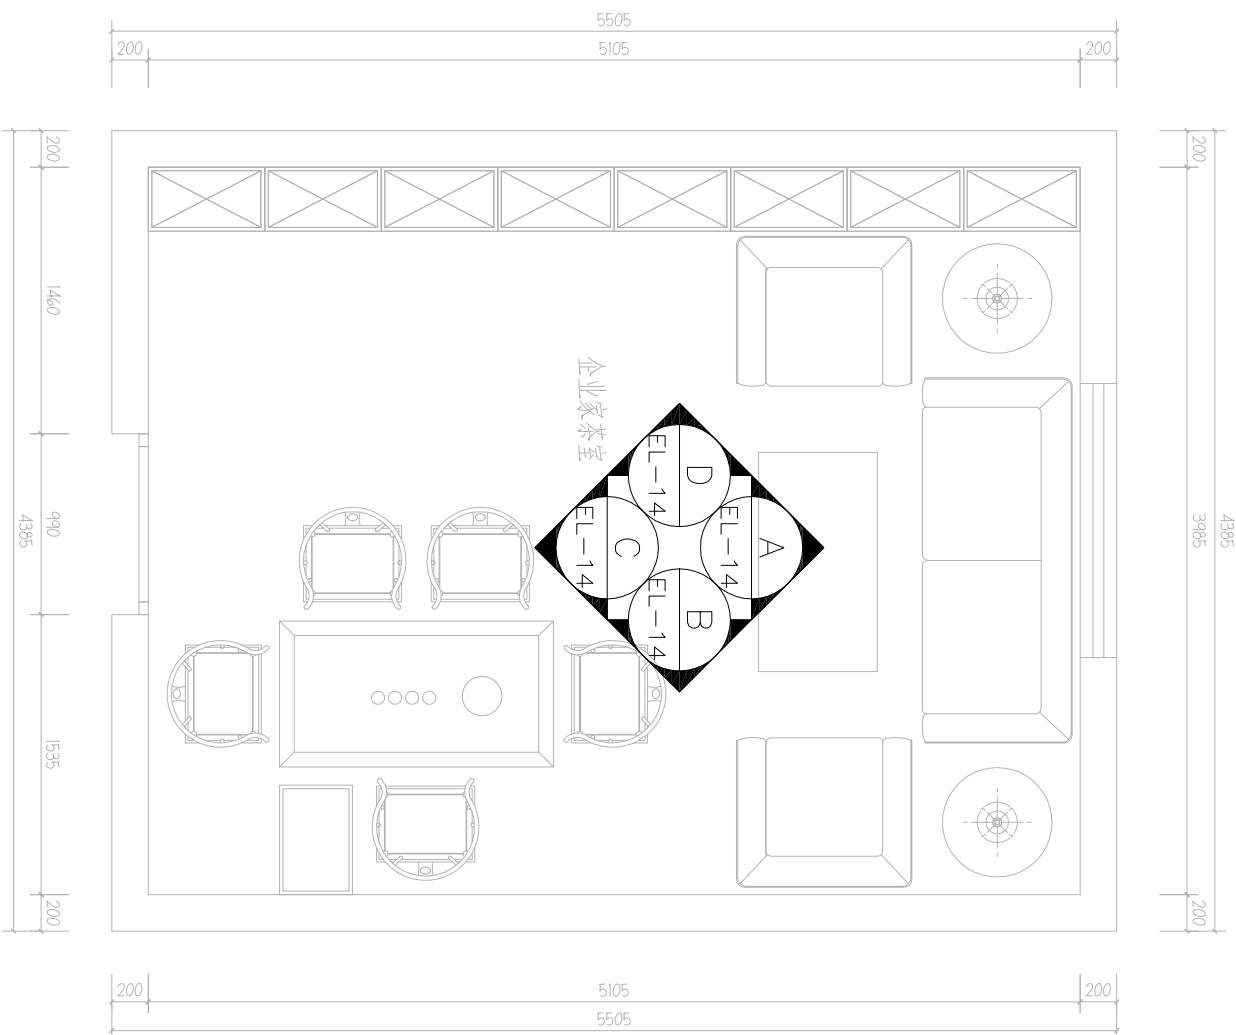

20.4平方米

注: 所有图纸需经审查机构审查合格后方可施工