
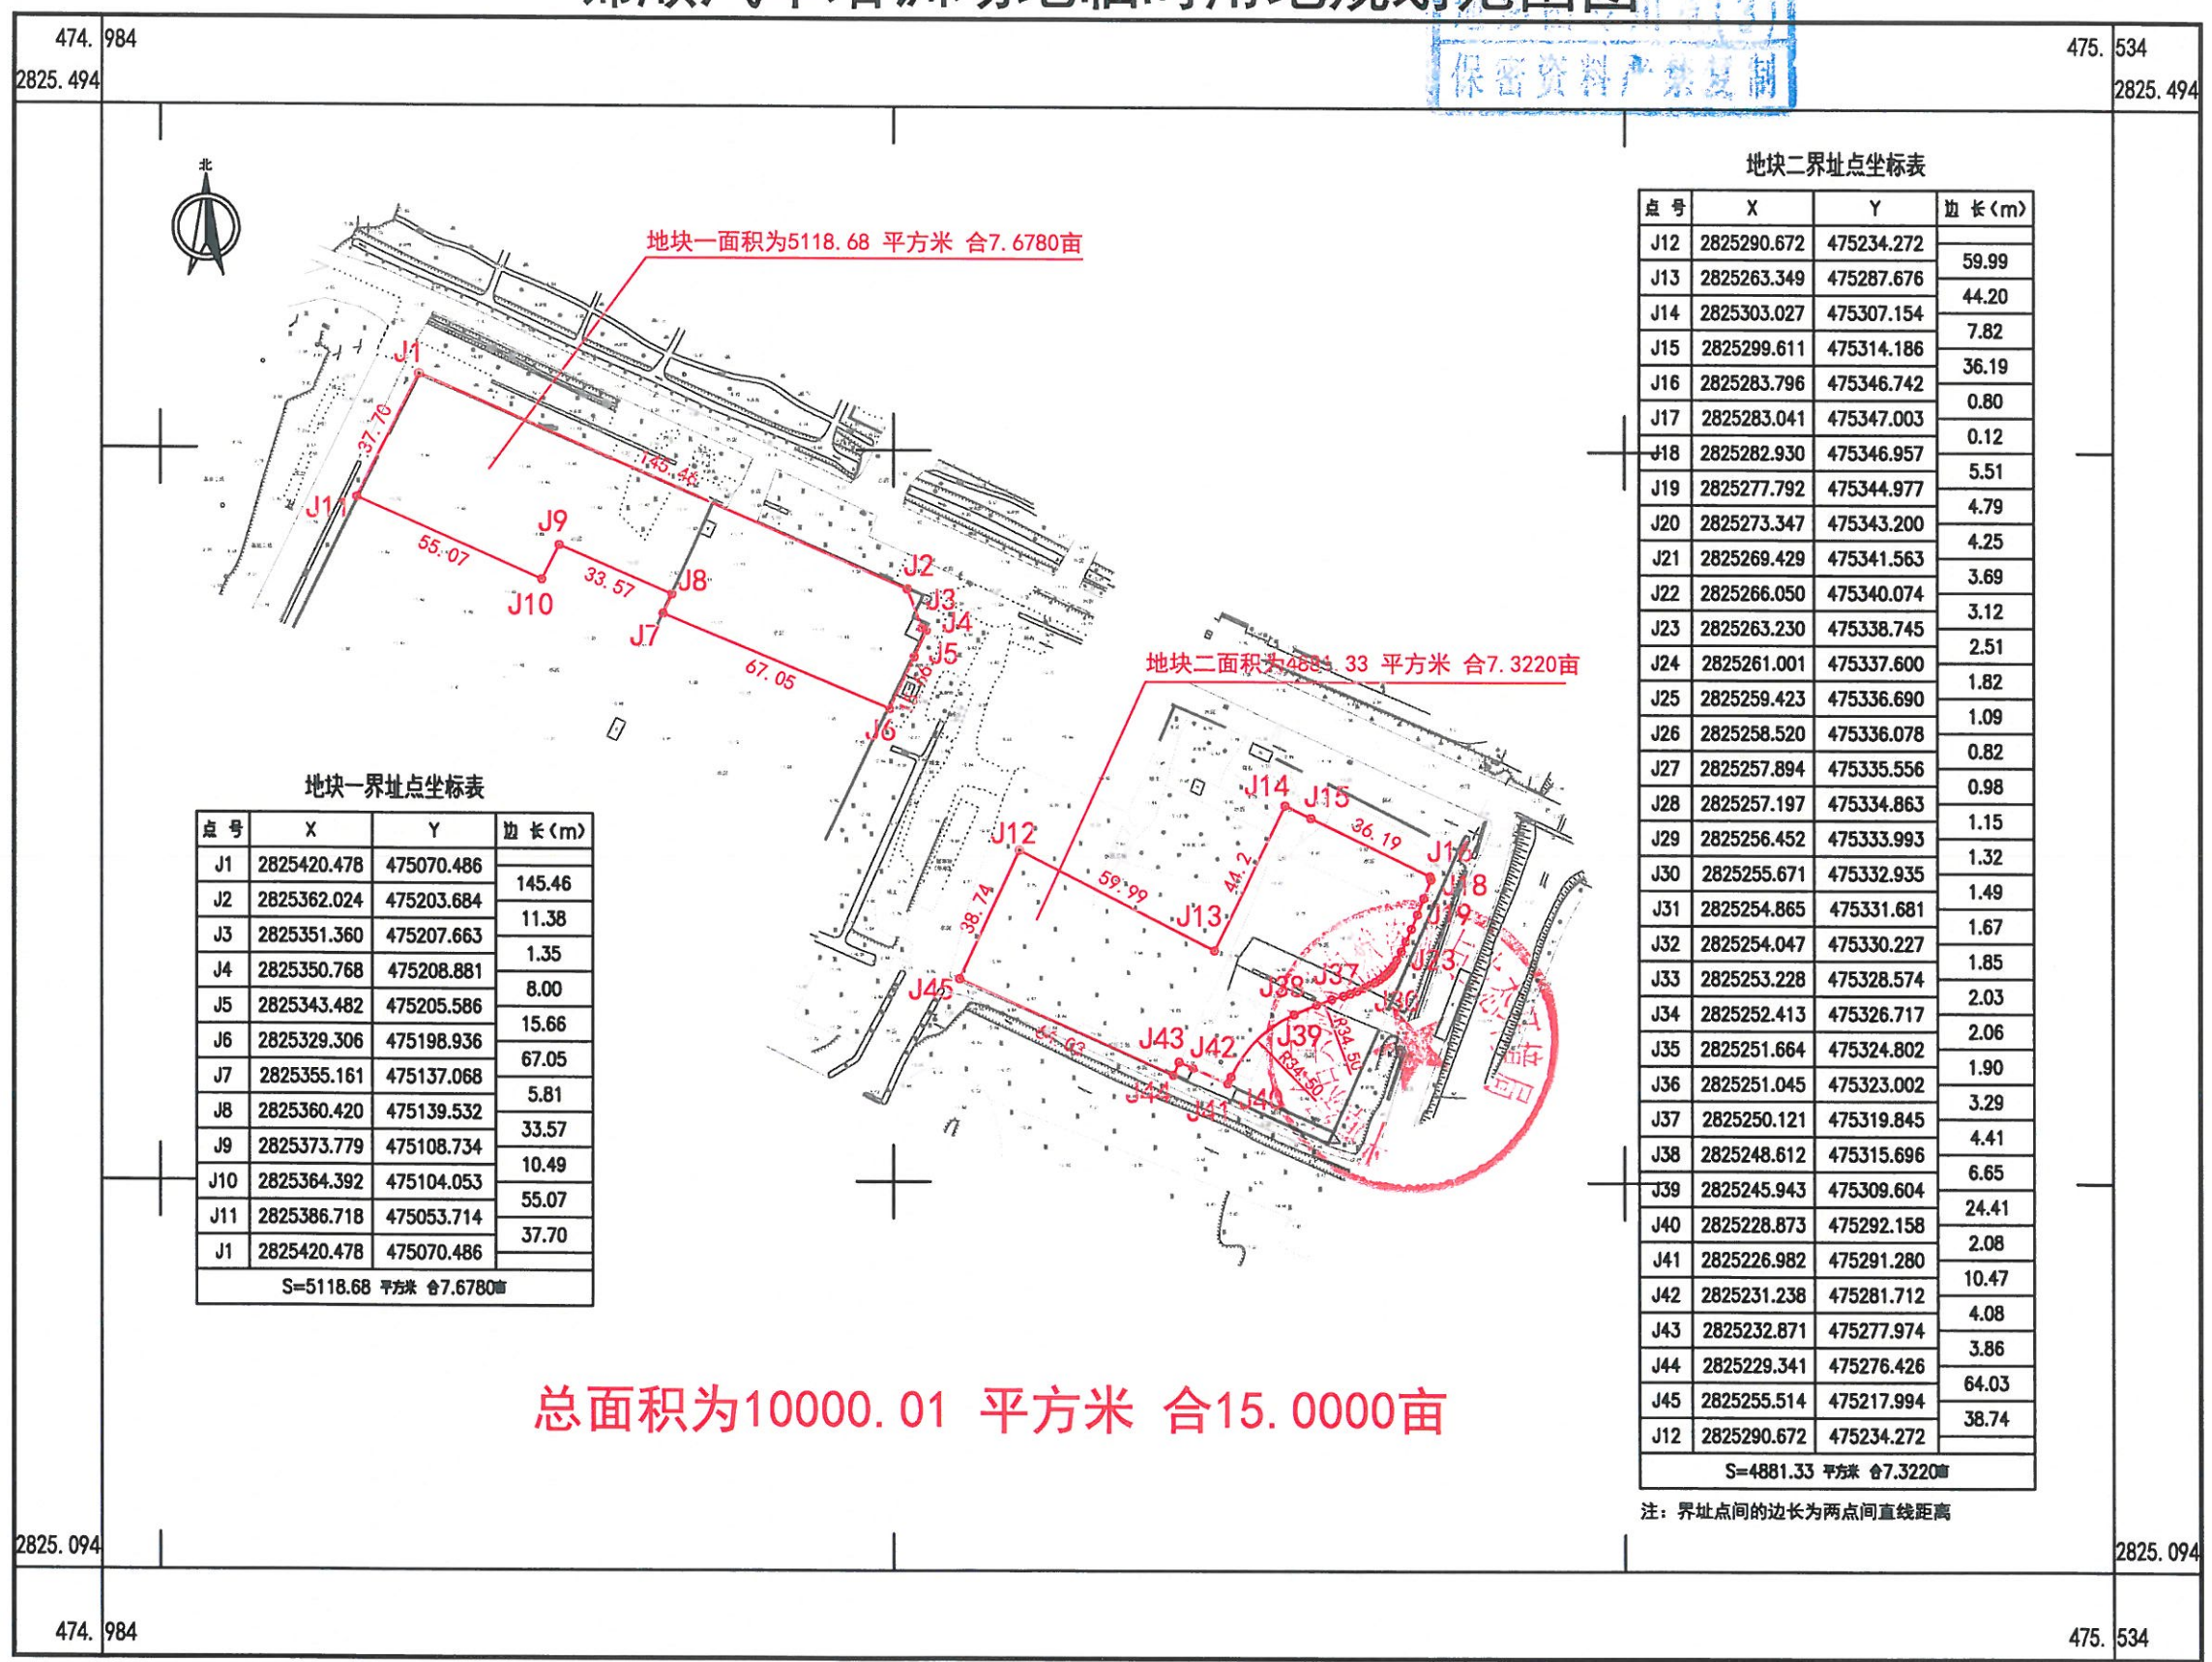


锦顺汽车培训场地临时用地规划范围图

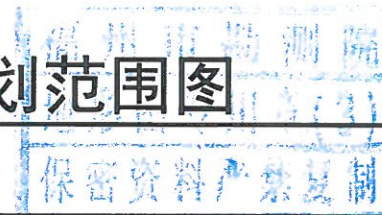

地块一界址点坐标表

点号	X	Y	边长(m)
J1	2825420.478	475070.486	145.46
J2	2825362.024	475203.684	11.38
J3	2825351.360	475207.663	1.35
J4	2825350.768	475208.881	8.00
J5	2825343.482	475205.586	15.66
J6	2825329.306	475198.936	67.05
J7	2825355.161	475137.068	5.81
J8	2825360.420	475139.532	33.57
J9	2825373.779	475108.734	10.49
J10	2825364.392	475104.053	55.07
J11	2825386.718	475053.714	37.70
J1	2825420.478	475070.486	

S=5118.68 平方米 合7.6780亩

地块二界址点坐标表

点号	X	Y	边长(m)
J12	2825290.672	475234.272	59.99
J13	2825263.349	475287.676	44.20
J14	2825303.027	475307.154	7.82
J15	2825299.611	475314.186	36.19
J16	2825283.796	475346.742	0.80
J17	2825283.041	475347.003	0.12
J18	2825282.930	475346.957	5.51
J19	2825277.792	475344.977	4.79
J20	2825273.347	475343.200	4.25
J21	2825269.429	475341.563	3.69
J22	2825266.050	475340.074	3.12
J23	2825263.230	475338.745	2.51
J24	2825261.001	475337.600	1.82
J25	2825259.423	475336.690	1.09
J26	2825258.520	475336.078	0.82
J27	2825257.894	475335.556	0.98
J28	2825257.197	475334.863	1.15
J29	2825256.452	475333.993	1.32
J30	2825255.671	475332.935	1.49
J31	2825254.865	475331.681	1.67
J32	2825254.047	475330.227	1.85
J33	2825253.228	475328.574	2.03
J34	2825252.413	475326.717	2.06
J35	2825251.664	475324.802	1.90
J36	2825251.045	475323.002	3.29
J37	2825250.121	475319.845	4.41
J38	2825248.612	475315.696	6.65
J39	2825245.943	475309.604	24.41
J40	2825228.873	475292.158	2.08
J41	2825226.982	475291.280	10.47
J42	2825231.238	475281.712	4.08
J43	2825232.871	475277.974	3.86
J44	2825229.341	475276.426	64.03
J45	2825255.514	475217.994	38.74
J12	2825290.672	475234.272	

S=4881.33 平方米 合7.3220亩

注：界址点间的边长为两点间直线距离

2010年7月数字化成图
 2000国家大地坐标系
 1985国家高程基准
 2009年福州基础地理信息数据图式
 加盖福州市勘测院地形图蓝章，方为正式材料

1:2000

2011.2.3