

万吨冷链产业园总体规划



备注：
本图版权归福建中恒华建筑设计有限公司所有，未经本公司书面许可，不得复制或用于其他用途。
THE OWNERSHIP OF THE COPYRIGHT IN THIS DRAWING IS RETAINED BY ZHHZ. WRITTEN CONSENT MUST BE OBTAINED BEFORE ANY USE OR REPRODUCTION OF THE DRAWING.

施工图审查合格章：
施工图审查合格章：
图章专用章：

注册建筑师章：
注册结构师章：

注册造价工程师：

注册监理工程师：

工程名称：
万吨冷链产业园总体规划

建设单位：
福建中恒华实业有限公司

工程编号：
日期：2020.07



- 图例
- 建筑轮廓线
 - 用地红线
 - 绿地
 - 地下室界线
 - 围墙线
 - 机动车位
 - 快充电桩车位
 - 慢充电桩车位
 - 非机动车位

1. 坐标及高程说明：
坐标采用2000国家大地坐标系，高程采用1985国家高程基准。
2. 建筑高度说明：
(屋面材料层按200mm计算)
H1为消防高度，室外地面至平屋面高度。
H2为规划高度，室外地面至女儿墙顶高度。
3. 消防道路说明：
消防道路最小宽度为4m，消防道路转弯半径为12m。
4. 人防说明：
办公楼建筑面积为3976m²，宿舍楼建筑面积1687m²。
应建的人防面积为：(3976+1687)×7%=396.4m²，小于400m²。
根据《福建省人民防空条例》，由建设单位申请易地建设，以平潭综合实验区人民防空办公室审批为准。
5. 停车位计算：办公楼及宿舍楼
机动车：0.8x (3976+1687) / 100=45.3部
需机动车停车位45.3部，实际停车46部。
非机动车：4x (3976+1687) / 100=226.5部
需非机动车停车位226.5部，实际停车227部。
汽车快充充电桩车位计算：46x10%=4.6部，实际设置5部。
汽车慢充电桩车位计算：46x20%=9.2部，实际设置10部。
6. 根据《福建省综合[2017]194号《平潭综合实验区海绵城市建设管理暂行办法》，年径流总量控制率不小于75%。

平潭综合实验区“粮食园区”二期



主要技术经济指标

项目	指标	备注
总用地面积	34858 m ²	
实际用地面积	34858 m ²	
总建筑面积	53222 m ²	
地上建筑面积	52079 m ²	
地下建筑面积	1143 m ²	
计容建筑面积	53875 m ²	
不计容建筑面积	1143 m ²	消防水池及水泵房
建筑占地面积	18375 m ²	
建筑密度	52.7%	
建筑系数	53.2%	
容积率	1.55	
绿地面积	3486 m ²	
绿地率	10.0%	
停车位		
机动车位	46个	
非机动车位	227个	
配套设施占地面积	1266 m ²	办公楼和宿舍楼
配套设施占比例	3.6%	不大于7%
配套设施建筑面积	5663 m ²	办公楼和宿舍楼
配套设施建筑面积比例	10.3%	不大于20%

建筑面积一览表 (单位:m²)

建筑名称	占地面积	建筑面积	计容面积	层数	备注
办公楼	816	3976	3976	5-6	
宿舍楼	450	1687	1687	4	
1#水产品冷库	7085	20240	21136	1-3	含新建建筑及占地面积
2#水产品冷库及加工区	9976	27275	27032	1-3	含地下消防水池面积143m ²
收发室	48	44	44	1	
合计	18375	53222	53875		

构筑物占地面积一览表 (单位:m²)

构筑物名称	占地面积	备注
围墙化粪池	60	埋地式
埋地水池	60	埋地式
污水处理池	60	埋地式
合计	180	

总平面图 1:500

万吨冷链产业园总体规划



注：本图版权归福建中恒华建筑设计有限公司所有，除本工程外不得用于其他用途和复制，必须获得本公司的书面许可。
THE OWNERSHIP OF THE COPYRIGHT IN THIS DRAWING IS RETAINED BY ZHYZ, WRITTEN CONSENT MUST BE OBTAINED BEFORE ANY USE OR REPRODUCTION OF THE DRAWING.

施工图审查批准书号：
施工图审查合格书号：

图例：

注：消防验收标准：

注：消防验收标准：

日期： 版本：

工程名称：
万吨冷链产业园总体规划


建设单位：
福建发实业有限公司

设计	设计
工程负责人	设计
专业负责人	设计
审核	设计
校核	设计
设计	设计
制图	设计
审核	设计

拟变更总平面图

工程编号	设计01
日期	2021.03

图幅：A1

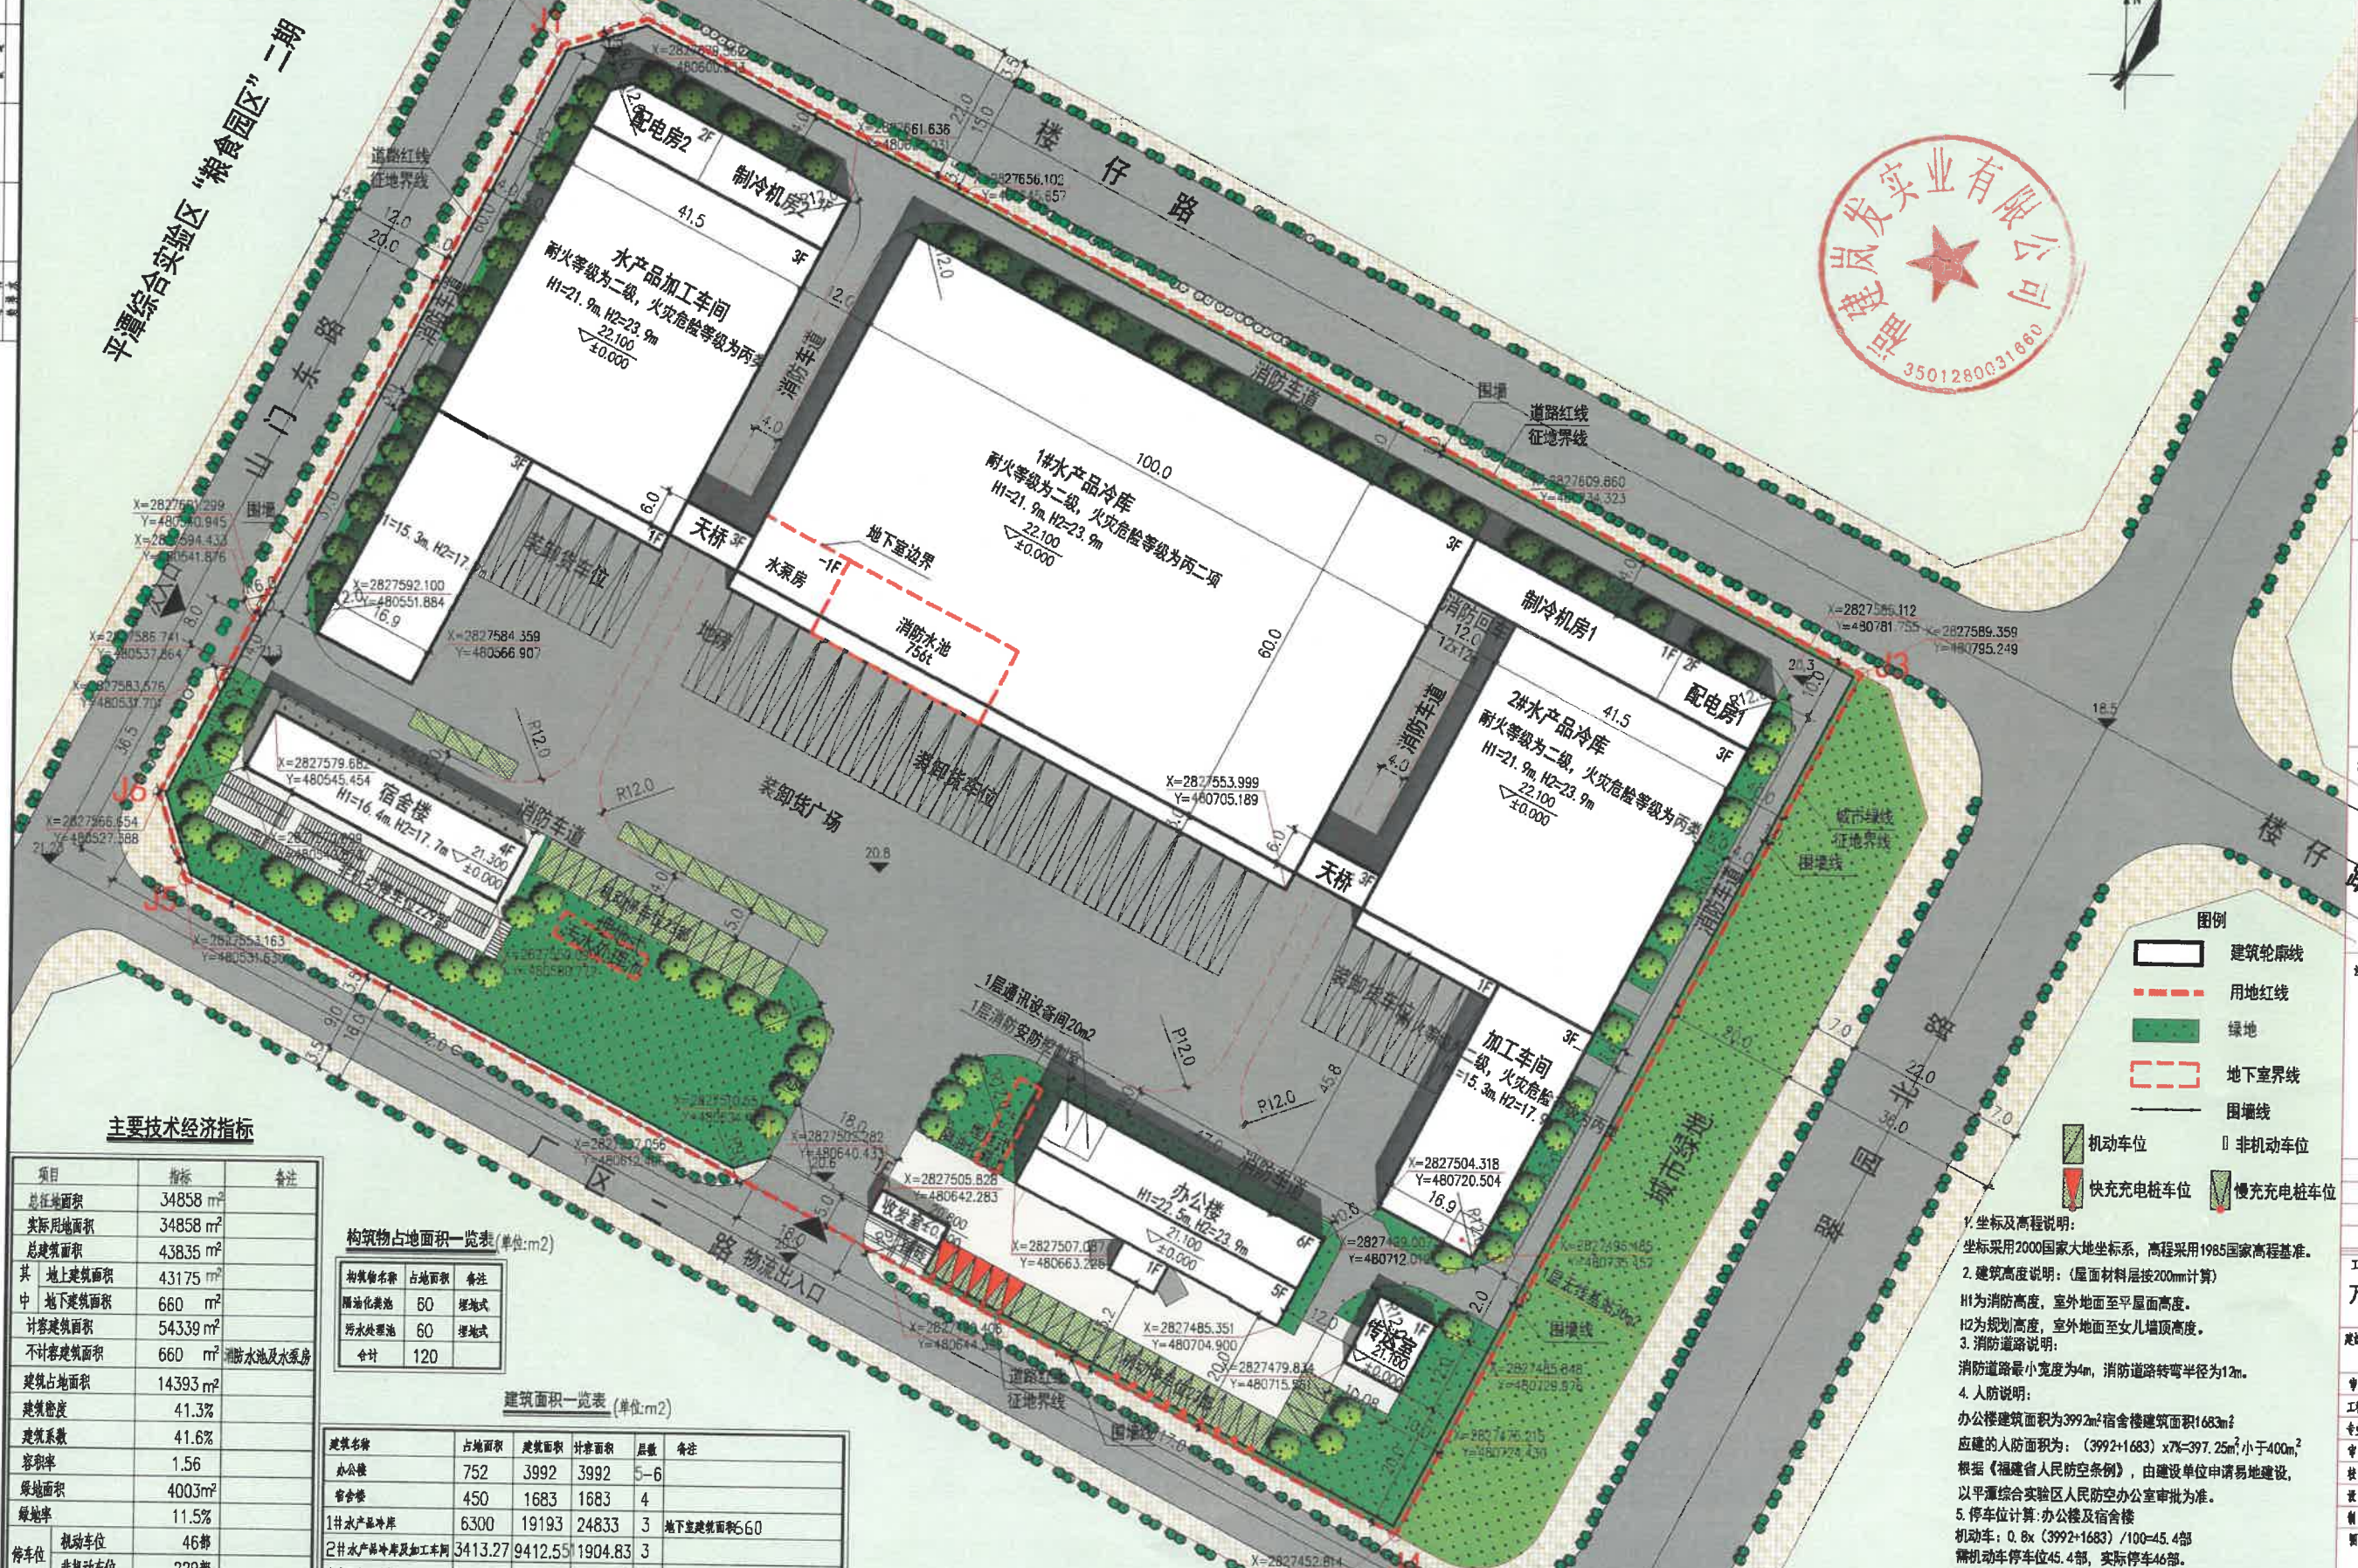

主要技术经济指标

项目	指标	备注
总用地面积	34858 m ²	
实际用地面积	34858 m ²	
总建筑面积	43835 m ²	
其中地上建筑面积	43175 m ²	
地下建筑面积	660 m ²	
计容积率建筑面积	54339 m ²	
不计容积率建筑面积	660 m ²	消防水池及水泵房
建筑占地面积	14393 m ²	
建筑密度	41.3%	
建筑系数	41.6%	
容积率	1.56	
绿地面积	4003 m ²	
绿地率	11.5%	
停车位	46个	
机动车位	46个	
非机动车位	229个	
配套设施占地面积	1202 m ²	办公楼和宿舍楼
配套设施占地比例	3.5%	不大于7%
配套设施建筑面积	5675 m ²	办公楼和宿舍楼
配套设施建筑面积比例	10.5%	不大于20%

构筑物占地面积一览表(单位:m²)

构筑物名称	占地面积	备注
消防水池	60	埋地式
污水处理池	60	埋地式
合计	120	

建筑面积一览表(单位:m²)

建筑名称	占地面积	建筑面积	计容积率	层数	备注
办公楼	752	3992	3992	5-6	
宿舍楼	450	1683	1683	4	
1#水产品冷库	6300	19193	24833	3	地下室建筑面积660
2#水产品冷库及加工车间	3413.27	9412.55	1904.83	3	
水产品加工车间	3308.42	9388.86	1761.47	3	
传达室	121	121	121	1	
收发室	48	44	44	1	
合计	14393	43835	54339		

拟变更总平面图 1:500

万吨冷链产业园变更内容说明

原报批总平面图



拟变更总平面图




万吨冷链产业园的建设单位福建岚发实业有限公司根据自身的开发需要，为了减小冷库的存储量，减小制冷剂的用量，根据工艺要求及平潭的气候条件，拟将原有报批总平提出变更，变更内容如下：

1. 为使办公区便于管理，方便员工收取信件包裹等物品，在地块东南角原宿舍楼的位置增设传达室。
2. 原来宿舍楼位于地块的东南角，东西朝向不好，不利于通风，将宿舍楼移至西南角，南北朝向布置，以利通风采光。
3. 应工艺及消防要求，此处厂内外高差较小，且原有山门东路中间的消防应急出入口不能与厂区内道路合理地贯通，故将次入口移到山门东路地块的西南角。
4. 为减小冷库存储容量，减少制冷剂用量，将2#水产品冷库及加工区改为水产品加工车间，长度及宽度变小（具体尺寸详单体平面变更图）。
5. 根据工艺要求，将此处的制冷机房移到东北角制冷机房。
6. 因平潭风较大，本地块的东南角增设一栋2#水产品冷库及加工车间。
7. 为方便车辆出入，将厂区铭牌移到中间，分开车流的出入方向。
8. 根据建设单位建设进度，减小开挖量，将消防水池及水泵房移到1#水产品冷库的封闭月台底下。变更后的指标与未变更的指标，符合出让合同要求。

原批复鸟瞰图



拟变更鸟瞰图

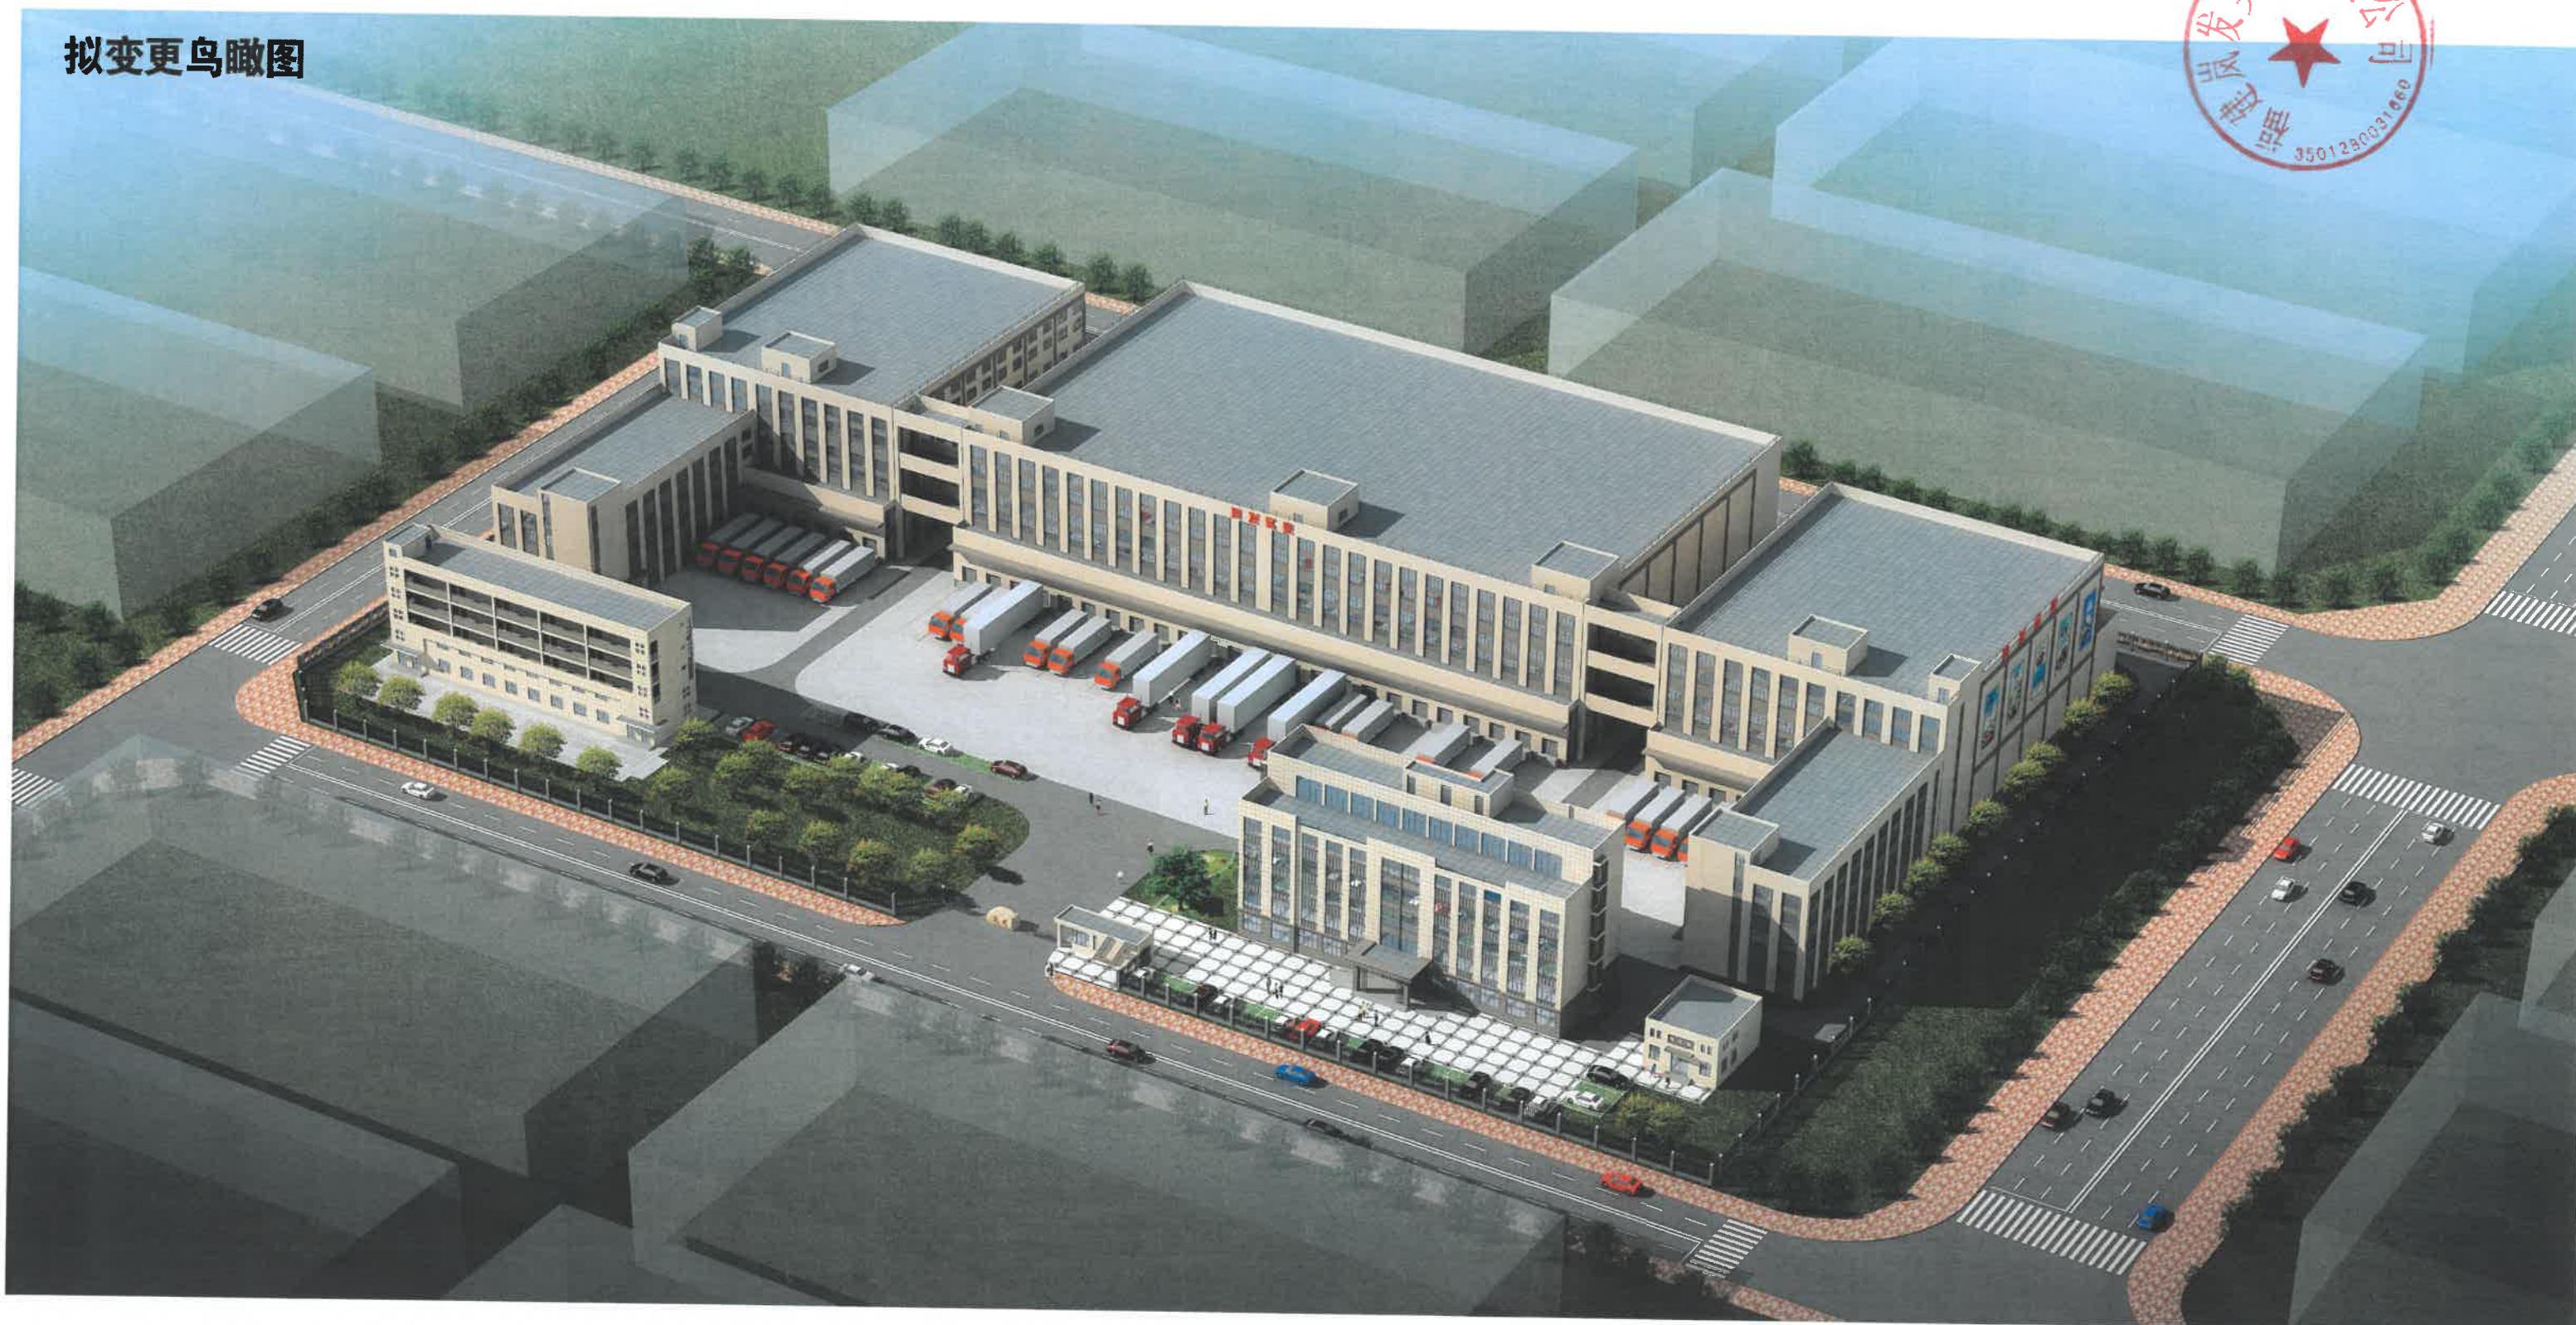

万吨冷链产业园鸟瞰图变更内容说明

原报批鸟瞰图



拟变更鸟瞰图



万吨冷链产业园的建设单位福建岚发实业有限公司根据自身的开发需要，为了减小冷库的存储量，减小制冷剂的用量，根据工艺要求及平潭的气候条件，拟将原有报批总平提出变更，鸟瞰图根据拟变更总平面图变更如下：


1. 为使办公区便于管理，方便员工收取信件包裹等物品，在地块东南角原宿舍楼的位置增设传达室。
2. 原来宿舍楼位于地块的东南角，东西朝向不好，不利于通风，将宿舍楼移至西南角，南北朝向布置，以利通风采光。
3. 应工艺要求，此处厂内外高差较小，且原有北侧楼仔路次入口不到20米处设有公交站，不利于道路开口，将次入口移到山门东路地块的西南角。
4. 为减小冷库存储容量，减少制冷剂用量，将2#水产品冷库及加工区改为水产品加工车间，长度及宽度变小（具体尺寸详单体平面变更图）。
5. 根据工艺要求，将此处的制冷机房移到东北角制冷机房。
6. 因平潭风较大，本地块的东南角增设一栋2#水产品冷库及加工车间。
7. 为方便车辆出入，将厂区铭牌移到中间，分开车流的出入方向。

变更后的指标与未变更的指标，符合出让合同要求。

万吨冷链产业园主要技术经济指标变更说明

原报批主要技术经济指标

拟变更主要技术经济指标

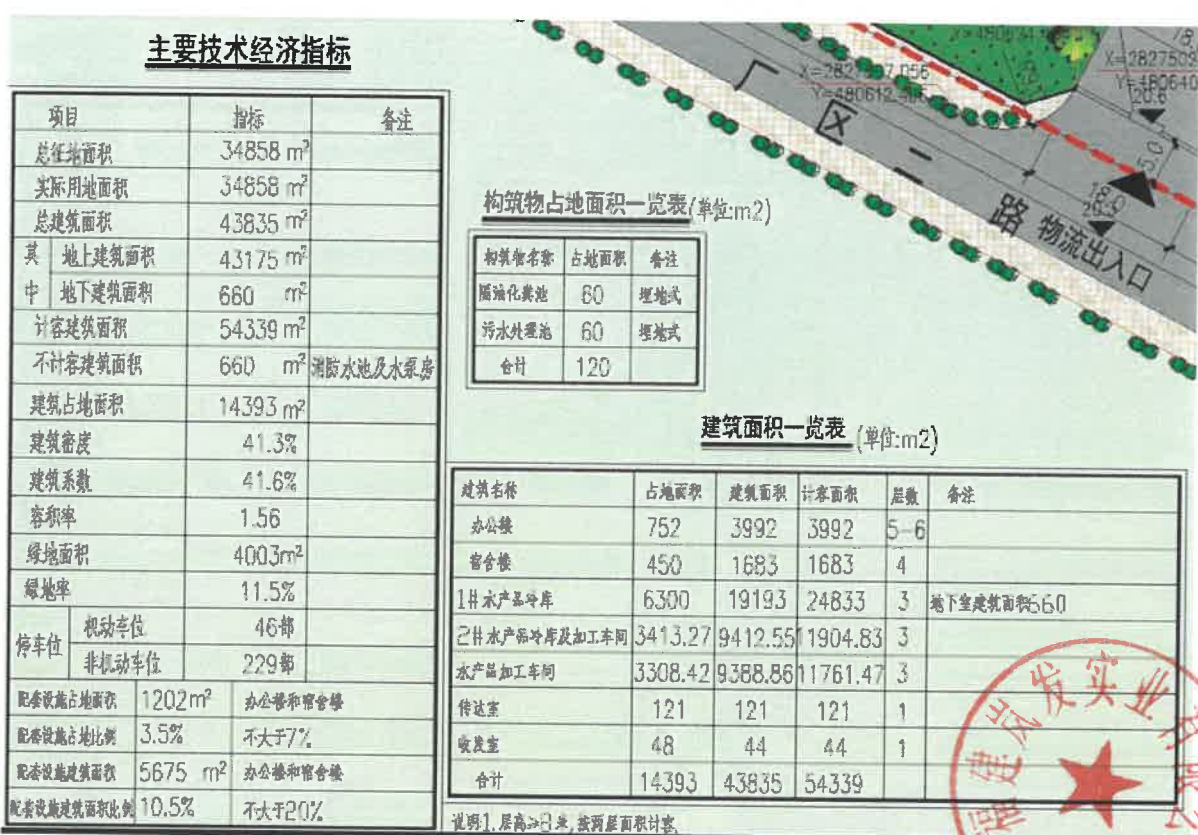

根据总平面图调整，主要技术经济指标也相应调整，原报批指标及拟变更指标对比如下，变更后的指标与未变更的指标，符合出让合同要求。

项目	原报批指标	拟变更指标
总建筑面积	53222 m ²	43835m ²
地上建筑面积	52079 m ²	43175 m ²
地下建筑面积	1143 m ²	660 m ²
计容建筑面积	53875 m ²	54339 m ²
不计容建筑面积	1143 m ²	660 m ²
建筑占地面积	18375 m ²	14393 m ²
建筑密度	52.7%	41.3%
建筑系数	53.2%	41.6%
容积率	1.55	1.56

项目	原报批指标	拟变更指标
绿地面积	3486 m ²	4003 m ²
绿地率	10.0%	11.5%
机动车停车位	46部	46部
非机动车停车位	227部	229部
配套设施占地面积	1266 m ²	1202 m ²
配套设施占地比例	3.6%	3.5%
配套设施建筑面积	5663 m ²	5675 m ²
配套设施建筑面积比例	10.3%	10.5%