


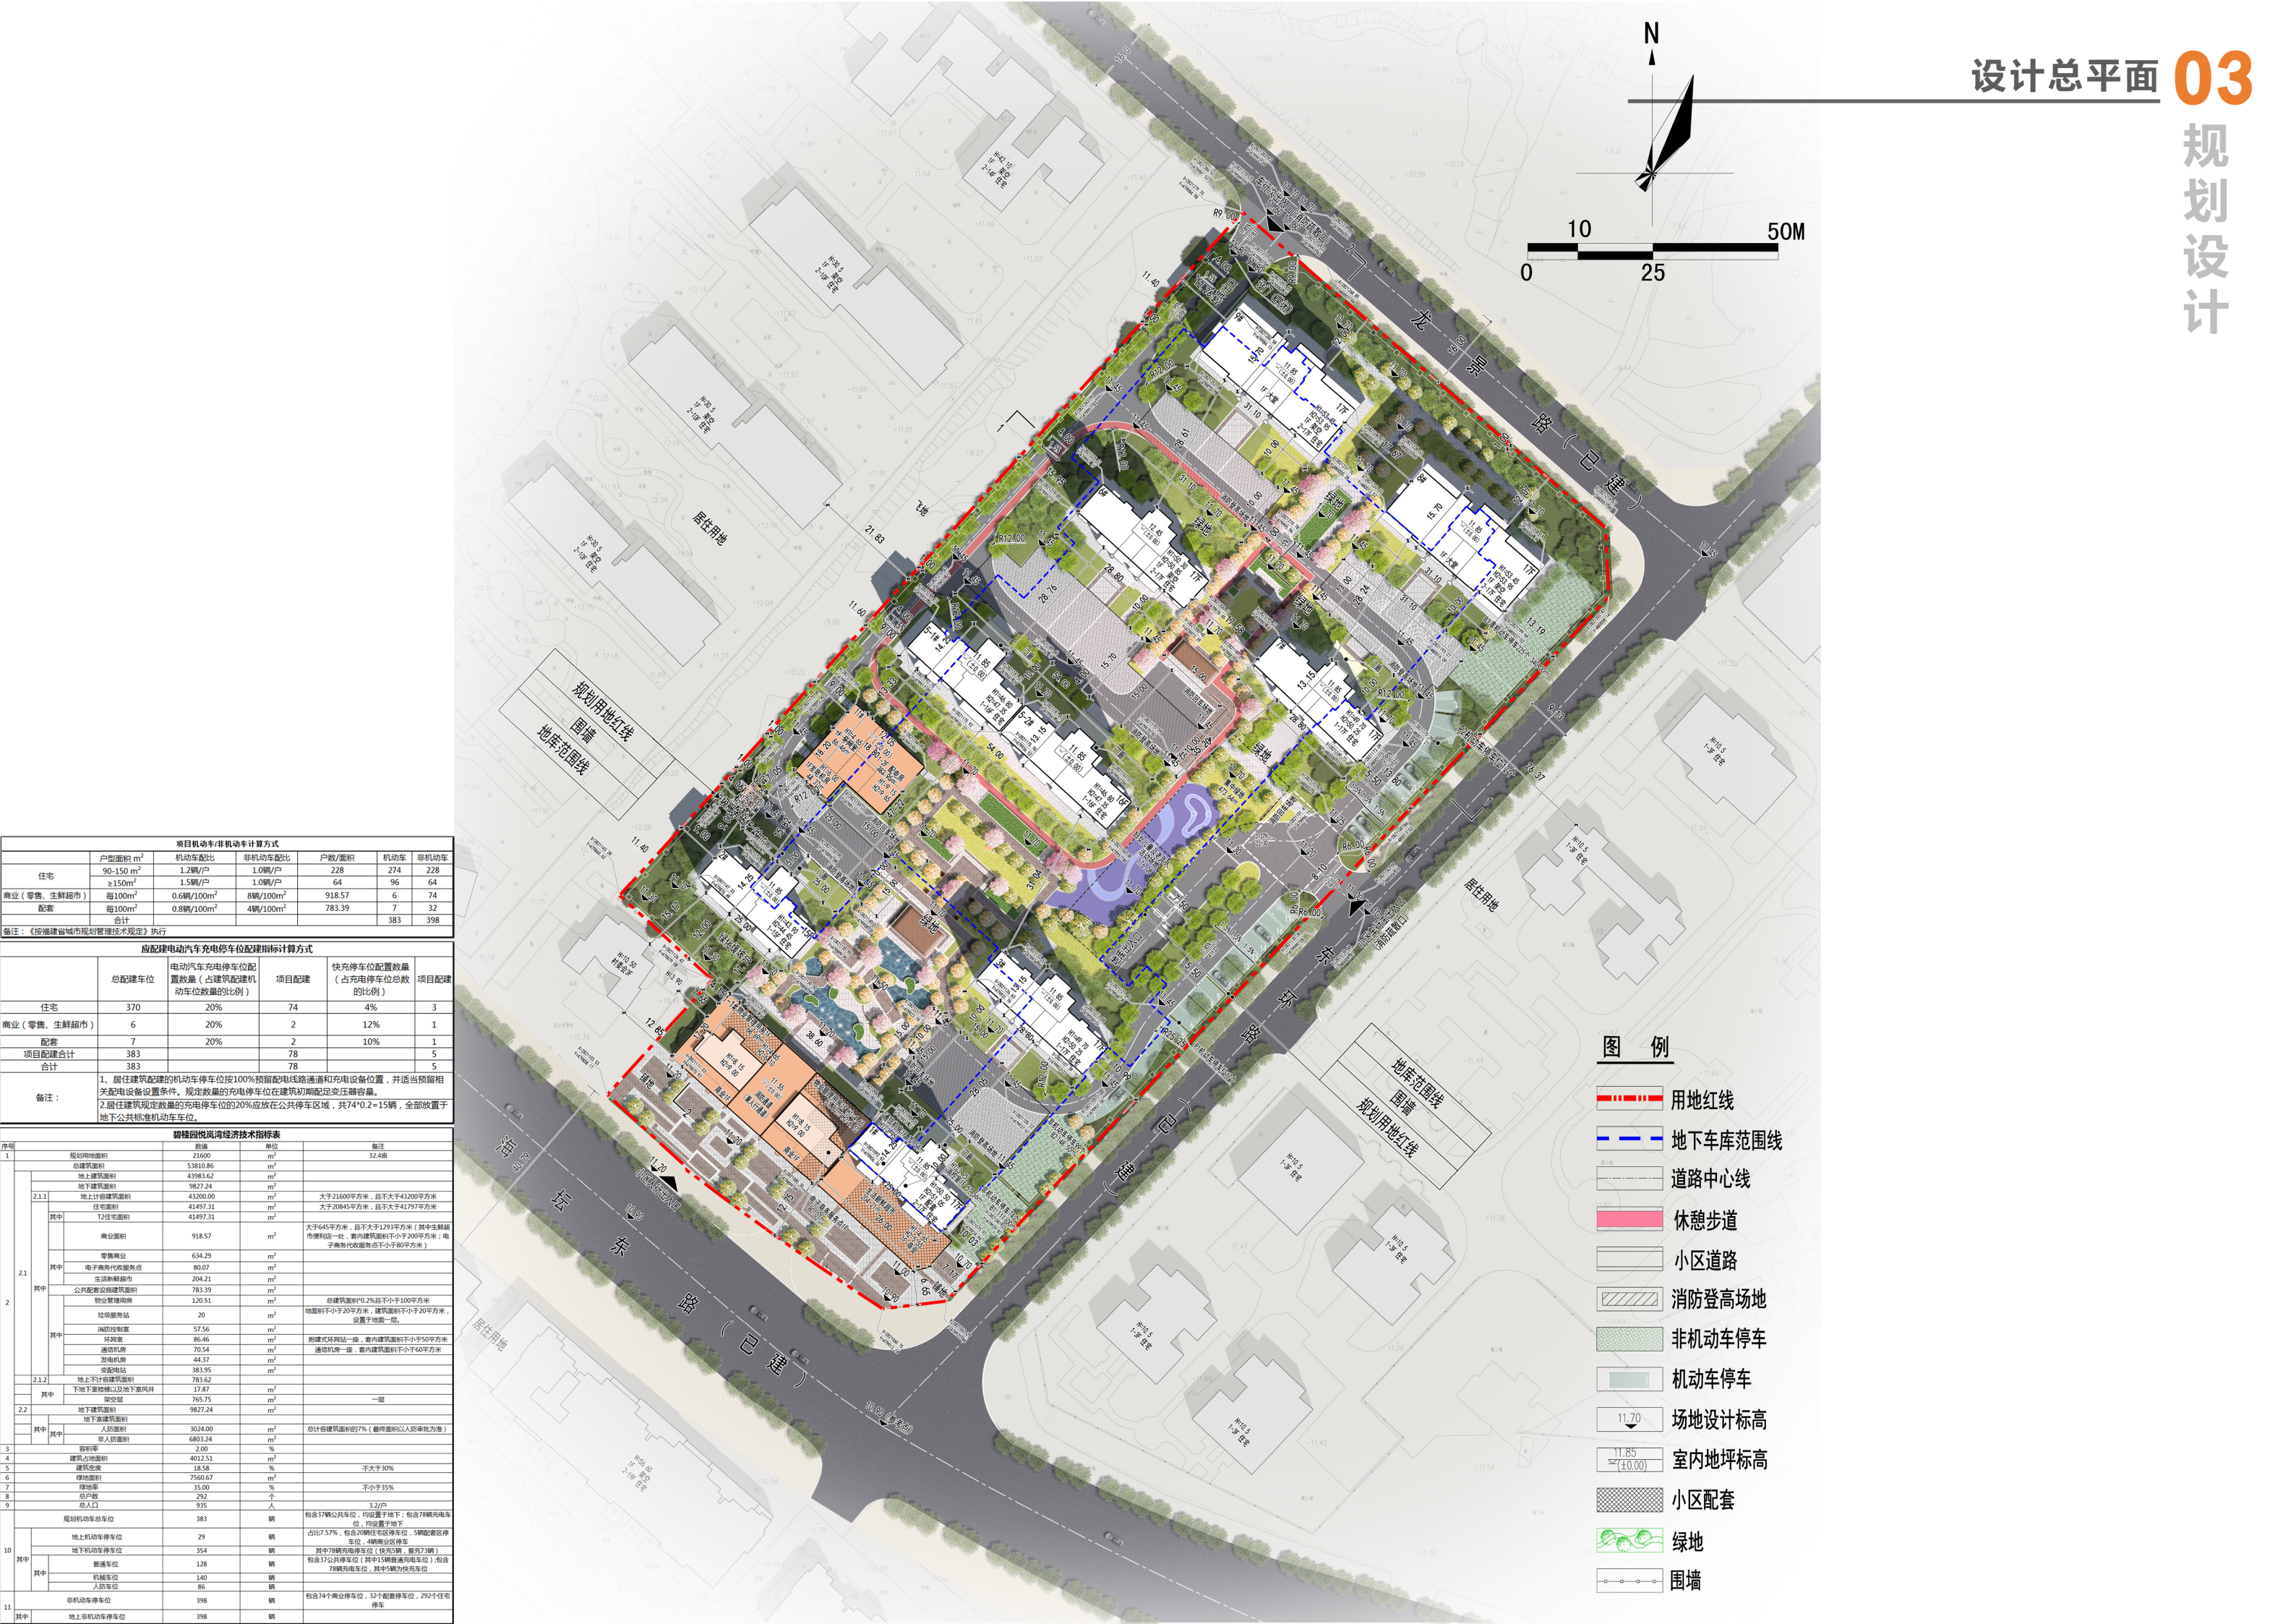

项目机动车/非机动车计算方式					
	户型面积 m ²	机动车配比	非机动车配比	户数/面积	机动车 非机动车
住宅	90-150 m ²	1.2辆/户	1.0辆/户	228	274 228
	≥150m ²	1.5辆/户	1.0辆/户	64	96 64
商业（零售、生鲜超市）	每100m ²	0.6辆/100m ²	8辆/100m ²	918.57	6 74
	配套	每100m ²	0.8辆/100m ²	783.39	7 32
合计					383 398

应配建电动汽车充电停车位配建指标计算方式					
	总配建车位	电动汽车充电停车位配置数量（占建筑配建机动车位数量的比例）	项目配建	快充停车位配置数量（占充电停车位总数的比例）	项目配建
住宅	370	20%	74	4%	3
商业（零售、生鲜超市）	6	20%	2	12%	1
配套	7	20%	2	10%	1
项目配建合计	383		78		5
合计	383		78		5
备注：	1. 居住建筑配建的机动车停车位按100%预留配电路线通道和充电设备位置，并适当预留相关配电设备设置条件。规定数量的充电停车位在建筑初期配足变压器容量。 2. 居住建筑规定数量的充电停车位20%应放在公共停车区域，共74*0.2=15辆，全部放置于地下公共标准机动车车位。				

碧桂园悦风湾经济技术指标表			
序号	指标名称	数值	单位
1	规划用地面积	21600	m ²
	总建筑面积	53810.86	m ²
2.1.1	地上建筑面积	43983.62	m ²
	地下建筑面积	9827.24	m ²
2.1.1.1	地上计容建筑面积	43200.00	m ²
	住宅面积	41497.31	m ²
2.1.1.1.1	住宅面积	41497.31	m ²
	商业面积	918.57	m ²
2.1.1.1.2	零售商业	634.29	m ²
	电子商务代服务点	80.07	m ²
2.1.1.1.3	生活生鲜超市	204.21	m ²
	公共配套设施建筑面积	783.39	m ²
2.1.1.1.4	物业管理用房	120.51	m ²
	垃圾服务站	20	m ²
2.1.1.1.5	消防控制室	57.56	m ²
	设备用房	86.46	m ²
2.1.1.1.6	通信机房	70.54	m ²
	发电机房	44.37	m ²
2.1.1.1.7	变电站	383.95	m ²
	地上不计容建筑面积	783.62	m ²
2.1.1.1.8	地下不计容建筑面积	17.87	m ²
	地下室楼梯以及地下室风井	765.75	m ²
2.2	地下建筑面积	9827.24	m ²
	地下建筑面积	3024.00	m ²
2.2.1	人防面积	6803.24	m ²
	非人防面积	2.00	%
3	建筑占地面积	4012.51	m ²
	建筑密度	18.58	%
4	绿地面积	7560.67	m ²
	绿地率	35.00	%
5	总户数	292	个
	总人口	935	人
6	规划机动车总车位	383	辆
	地上机动车停车位	29	辆
7	地下机动车停车位	354	辆
	普通车位	128	辆
8	机动车位	140	辆
	非机动车位	86	辆
9	非机动车停车位	398	辆
	地上非机动车停车位	398	辆

图例

- 用地红线
- 地下车库范围线
- 道路中心线
- 休憩步道
- 小区道路
- 消防登高场地
- 非机动车停车
- 机动车停车
- 场地设计标高
- 室内地坪标高
- 小区配套
- 绿地
- 围墙