



中科经纬
ZHONGKE JINGWEI

中华人民共和国建设工程设计证书

行业乙级 A251034247

地址: 中国·成都·高新区东虹湾中心2栋7楼

电话: 028-67775960

传真: 028-67775920

网址: www.zkjwgcjs.cn

E-mail: 3211911868@qq.com

邮编: 610041

注册执业章

REGISTERED PRACTICE SIGNET

姓名
NAME

注册印章号
REGISTERED SIGNET NO.

注册证书号
REGISTERED CERTIFICATE NO.

设计总负责人
PROJECT LEADER

专业负责人
DIVISION CHIEF

设计
DESIGNED BY

校对
PROCESSED BY

审核
CHECKED BY

审定
APPROVED BY

设计单位 DESIGNER

中科经纬工程技术有限公司

建设单位 CLIENT

工程名称 PROJECT

吴子春 个人住宅

子项名称 SUB PROJECT

图名 TITLE

①~④轴立面图

设计号
PROJECT NO. MF-2020-宝城144

图别
DWG TYPE 方案


图号
DWG TYPE 07

版本号
Ver. A

日期
DATE 2021.01

所有设计图以最新版本为有效版本

本图若未盖本单位出图章则无效

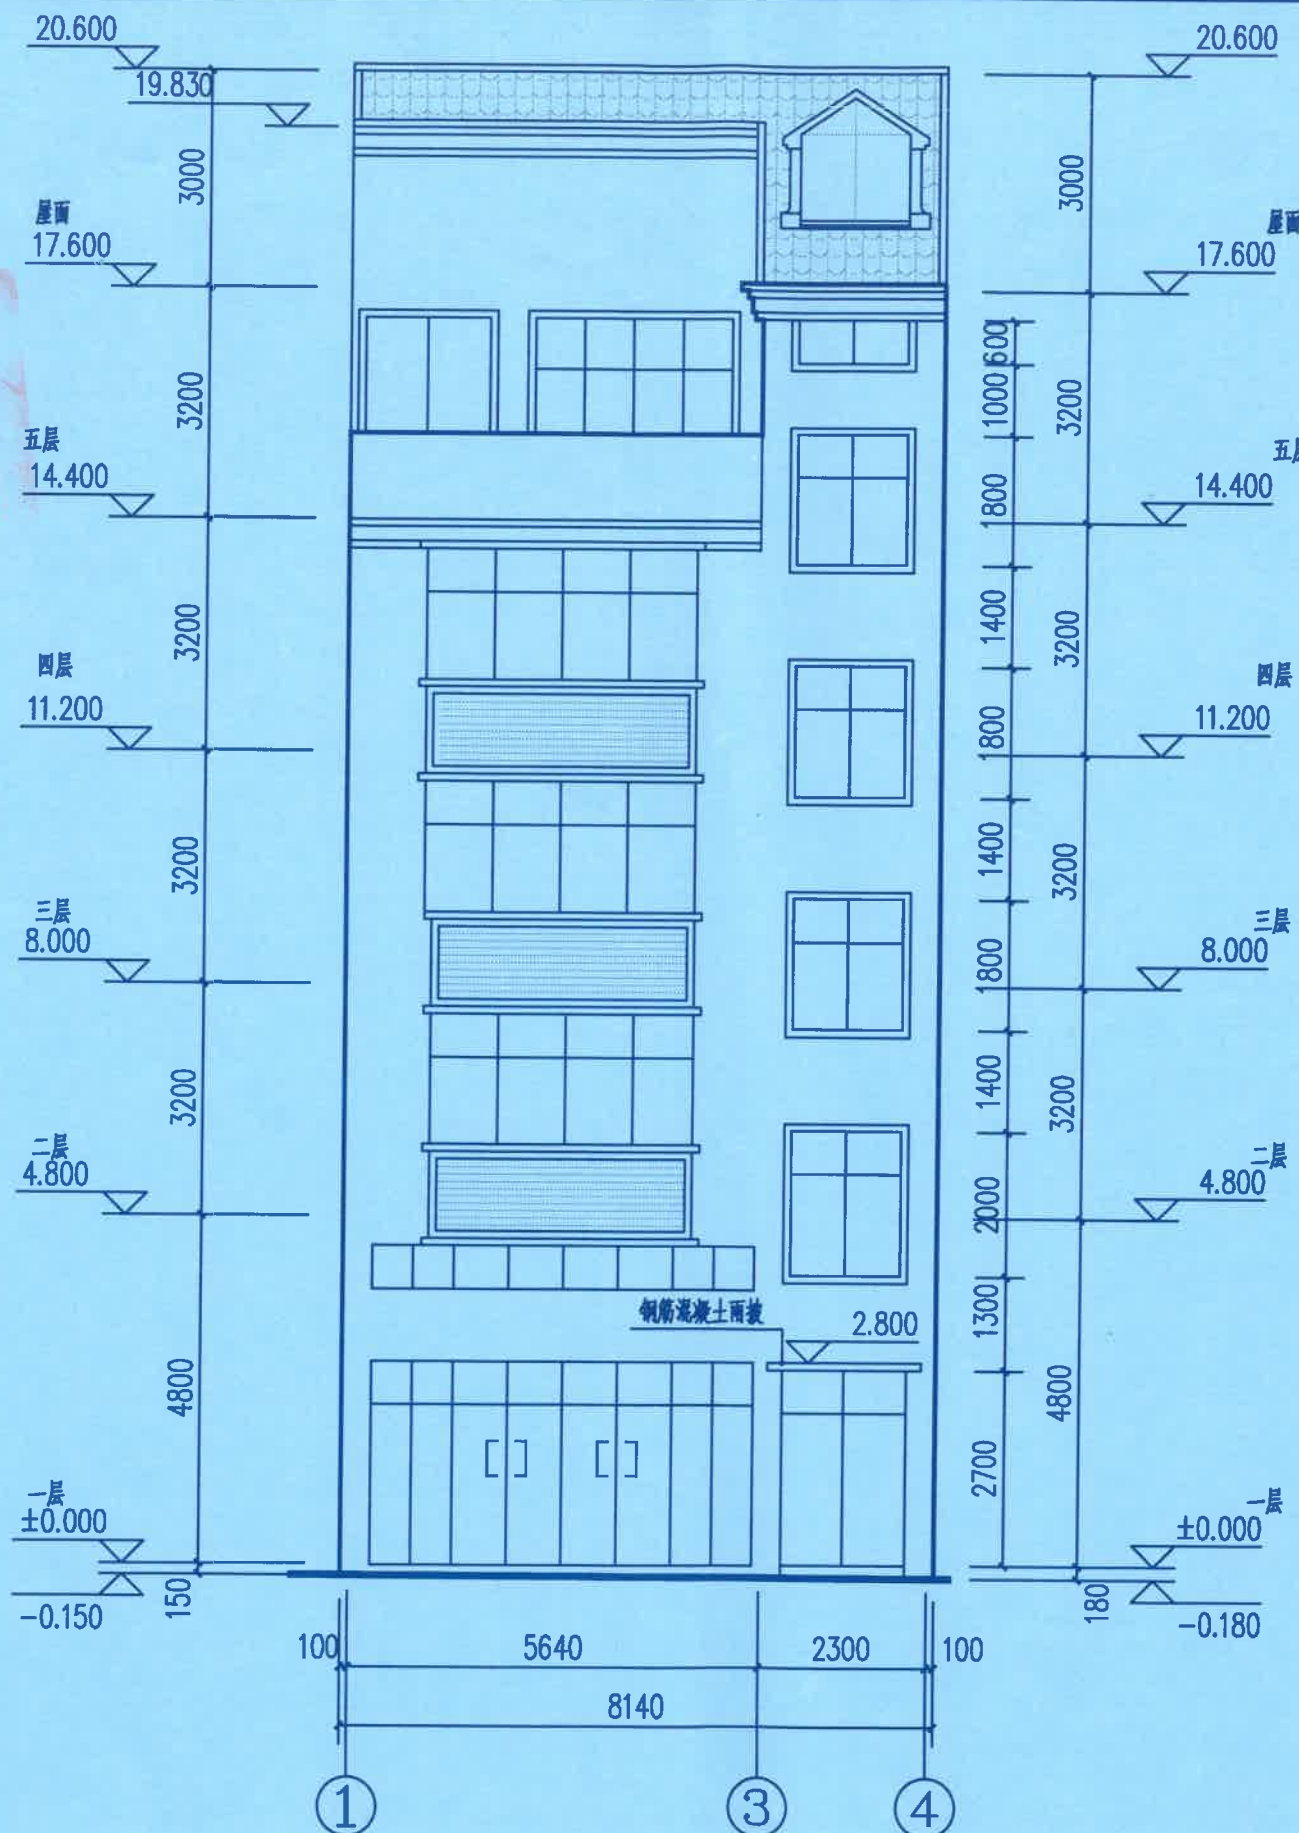


①~④轴立面图 1:100

中华人民共和国一级注册建筑师
姓名: 曾雯
注册号: 5103424-002
有效期: 至2022年12月

四川省建设工程设计出图专用章
中科经纬工程技术有限公司
资质等级范围: 市政行业乙级;
建筑行业乙级。

资质证书编号: A251034247 有效期至: 2024年03月13日

平潭综合实验区自然资源与生态环境局
图纸专用章(1)
随学建城16.m264p 号有效

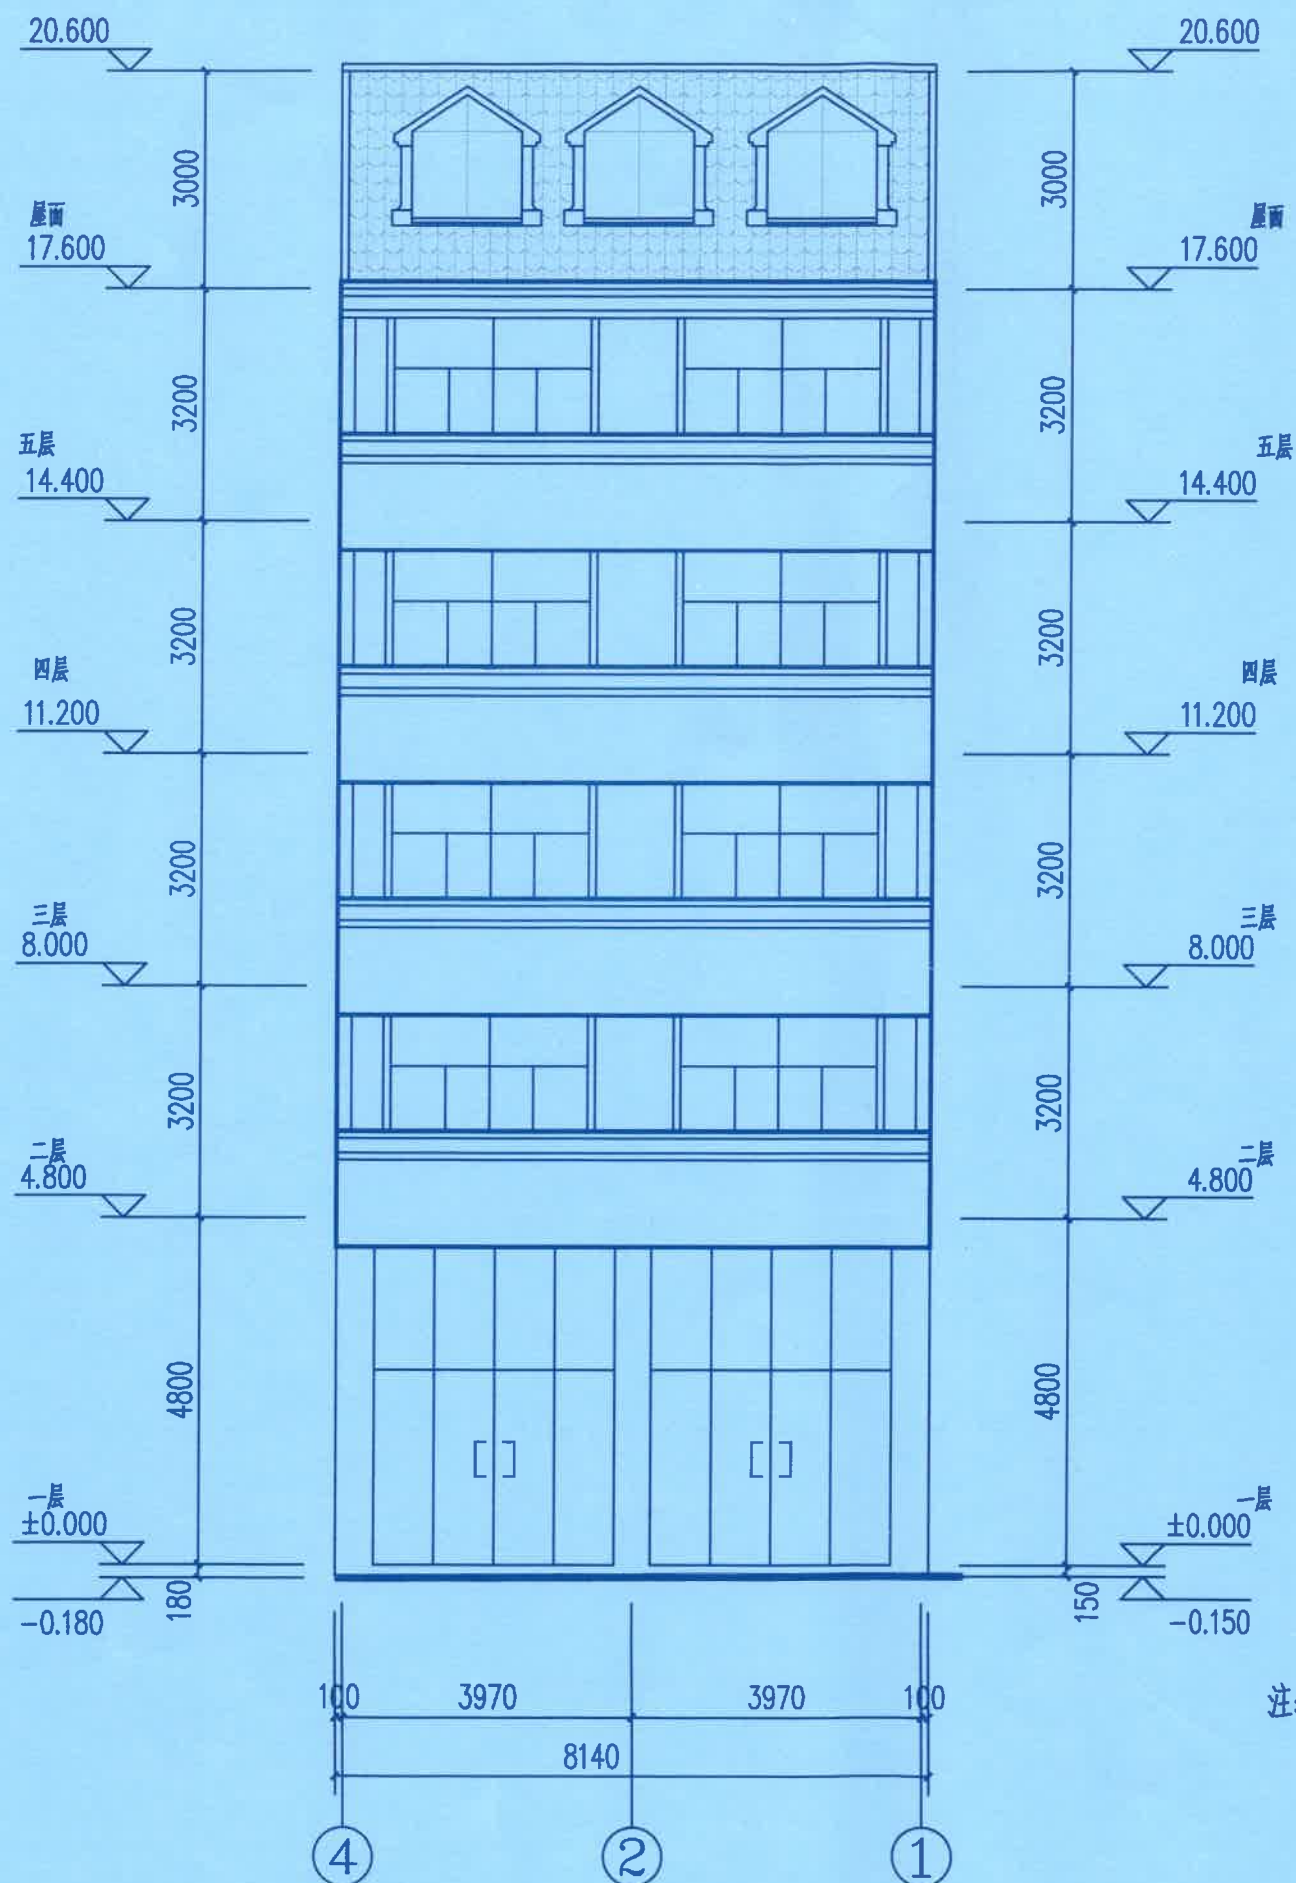

④~①轴立面图 1:100

(沿街面)

注: 1. 室外地坪线依据现场物理测量获得, 但不能排除测量时可能出现的误差。因此尺寸应以现场实际尺寸为准, 本次不另行出图, 但是室内外高差最低值不应大于150mm。



中科经纬
ZHONGKE JINGWEI

中华人民共和国建设工程设计证书

行业乙级 A251034247

地址: 中国·成都·高新区东虹湾中心2栋7楼

电话: 028-67775960

传真: 028-67775920 网址: www.zkjwgcjs.com

E-mail: 3211911868@qq.com 邮编: 610041

注册执业章

REGISTERED PRACTICE SIGNET

姓名

NAME

注册印章号
REGISTERED SIGNET NO.注册证书号
REGISTERED CERTIFICATE NO.设计总负责人
PROJECT LEADER专业负责人
DIVISION CHIEF设计
DESIGNED BY校对
CHECKED BY审核
APPROVED BY设计单位
DESIGNER

姓名: 曹

注册号: 5105421082

有效期: 至2022年12月

设计单位: 中科经纬工程技术有限公司

建设单位: CLIENT

工程名称: PROJECT

吴子春 个人住宅

子项名称: SUB PROJECT

四川省建设工程设计出图专用章

中科经纬工程技术有限公司

图名: TITLE

④~①轴立面图

设计号: 2021034247

PROJECT NO.

图别: 方案

图号: 08

版本号: A

日期: 2021.01

所有设计图以最新版本为有效版本

本图若未盖本单位出图章则无效