经济技术指标表

序号				项目	数值	单位	备注
1				用地面积	45755.00	m²	68.6亩
2				总建筑面积	132013.06	m²	
2.1				地上建筑面积	106967.55	m²	
	2.1.1			地上计容建筑面积	105236.00	m²	大于45755平方米，且不大于105236平方米
	其中			住宅建筑面积	97678.94	m²	居住大于41639㎡，且不大于98147㎡
		其中		高层住宅面积	97678.94	m²	
				商业建筑面积	4242.60	m²	商业计容建筑面积不小于2192㎡，且不得超过5165㎡
		其中		沿街商铺	4242.60	m²	
				公共配套设施建筑面积	1435.10	m²	
			其中	物业管理用房	264.13	m²	建筑面积*0.2%,不少于100㎡
				小区门卫	8.00	m²	
				电子商务代收服务点	80.04	m²	建筑面积≥80㎡
				附建式环网站	123.94	m²	套内建筑面积≥45㎡
			其中	变配电房	599.81	m²	
				发电机房	99.81	m²	
				公共电房	129.52	m²	
				通信机房	49.20	m²	
				电视机房	21.85	m²	
				消防控制室	58.80	m²	
				幼儿园	1879.36	m²	6班，用地面积≥2880㎡，建筑面积≥1879㎡
		其中		门卫	12.76	m²	
	2.1.2			地上不计容建筑面积	1731.55	m²	
				地上架空层	1575.82	m²	
				人行通道、下地下室楼梯及地下室风井等	140.73	m²	
				垃圾分类用房	15.00	m²	
2.2				地下建筑面积	25045.51	m²	
	其中			地下室建筑面积	25045.51	m²	
		其中		普通地下室	17605.29	m²	
				人防地下室	7440.22	m²	计容总建筑面积的7%，应建人防面积7366.6㎡
3				容积率	2.30		
4				建筑占地面积	10020.02	m²	
5				建筑密度	21.90%		不大于22%
6				绿地面积	16033.33	m²	
7				绿地率	35.04%		
8				总户数	808.00	户	
9				总人口	2828.00	人	3.5人/户
10				机动车停车位	1012	辆	住宅：1.2泊/户(90~150㎡)；配套：0.8泊/100㎡；商业：0.6泊/100㎡；幼儿园：1.5/100名学生
	其中			地上机动车停车位	88	辆	
				地下机动车停车位	924	辆	含97个公共标准机动车车位
		其中		普通车位	683	辆	
				人防车位	241	辆	
11				非机动车停车位	1215	辆	住宅：1泊/户(90~150)；配套：4泊/100㎡；商业：8泊/100㎡；幼儿园：5/100名学生
	其中			地上非机动车停车位	765	辆	
				地下非机动车停车位	450	辆	

6班幼儿园经济技术指标

项目名称	数值	单位	备注
地块用地面积	2880.00	m²	6班，用地面积≥2880㎡
总建筑面积	1879.36	m²	
计容建筑面积	1879.36	m²	建筑面积≥1879㎡
容积率	/	m²	
分班活动场地	360.00	m²	
公共活动场地	360.00	m²	
建筑占地面积	664.73	m²	
建筑密度	23.08%		
绿地率	30.00%		
机动车停车位	3	辆	
非机动车停车位	9	辆	

平潭综合实验区2019G043号宗地机动车/非机动车计算方式

	户型面积	机动车配比	非机动车配比	户数/面积/人数	机动车车位数	非机动车车位数
住宅	45㎡-90㎡	0.8辆/户	2辆/户	\	\	\
	90㎡-150㎡	1.2辆/户	1辆/户	808户	970	808
	150㎡以上	1.5辆/户	1辆/户	\	\	\
商业（零售）	每100㎡	0.6辆/100㎡	8辆	4242.60㎡	26	340
配套	每100㎡	0.8辆/100㎡	4辆/100㎡	1435.10㎡	12	58
幼儿园	每100学生	1.5辆/100人	5辆/100人	180人	3	9
	合计				1011	1215
备注	1、住宅的公共标准机动车车位配置于地下，数量不低于住宅最低应配建标准机动车车位数量的10%，970*10%=97辆公共标准机动车车位设置于地下。					

电动汽车充电停车位配建指标

类型	类型车位数	配建标准 电动汽车充电停车位配置数量（占建筑配建机动车停车位数量的比例）	项目配建	配建标准 快充停车位配置数量（占充电停车位总数的比例）	项目配建
住宅	970	20%	194	4%	8
商业	26	20%	6	12%	1
配套	12	20%	3	12%	1
幼儿园	3	12%	1	4%	1
项目配建合计	1011		204		11
实际配建	1012		204		11
备注	1、居住建筑配建的机动车停车位按100%预留配电线路通道和充电设备位置，并适当预留相关配电设备设置条件。规定数量的充电停车位在建筑初期配足变压器容量。 2、规定数量的充电停车位的20%应放在公共停车区域，204*0.2=41辆公共标准机动车，其中：11辆放于地上快充停车位，30辆放于地下充电桩车位。				

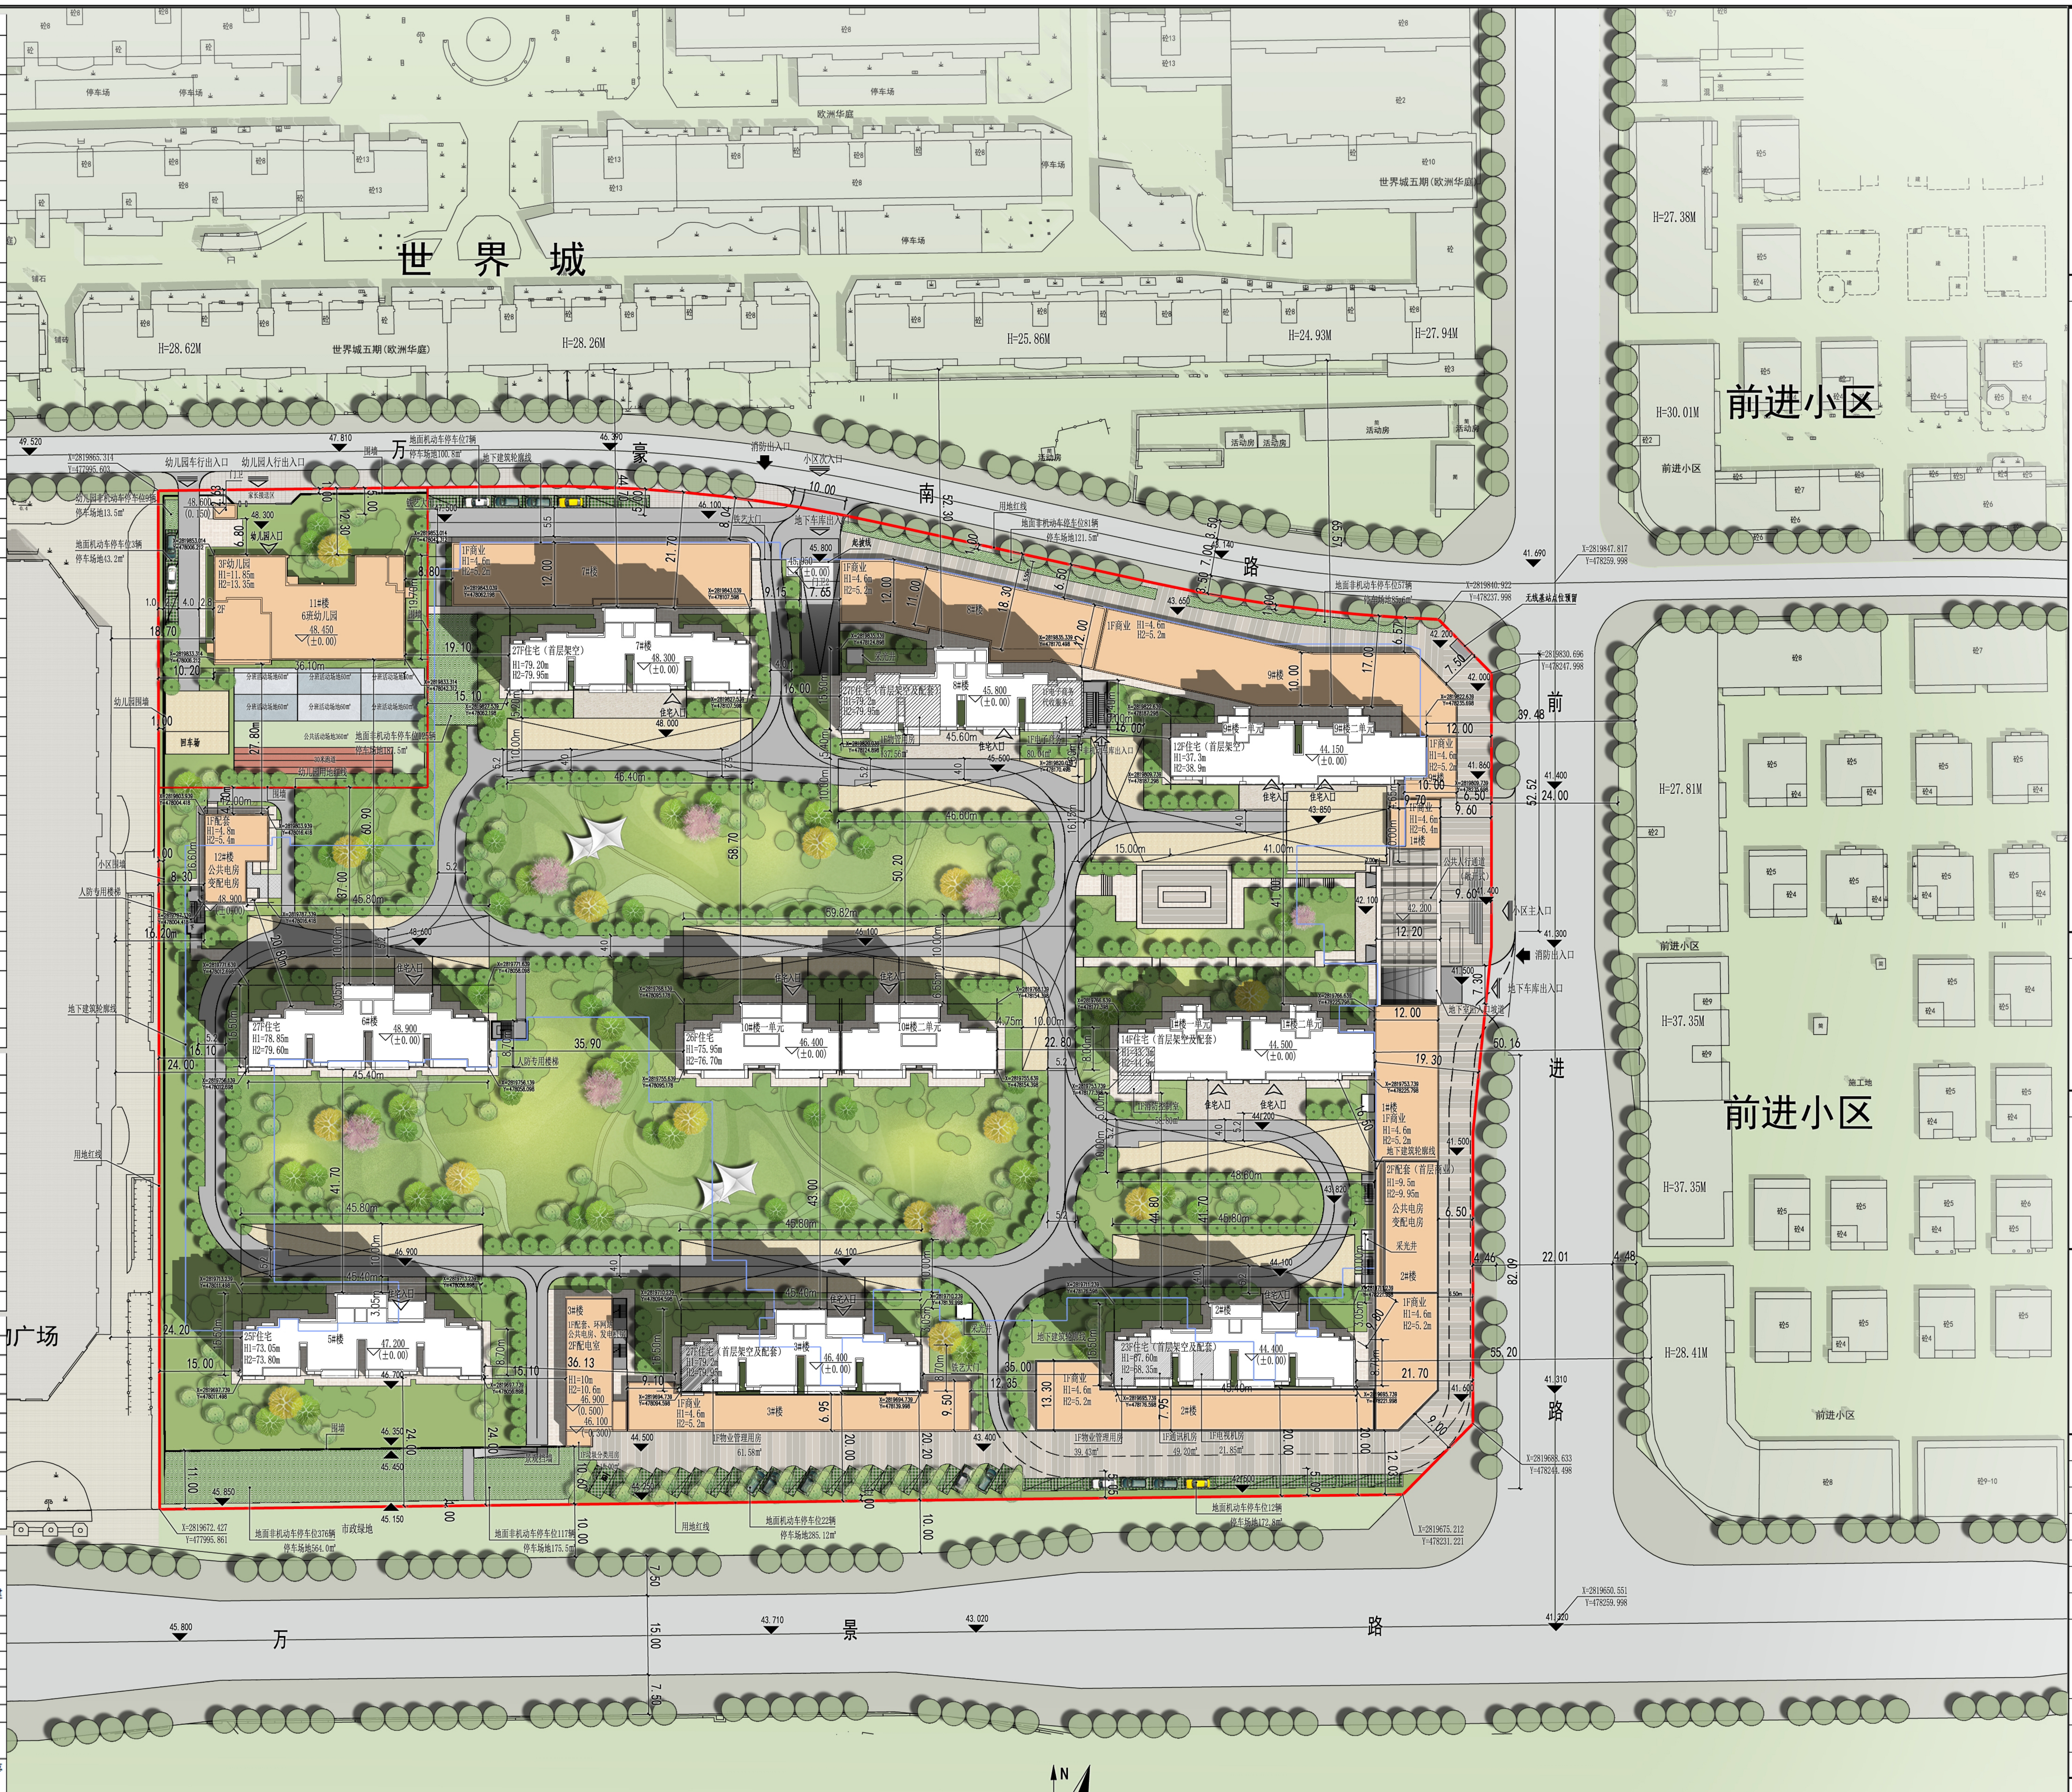

世界城
世界城五期（欧洲华庭）
欧洲华庭
H=28.62M
H=28.26M
H=25.86M
H=24.93M
H=27.94M
前进小区
H=27.38M
H=30.01M
H=27.81M
H=37.35M
H=37.35M
H=28.41M
施工地
万豪南路
前进路
万景路
广场
幼儿园车行出入口
幼儿园人行出入口
消防出入口
小区次入口
地下车库出入口
小区主入口
地下车库出入口
地下室出入口坡道
公共人行通道（敞开式）
无线基站点位预留
3F幼儿园 H1=11.85m H2=13.35m
11#楼 6班幼儿园 48.450 (±0.00)
12#楼 公共电房 变配电房
1F商业 H1=4.6m H2=5.2m 7#楼
27F住宅（首层架空） H1=79.20m H2=79.95m 7#楼 48.300 (±0.00)
27F住宅（首层架空及配套） H1=79.2m H2=79.95m 8#楼 45.800 (±0.00)
1F电子商务代收服务点
1F物业管理用房 137.56㎡
12F住宅（首层架空） H1=37.3m H2=38.9m 9#楼 44.150 (±0.00)
27F住宅 H1=78.85m H2=79.60m 6#楼 48.900 (±0.00)
26F住宅 H1=75.95m H2=76.70m 10#楼 46.400 (±0.00)
14F住宅（首层架空及配套） H1=43.3m H2=44.9m 1#楼 44.500 (±0.00)
1F消防控制室 58.80㎡
25F住宅 H1=73.05m H2=73.80m 5#楼 47.200 (±0.00)
3#楼 1F配套、环网站 公共电房、发电机房 2F配电室 H1=10m H2=10.6m
27F住宅（首层架空及配套） H1=79.2m H2=79.95m 3#楼 46.400 (±0.00)
23F住宅（首层架空及配套） H1=67.60m H2=68.35m 2#楼 44.400 (±0.00)
2F配套（首层商业） H1=9.5m H2=9.95m 公共电房 变配电房
1F物业管理用房 61.58㎡
1F物业管理用房 39.43㎡
1F通讯机房 49.20㎡
1F电视机房 21.85㎡
地面非机动车停车位376辆 停车场地564.0㎡
地面非机动车停车位117辆 停车场地175.5㎡
地面机动车停车位22辆 停车场地285.12㎡
地面机动车停车位12辆 停车场地172.8㎡
地面非机动车停车位81辆 停车场地121.5㎡
地面非机动车停车位57辆 停车场地85.6㎡
地面机动车停车位7辆 停车场地100.8㎡
地面非机动车停车位125辆 停车场地187.5㎡
用地红线
地下建筑轮廓线
人防专用楼梯
市政绿地

总平面图 1:500

N
0 5 10 15 20 25M

图例	名称	图例	名称
— · —	用地红线	45.000 ▼	场地设计标高
——	地下建筑轮廓线	45.30(±0.00)	室内设计标高
	道路（详景观二次设计）	• 45.35	道路标高
	消防登高场地		小区绿地
	小区地面非机动车停车位	——	小区围墙
	小区地面无障碍机动车停车位		化粪池
	小区地面机动车停车位		隔油池
	生态停车场		
	快充充电车位		

说明：

1. 本工程规划设计主要依据为平潭综合实验区城市规划管理技术暂行规定(2011年版)和福建省城市规划管理技术规定（2017版）。
2. 本工程物业管理用房按《福建省物业管理条例》配置。
3. H1=室外地坪到建筑顶层屋面结构高度；H2=室外地坪到建筑顶层女儿墙高度。
4. 本工程按100%预留配电线路通道和充电设备位置。
5. 本工程按照福建省一星级绿色建筑标准设计要求进行建筑设计。
6. 本工程采用2000国家大地坐标系，绝对标高值为1985国家高程基准，图中标注的尺寸、坐标、标高和坡长以米为单位，坡度以百分数计。
7. 根据《福建省人民防空条例2016-9-30修改》，人防面积计算公式为：总计容面积x7%，即105236m²x7%=7366.52m²。本工程实际设计人防面积为7497.91m²，满足人防面积要求。（具体以人防部门意见为准）

ZHOYU
洲宇集团

洲宇设计集团股份有限公司
Zhoyu Design Group Co.,Ltd.
证书编号：甲级 A151001605 联系电话：028-85357531
地 址：成都天府新区华府大道1号
蓝润置地广场T1/27-30楼

附注：

工程设计出图专用章：

注册章：

单体位置示意图：

设计号：			
工程名称：	奥园·玺悦府		
子项名称：			
建设单位：	平潭宏新置业有限公司		
图 名：			
图 别		图 号	
比 例		图 幅	
日 期	2020.10	版 本	A
制 图	江定基	江定基	
设 计	江定基	江定基	
校 对	陈德顺	陈德顺	
专业负责人	陈德顺	陈德顺	
审 核	陈浩帆	陈浩帆	
审 定	马学聪	马学聪	
设 总	马学聪	马学聪	

图纸使用说明

1、如图框中版次栏所示"A"，意为本图第一次出图版，如示"B"意为第二次修改版，以此类推。
2、修改图所对应的原设计图纸作废。
3、未经加盖公司出图章，本图无效。