


专业	日期	姓名	专业	日期	姓名
建筑			建筑		
结构			结构		
电气			电气		

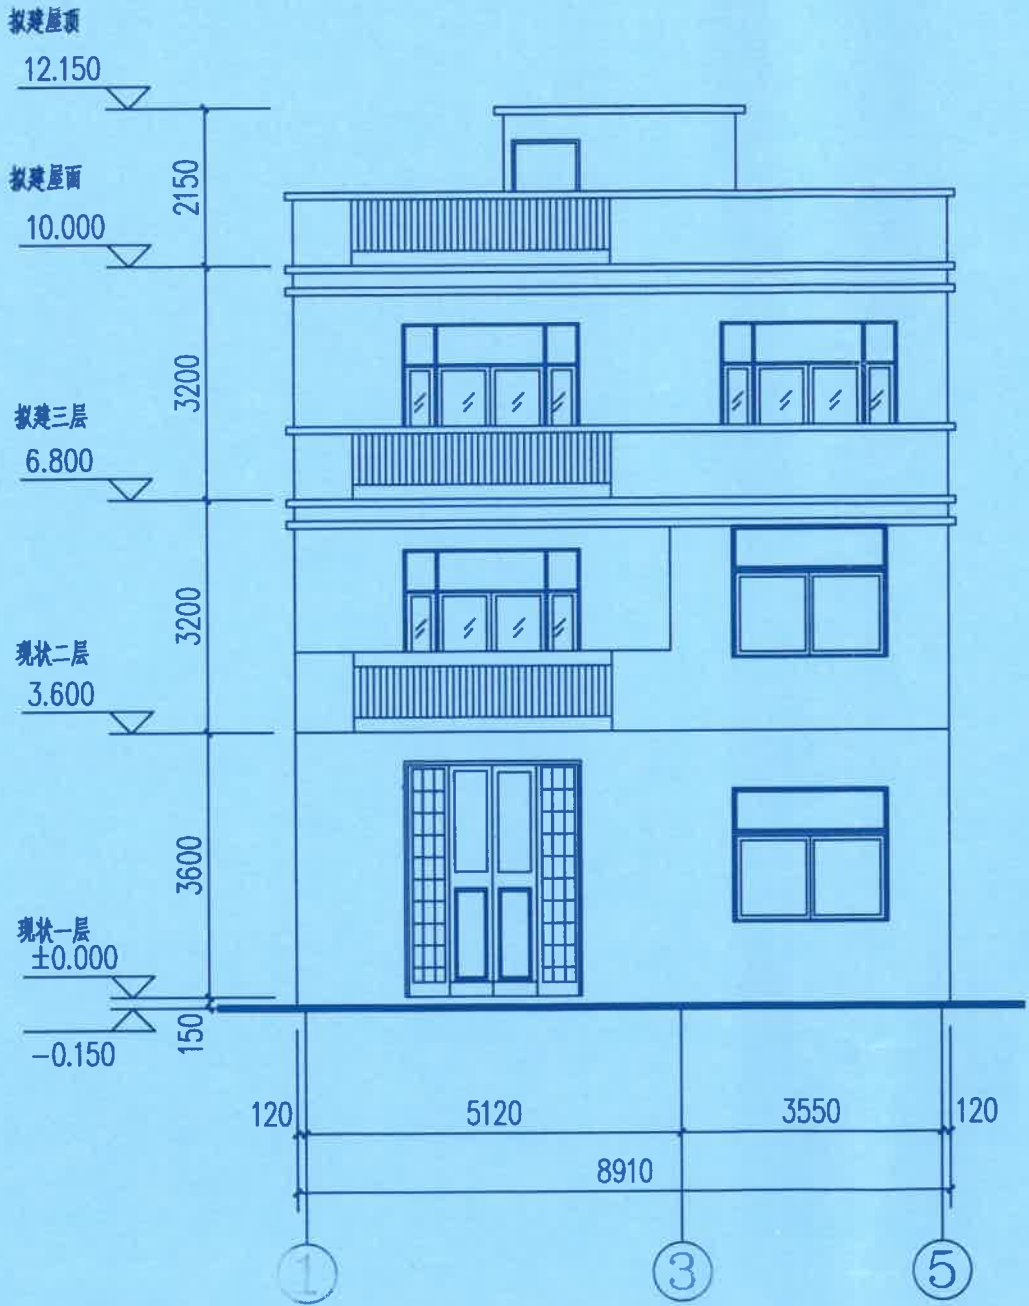

① - ⑤ 轴立面图 1:100

平潭综合实验区自然资源局与生态环境局
图纸专用章 (1)
陈建城 10.000 4999 号有效
2021.10.12



平潭综合实验区规划设计研究院
(平潭县建筑勘察设计院)

Pingtan Comprehensive Experimentation Zone
Planning Programming Institute
(Pingtan Architectural Design Institute)

注册: A230000610
ARCHITECTURAL DESIGN LICENSE No. A230000610

备注:

图纸专用章

注册建筑师执业章

注册结构师执业章

施工图审查批准单位

施工图审查批准证书号

工程名称

林华 林华娟 个人住宅

建设单位

审定

工程负责人

专业负责人

审核

校对

设计

制图

图名

南立面图

工程编号

MF210824

图例

建筑


图号

07

日期

2021.08

专业	姓名	日期	专业	姓名	日期
建筑			建筑		
结构			结构		
电气			电气		
给排水			给排水		
暖通			暖通		
动力			动力		
其他			其他		

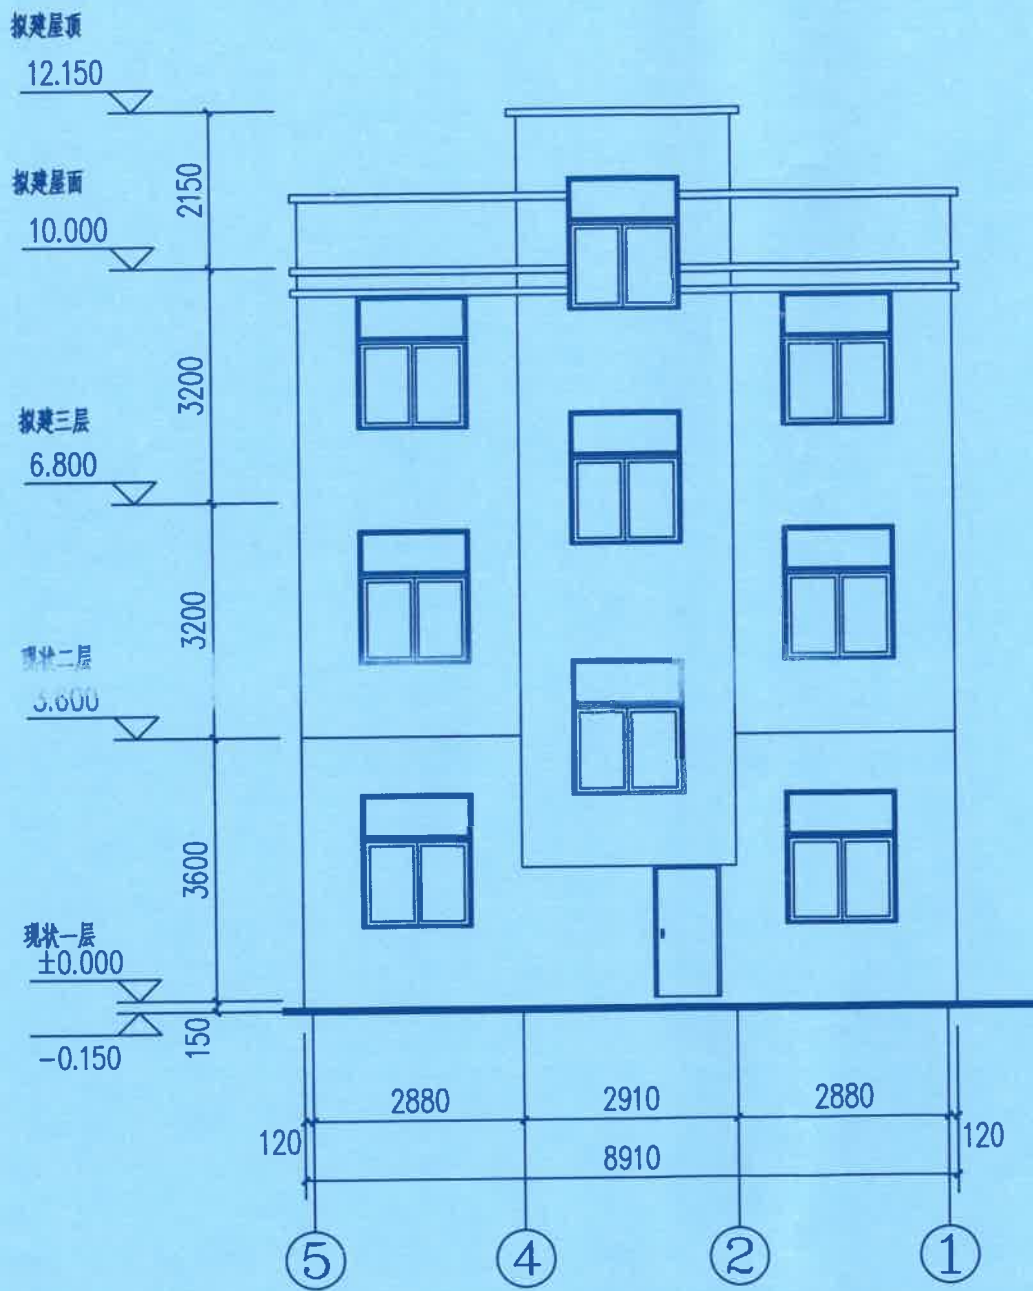

平潭综合实验区自然资源局与生态环境局
图纸专用章(1)
随 建 设 项 目 附 件 号 有 效
2021.10.12



平潭综合实验区规划设计研究院
(平潭县建筑勘察设计院)
Pingtan Comprehensive Experimentation Zone
Planning Programming Institute
(Pingtan Architectural Design Institute)
证书编号: A235005610
ARCHITECTURAL DESIGN LICENSE No. A235005610

备注:

图纸专用章

注册建筑师执业章


姓名: 陈明建

注册号: 1-0001

有效期至: 2021年12月

建设单位	陈明建
审定	陈明建
工程负责人	陈春
专业负责人	林凯
审核	林凯
校对	林凯
设计	林凯
制图	林凯
图名	北立面图
工程编号	MF210824
图别	建筑
图号	08
日期	2021.08

专业	姓名	日期	专业	姓名	日期
建筑			建筑		
结构			结构		
电气			电气		
给排水			给排水		
暖通			暖通		
工艺			工艺		

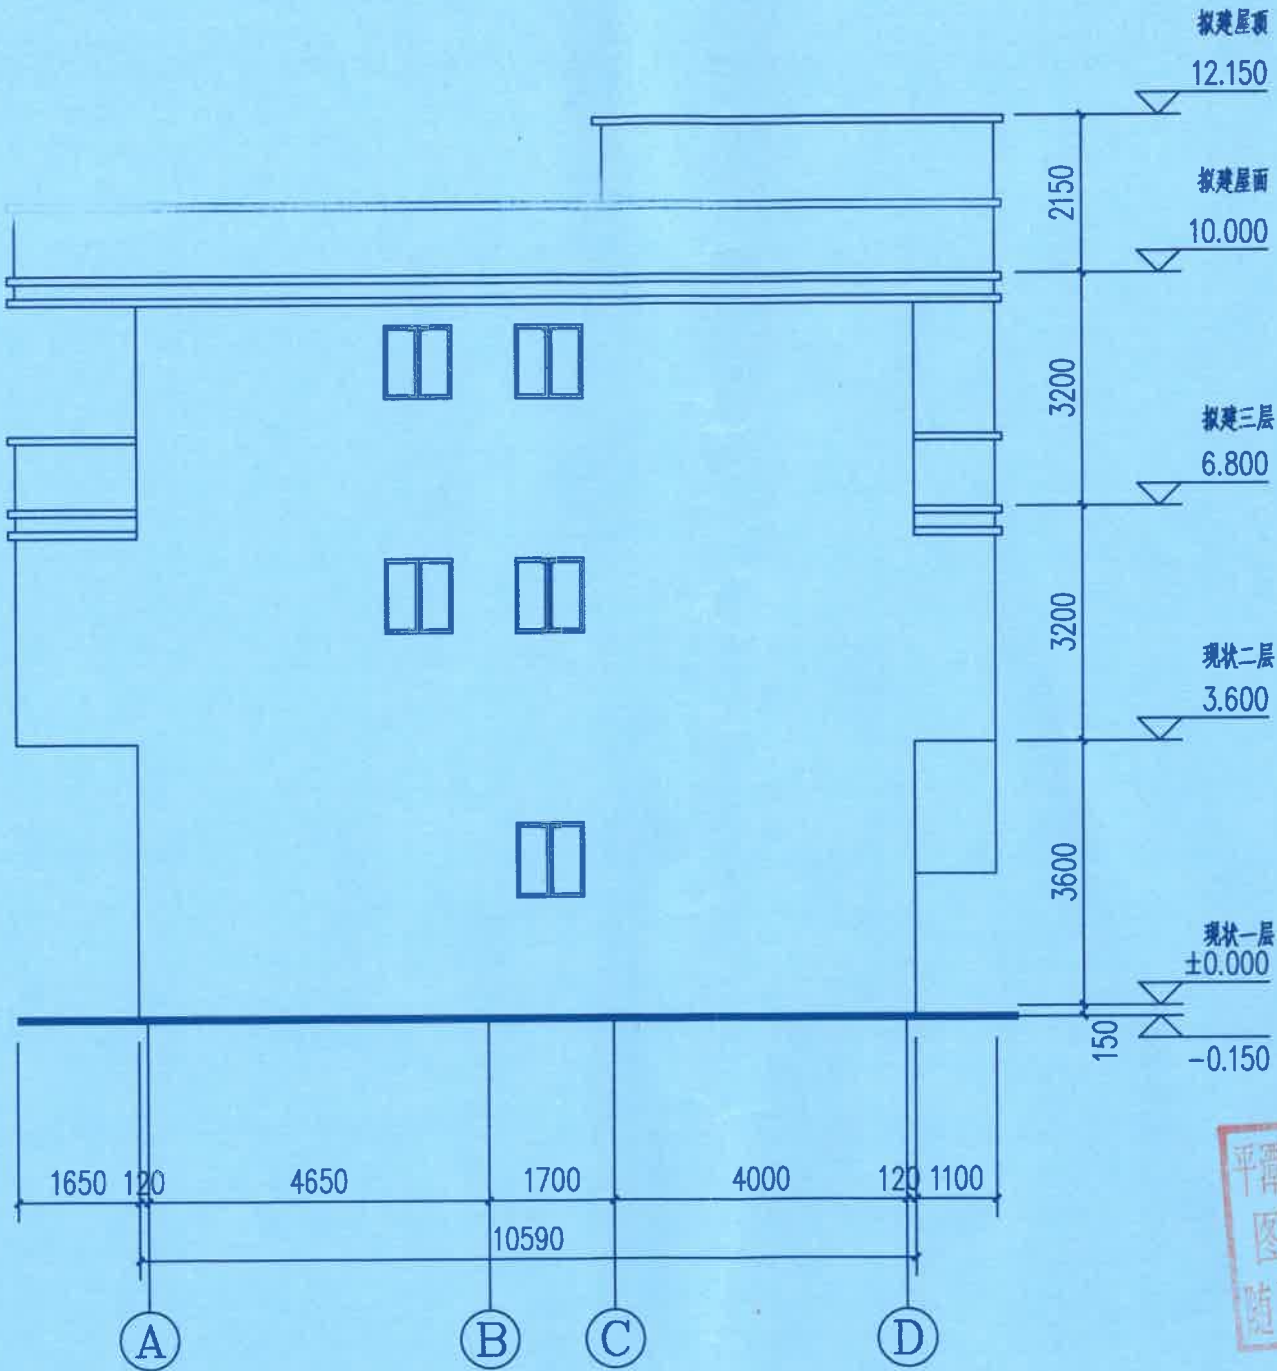

④ - ④ 轴立面图 1:100



平潭综合实验区规划设计研究院
(平潭县建筑勘察设计院)

Pingtan Comprehensive Experimentation Zone
Planning Programming Institute
(Pingtan Architectural Design Institute)

注册建筑师执业章
ARCHITECTURAL DESIGN LICENSE No. A236005610

备注

图纸专用章



注册建筑师执业章



施工图审查批准单位

施工图审查批准书证号

工程名称

林华 林华娟 个人住宅

建设单位

审定

工程负责人

专业负责人

审核

校对

设计

制图

图名

东立面图

工程编号

MF210824

图例

建筑

图号

09

日期

2021.08