

日期	
姓名	
专业	建筑
专业	给排水
专业	暖通
专业	电气



①-④轴立面图 1:100

平潭综合实验区自然资源与生态环境局
图纸专用章(1)
随发改线办(2021)395号有效

平潭综合实验区规划设计研究院
(平潭县建筑勘察设计院)
Pingtan Comprehensive Experimentation Zone
Planning Programming Institute
(Pingtan Architectural Design Institute)
注册证书: A235005610
ARCHITECTURAL DESIGN LICENSE No. A235005610

备注

图章专用章

注册建筑师执业章

注册结构师执业章

施工图审查批准单位

施工图审查批准证书号

工程名称

谢晓东个人住宅

建设单位

审定

工程负责人

专业负责人

审核

校对

设计

制图

图名

①~④轴立面图

工程编号

MF200910

图别

建筑

图号

07

日期

2021.03

专业	日期	姓名	专业	日期	姓名
建筑			建筑		
结构			结构		
电气			电气		
给排水			给排水		
暖通			暖通		
人防			人防		



④-①轴立面图 1:100

平潭综合实验区自然资源局与生态环境局
图纸专用章(1)
随发建成 10.000395 号有效

平潭综合实验区规划设计研究院
(平潭县建筑勘察设计院)
Pingtan Comprehensive Experimentation Zone
Planning Programming Institute
(Pingtan Architectural Design Institute)
注册证书号: A235005610
ARCHITECTURAL DESIGN LICENSE No. A235005610

备注

图纸专用章

注册建筑师执业章

注册结构师执业章

施工图审查批准单位

施工图审查批准证书号

工程名称

谢晓东个人住宅

建设单位

审定

工程负责人

专业负责人

审核

校对

设计

制图

图名

④~①轴立面图

工程编号

MF200910

图别

建筑


图号

08

日期

2021.08

日期		姓名		专业	
				水卫	
				暖通	
				工艺	
日期		姓名		专业	
				建筑	
				结构	
				电气	

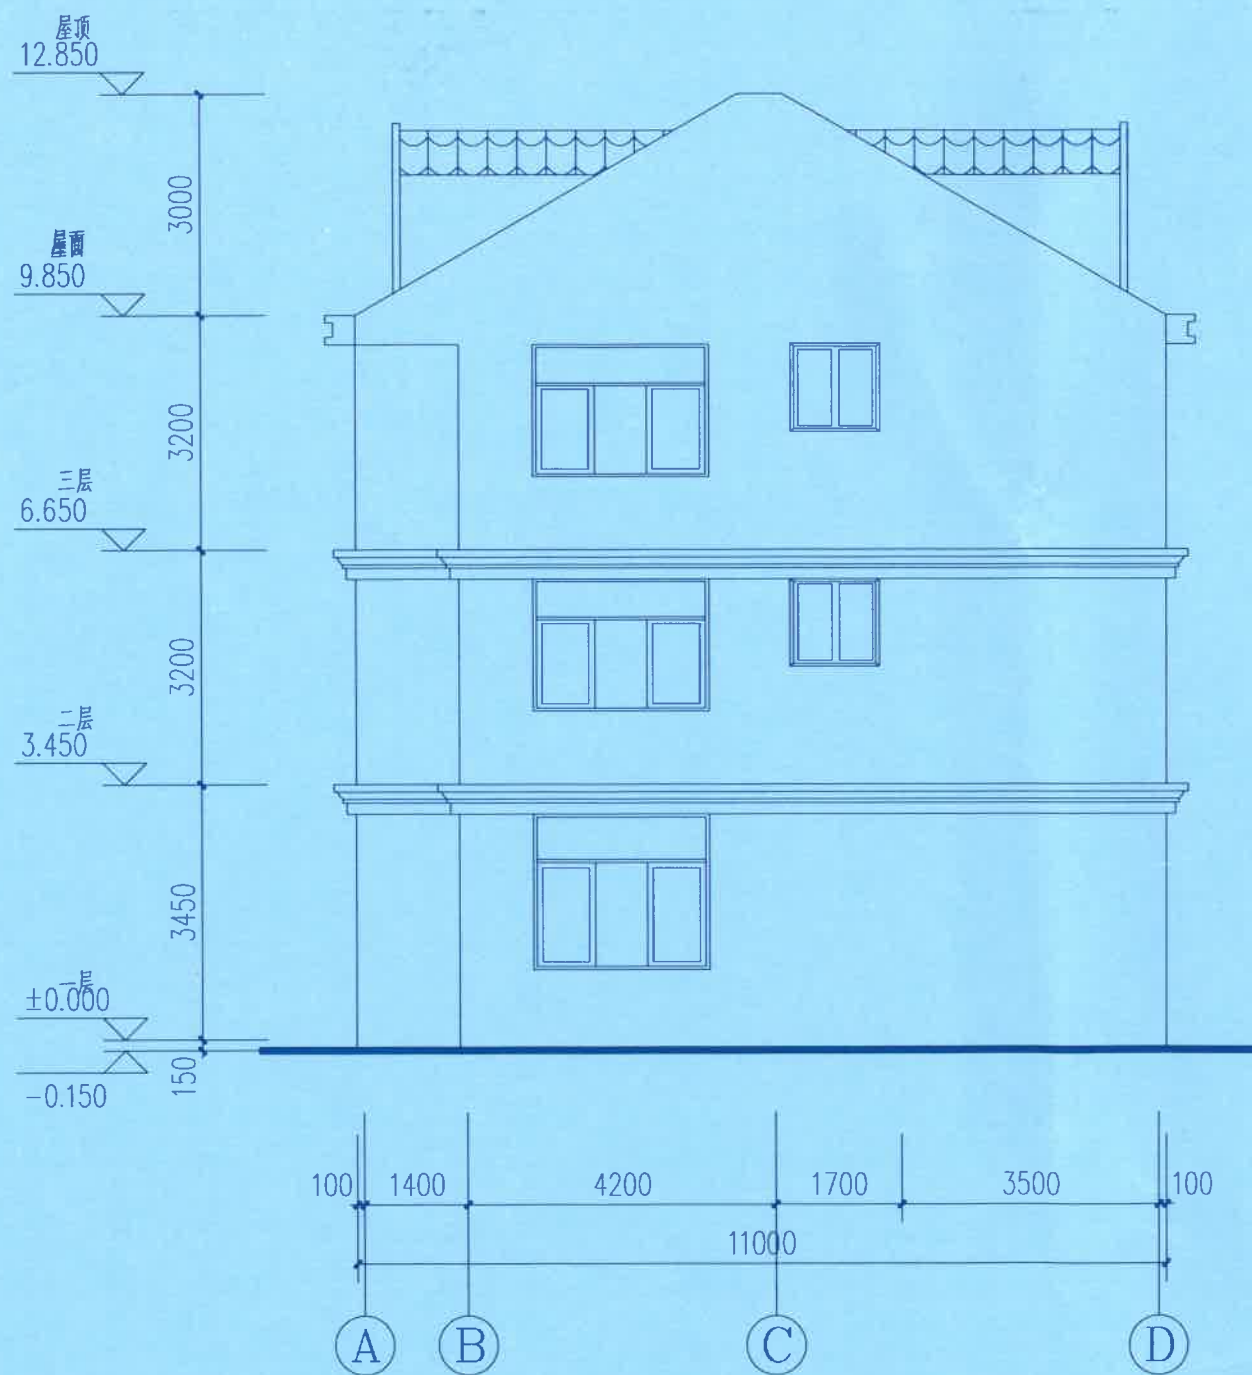

①-③轴立面图 1:100

平潭综合实验区自然资源局与生态环境局
图纸专用章(1)
随 崇建+成 No.000395 号有效

平潭综合实验区规划设计研究院
(平潭县建筑勘察设计院)
Pingtan Comprehensive Experimentation Zone
Planning Programming Institute
(Pingtan Architectural Design Institute)
注册编号: A235005610
ARCHITECTURAL DESIGN LICENSE No. A235005610

备注

图纸专用章

注册建筑师执业章

注册结构师执业章

施工图审查批准单位

施工图审查批准书证号

工程名称

谢晓东个人住宅

建设单位

审定

工程负责人

专业负责人

审核

校对

设计

制图

图名

①~③轴立面图

工程编号

MF200910

图别

建筑

图号

09

日期

2021.08