

平潭综合实验区潭城管理单元环岛东路与中湖路东路交叉口西南侧地块控制性详细规划


01.区域位置图



规划范围于平潭岛中的位置




规划范围于潭城组团中的位置

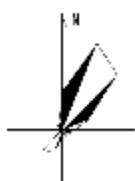


平潭综合实验区潭城管理单元环岛东路与中湖路交叉路口西南侧地块控制性详细规划

03.用地规划图

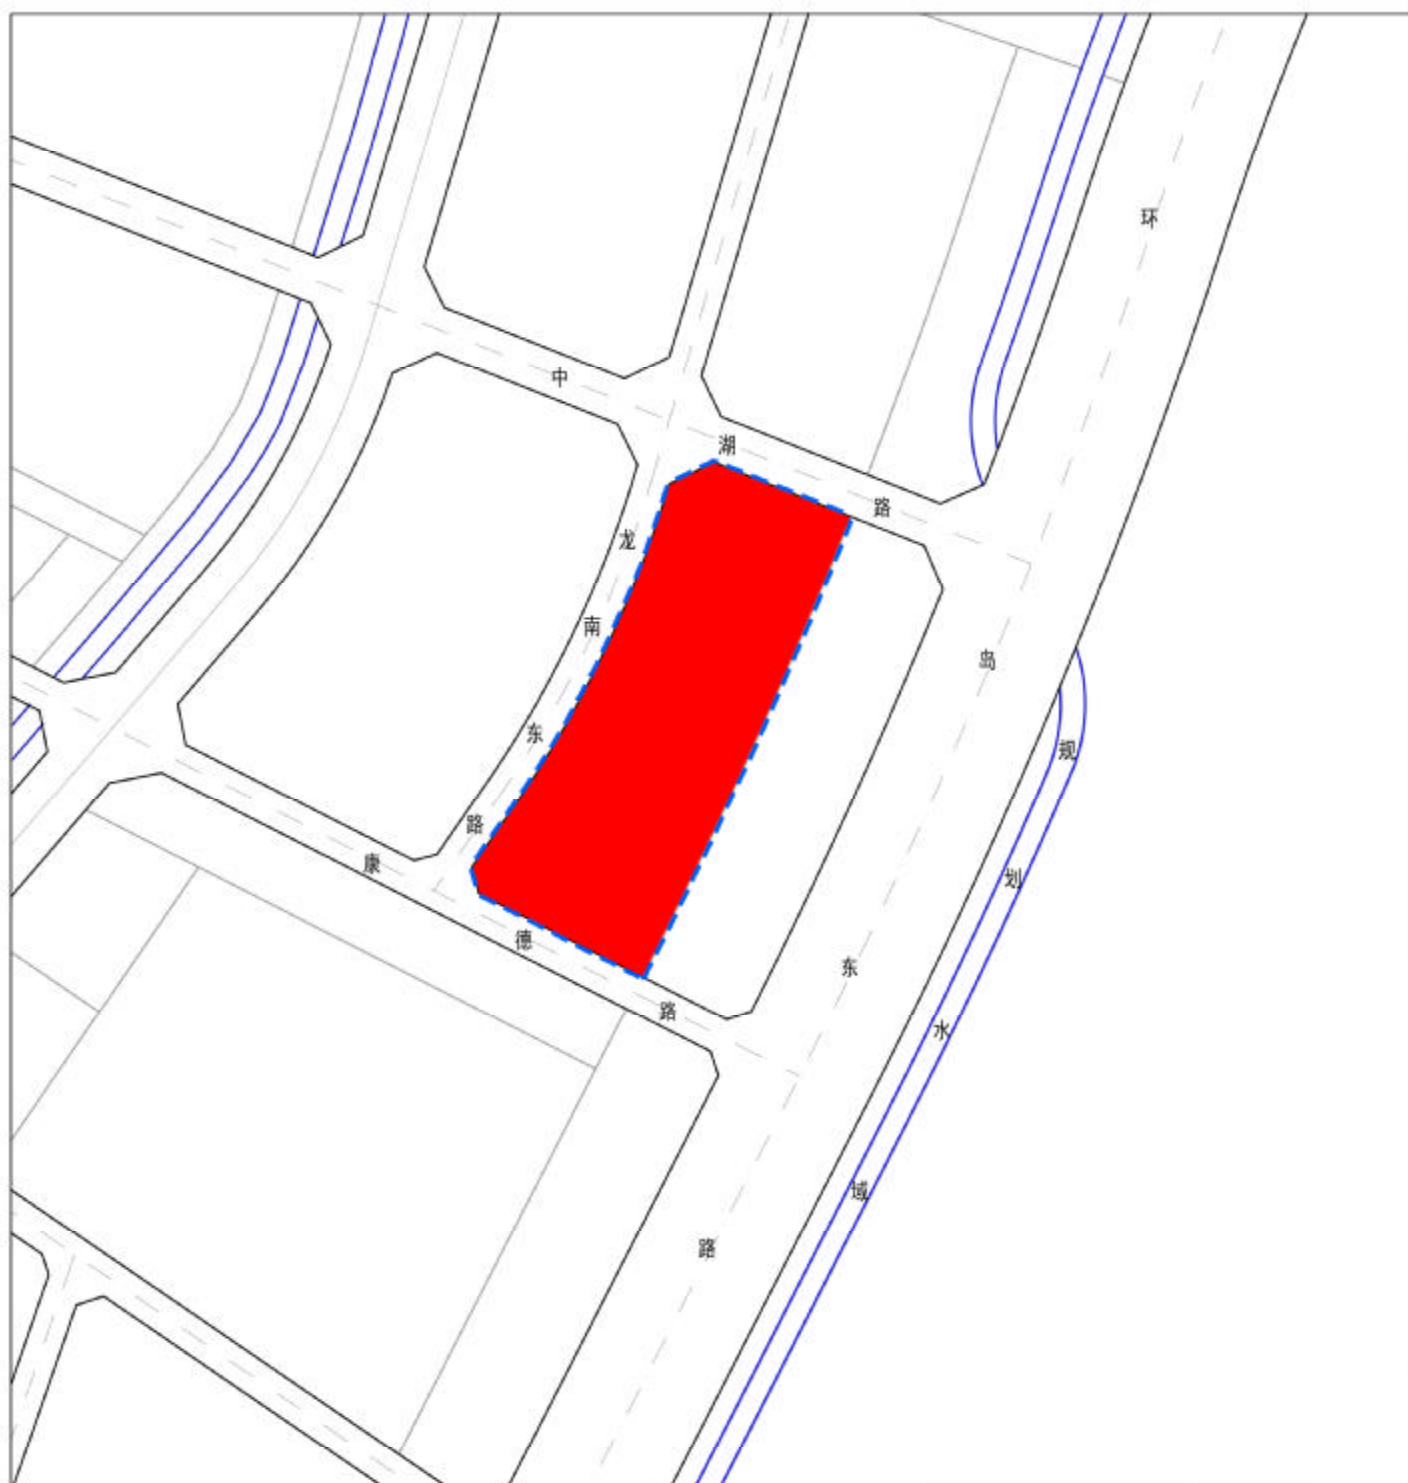


- 旅馆用地
- 城市道路
- - - 规划范围

平潭综合实验区潭城管理单元环岛东路与中湖路交叉口西南侧地块控制性详细规划

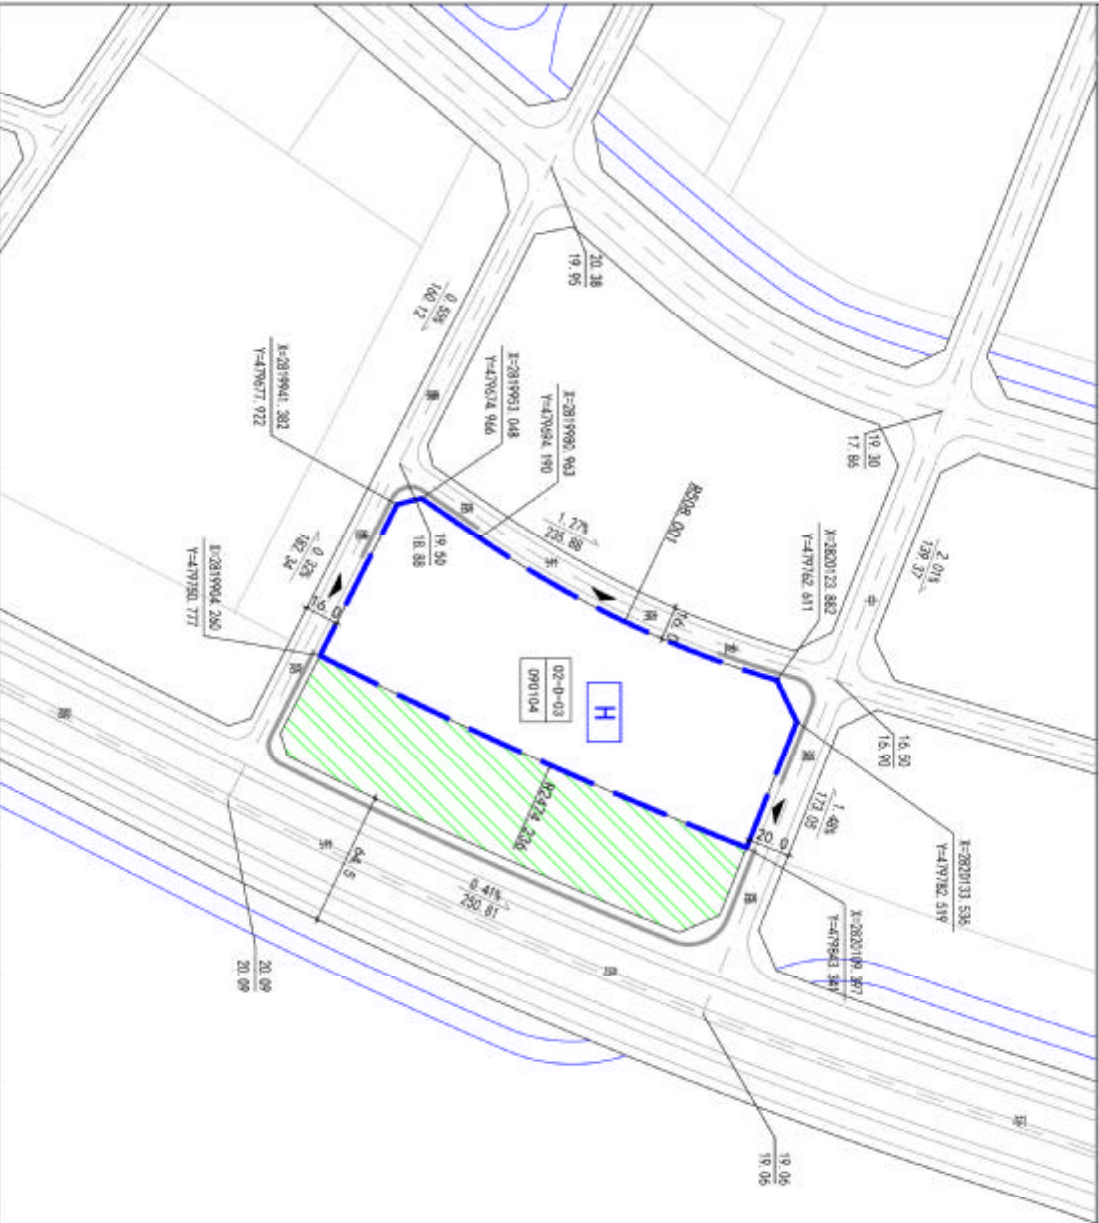

地块编号	用地代码	用地性质	用地面积 (平方米)	建筑面积 (平方米)	容积率	建筑密度 (%)	绿地率 (%)	建筑高度 (米)	配套设施
02-D-03	090104	商业用地	17774.103	535550	≤2.0	≤40	≥30	50	H
备注：控制指标未明确的城市公共设施、交通设施等地块，可参照相关行业标准或现行法律法规部门意见确定具体项目用地、建设规模及规划控制指标等，作为审批依据。									

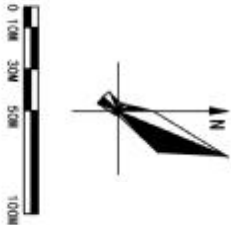

图例

- 地块控制线名称
- 城市道路
- 规划道路
- 道路红线宽度
- 绿地
- 机动车出入口
- 地块编号
- 用地性质
- 禁止机动车开口线
- 10kV变电站

规划控制条文

- 规划地块用地性质为商业用地，用地面积约1.78公顷，不得随意更改地块用地性质和位置。
- “五线”属于强制性内容，其线位、规模及性质一经确定不得擅自调整，控制内容如下：道路红线：环岛东路，道路宽度64.5米；中湖路，道路宽度20米；康乐路，道路宽度16米；龙海路，道路宽度16米。城市绿线：环岛东路西侧绿地宽度50米。
- “三大设施”控制应按《福建省城市规划设计管理技术规定》(2017年版) 公共服务设施配置标准，具体指标如下：02-D-01地块配置一处10kV变电站，室内建筑面积不小于45平方米。
- 配套设施的项目、数量和用地或建筑面积不得少于规划的规定，如有变更，必须申报城市行政主管部门批准。
- 建筑间距应符合日照、防火、消防、抗震、环保、工程管线和文物、建筑保护等方面的要求，同时还应满足《福建省城市规划设计管理技术规定》(2017) 中的建筑间距控制要求。
- 地块出入口及配建停车位应满足《福建省城市规划设计管理技术规定》(2017) 要求。
- 地块城市设计应注重于周边城市主次干路的关系；竖向及市政工程管线规划应与周边道路的竖向及工程管线相衔接；图中道路的线位、断面形式、交叉口形式、控制标高及具体位置均以批准的工程方案为准。
- 地块图则未涉及的其他规划要求由平潭综合实验区自然资源与生态环境局根据相关规定确定并执行。

图名	地块编号及图则
编制单位	厦门市城市规划设计研究院有限公司
图号	12
日期	2021.11