

潭综合实验区潭城管理单元龙山路与中湖路交叉口东侧 地块控制性详细规划

01.区域位置图



规划范围于平潭岛中的位置




规划范围于潭城组团中的位置



潭综合实验区潭城管理单元龙山路与中湖路交叉口东侧 地块控制性详细规划



02.用地现状图

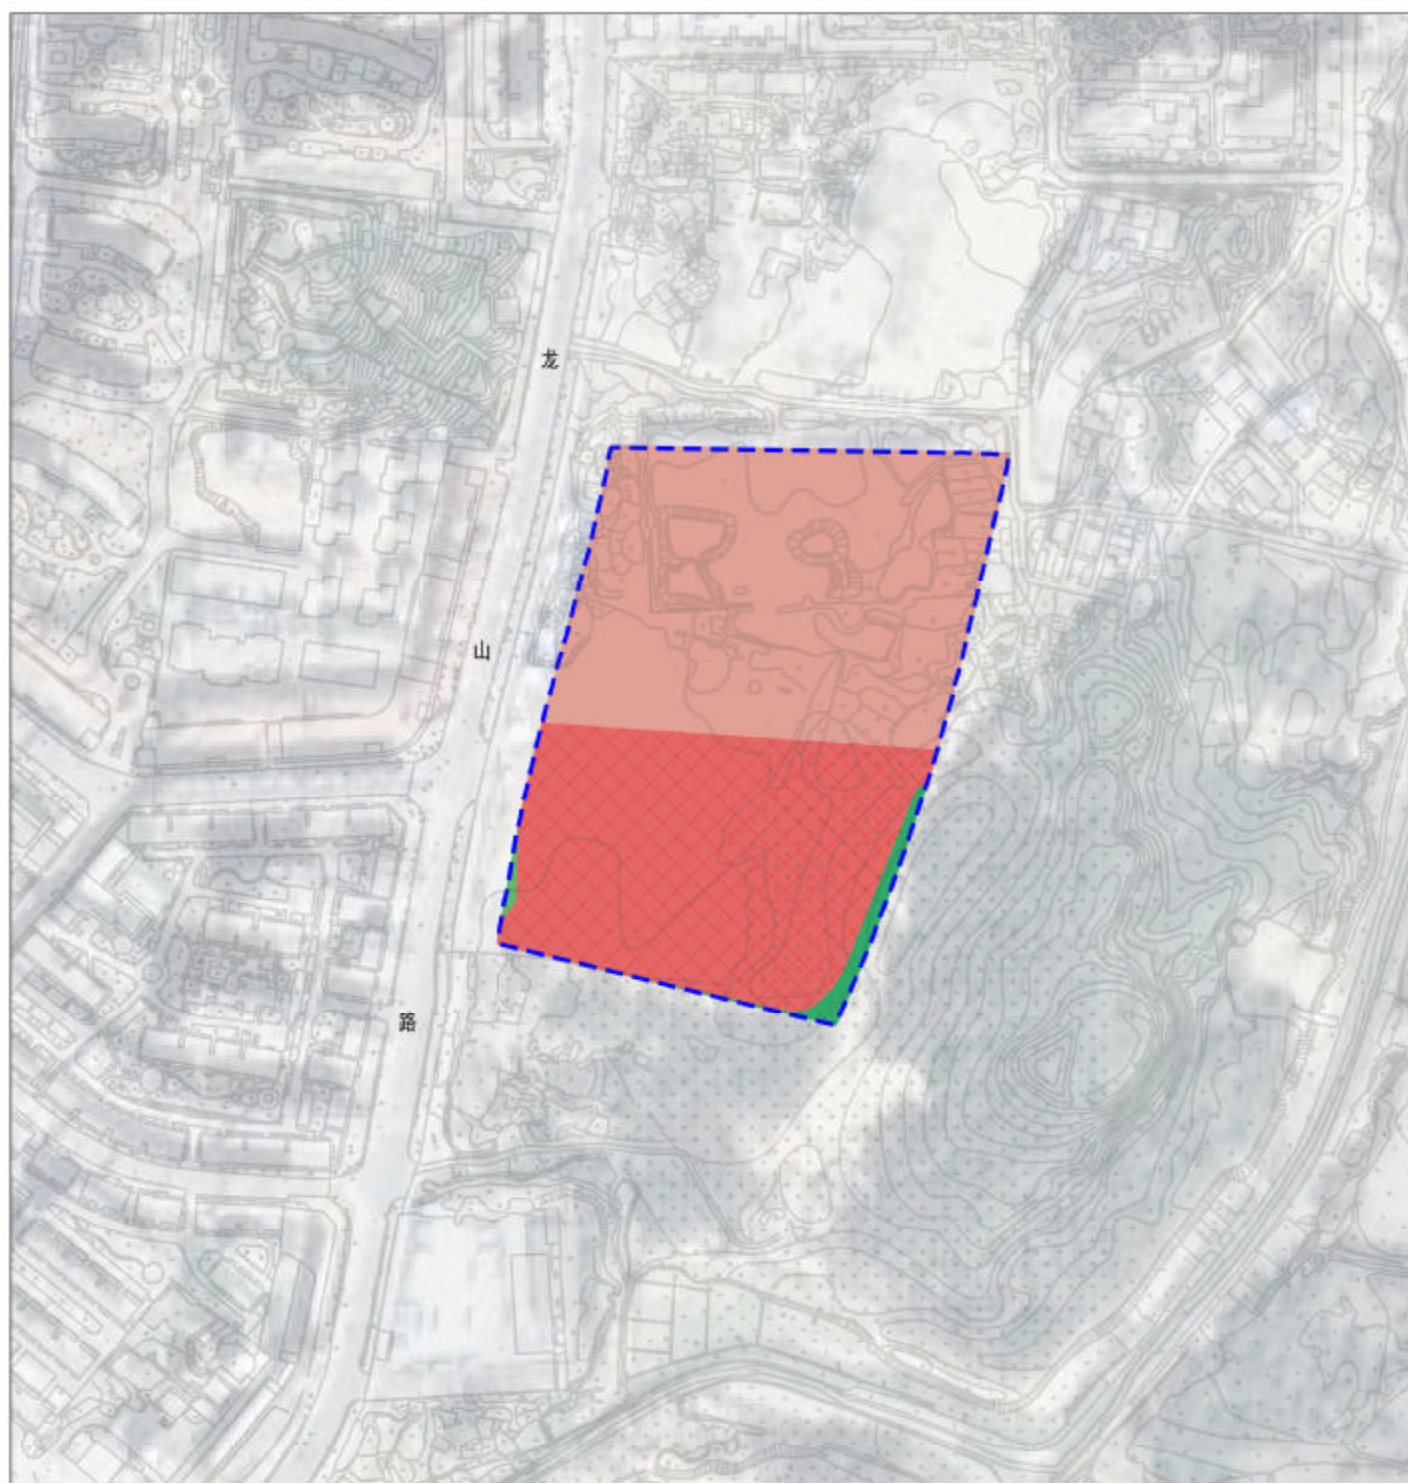


- 乔木林地
- 农村道路
- 商业服务业设施用地
- 城镇住宅用地
- 灌木林地

规划范围

平潭综合实验区潭城管理单元龙山路与中湖路交叉口东侧地块控制性详细规划

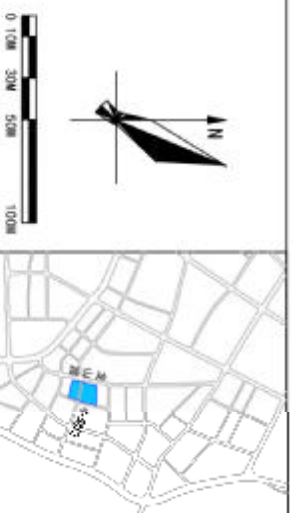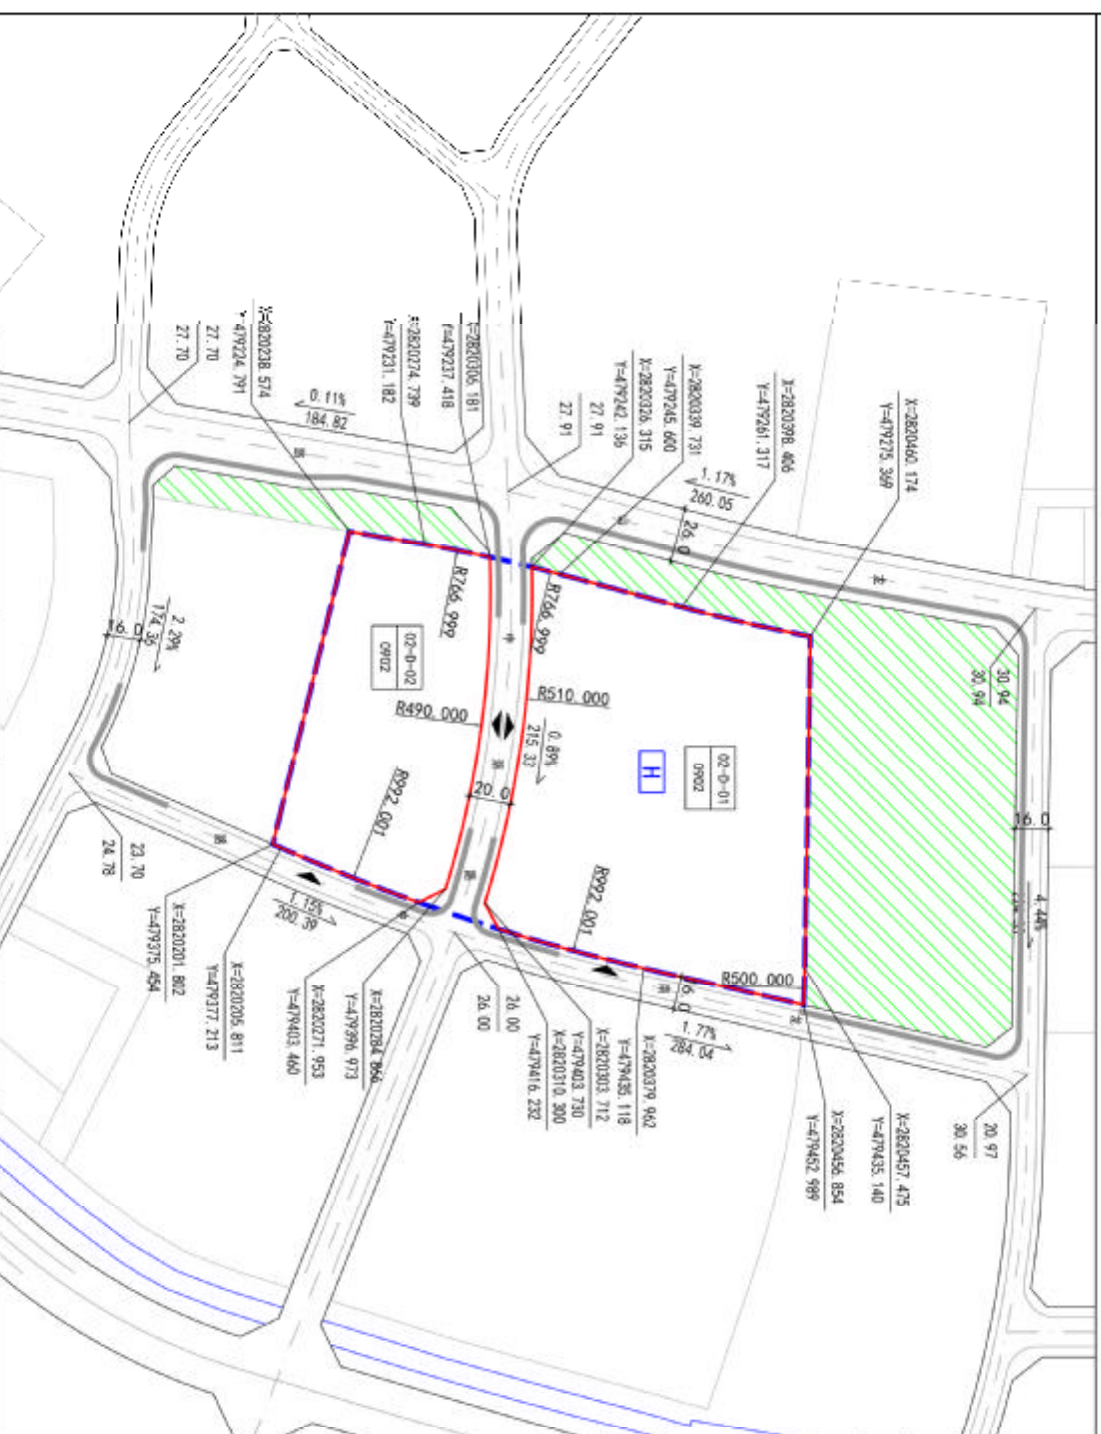

图例

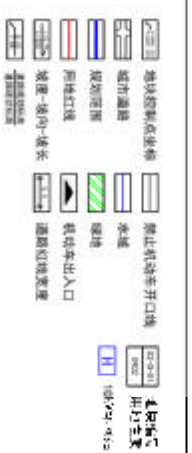

规划控制条文

- 1、规划区用地性质包含商务金融用地、城镇道路用地。其中，商务金融用地用地面积约3.83公顷，城镇道路用地约0.36公顷。不得随意更改地块用地性质和位置。
- 2、“五线”属于强制性内容，其线位、规模及性质一经确定不得擅自调整，控制内容如下：
 - 道路红线：龙山路，道路宽度26米；中湖路，道路宽度20米；龙平一路，道路宽度16米。
 - 城市绿线：龙湖北路南侧绿地，宽度100米；龙山路东侧绿地，宽度20米。
- 3、“三大设施”控制按照《福建省城市控制性详细规划管理技术规定》(2017)公共服务设施配置标准，具体如下：
 - 02-0-01地块配建一处10KV变电站，需内建面积不小于50平方米。
- 4、配套设施的项目、数量和用地或建筑面积不得少于规定的规定，如有变更，必须经审批行政主管部门批准。
- 5、建筑密度应符合日照、防火、消防、抗震、环保、工程管线等技术规定，建筑密度应符合日照、防火、消防、抗震、环保、工程管线等技术规定。(2017)中的建筑密度控制要求。
- 6、地块出入口及配建停车位应满足《福建省城市控制性详细规划技术规定》(2017)要求。
- 7、地块城市设计应注重于周边城市主干干路的关系；建筑高度、工程管线规划应与周边道路的走向及工程管线相协调；建筑高度、建筑形式、建筑形式、控制点标高及具体位置均以批准方案为准。
- 8、地块规划未涉及的其他规划要求由平潭综合实验区自然资源局与生态环境等部门根据相关规定确定并执行。

序号	名称	用地性质	用地面积 (平方米)	建筑密度 (%)	容积率	建筑高度 (米)	配套设施
02-0-01	商务金融用地	25007.526	≤25000	≤1.0	≤40	24	H
02-0-02	商务金融用地	11356.321	≤20000	≤1.5	≤40	24	H

注：1、本规划图则及用地红线、建筑密度控制线、建筑高度控制线、配套设施控制线等，作为审批依据。

图名

地块编号及图例

编制单位 厦门市城市规划设计研究院有限公司
厦门市规划院(平潭)规划设计有限公司

图号 12 日期 2021.11